План (1 : 150)

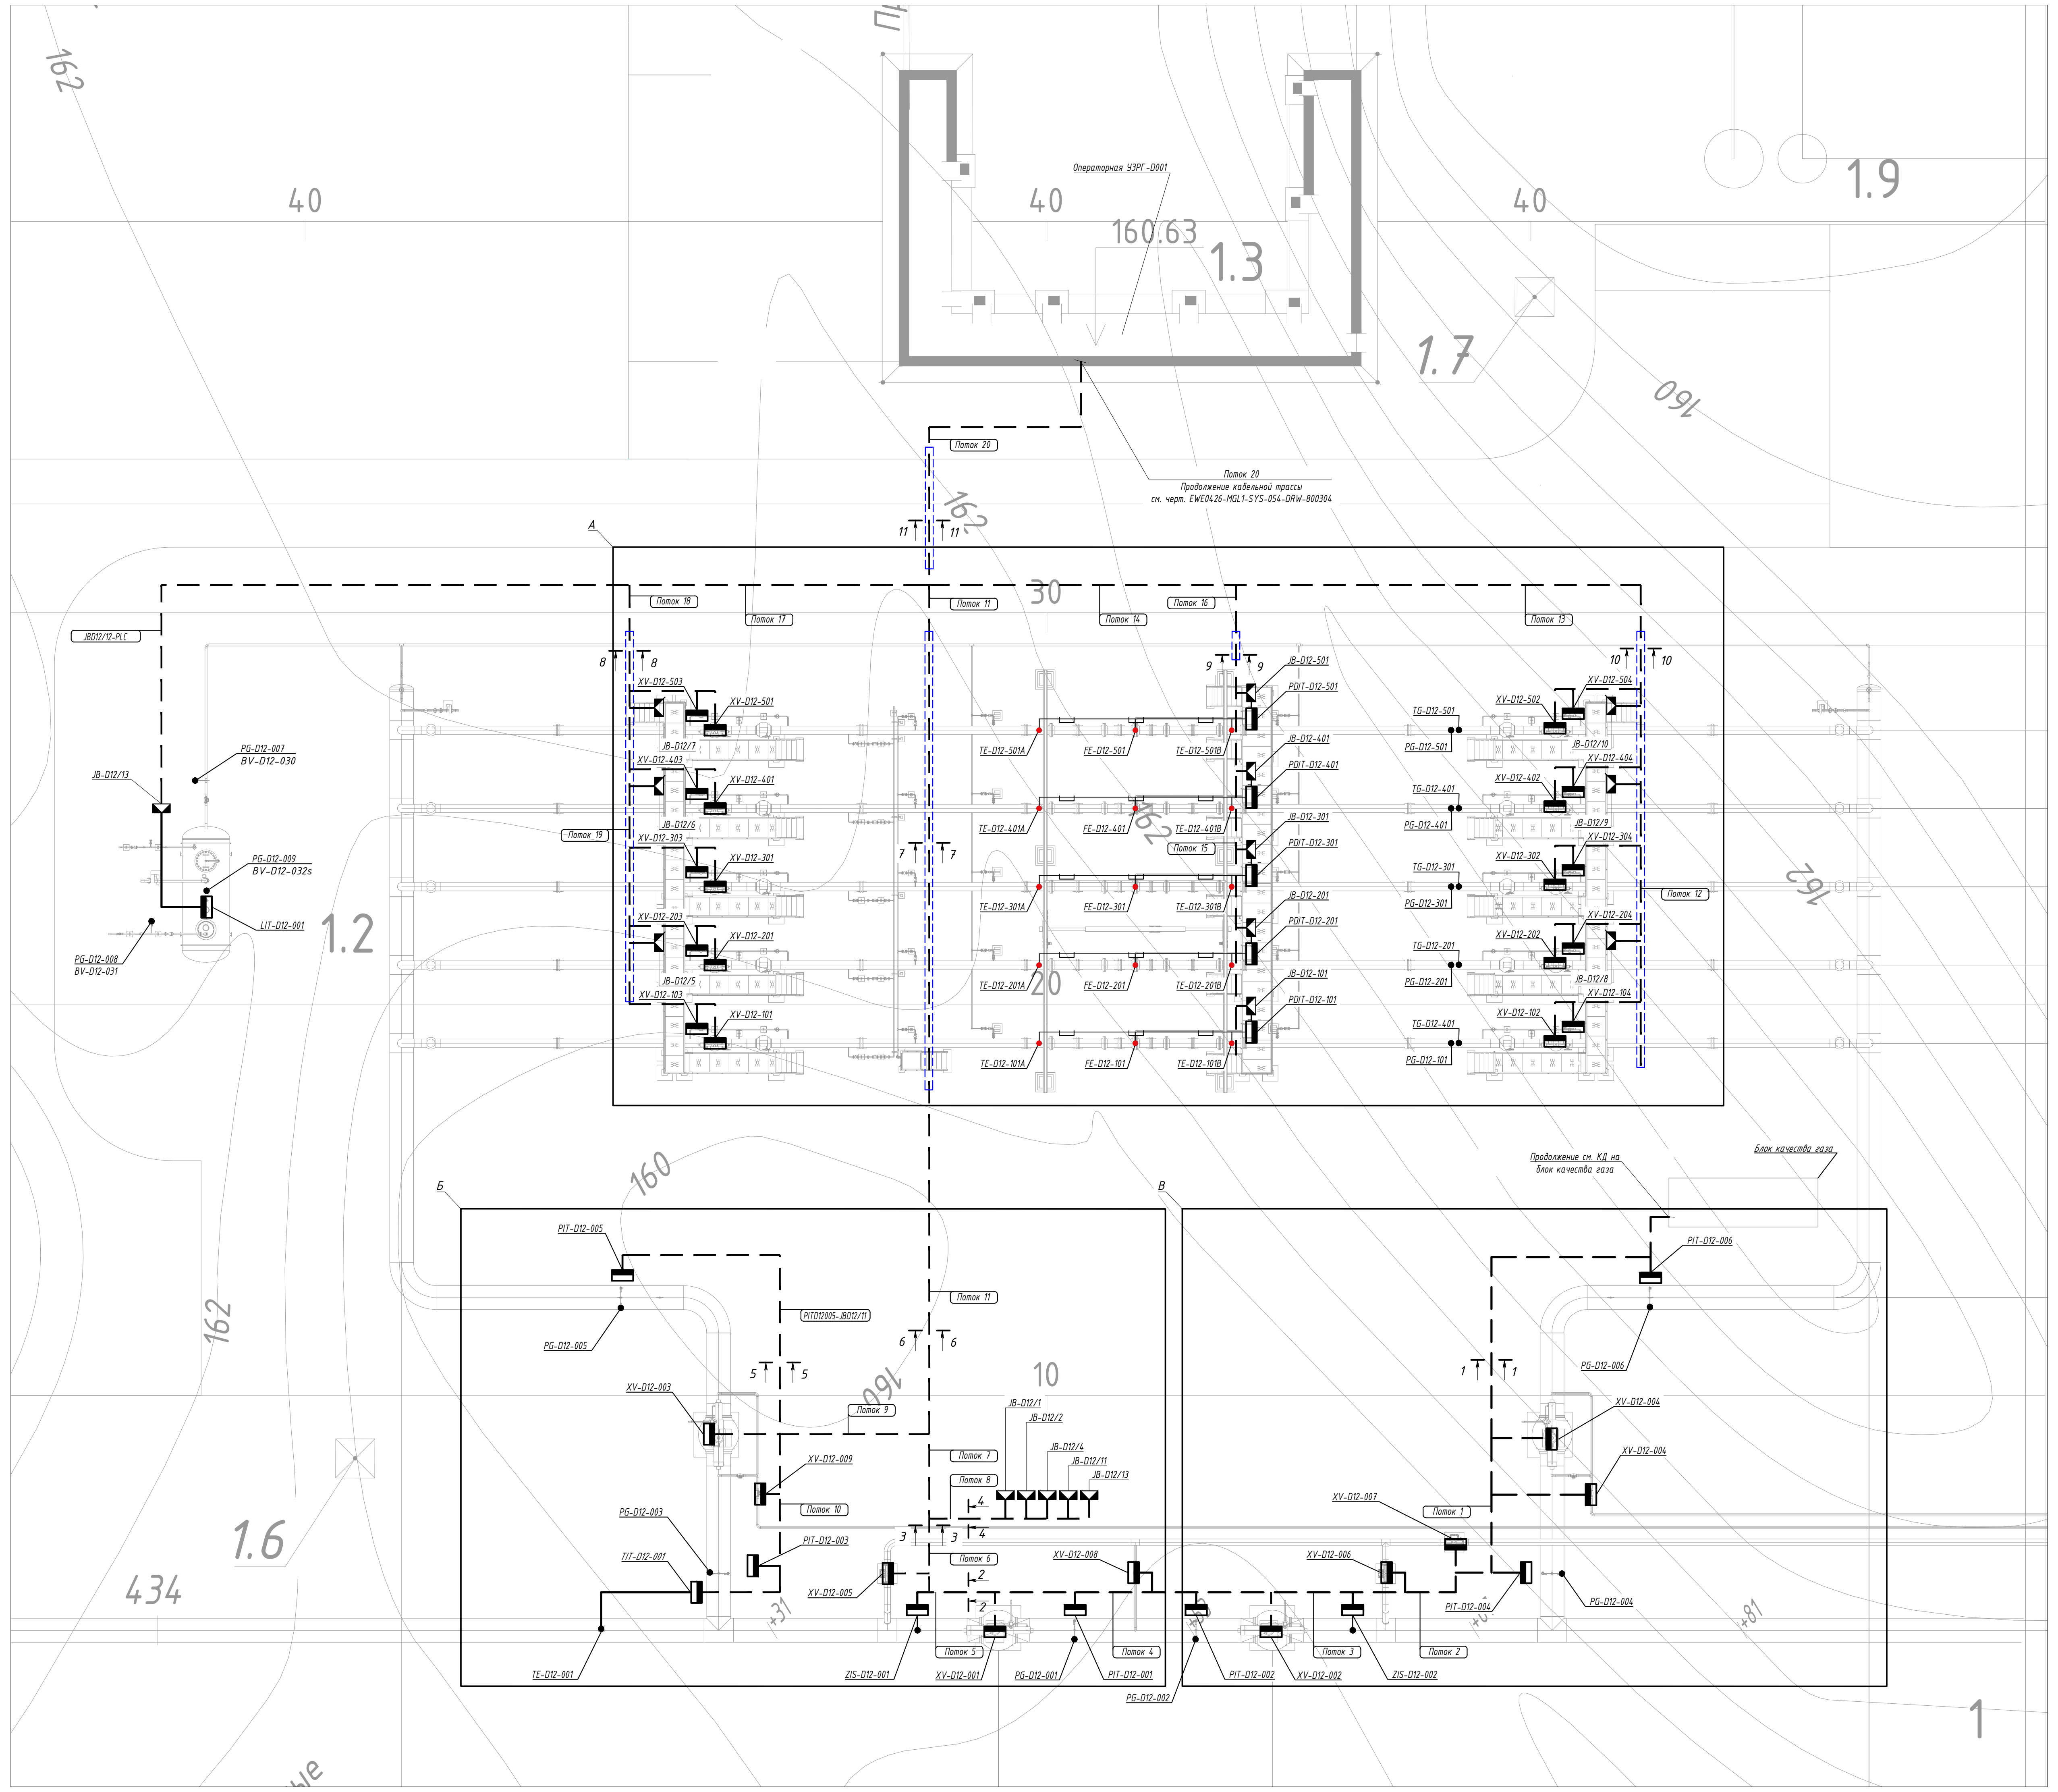

А (1 : 100)

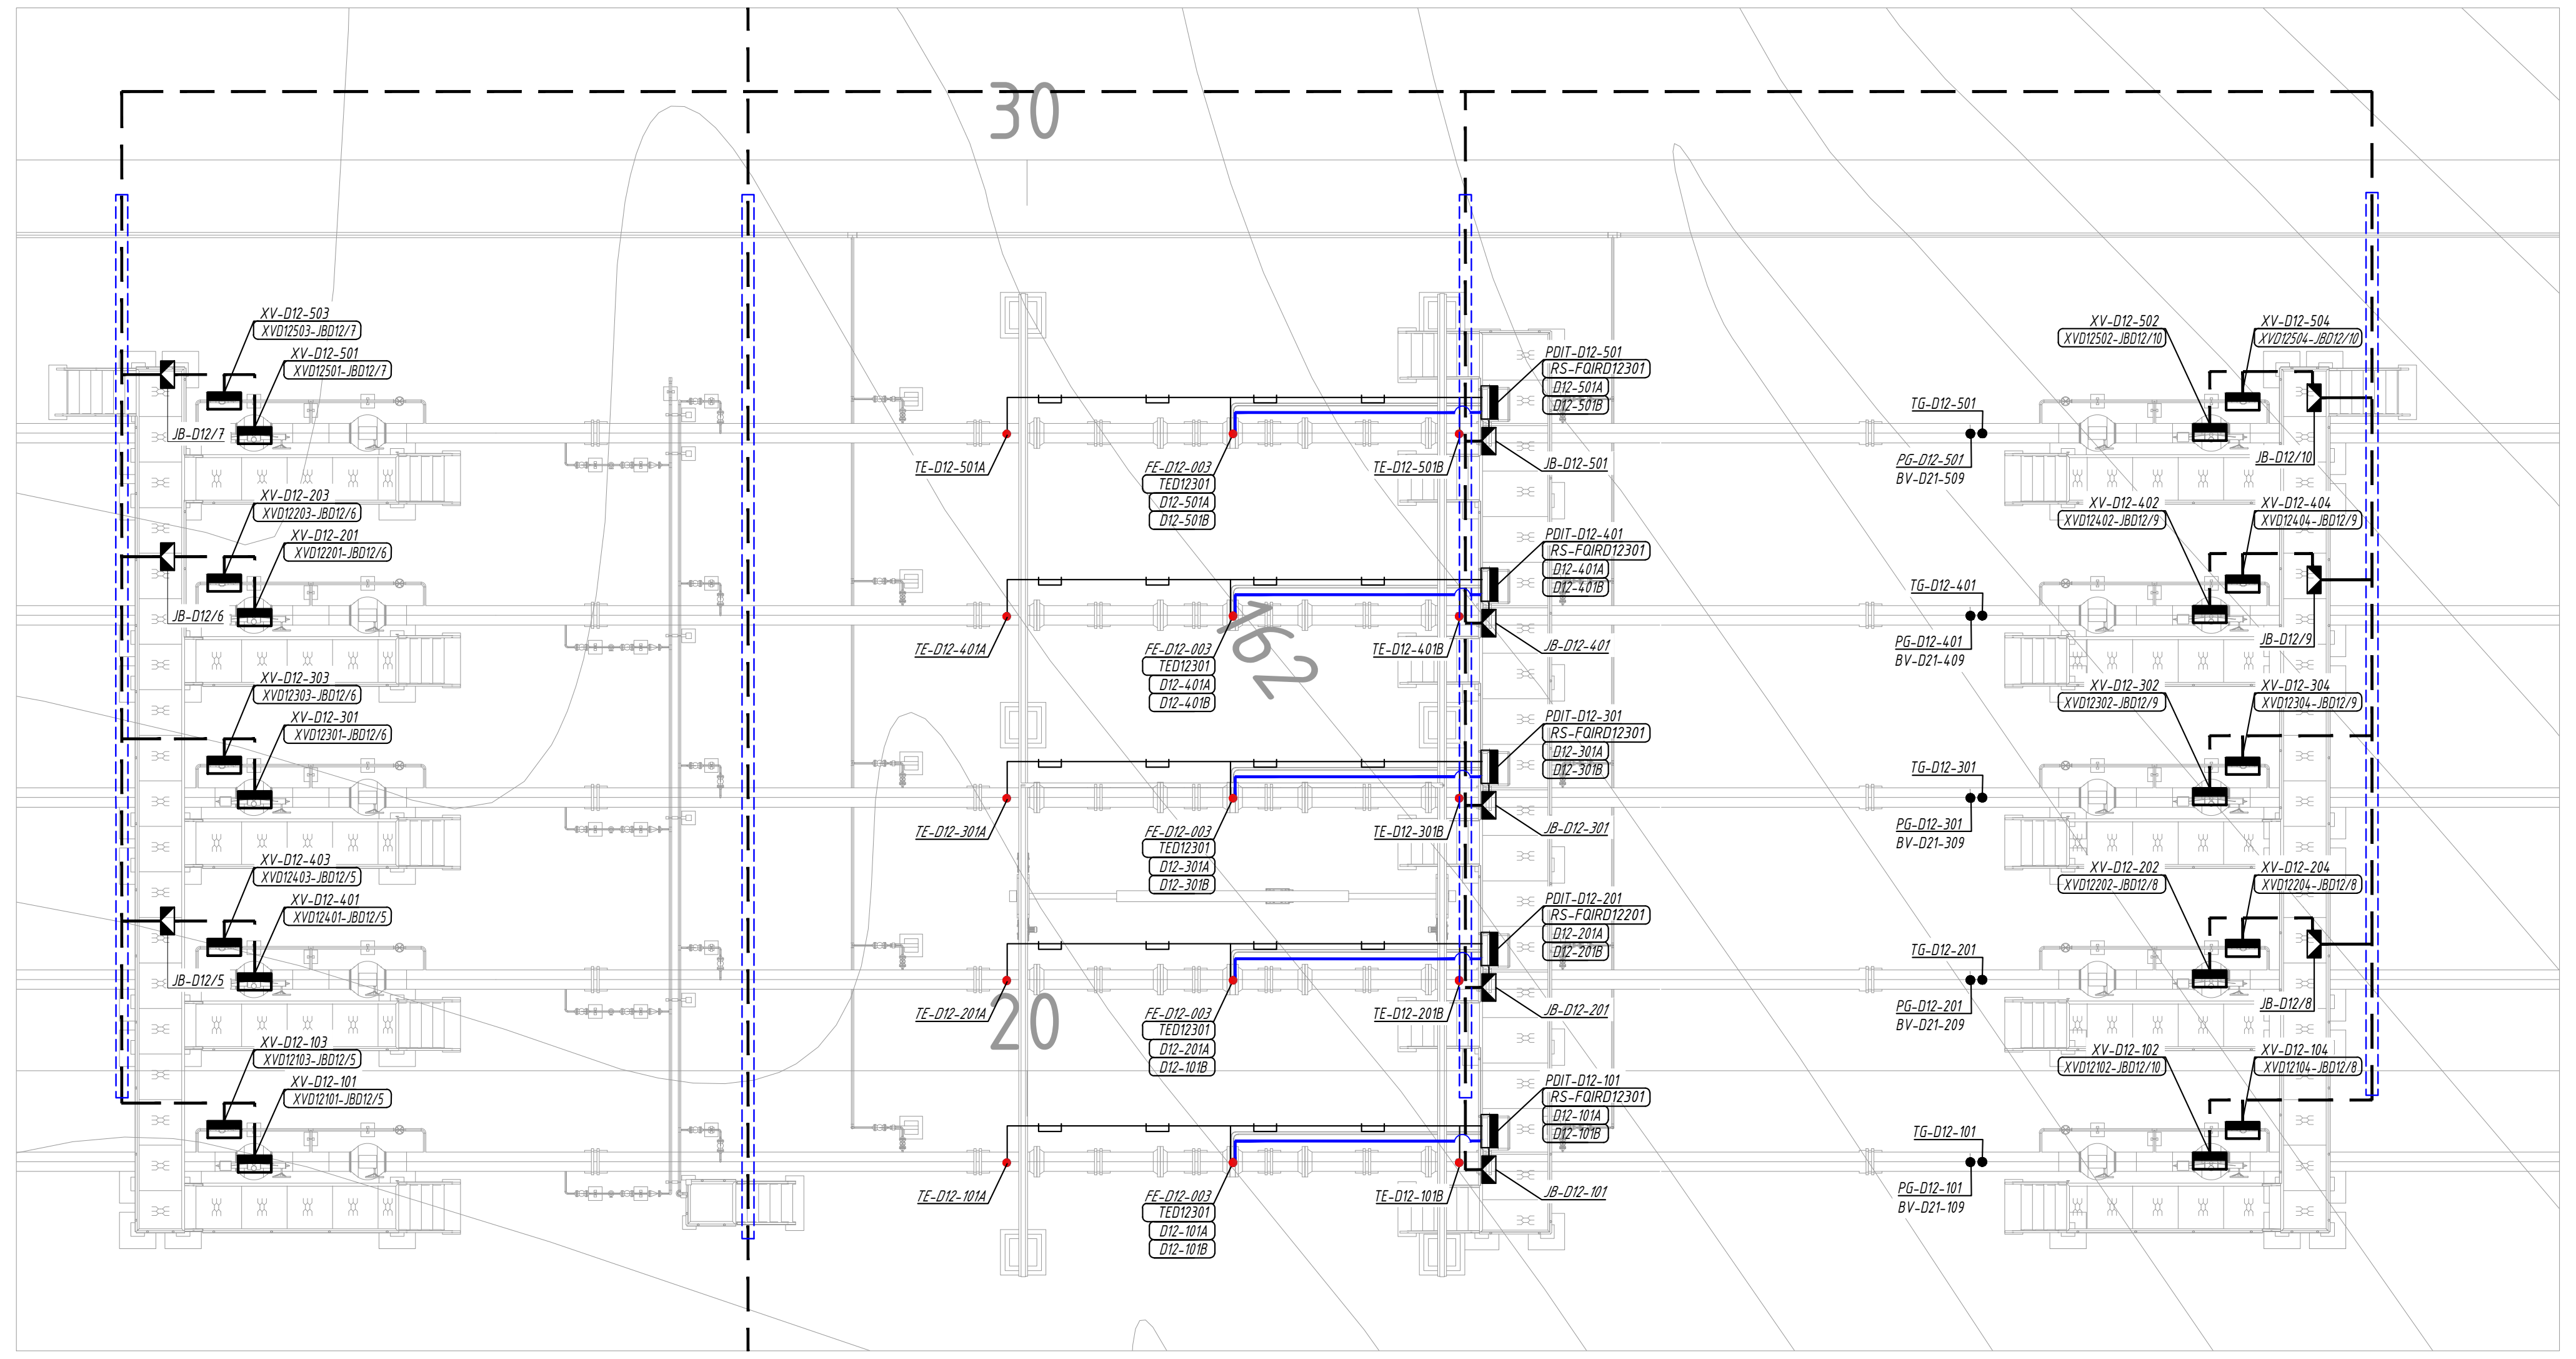

Б (1 : 100)

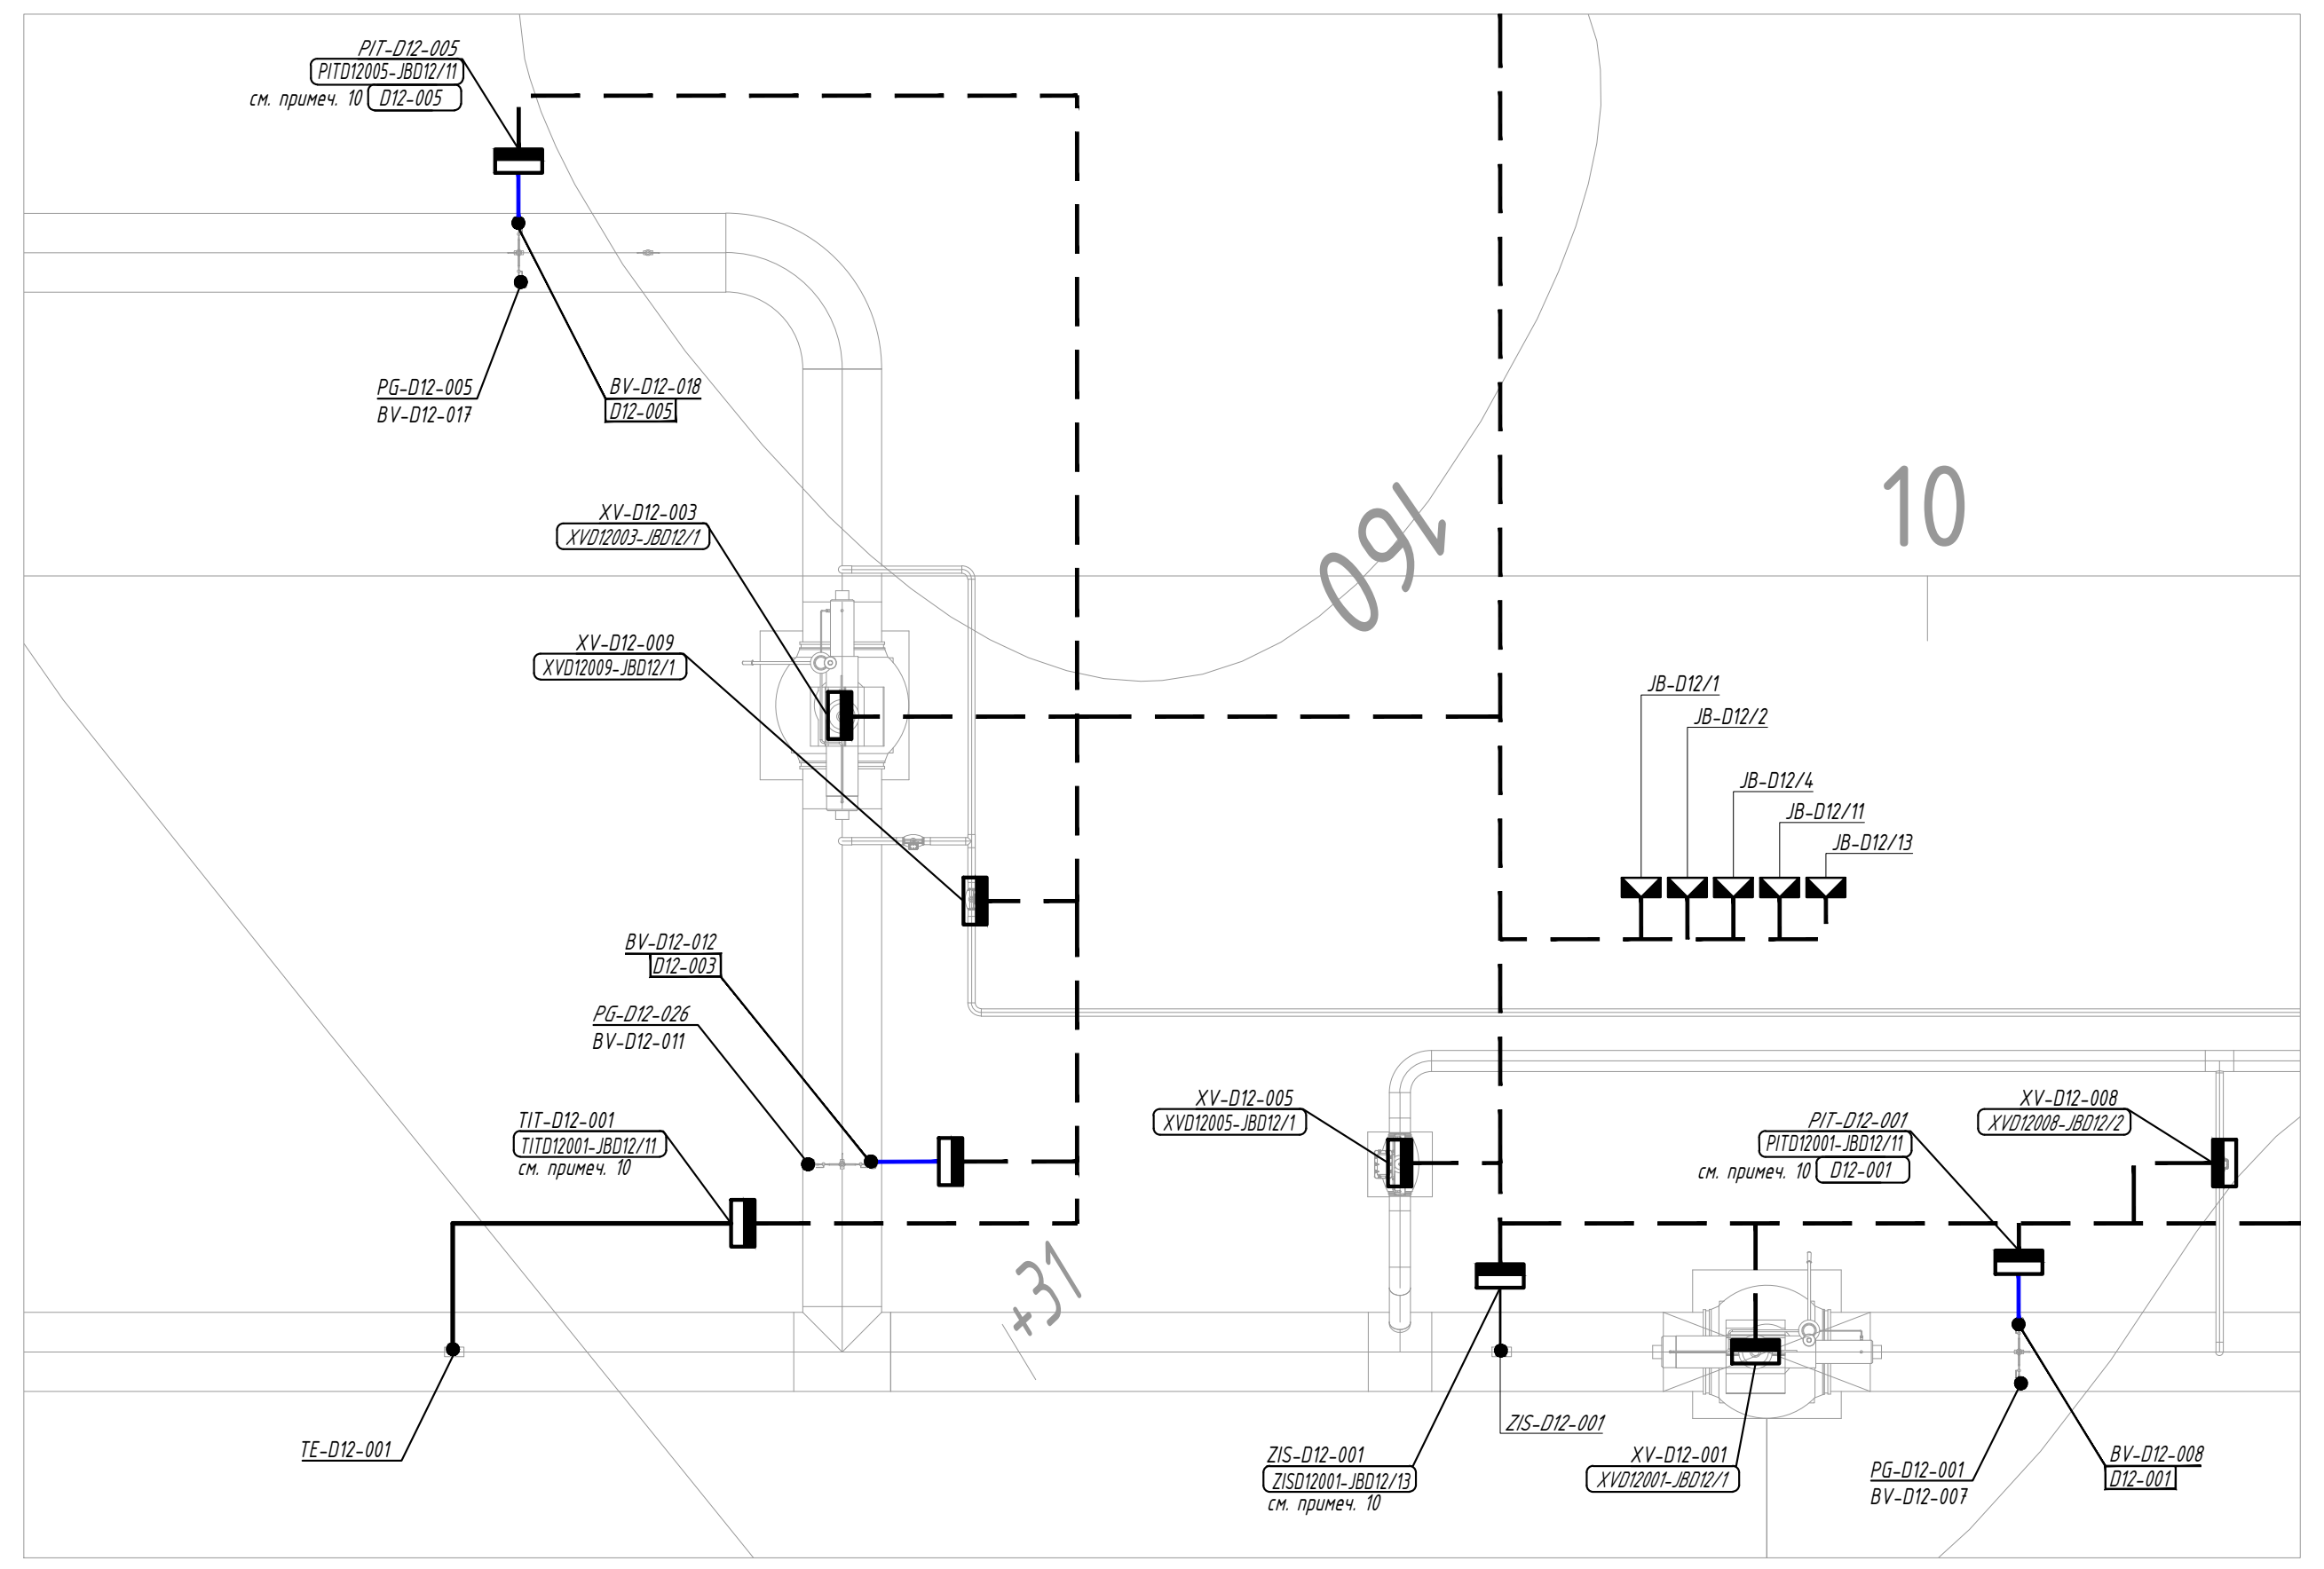

В (1 : 100)

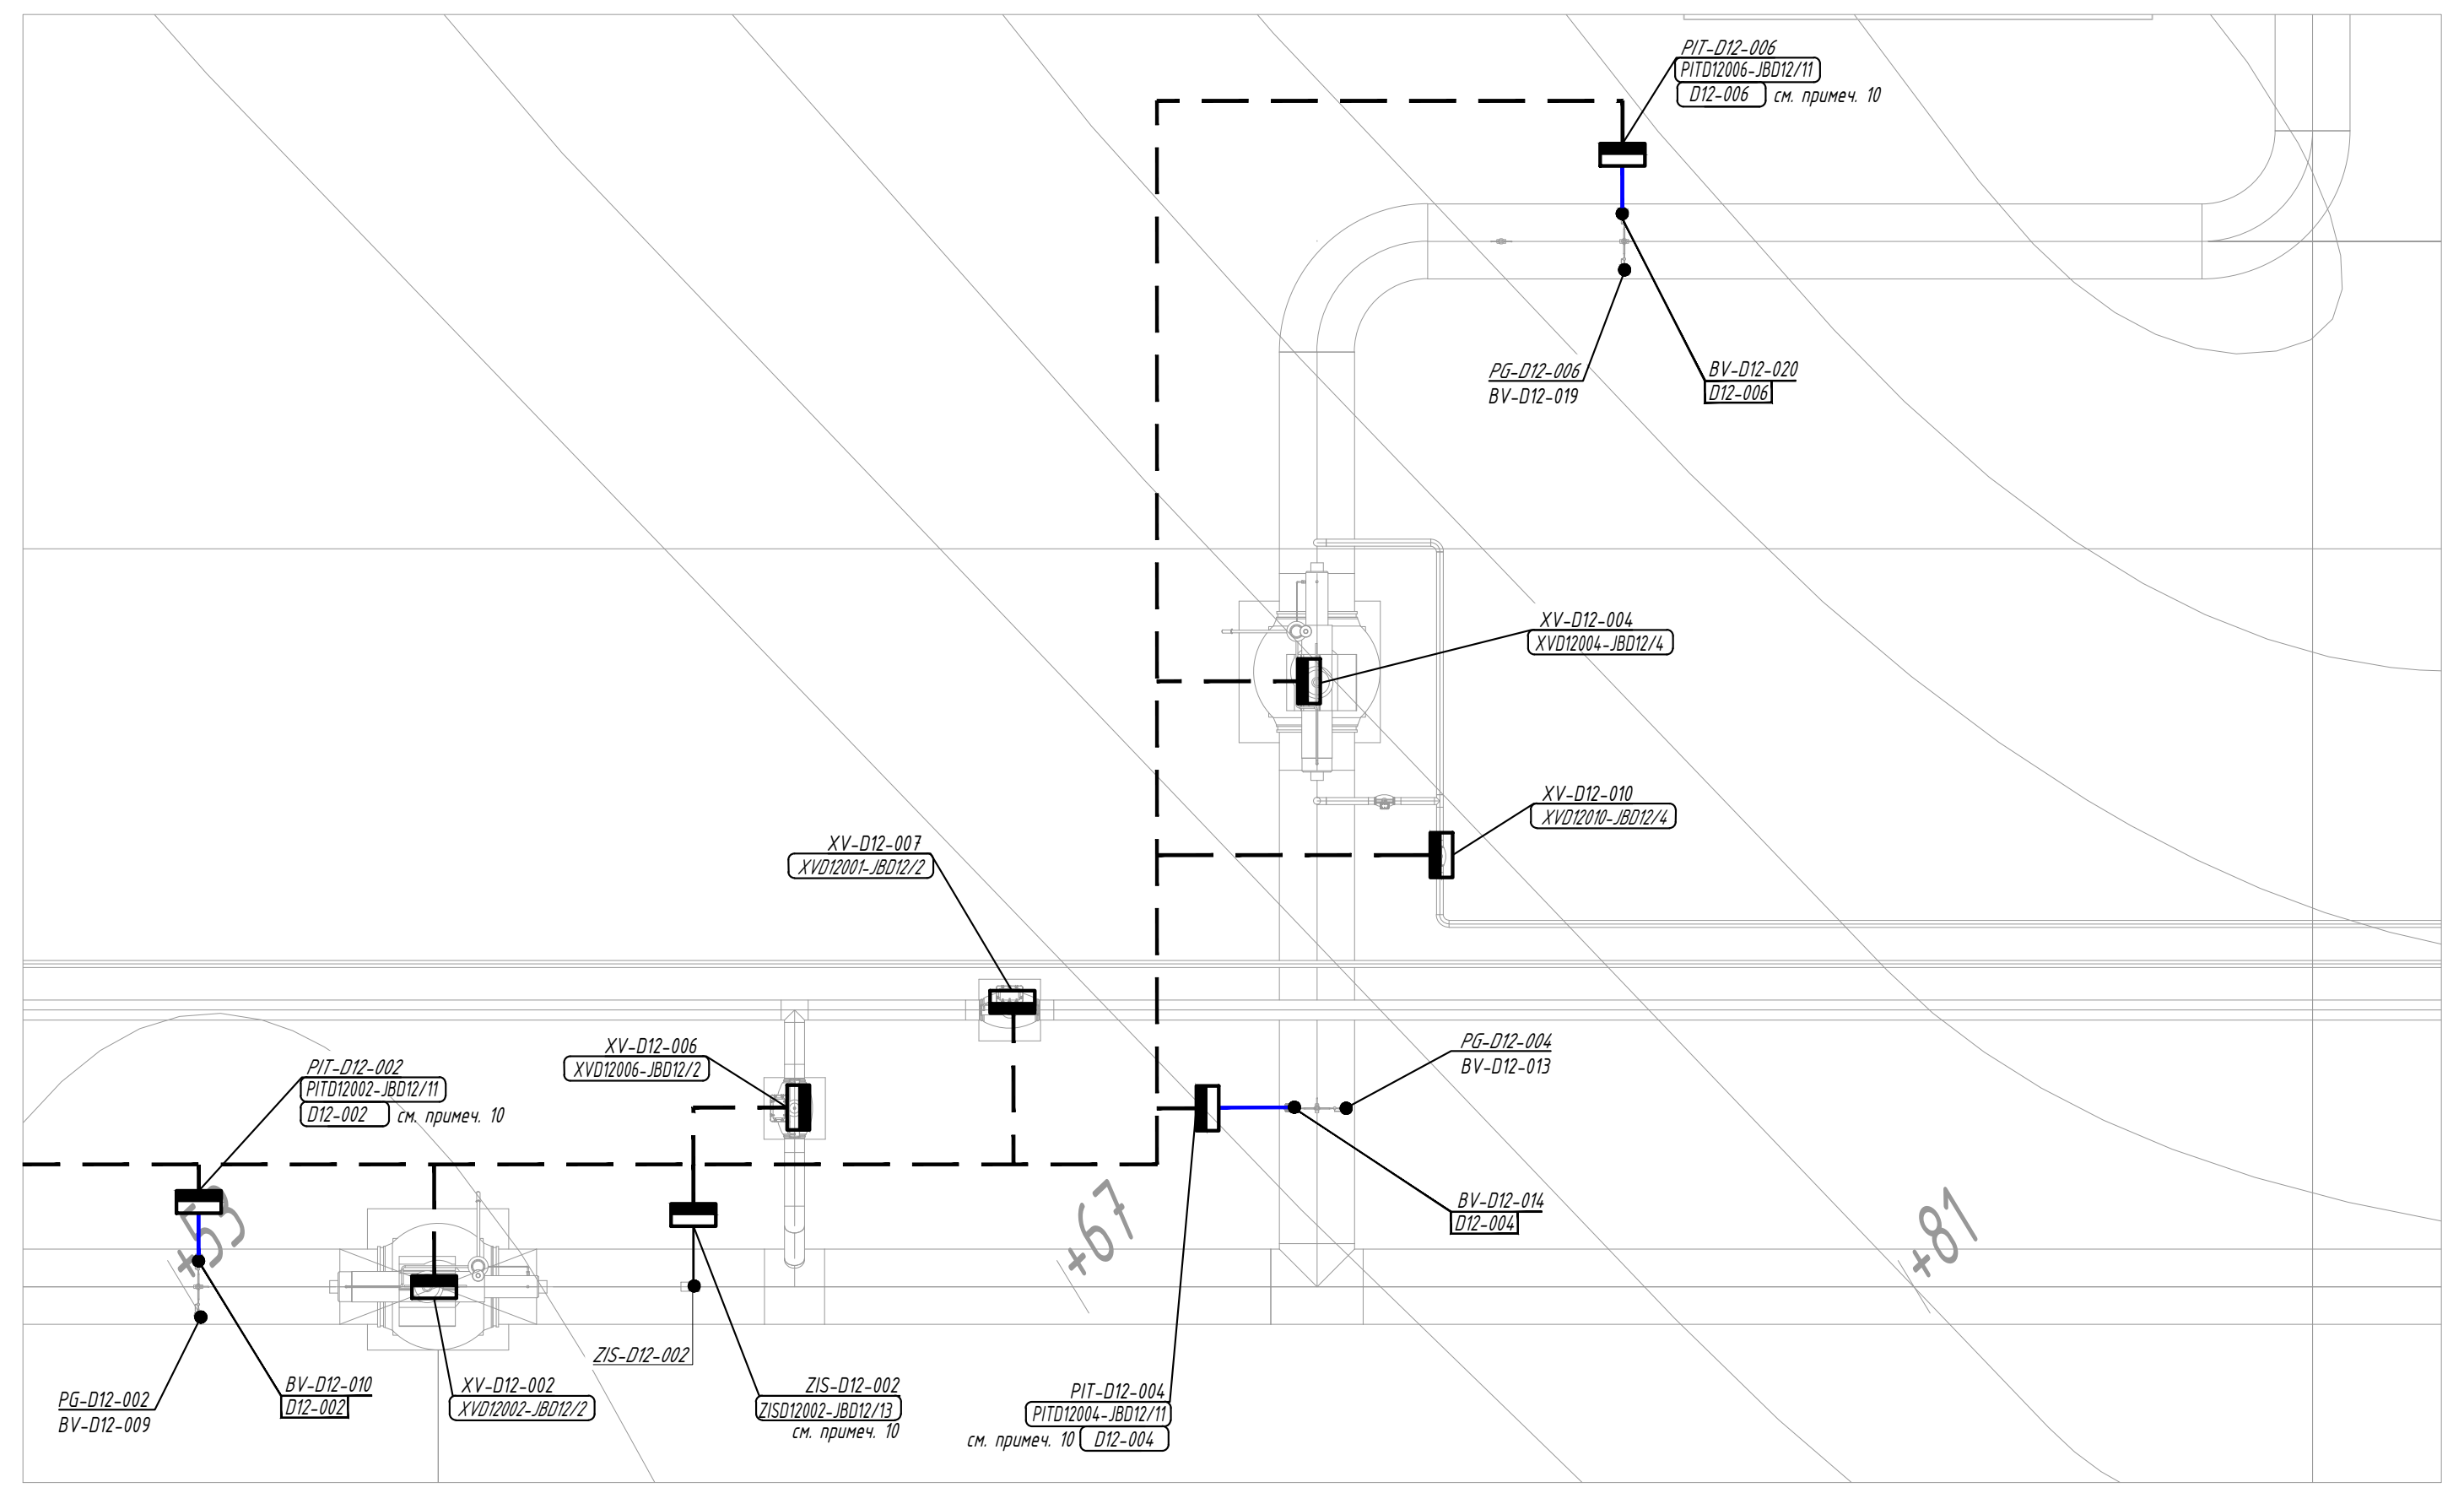

1-1 (1:20)

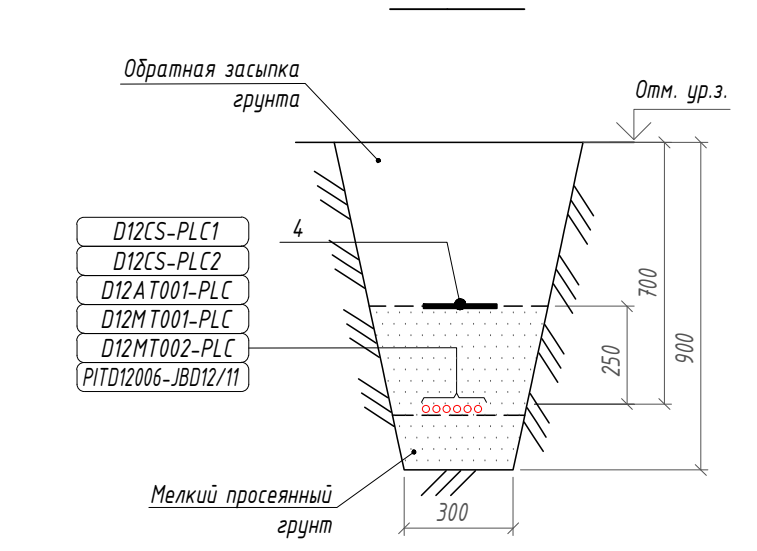

2-2 (1:20)

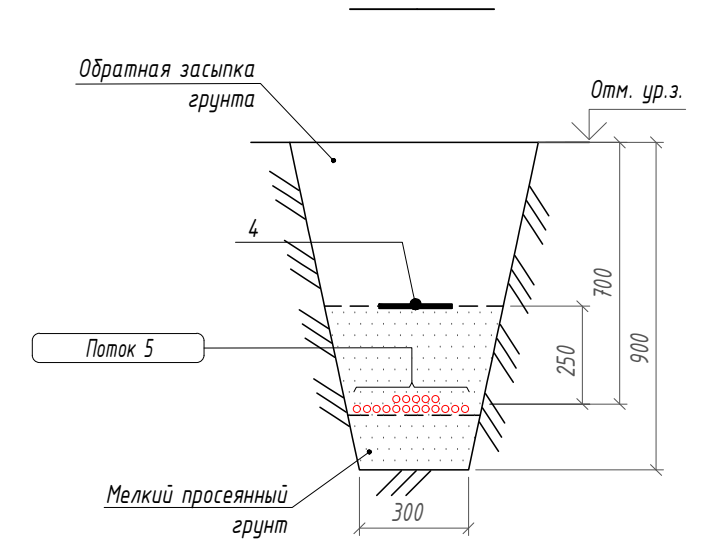

3-3 (1:20)

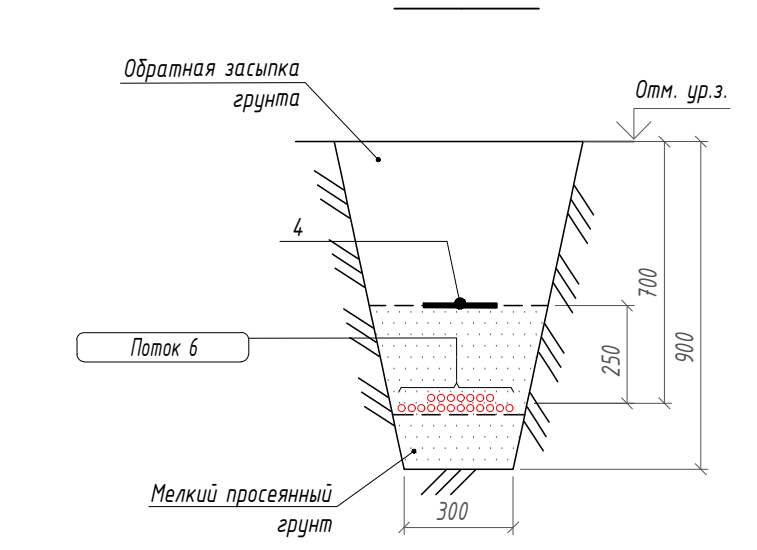

4-4 (1:20)

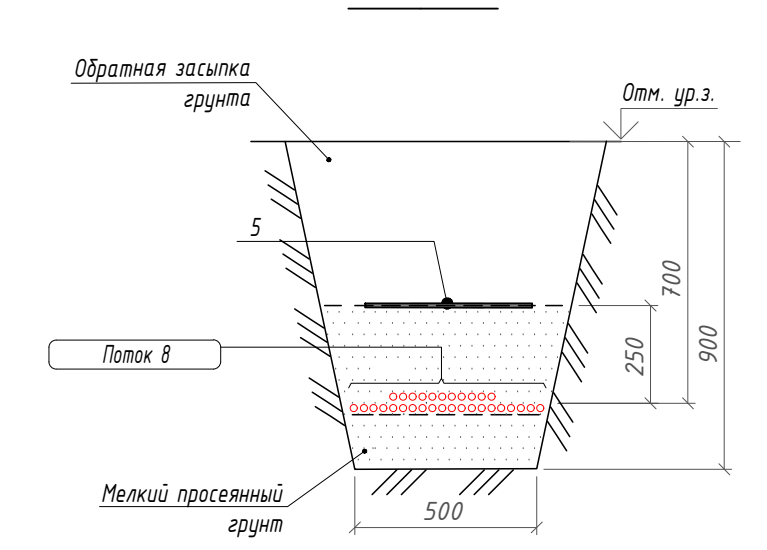

5-5 (1:20)

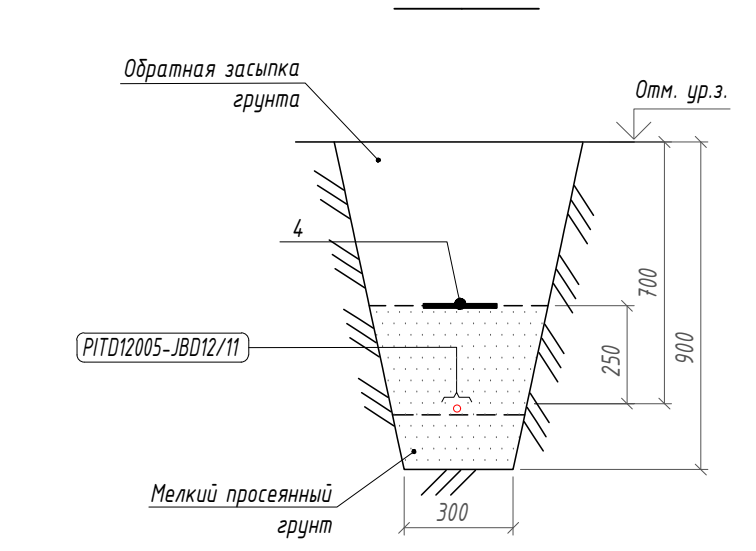

6-6 (1:20)

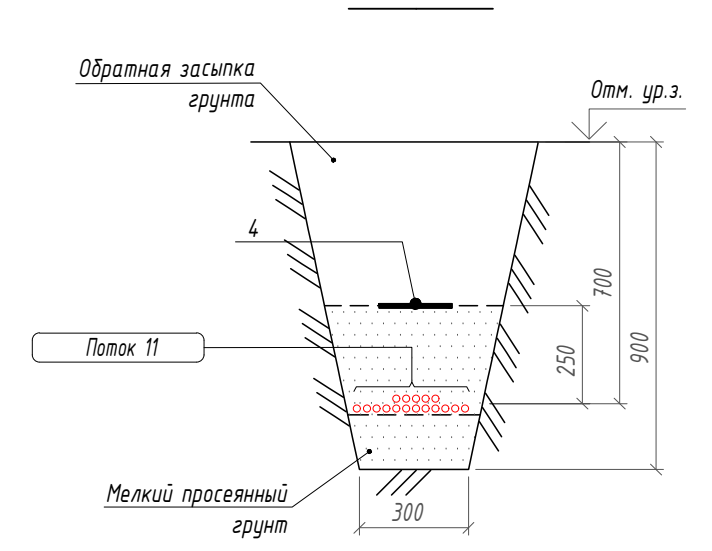

7-7 (1:20)

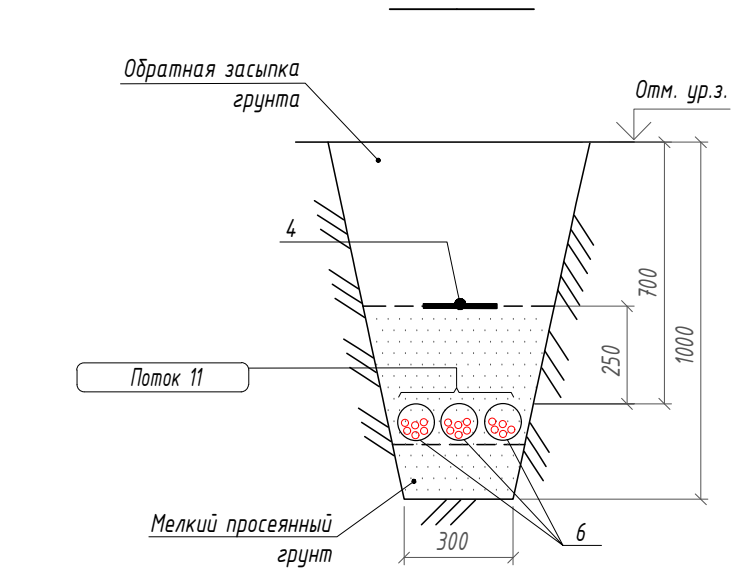

8-8 (1:20)

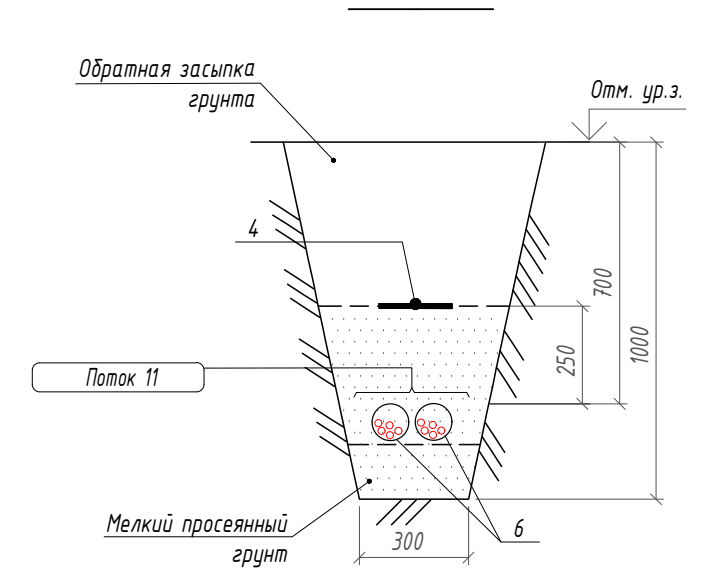

9-9 (1:20)

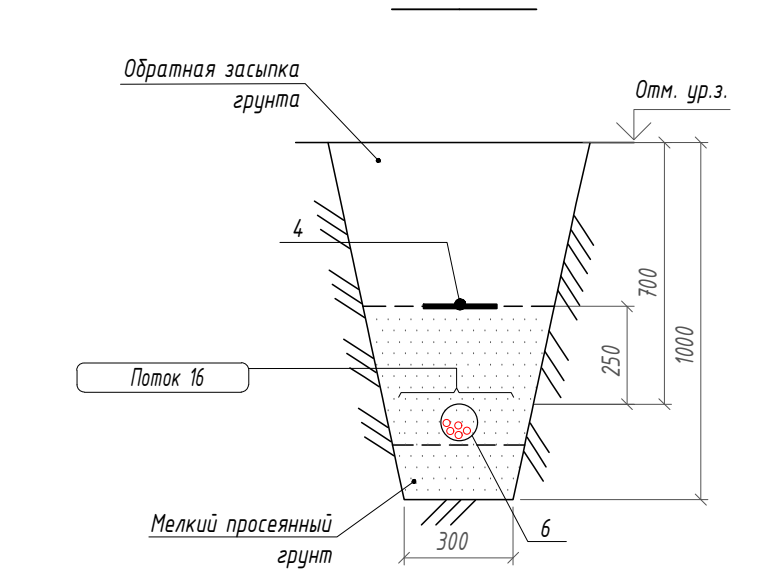

10-10 (1:20)

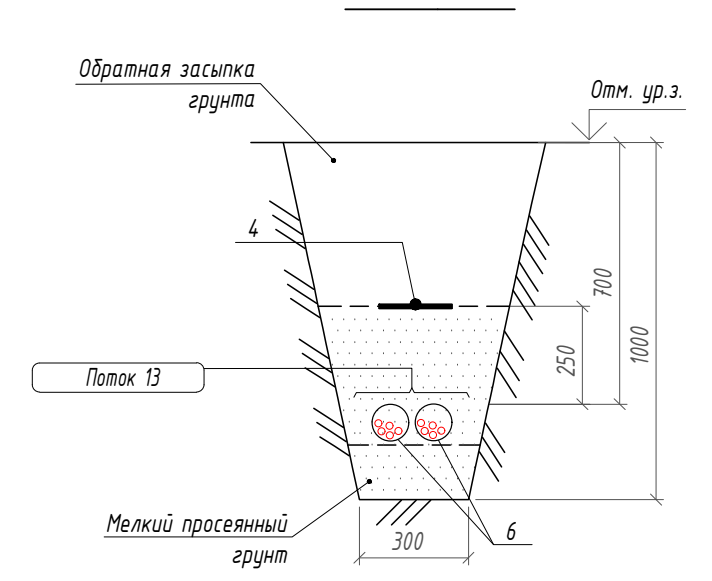

11-11 (1:20)

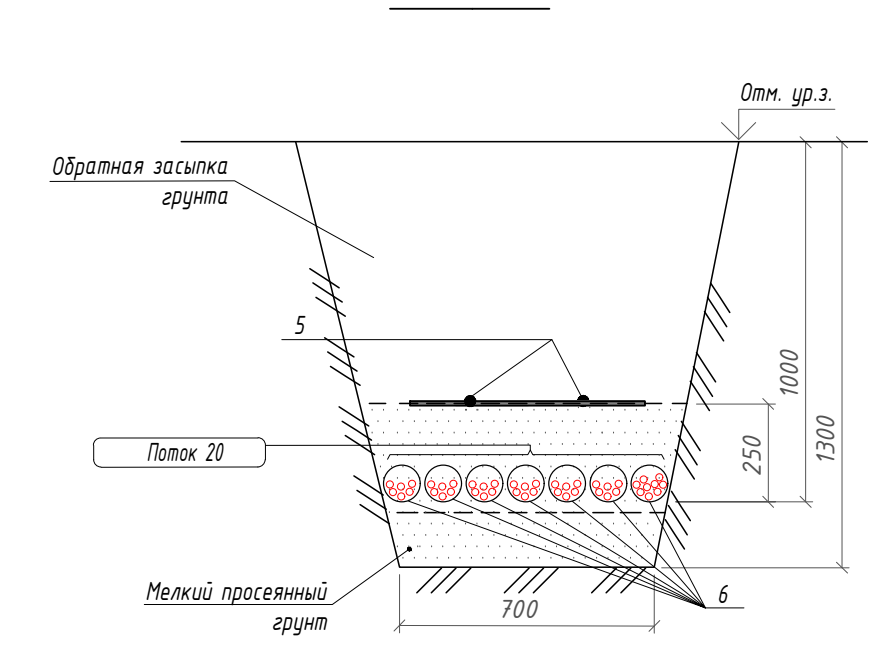

Поток 1
PITD12006-JBD12/11
XVD12004-JBD12/4
XVD12010-JBD12/4
D12CS-PLC1
D12CS-PLC2
D12AT001-PLC
D12MT001-PLC
D12MT002-PLC

Поток 2
PITD12006-JBD12/11
XVD12004-JBD12/4
XVD12010-JBD12/4
XVD12001-JBD12/2
PITD12004-JBD12/11
D12CS-PLC1
D12CS-PLC2
D12AT001-PLC
D12MT001-PLC
D12MT002-PLC

Поток 3
PITD12006-JBD12/11
XVD12004-JBD12/4
XVD12010-JBD12/4
XVD12001-JBD12/2
PITD12004-JBD12/11
XVD12006-JBD12/2
ZISD12002-JBD12/13
D12CS-PLC1
D12CS-PLC2
D12AT001-PLC
D12MT001-PLC
D12MT002-PLC

Поток 4
PITD12006-JBD12/11
XVD12004-JBD12/4
XVD12010-JBD12/4
XVD12001-JBD12/2
PITD12004-JBD12/11
XVD12006-JBD12/2
ZISD12002-JBD12/13
XVD12002-JBD12/2
PITD12002-JBD12/11
XVD12008-JBD12/2
D12CS-PLC1
D12CS-PLC2
D12AT001-PLC
D12MT001-PLC
D12MT002-PLC

Поток 5
PITD12006-JBD12/11
XVD12004-JBD12/4
XVD12010-JBD12/4
XVD12001-JBD12/2
PITD12004-JBD12/11
XVD12006-JBD12/2
ZISD12002-JBD12/13
XVD12002-JBD12/2
PITD12002-JBD12/11
XVD12008-JBD12/2
PITD12001-JBD12/11
XVD12001-JBD12/1
D12CS-PLC1
D12CS-PLC2
D12AT001-PLC
D12MT001-PLC
D12MT002-PLC

Поток 6
PITD12006-JBD12/11
XVD12004-JBD12/4
XVD12010-JBD12/4
XVD12001-JBD12/2
PITD12004-JBD12/11
XVD12006-JBD12/2
ZISD12002-JBD12/13
XVD12002-JBD12/2
PITD12002-JBD12/11
XVD12008-JBD12/2
PITD12001-JBD12/11
XVD12001-JBD12/1
ZISD12001-JBD12/13
XVD12005-JBD12/1
D12CS-PLC1
D12CS-PLC2
D12AT001-PLC
D12MT001-PLC
D12MT002-PLC

Поток 7
TITD12001-JBD12/11
XVD12004-JBD12/4
XVD12010-JBD12/4
PITD12005-JBD12/11
XVD12009-JBD12/1
JBD12/1.1-PLC
JBD12/1.2-PLC
JBD12/1.3-PLC
JBD12/1.4-PLC
JBD12/2.1-PLC
JBD12/2.2-PLC
JBD12/2.3-PLC
JBD12/2.4-PLC
JBD12/4.1-PLC
JBD12/4.2-PLC
JBD12/11-PLC
JBD12/13-PLC
D12CS-PLC1
D12CS-PLC2
D12AT001-PLC
D12MT001-PLC
D12MT002-PLC

Поток 8
TITD12001-JBD12/11
XVD12004-JBD12/4
XVD12010-JBD12/4
PITD12005-JBD12/11
XVD12009-JBD12/1
JBD12/1.1-PLC
JBD12/1.2-PLC
JBD12/1.3-PLC
JBD12/1.4-PLC
JBD12/2.1-PLC
JBD12/2.2-PLC
JBD12/2.3-PLC
JBD12/2.4-PLC
JBD12/4.1-PLC
JBD12/4.2-PLC
JBD12/11-PLC
JBD12/13-PLC
PITD12006-JBD12/11
XVD12004-JBD12/4
XVD12010-JBD12/4
XVD12001-JBD12/2
PITD12004-JBD12/11
XVD12006-JBD12/2
ZISD12002-JBD12/13
XVD12002-JBD12/2
PITD12002-JBD12/11
XVD12008-JBD12/2
PITD12001-JBD12/11
XVD12001-JBD12/1
ZISD12001-JBD12/13
XVD12005-JBD12/1

Поток 9
TITD12001-JBD12/11
XVD12004-JBD12/4
XVD12010-JBD12/4
PITD12005-JBD12/11
XVD12009-JBD12/1

Поток 10
TITD12001-JBD12/11
XVD12004-JBD12/4
XVD12010-JBD12/4

Поток 11
JBD12/1.1-PLC
JBD12/1.2-PLC
JBD12/1.3-PLC
JBD12/1.4-PLC
JBD12/2.1-PLC
JBD12/2.2-PLC
JBD12/2.3-PLC
JBD12/2.4-PLC
JBD12/4.1-PLC
JBD12/4.2-PLC
JBD12/11-PLC
JBD12/13-PLC
D12CS-PLC1
D12CS-PLC2
D12AT001-PLC
D12MT001-PLC
D12MT002-PLC

Поток 12
JBD12/8.1-PLC
JBD12/8.2-PLC
JBD12/8.3-PLC
JBD12/8.4-PLC

Поток 13
JBD12/8.1-PLC
JBD12/8.2-PLC
JBD12/8.3-PLC
JBD12/8.4-PLC
JBD12/9.1-PLC
JBD12/9.2-PLC
JBD12/9.3-PLC
JBD12/9.4-PLC
JBD12/10.1-PLC
JBD12/10.2-PLC

Поток 14
RS-FQIRD12101
RS-FQIRD12201
RS-FQIRD12301
RS-FQIRD12401
RS-FQIRD12501
JBD12/8.1-PLC
JBD12/8.2-PLC
JBD12/8.3-PLC
JBD12/8.4-PLC
JBD12/9.1-PLC
JBD12/9.2-PLC
JBD12/9.3-PLC
JBD12/9.4-PLC
JBD12/10.1-PLC
JBD12/10.2-PLC

Поток 15
RS-FQIRD12101
RS-FQIRD12201
RS-FQIRD12301

Поток 16
RS-FQIRD12101
RS-FQIRD12201
RS-FQIRD12301
RS-FQIRD12401
RS-FQIRD12501

Поток 17
JBD12/5.1-PLC
JBD12/5.2-PLC
JBD12/5.3-PLC
JBD12/5.4-PLC
JBD12/6.1-PLC
JBD12/6.2-PLC
JBD12/6.3-PLC
JBD12/6.4-PLC
JBD12/7.1-PLC
JBD12/7.2-PLC
JBD12/12-PLC

Поток 18
JBD12/5.1-PLC
JBD12/5.2-PLC
JBD12/5.3-PLC
JBD12/5.4-PLC
JBD12/6.1-PLC
JBD12/6.2-PLC
JBD12/6.3-PLC
JBD12/6.4-PLC
JBD12/7.1-PLC
JBD12/7.2-PLC

Поток 19
JBD12/5.1-PLC
JBD12/5.2-PLC
JBD12/5.3-PLC
JBD12/5.4-PLC
XVD12301-JBD12/6
XVD12303-JBD12/6

Поток 20	
JBD12/5.1-PLC	JBD12/11-PLC
JBD12/5.2-PLC	JBD12/13-PLC
JBD12/5.3-PLC	JBD12/11-PLC
JBD12/5.4-PLC	JBD12/13-PLC
JBD12/6.1-PLC	RS-FQIRD12101
JBD12/6.2-PLC	RS-FQIRD12201
JBD12/6.3-PLC	RS-FQIRD12301
JBD12/6.4-PLC	RS-FQIRD12401
JBD12/7.1-PLC	RS-FQIRD12501
JBD12/7.2-PLC	JBD12/8.1-PLC
JBD12/12-PLC	JBD12/8.2-PLC
JBD12/1.1-PLC	JBD12/8.3-PLC
JBD12/1.2-PLC	JBD12/8.4-PLC
JBD12/1.3-PLC	JBD12/9.1-PLC
JBD12/1.4-PLC	JBD12/9.2-PLC
JBD12/2.1-PLC	JBD12/9.3-PLC
JBD12/2.2-PLC	JBD12/9.4-PLC
JBD12/2.3-PLC	JBD12/10.1-PLC
JBD12/2.4-PLC	JBD12/10.2-PLC
JBD12/4.1-PLC	D12AT001-PLC
JBD12/4.2-PLC	D12MT001-PLC
D12CS-PLC1	D12MT002-PLC
D12CS-PLC2	

Поз.	Обозначение	Наименование	Кол.	Масса ед., кг	Приме-чание
1		Профиль С-образный, 41x21, L=600 мм, толщ. 2,5 мм	14	шт.	для крепления JB
2		Профиль С-образный, 41x21, L=1000 мм, толщ. 2,5 мм	2	шт.	для крепления JB
3		Винт для крепления к С-образному профилю, М10х50	48	шт.	для крепления JB
4		Лента сигнальная ЛСЭ-250	340	м	
5		Лента сигнальная ЛСЭ-450	50	м	
6		Жесткая двустенная гофрированная труба для прокладки в грунте и под автомобильными дорогами, ПНД, Ф110 мм	120	м	

Экспликация зданий и сооружений

Номер на плане	Наименование	Примечание
1	Площадка УЗРГ	
1.1	Блок качества газа	
1.2	Площадка дренажной емкости V=25м3	
1.3	Операторная	
1.6	Прожекторная мачта ПМЖ-22.8 (ПМ1)	
1.7	Прожекторная мачта ПМЖ-22.8 (ПМ1)	
1.9	Выгреб	

Условные обозначения

Обозначение	Наименование
●	Отборное устройство, первичный измерительный прибор или датчик, встраиваемый в технологическое оборудование
▬	Прибор, исполнительный механизм, электроаппаратура и другое оборудование устанавливаемое вне щита
◪	Соединительная коробка
ур.з.	Отметка уровня земли.
───	Импульсная трубная проводка
— — —	Проводка в траншее
—[– – –]—	Проводка в траншее, в защитном трубопроводе
─┘	Линия сети автоматики с указанием нумерации кабелей в соответствии со схемой внешних соединений
─┴─	Проводка в лотке по конструкциям

1. Данный чертеж составлен на основе P&ID: EWE0426-MGL1-PRE-054-SCM-610120.
2. Позиции приборов, нумерация кабелей соответствует схемам соединений внешних проводок EWE0426-MGL1-SYS-054-SCM-800302.
3. Монтаж средств автоматизации выполнить согласно КМК 3.05.07-97.
4. Конструкции лотков должны обеспечивать непрерывный электрический контакт в месте соединения прямых или фасонных секций. Все приборы, находящиеся под напряжением, заземлить согласно ПУЭ и руководствам по эксплуатации на приборы.
5. Подключение к контуру заземления конструкции лотков выполняется в электротехнической части проекта.
6. За отм. 0.000 принята отметка уровня земли. Конструкции кабельной эстакады (ригели) показаны условно (смотри строительную часть проекта).
   * - комплектная поставка УЗРГ-D001.
7. Кабельные потоки в местах опуска в траншею защитить трубой гибкой (поз. 7).
8. Во взрывоопасной зоне выполнить герметизацию прохода между кабелем и трубой с помощью набивки в трубу кабельного джута или асбестового шнура на глубину 100-120 мм с последующим заполнением уплотнительным составом толщиной не менее 10 мм и набивкой сверху кабельного джута или асбестового шнура.
9. При пересечении в земле кабелем КИП технологических трубопроводов, кабель проложить на расстоянии не менее 0,25 м в свету по вертикали от трубопровода (лотка). На участке пересечения, а также на расстоянии по 2 м в каждую сторону от него, кабель проложить в трубе ПНД двустенной гибкой.
10. Установка приборов на стойке КИПиА см. документ EWE0426-MGL1-SYS-054-DRW-800305.
11. При пересечении кабелей с подземным трубопроводом и дорогой выполнить углубление кабелей на 1м в свету от дороги и подземном трубопроводе.

Типовой чертеж установки коробки соединительной
на швеллер или опору обслуживающей площадки и трубопроводов

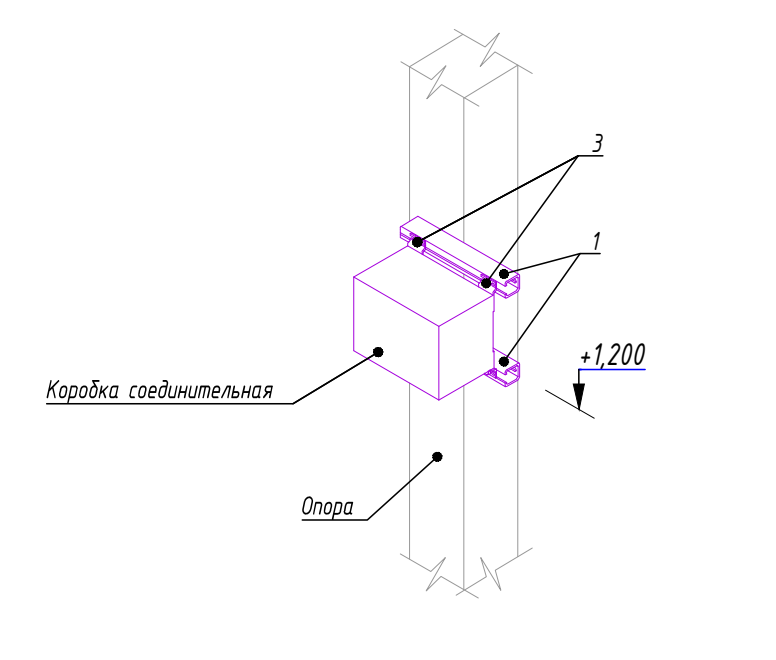

Типовой чертеж установки коробки соединительной
на стойке

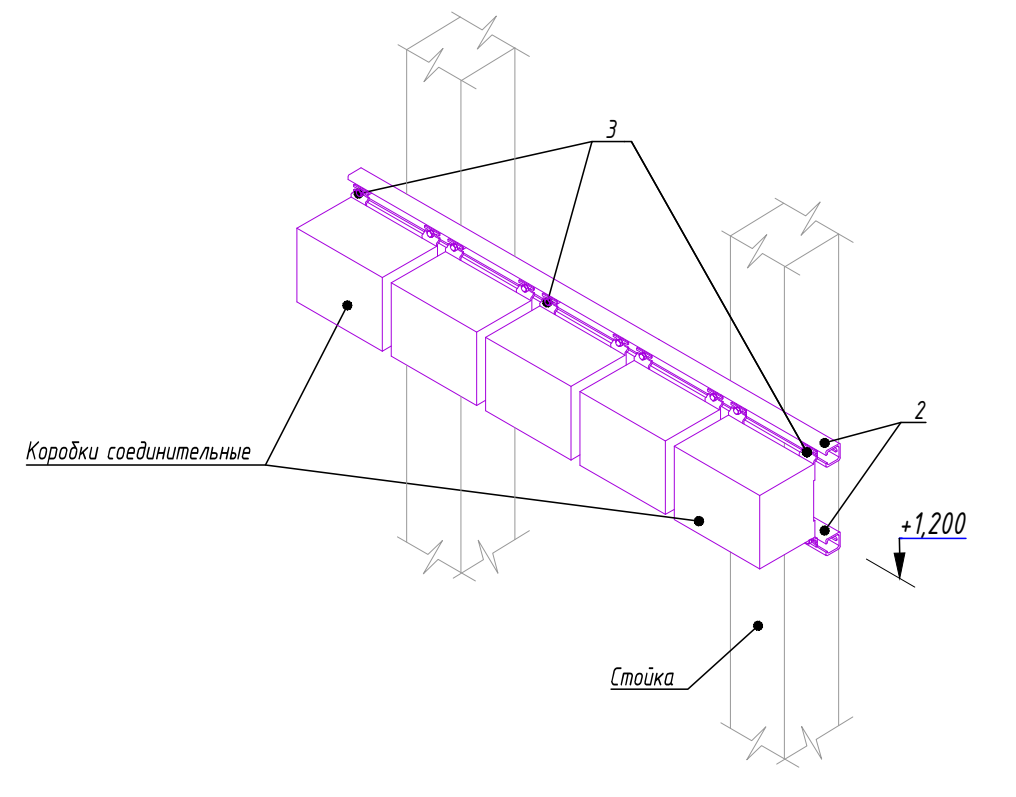

Рев.	Дата	Назначение ревизии	Проверил	Утвердил
R1	03.08.2026	Выпущено для рассмотрения		

ЗАКАЗЧИК: UTG UZTRANSGAZ
ГЕНЕРАЛЬНЫЙ ПОДРЯДЧИК: UET UZBEKENERGOTAMIR
ПОДРЯДЧИК: PBG Pro Build Generation
ГЕНЕРАЛЬНЫЙ ПРОЕКТИРОВЩИК: EAST WEST ENGINEERING

EWE0426-MGL1-SYS-054-DRW-800303-R1

«СТРОИТЕЛЬСТВО НОВЫХ НИТОК (УЧАСТКОВ) ГАЗОПРОВОДОВ «ГАЗЛИ - САРИМОЙ» И «АКЧАЛОК - ГАЗЛИ - НУКУС» ОБЩЕЙ ПРОТЯЖЕННОСТЬЮ НЕ МЕНЕЕ 275 КМ».

Изм.	Кол.уч.	Лист	№док.	Подпись	Дата
ГИП		Схабицкий А.			08.2026
Нач.отд.		Кабулова Е.			08.2026
Исполн.		Смехов Д.			08.2026
Н.контр		Схабицкий А.			08.2026

ГАЗОПРОВОД «ГАЗЛИ-САРИМОЙ» (54 КМ)
УЗРГ-D001

Стадия	Лист	Листов
РД		1

План расположения оборудования и проводок. Площадка УЗРГ -D001

ООО "EAST-WEST Engineering"
г. Ташкент 2026г.

Формат А1х3

Взам. инв. №
Подпись и дата
Инв.№ подл.