
План размещения оборудования в помещениях электрощитовой и операторной на отм. 0.000
М 1:100

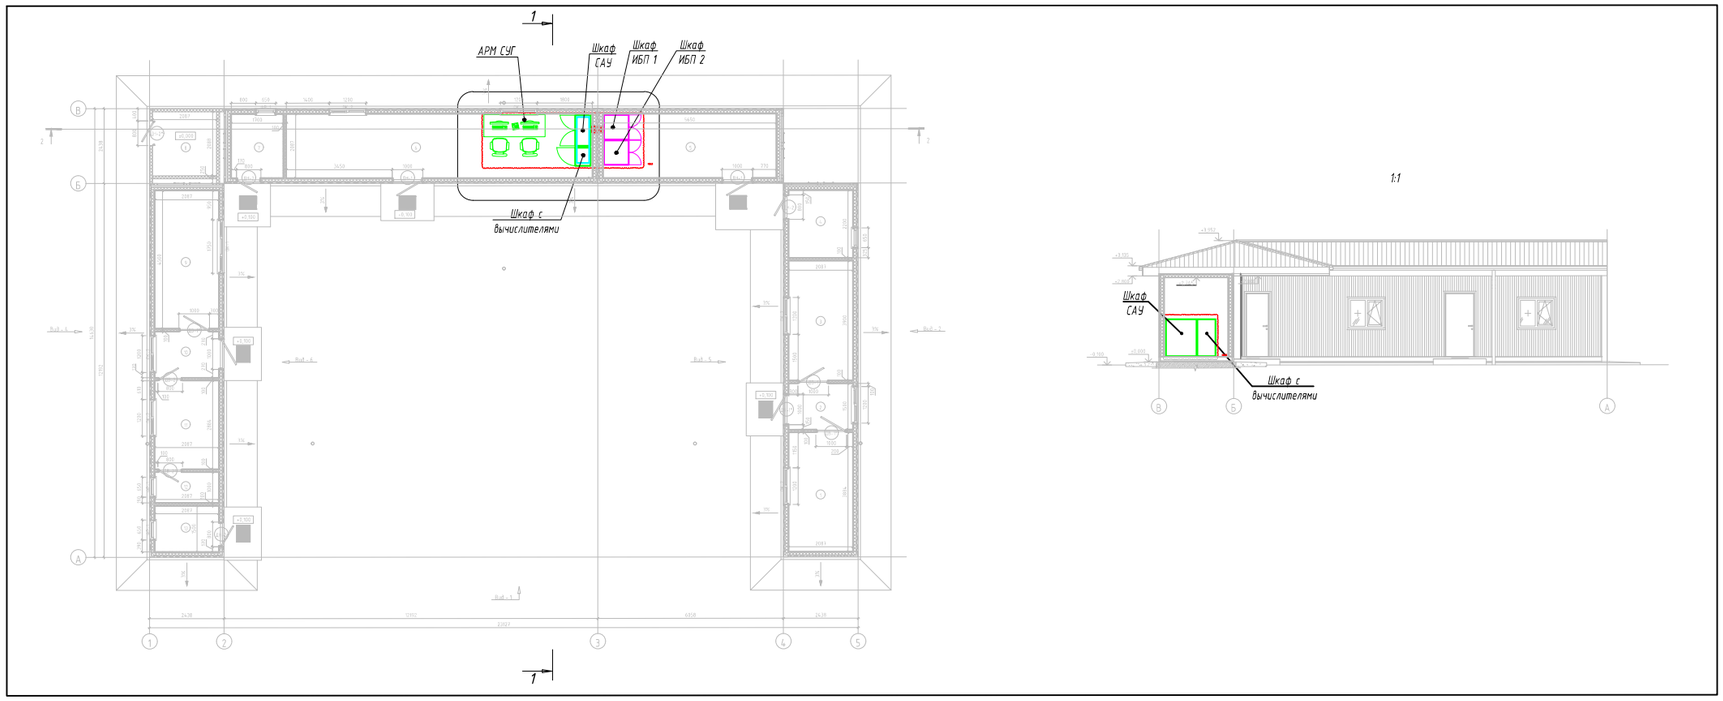


1:1

Экспликация помещений

№	Наименование	Площадь, м²	Кат. помещения
1	Кабинет ведущего инженера	8,1	?
2	Тамбур	3,1	?
3	Кабинет инженера химика	8,1	?
4	Кладовая	4,6	?
5	Электрощитовая	11,8	?
6	Кабинет операторов	20,8	?
7	Инвентарная	3,5	-
8	Насосная	4,4	?
9	Комната отдыха и приема пищи	9,4	-
10	Тамбур	3,1	?
11	Гардероб	6	?
12	Душ	2,1	-
13	С/У	3,1	-

Фрагмент А.
Расположение кабельных трасс в помещениях электрощитовой и кабинета операторов
М 1:20

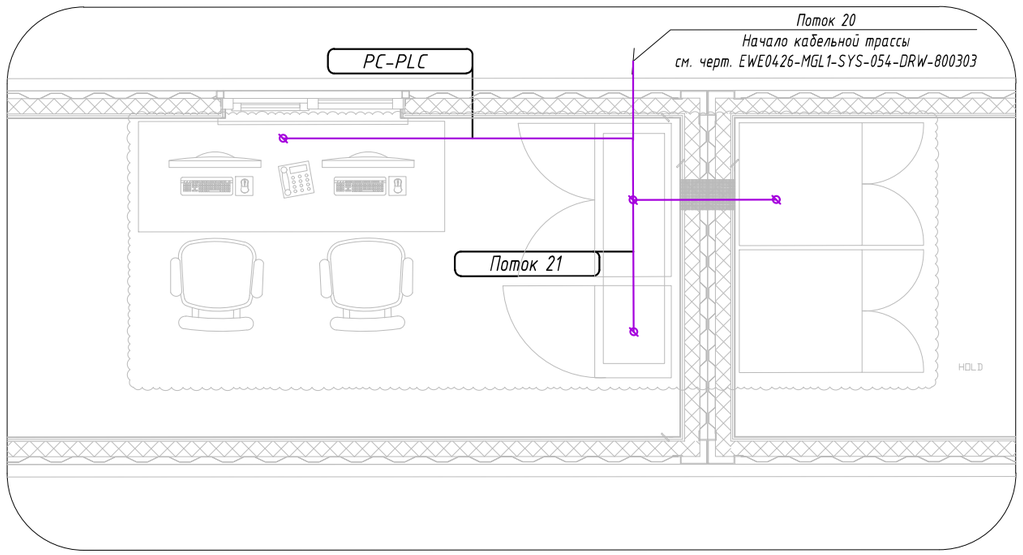

Поток 20

JBD12/5.1-PLC	JBD12/6.4-PLC	JBD12/1.4-PLC	D12CS-PLC1	RS-FQIRD12201	JBD12/8.4-PLC	D12AT001-PLC
JBD12/5.2-PLC	JBD12/7.1-PLC	JBD12/2.1-PLC	D12CS-PLC2	RS-FQIRD12301	JBD12/9.1-PLC	D12MT001-PLC
JBD12/5.3-PLC	JBD12/7.2-PLC	JBD12/2.2-PLC	JBD12/11-PLC	RS-FQIRD12401	JBD12/9.2-PLC	D12MT002-PLC
JBD12/5.4-PLC	JBD12/12-PLC	JBD12/2.3-PLC	JBD12/13-PLC	RS-FQIRD12501	JBD12/9.3-PLC	
JBD12/6.1-PLC	JBD12/1.1-PLC	JBD12/2.4-PLC	JBD12/11-PLC	JBD12/8.1-PLC	JBD12/9.4-PLC	
JBD12/6.2-PLC	JBD12/1.2-PLC	JBD12/4.1-PLC	JBD12/13-PLC	JBD12/8.2-PLC	JBD12/10.1-PLC	
JBD12/6.3-PLC	JBD12/1.3-PLC	JBD12/4.2-PLC	RS-FQIRD12101	JBD12/8.3-PLC	JBD12/10.2-PLC	

Поток 21

RS-FQIRD12101	FQIRD12101-PLC
RS-FQIRD12201	FQIRD12201-PLC
RS-FQIRD12301	FQIRD12301-PLC
RS-FQIRD12401	FQIRD12401-PLC
RS-FQIRD12501	FQIRD12501-PLC

1. Нумерация кабелей соответствует схемам соединений внешних проводок, шифр EWE0426-MGL1-SYS-054-SCM-800302
   Оборудование, входящее в комплект поставки системы САУ УЗРГ-D001 согласно "Опросный лист. Узел замера расхода газа УЗРГ-C001", шифр EWE0426-MGL1-PRE-054-DSH-610116:
   -Шкаф САУ - шкаф системы САУ УЗРГ;
   -Шкаф с вычислителями
   -АРМ СУГ - автоматизированное рабочее место оператора УЗРГ;
   -столы и кресла под установку вышеперечисленного оборудования.
2. Монтаж защитного заземления выполнить в соответствии с требованиями ПУЭ.

Рев.	Дата	Назначение ревизии	Проверил	Утвердил
R1	03.08.2026	Выпущено для рассмотрения		

ЗАКАЗЧИК: UTG UZKIMYOSANOAT | ГЕНЕРАЛЬНЫЙ ПОДРЯДЧИК: UET UZBEKENERGOTAMIR | ПОДРЯДЧИК: PBG Pro Build Generation | ГЕНЕРАЛЬНЫЙ ПРОЕКТИРОВЩИК: EAST WEST ENGINEERING

Изм.	Кол.уч.	Лист	№док.	Подпись	Дата
ГИП		Схабицкий А.			08.2026
Нач.отд.		Кабулова Е.			08.2026
Исполн.		Смехов Д.			08.2026
Н.контр		Схабицкий А.			08.2026

EWE0426-MGL1-SYS-054-DRW-800304-R1

«СТРОИТЕЛЬСТВО НОВЫХ НИТОК (УЧАСТКОВ) ГАЗОПРОВОДОВ «ГАЗЛИ - САРИМОЙ» И «АКЧАЛОК - ГАЗЛИ - НУКУС» ОБЩЕЙ ПРОТЯЖЕННОСТЬЮ НЕ МЕНЕЕ 275 КМ».

ГАЗОПРОВОД «ГАЗЛИ-САРИМОЙ» (54 КМ) УЗРГ-D001

Стадия	Лист	Листов
РД		1

План расположения оборудования и проводок. Операторная

EAST WEST ENGINEERING

ООО "EAST-WEST Engineering"
г. Ташкент 2026г.

Взам. инв. №
Подпись и дата
Инв.№ подл.

Формат А3