Таблица 1

Позиция прибора	Место установки
Узел замера расхода газа УЗРГ -D001: EWE0426-MGL1-PRE-054-SCM-610120	
PG-D12-001	Трубопровод 1200-GT-63CS00-HH-D12001
PG-D12-002	Трубопровод 1200-GT-63CS00-HH-D12001
PG-D12-003	Трубопровод 1200-GT-63CS00-N-D12002
PG-D12-004	Трубопровод 1200-GT-63CS00-N-D12005
PG-D12-005	Трубопровод 1200-GT-63CS00-N-D12002
PG-D12-006	Трубопровод 1200-GT-63CS00-N-D12005
PG-D12-101	Трубопровод 400-GT-63CS00-N-D12101
PG-D12-201	Трубопровод 400-GT-63CS00-N-D12201
PG-D12-301	Трубопровод 400-GT-63CS00-N-D12301
PG-D12-401	Трубопровод 400-GT-63CS00-N-D12401
PG-D12-501	Трубопровод 400-GT-63CS00-N-D12501
PG-D12-007	Трубопровод 100-DC-63CS00-HH-D12029
PG-D12-008	Трубопровод 80-DC-16CS00-EH-D12031

Поз.	Обозначение	Наименование	Кол.	Масса ед, кг	Примечание
1	См. таблицу 1	Манометр для установки на вертикальном трубопроводе	1		
2		Двухвентильный блок	1		в компл. с датчиком
3	OC-16-02-Ш(В)-Ш(Н)-1/2NPT-1/2NPT-Ац-Б	Трубка угловая. Присоединение со стороны процесса - наружная резьба 1/2'' NPT-M, присоединение со стороны датчика - внутренняя резьба 1/2'' NPT-F	1		

Установочный чертеж манометра на горизонтальном трубопроводе (среда Жидкость)

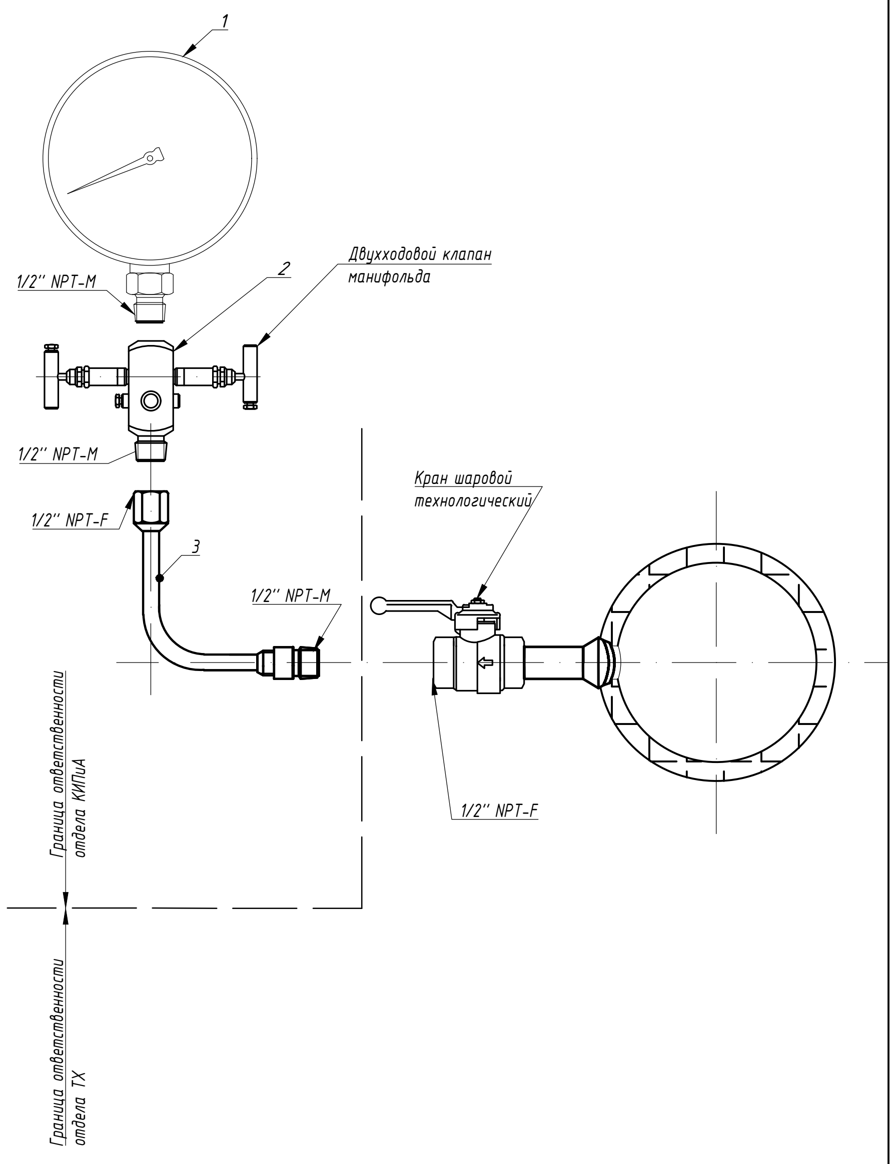
1
1/2'' NPT-M
2
Двухходовой клапан манифольда
1/2'' NPT-M
1/2'' NPT-F
3
1/2'' NPT-M
Кран шаровой технологический
1/2'' NPT-F
Граница ответственности отдела КИПиА
Граница ответственности отдела ТХ

Установочный чертеж манометра на горизонтальном трубопроводе (среда Газ)

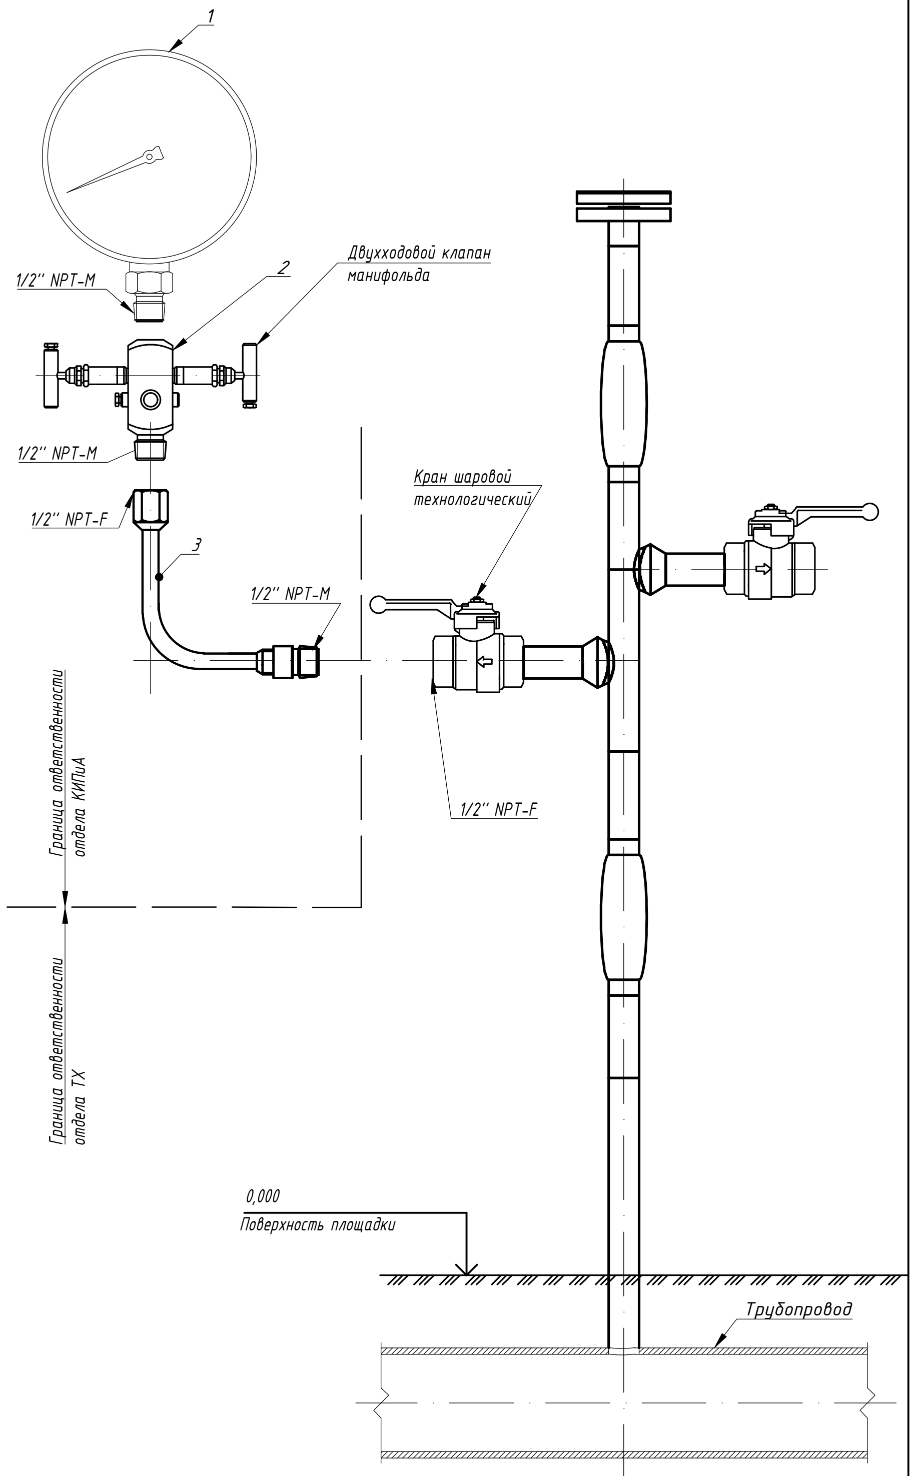
1
1/2'' NPT-M
2
Двухходовой клапан манифольда
1/2'' NPT-M
1/2'' NPT-F
3
Кран шаровой технологический
1/2'' NPT-M
1/2'' NPT-F
Граница ответственности отдела КИПиА
Граница ответственности отдела ТХ
0,000
Поверхность площадки
Трубопровод

1. По данному чертежу смонтировать позиции указанные в Таблице 1.
2. Позиции приборов соответствуют схеме P&ID (указанной в таблице).
3. Количество монтажных изделий показано для одного манометра.

Взам. инв. №

Подпись и дата

Инв.№ подл.

Рев.	Дата	Назначение ревизии	Проверил	Утвердил
R1	03.08.2026	Выпущено для рассмотрения		

ЗАКАЗЧИК:
ГЕНЕРАЛЬНЫЙ ПОДРЯДЧИК:
ПОДРЯДЧИК:
ГЕНЕРАЛЬНЫЙ ПРОЕКТИРОВЩИК:

EWE0426-MGL1-SYS-054-DRW-800305-R1

«СТРОИТЕЛЬСТВО НОВЫХ НИТОК (УЧАСТКОВ) ГАЗОПРОВОДОВ «ГАЗЛИ - САРИМОЙ» И «АКЧАЛОК - ГАЗЛИ - НУКУС» ОБЩЕЙ ПРОТЯЖЕННОСТЬЮ НЕ МЕНЕЕ 275 КМ».

Изм.	Кол.уч.	Лист	№док.	Подпись	Дата
ГИП		Схабицкий А.			08.2026
Нач.отд.		Кабулова Е.			08.2026
Исполн.		Смехов Д.			08.2026
Н.контр		Схабицкий А.			08.2026

ГАЗОПРОВОД «ГАЗЛИ-САРИМОЙ» (54 КМ)
УЗРГ-D001

Стадия	Лист	Листов
РД	1	5

Установочный чертеж КИП

ООО "EAST-WEST Engineering"
г. Ташкент 2026г.

Формат А3

Таблица 2

Позиция прибора	Место установки	Номер импульсной линии
Узел замера расхода газа УЗРГ-D001: EWE0426-MGL1-PRE-054-SCM-610120		
PIT-D12-001	Трубопровод 1200-GT-63CS00-HH-D12001	D12-001
PIT-D12-002	Трубопровод 1200-GT-63CS00-HH-D12001	D12-002
PIT-D12-003	Трубопровод 1200-GT-63CS00-N-D12002	D12-003
PIT-D12-004	Трубопровод 1200-GT-63CS00-N-D12005	D12-004
PIT-D12-005	Трубопровод 1200-GT-63CS00-N-D12002	D12-005
PIT-D12-006	Трубопровод 1200-GT-63CS00-N-D12005	D12-006

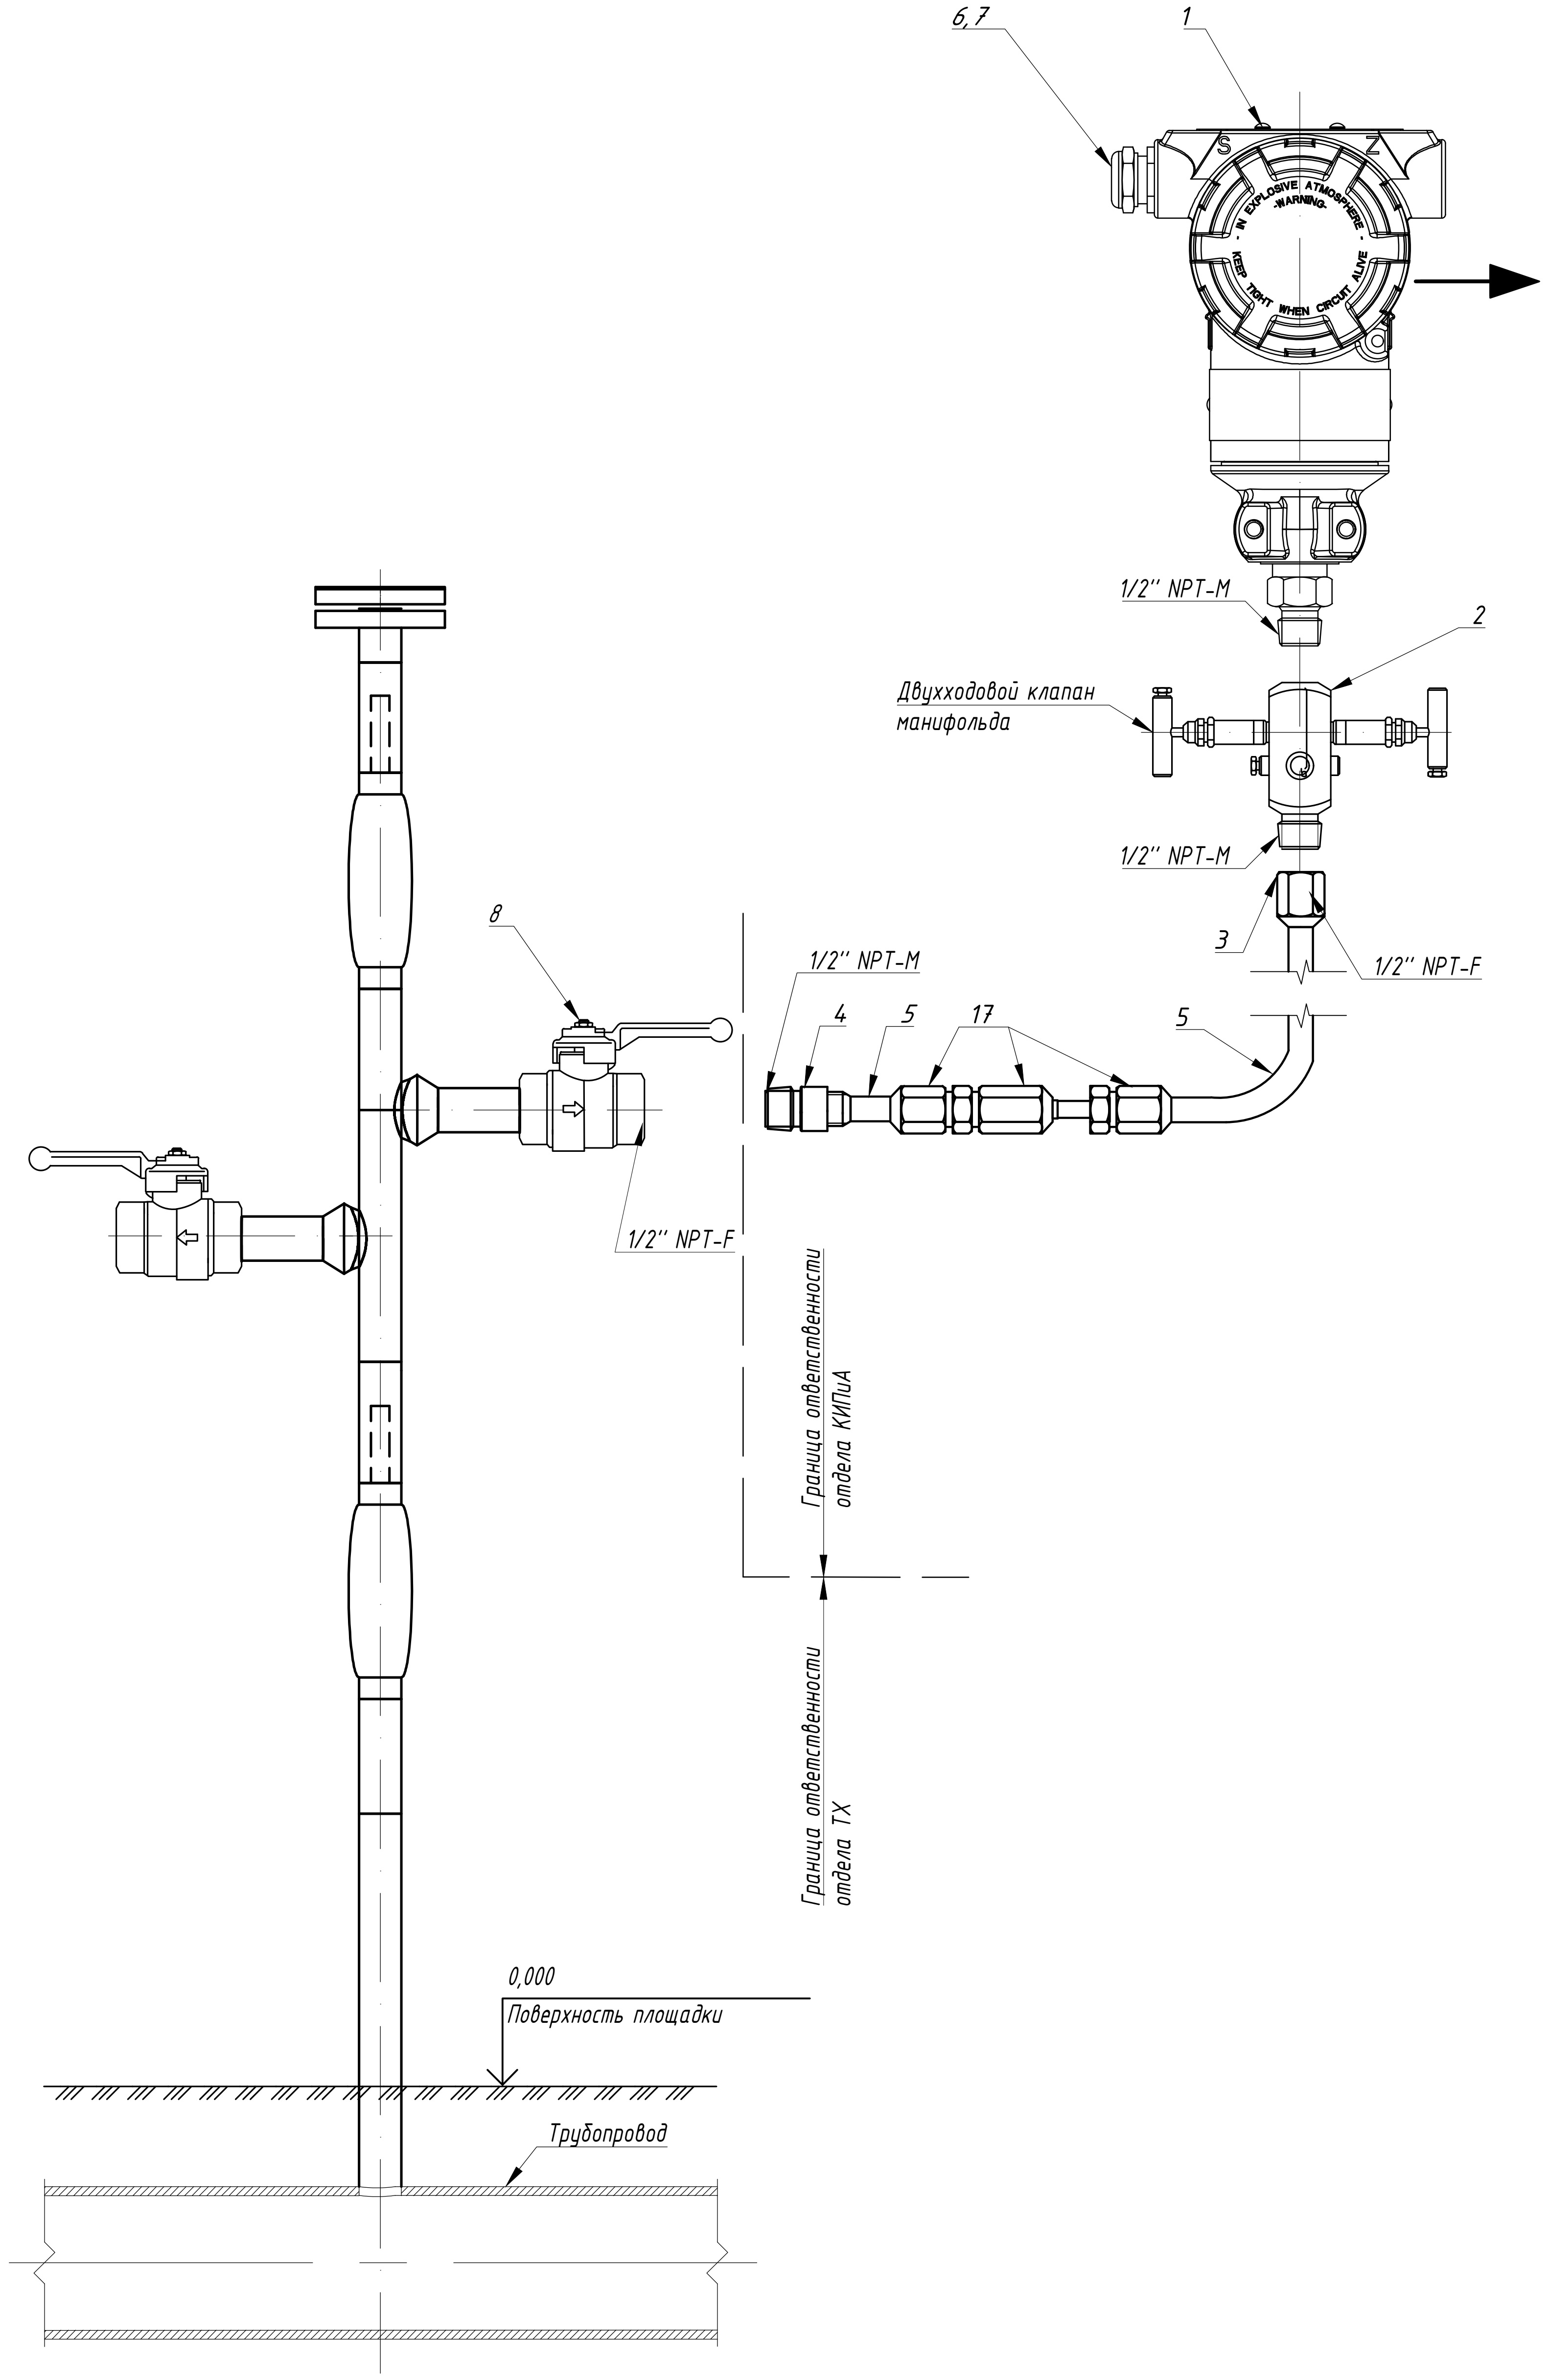
6,7
1
1/2'' NPT-M
2
Двухходовой клапан манифольда
1/2'' NPT-M
3
1/2'' NPT-F
1/2'' NPT-M
4
5
17
5
8
1/2'' NPT-F
Граница ответственности отдела КИПиА
Граница ответственности отдела ТХ
0,000
Поверхность площадки
Трубопровод

Стойка приборная КИПиА 1:5

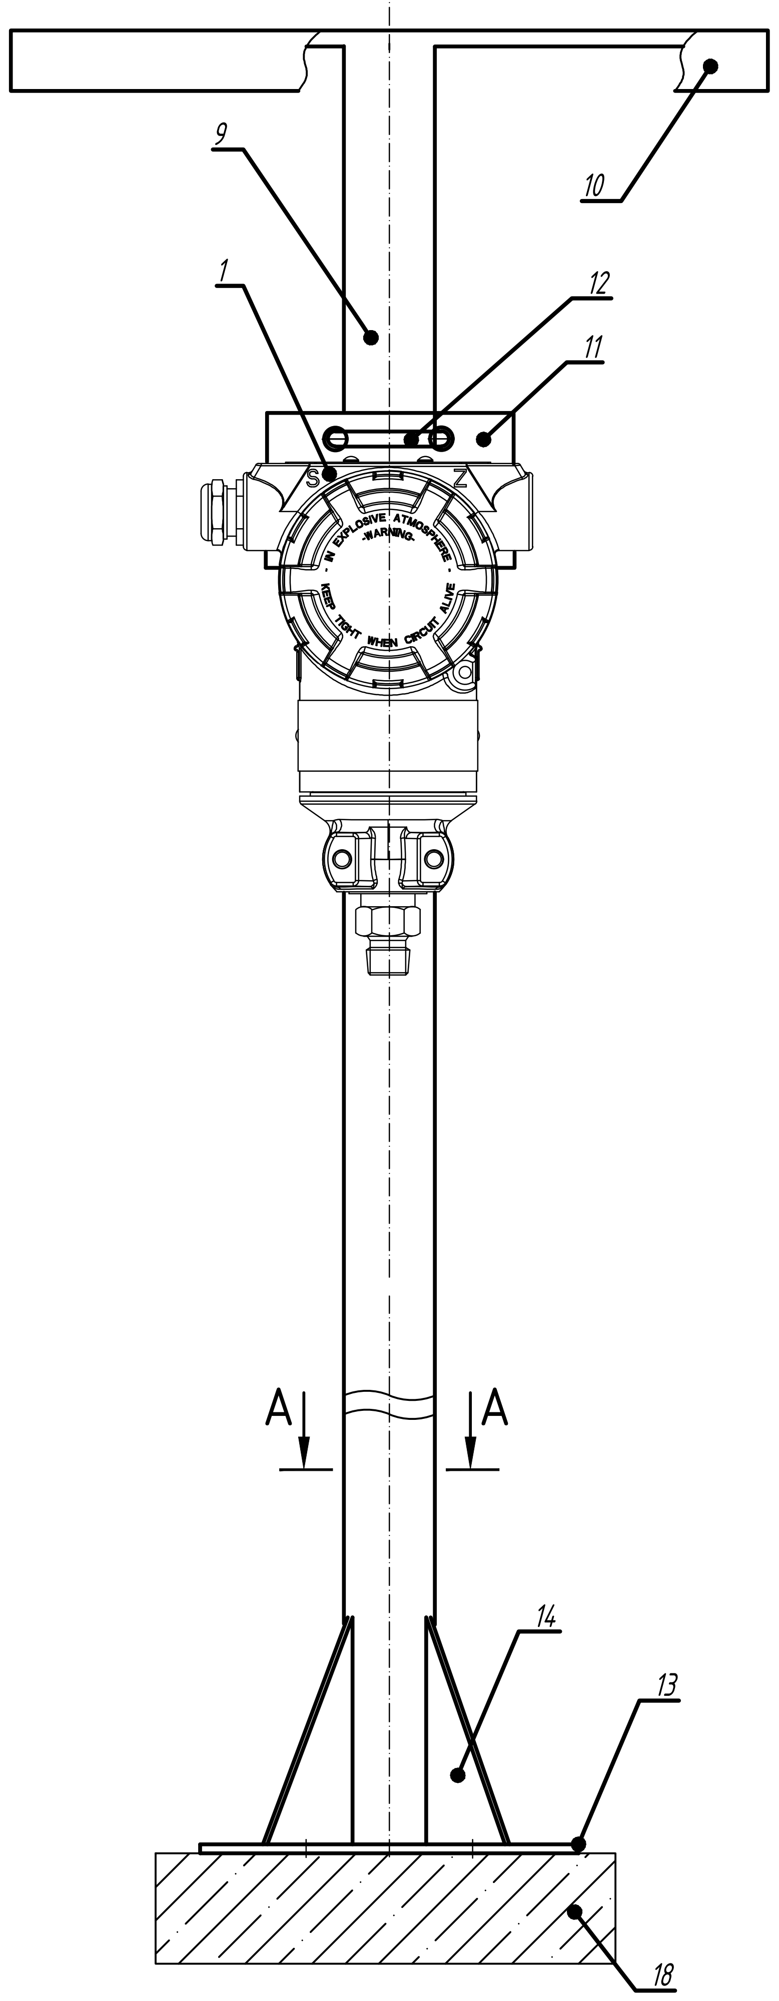
9
10
1
12
11
A
A
14
13
18

А-А

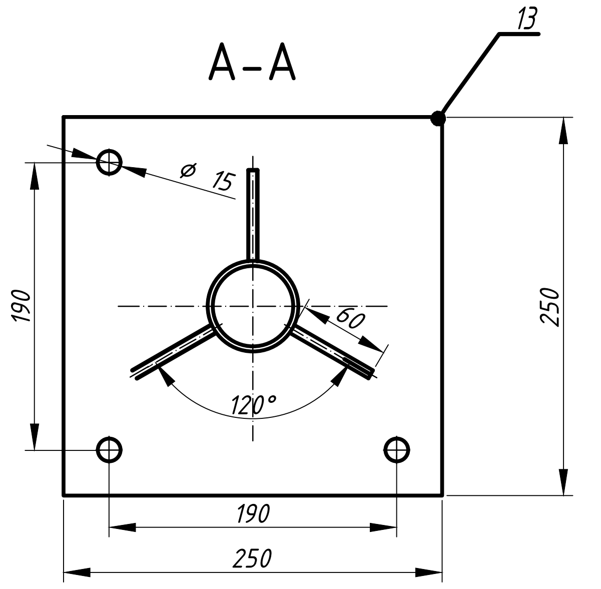
13
⌀ 15
60
120°
190
250
190
250

Поз.	Обозначение	Наименование	Кол.	Масса ед, кг	Примечание
1	См. таблицу 2	Преобразователь давления	1		
2		Двухвентильный блок	1		в компл. с датчиком
3	SS-810-7-8RG	Трубный обжимной фитинг Swagelok из нерж. стали, соединитель с внутренней резьбой, диам. трубки 1/2 дюйма – внутр. резьба NPT 1/2 дюйма.	1		
4	SS-810-1-8	Трубный обжимной фитинг Swagelok из нерж. стали, соединитель с наруж. резьбой, наруж. диам. трубки 1/2 дюйма – наруж. резьба NPT 1/2 дюйма.	1		
5		Импульсная трубка 1/2x0,049; 12X18H10T, Swagelok	2		м
6		Кабельный ввод M20x1.5	1		комплектно с датчиком
7		Кабельная заглушка M20x1.5	1		
8		Шаровой кран	1		см. технол. часть проекта
9		Труба оцинкованная Ц-50x3,5 ГОСТ 3262-75	1,8		м
10		Сталь листовая, 500x500 $\frac{800x500\ ГОСТ\ 19903-74}{ОК\ 360В-1\ ГОСТ\ 16523-97}$	1		
11		Сталь листовая, 102x164 $\frac{800x500\ ГОСТ\ 19903-74}{ОК\ 360В-1\ ГОСТ\ 16523-97}$	1		
12		Хомут Х50 ТУ 34-1107-80	1		
13		Плита опорная 300x300x10	1		
14		Лист 2x400x500 ГОСТ19903-74/ОК 360В-1 ГОСТ 16523-97	2		
15		Кабельный наконечник AHI DIN N $^6/_{12}$	2		LAPP GROUP
16		Провод ПВ3 - 1x6 ГОСТ 6323-79 (для заземления)	1,5		м
17	SS-8-DE-6	Муфта проходная диэлектрическая на трубку 1/2" (Swagelock)	1		
18		Бетон марки M200 (300x300x400)мм		0,036	$м^3$
19		Болт анкерный	4	шт	

1. По данному чертежу смонтировать на стойку позиции указанные в таблице.
2. Позиции приборов соответствуют схеме P&ID (указанной в таблице).
3. Количество монтажных изделий показано для одного датчика давления.

Взам. инв. N
Подп. и дата
Инв. N подл.

Изм.	Кол.	Лист	N°док.	Подпись	Дата	EWE0426-MGL1-SYS-054-DRW-800305-R1	Лист 2

Формат A2

Установочный чертеж термометра показывающего на горизонтальном трубопроводе

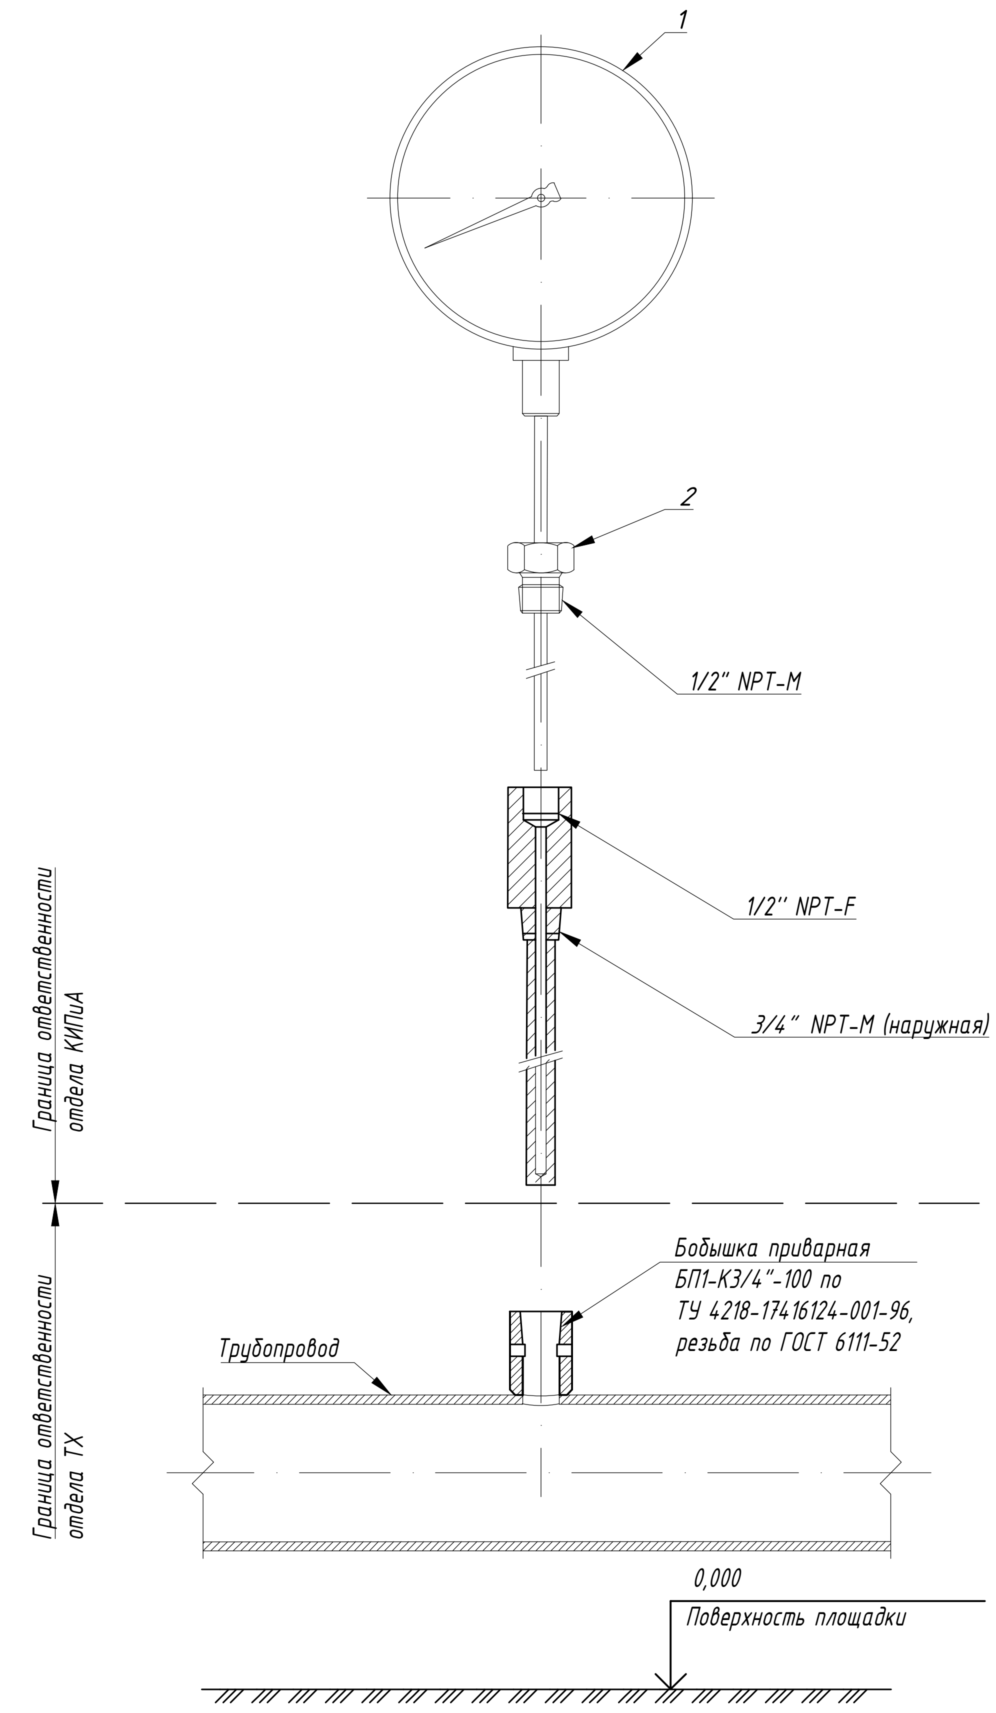
1
2
1/2" NPT-M
1/2" NPT-F
3/4" NPT-M (наружная)
Граница ответственности отдела КИПиА
Граница ответственности отдела ТХ
Бобышка приварная БП1-К3/4"-100 по ТУ 4218-17416124-001-96, резьба по ГОСТ 6111-52
Трубопровод
0,000
Поверхность площадки

Поз.	Обозначение	Наименование	Кол.	Масса ед, кг	Примечание
1	См. таблицу 3	Термометр показывающий	1		
2		Защитная гильза	1		в компл. с прибором

Таблица 3	
Позиция прибора	Место установки
Узел замера расхода газа УЗРГ-D001: EWE0426-MGL1-PRE-054-SCM-610120	
TG-D12-101	Трубопровод 400-GT-63CS00-N-D12101
TG-D12-201	Трубопровод 400-GT-63CS00-N-D12201
TG-D12-301	Трубопровод 400-GT-63CS00-N-D12301
TG-D12-401	Трубопровод 400-GT-63CS00-N-D12401
TG-D12-501	Трубопровод 400-GT-63CS00-N-D12501

1. По данному чертежу смонтировать позиции указанные в таблице.
2. Позиции приборов соответствуют схеме P&ID (указанной в таблице).

Взам. инв. N

Подп. и дата

Инв. N подл.

						EWE0426-MGL1-SYS-054-DRW-800305-R1	Лист
Изм.	Кол.	Лист	N°док.	Подпись	Дата		3

Формат А3

Таблица 4

Позиция прибора	Место установки
Узел замера расхода газа УЗРГ-D001: EWE0426-MGL1-PRE-054-SCM-610120	
TIT-D12-001	Трубопровод 1200-GT-63CS00-HH-D12001

Стойка приборная КИПиА 1:5

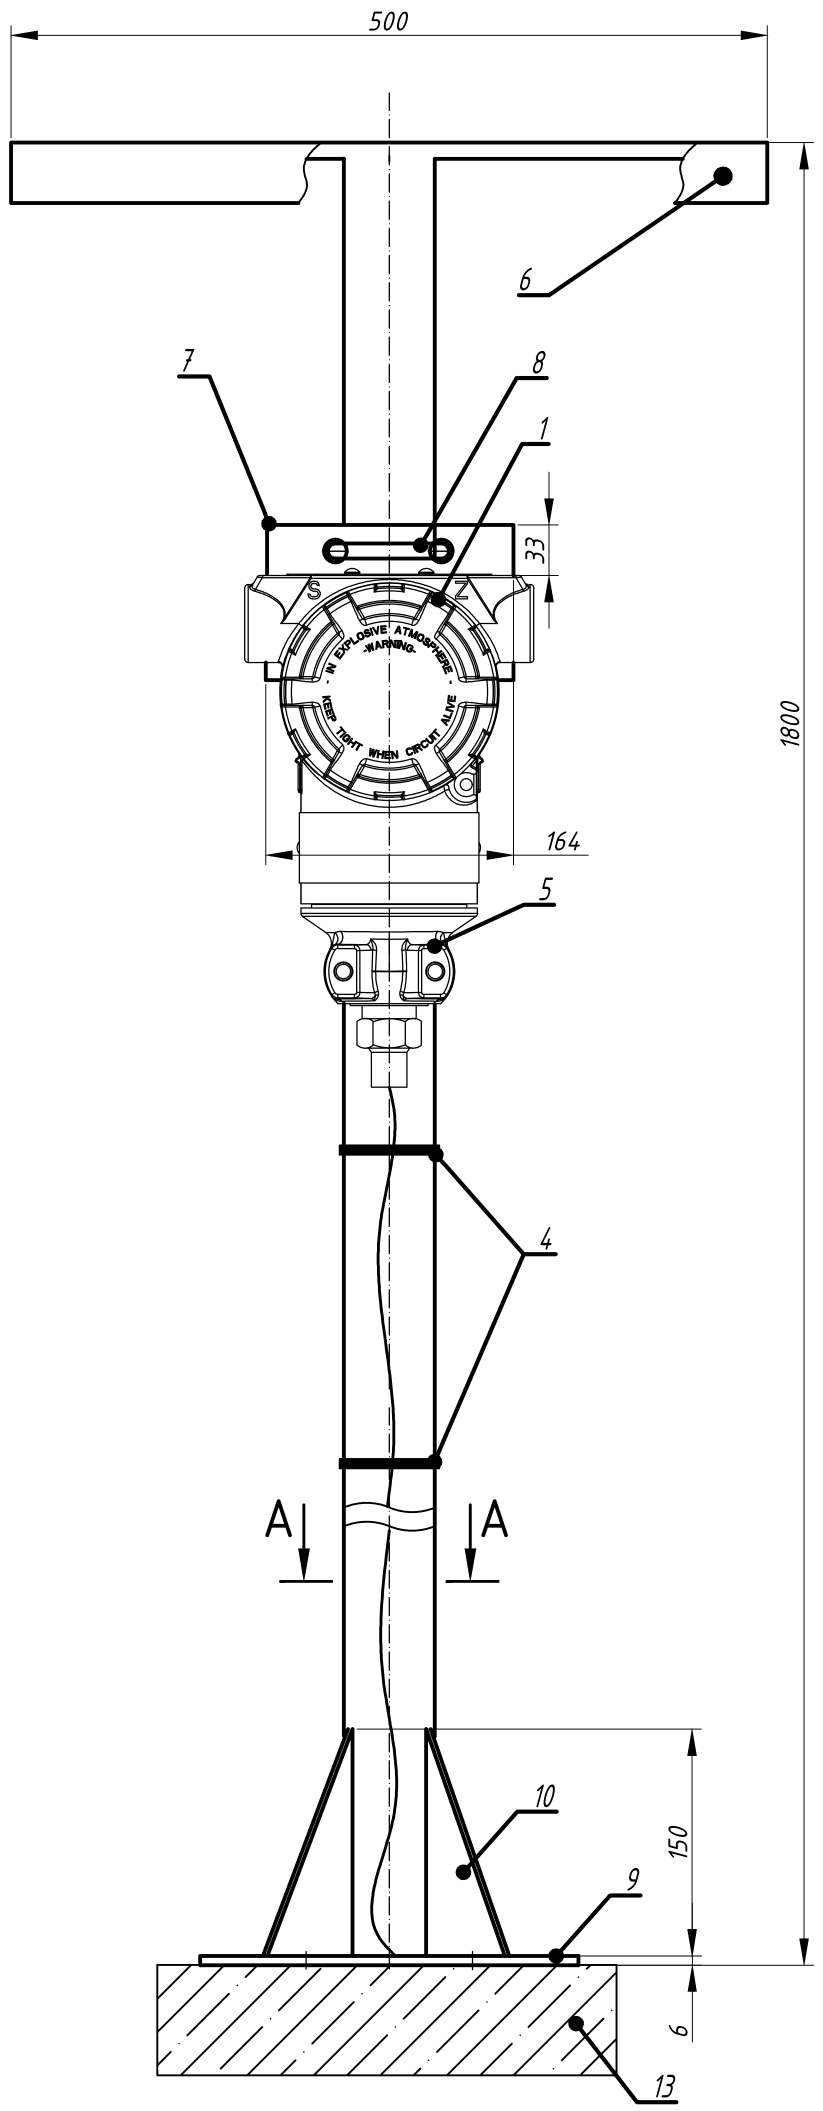

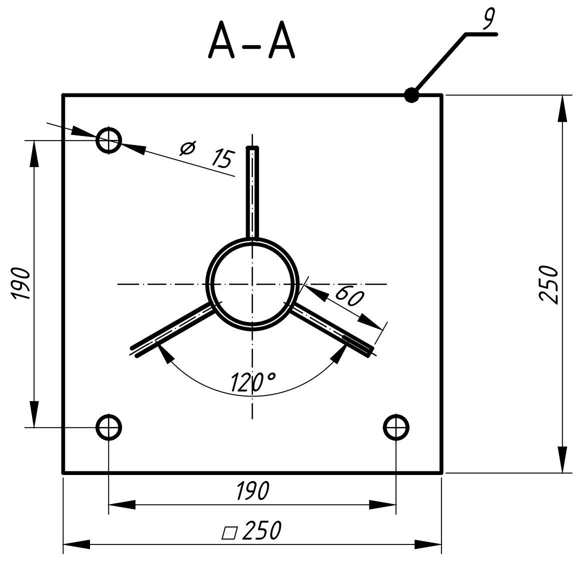

Установочный чертеж термопреобразователя

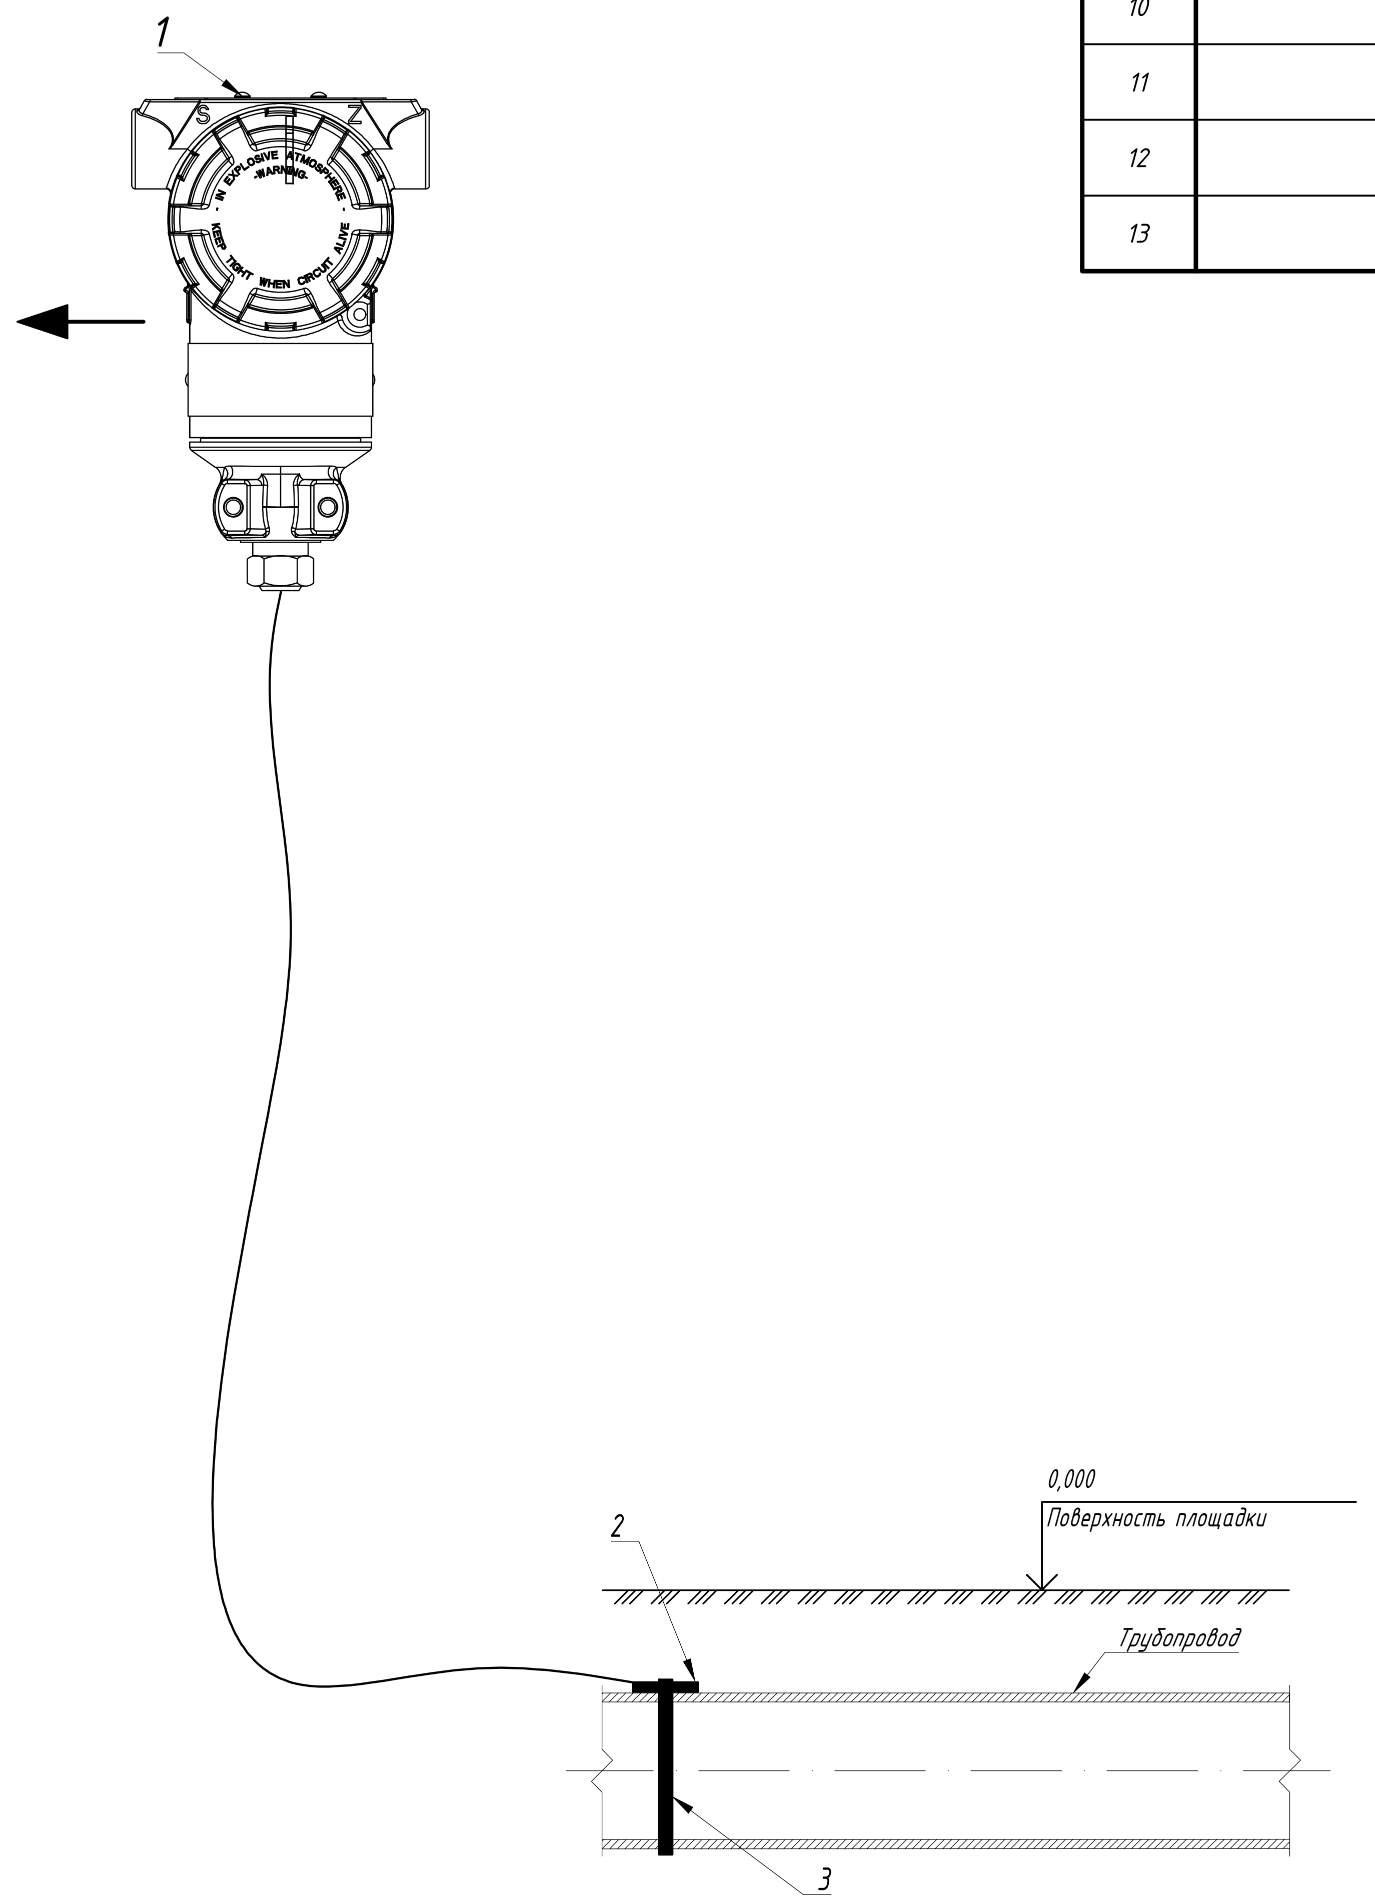

Поз.	Обозначение	Наименование	Кол.	Масса ед, кг	Примечание
1	См. таблицу 4	Термопреобразователь	1		
2		Сенсор термопреобразователя	1		в компл. с датчиком
3		Хомут для сенсора термопреобразователя	1		
4		Хомут червячный (металлический) Ф100 мм для крепления к трубе кабеля от сенсора к датчику	2		
5		Труба оцинкованная Ц-50х3,5 ГОСТ 3262-75	1,8		м
6		Сталь листовая, 500х500 800х500 ГОСТ 19903-74 ОК 360В-1 ГОСТ 16523-97	1		
7		Сталь листовая, 102х164 800х500 ГОСТ 19903-74 ОК 360В-1 ГОСТ 16523-97	1		
8		Хомут Х50 ТУ 34-1107-80	1		
9		Плита опорная 300х300х10	1		
10		Лист 2х400х500 ГОСТ19903-74/ОК 360В-1 ГОСТ 16523-97	2		
11		Кабельный наконечник AHI DIN N 6/12	2		LAPP GROUP
12		Провод ПВ3 - 1х6 ГОСТ 6323-79 (для заземления)	1,5		м
13		Бетон марки М200 (300х300х400)мм		0,036	$м^3$

1. По данному чертежу смонтировать на стойку позиции указанные в таблице.
2. Позиции приборов соответствуют схемам P&ID (указанным в таблицах) и заказной спецификации.
3. Количество монтажных изделий показано для одного термопреобразователя.

Взам. инв. N

Подп. и дата

Инв. N подл.

Изм.	Кол.	Лист	N°док.	Подпись	Дата

Таблица 5

Позиция прибора	Место установки
Узел замера расхода газа УЗРГ-D001: EWE0426-MGL1-PRE-054-SCM-610120	
ZIS-D12-001	Трубопровод 11200-GT-63CS00-HH-D12001
ZIS-D12-002	Трубопровод 11200-GT-63CS00-HH-D12001

Поз.	Обозначение	Наименование	Кол.	Масса ед, кг	Примечание
1	См. таблицу 6	Сигнализатор прохождения очистного устройства с клеммной коробкой	1		
2		Антенна сигнализатора	1		в компл. с сигнализатором
3		Гибкий кабель до антенны 5м	1		
4		Металлический крепежный хомут с изолирующей прослойкой	2		
5		Защитная коробка	1		
6		Козырек	1		
7		Профиль С-образный, 41х21, L=600 мм, толщ. 2,5 мм	2		
8		Хомут Х50 ТУ 34-1107-80	2		
9		Труба оцинкованная Ц-50х3,5 ГОСТ 3262-75	1,8		м
10		Хомут червячный (металлический) Ф100 мм для крепления к трубе кабеля от сенсора к датчику	2		
11		Лист 2х400х500 ГОСТ 19903-74/ОК 360В-1 ГОСТ 16523-97	2		
12		Плита опорная 300х300х10	1		
13		Бетон марки М200 (300х300х400)мм		0,036	$м^3$
14		Труба ПНД гибкая для кабельной канализации Ф50 с протяжкой. ТУ 2248-015-47022248-2006	5		м
15		Болт анкерный	4		
16		Провод ПВЗ - 1х6 ГОСТ 6323-79 (для заземления)	1,5		м

Стойка приборная КИПиА 1:5

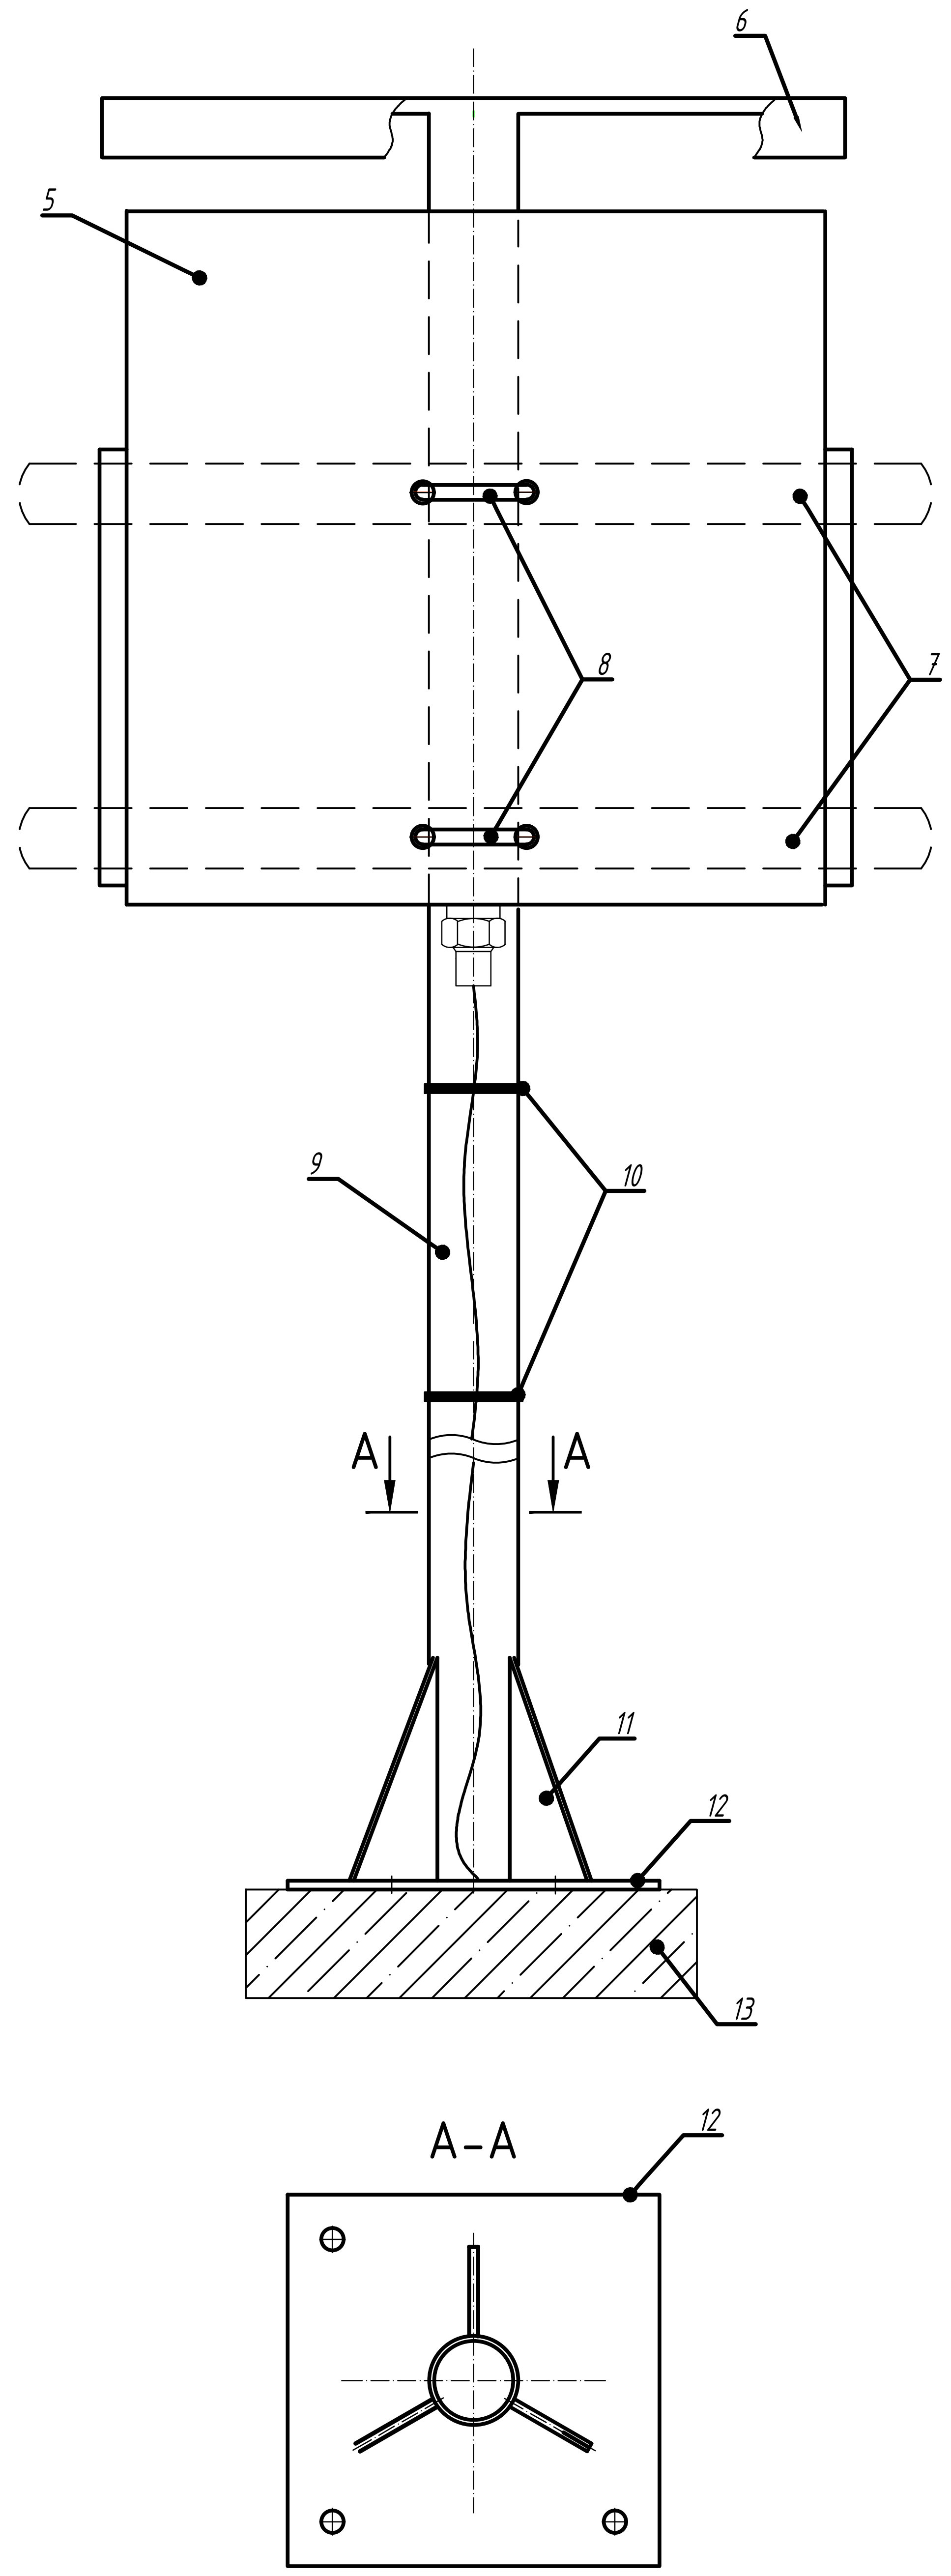

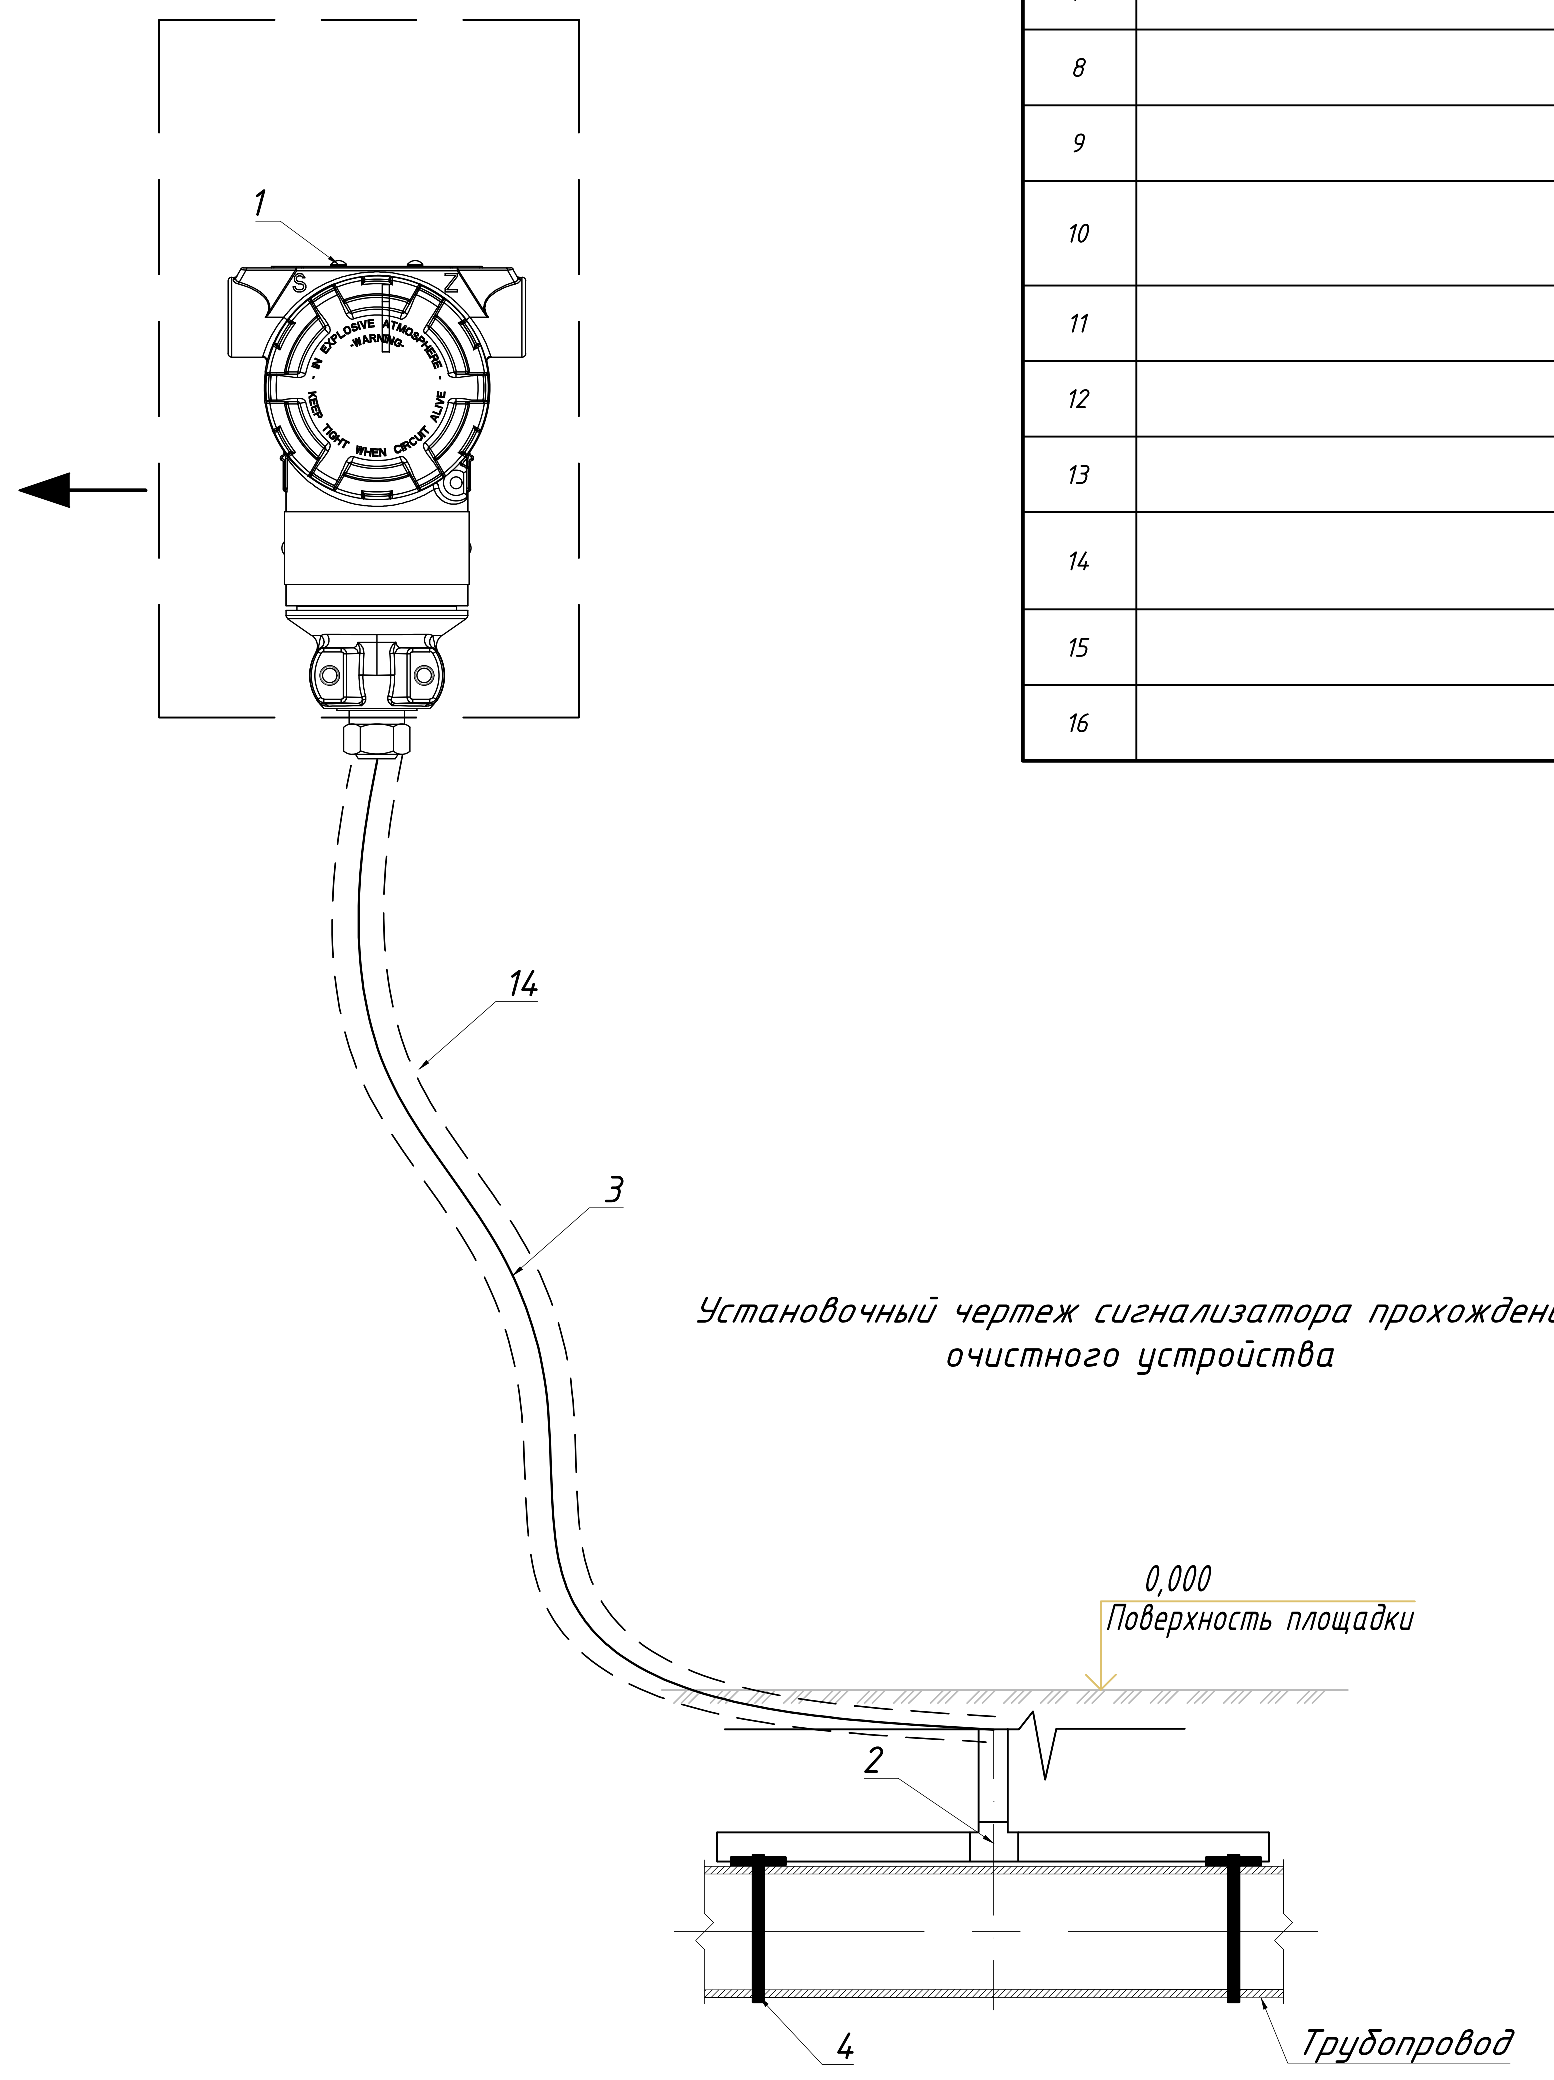

Установочный чертеж сигнализатора прохождения очистного устройства

1. По данному чертежу смонтировать на стойку позиции указанные в таблице.
2. Позиции приборов соответствуют схеме P&ID (указанной в таблице).
3. Количество монтажных изделий показано для одного сигнализатора прохождения очистного устройства.

Взам. инв. N

Подп. и дата

Инв. N подл.

Изм. Кол. Лист N°док. Подпись Дата

EWE0426-MGL1-SYS-054-DRW-800305-R1

Лист
5

Формат A2