
Монтажная схема подключения технологического оборудования

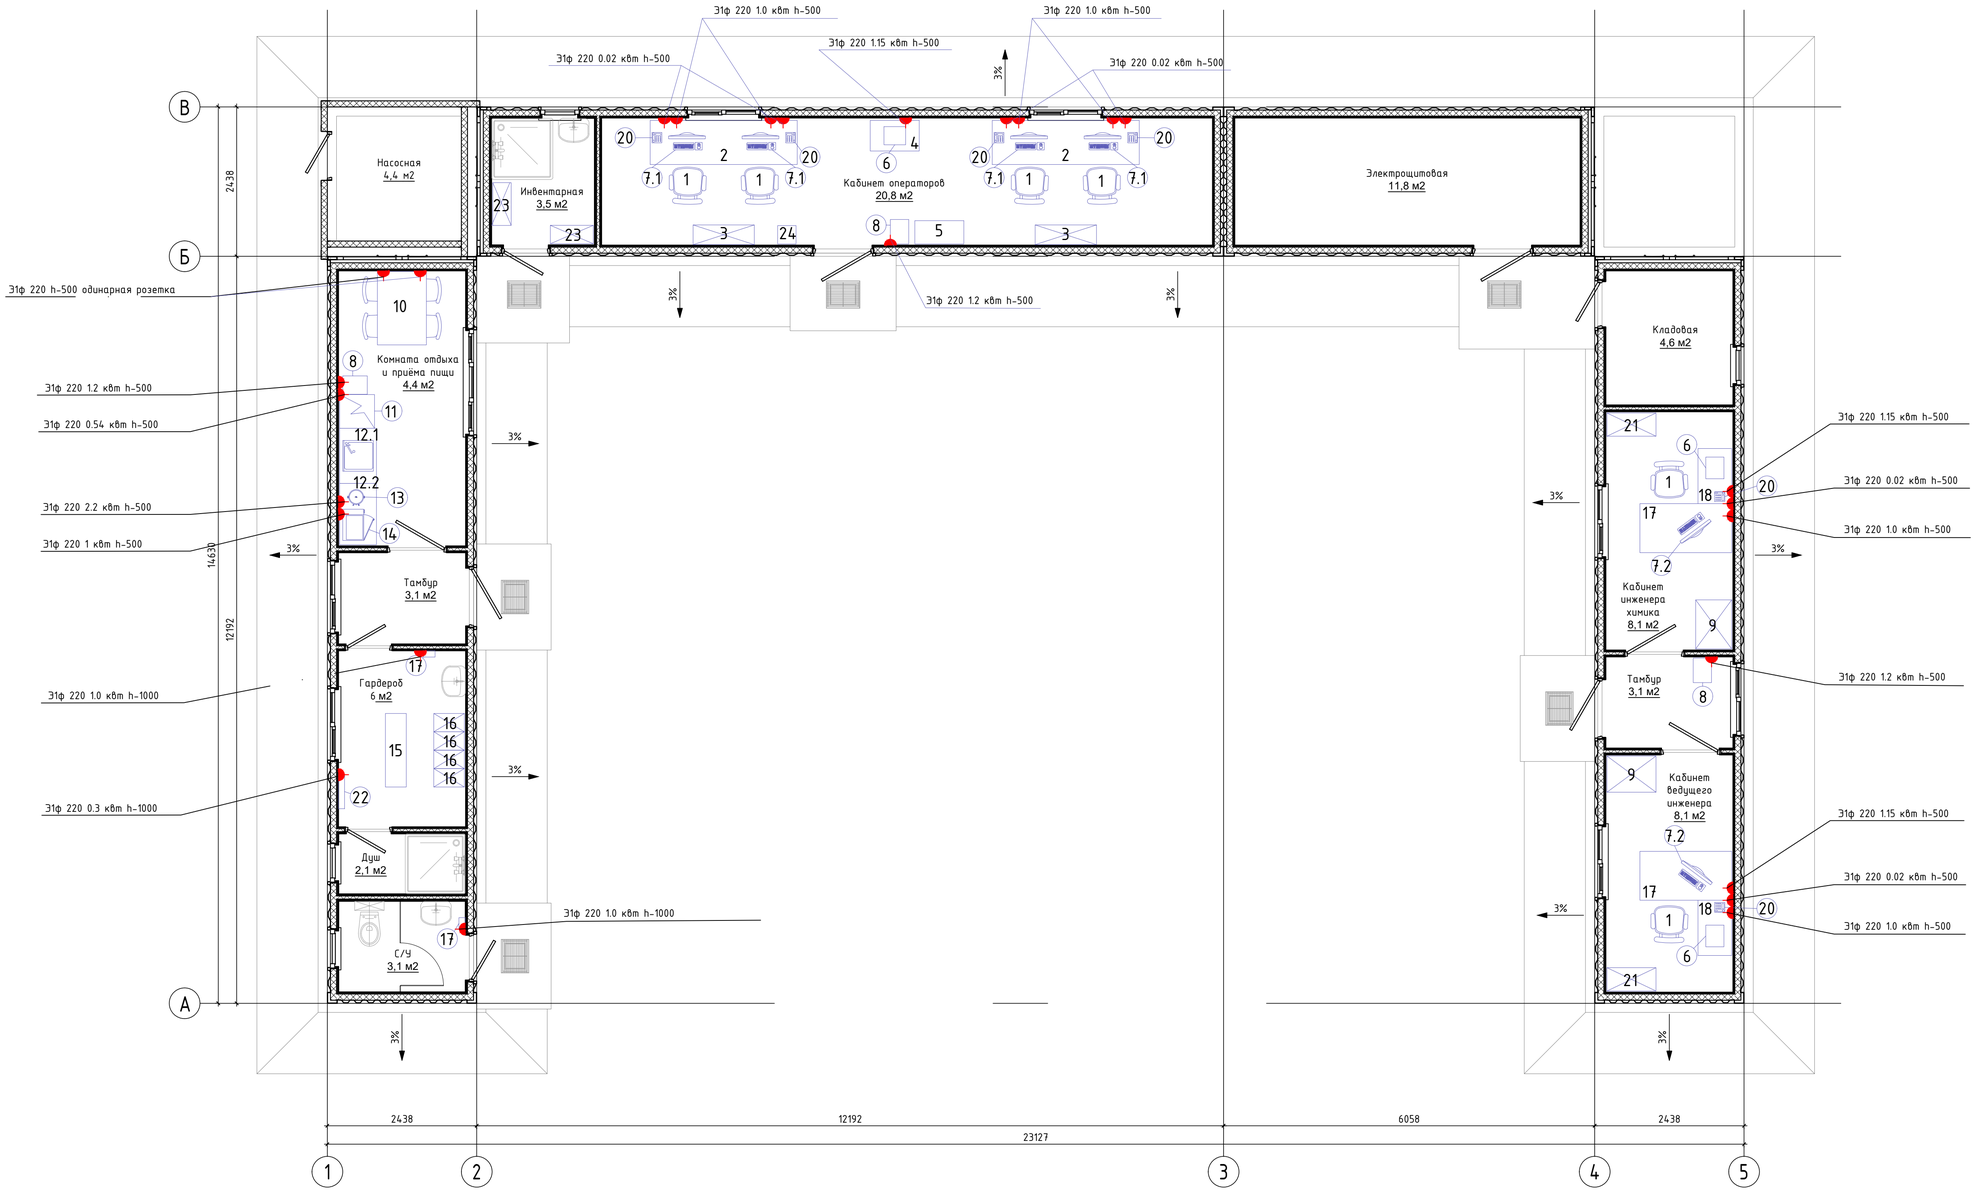

Примечание:
Номера позиций оборудования соответствуют номерам позиций данным в спецификации оборудования.

- Электророзетка 220 V настенная
- (17) - Нумерация позиций для электрооборудования
- 9 - Нумерация позиций для мебели и инвентаря

Ред.	Дата	Назначение ревизии	Проверил	Утвердил
A1	12.08.2026	Утверждено для строительства		
R1	07.08.2026	Выпущено для рассмотрения		

ЗАКАЗЧИК: UTG INTERNATIONAL
ГЕНЕРАЛЬНЫЙ ПОДРЯДЧИК: UET
ПОДРЯДЧИК: PBG
ГЕНЕРАЛЬНЫЙ ПРОЕКТИРОВЩИК: EAST WEST ENGINEERING

EWE0426-MGL1-PRE-054-DRW-801603-A1

«СТРОИТЕЛЬСТВО НОВЫХ НИТОК (УЧАСТКОВ) ГАЗОПРОВОДОВ «ГАЗЛИ – САРИМОЙ» И «АКЧАЛОК – ГАЗЛИ – НУКУС» ОБЩЕЙ ПРОТЯЖЕННОСТЬЮ НЕ МЕНЕЕ 275 КМ».

Изм.	Кол. уч.	Лист.	№док.	Подп.	Дата
ГИП		Схабицкий А.			08.2026
Нач.отд.		Юлдашев Х.			08.2026
Исполн.		Цой Р.			08.2026
Н. контр.		Схабицкий А.			08.2026

ГАЗОПРОВОД «ГАЗЛИ-САРИМОЙ» (54 КМ)

Стадия	Лист	Листов
РД	1	1

Монтажная схема подключения технологического оборудования

ООО "EAST-WEST Engineering" г. Ташкент 2026г.

Взам. инв. №
Подпись и дата
Инв.№ подл.

Формат А1