План расположения технологического оборудования

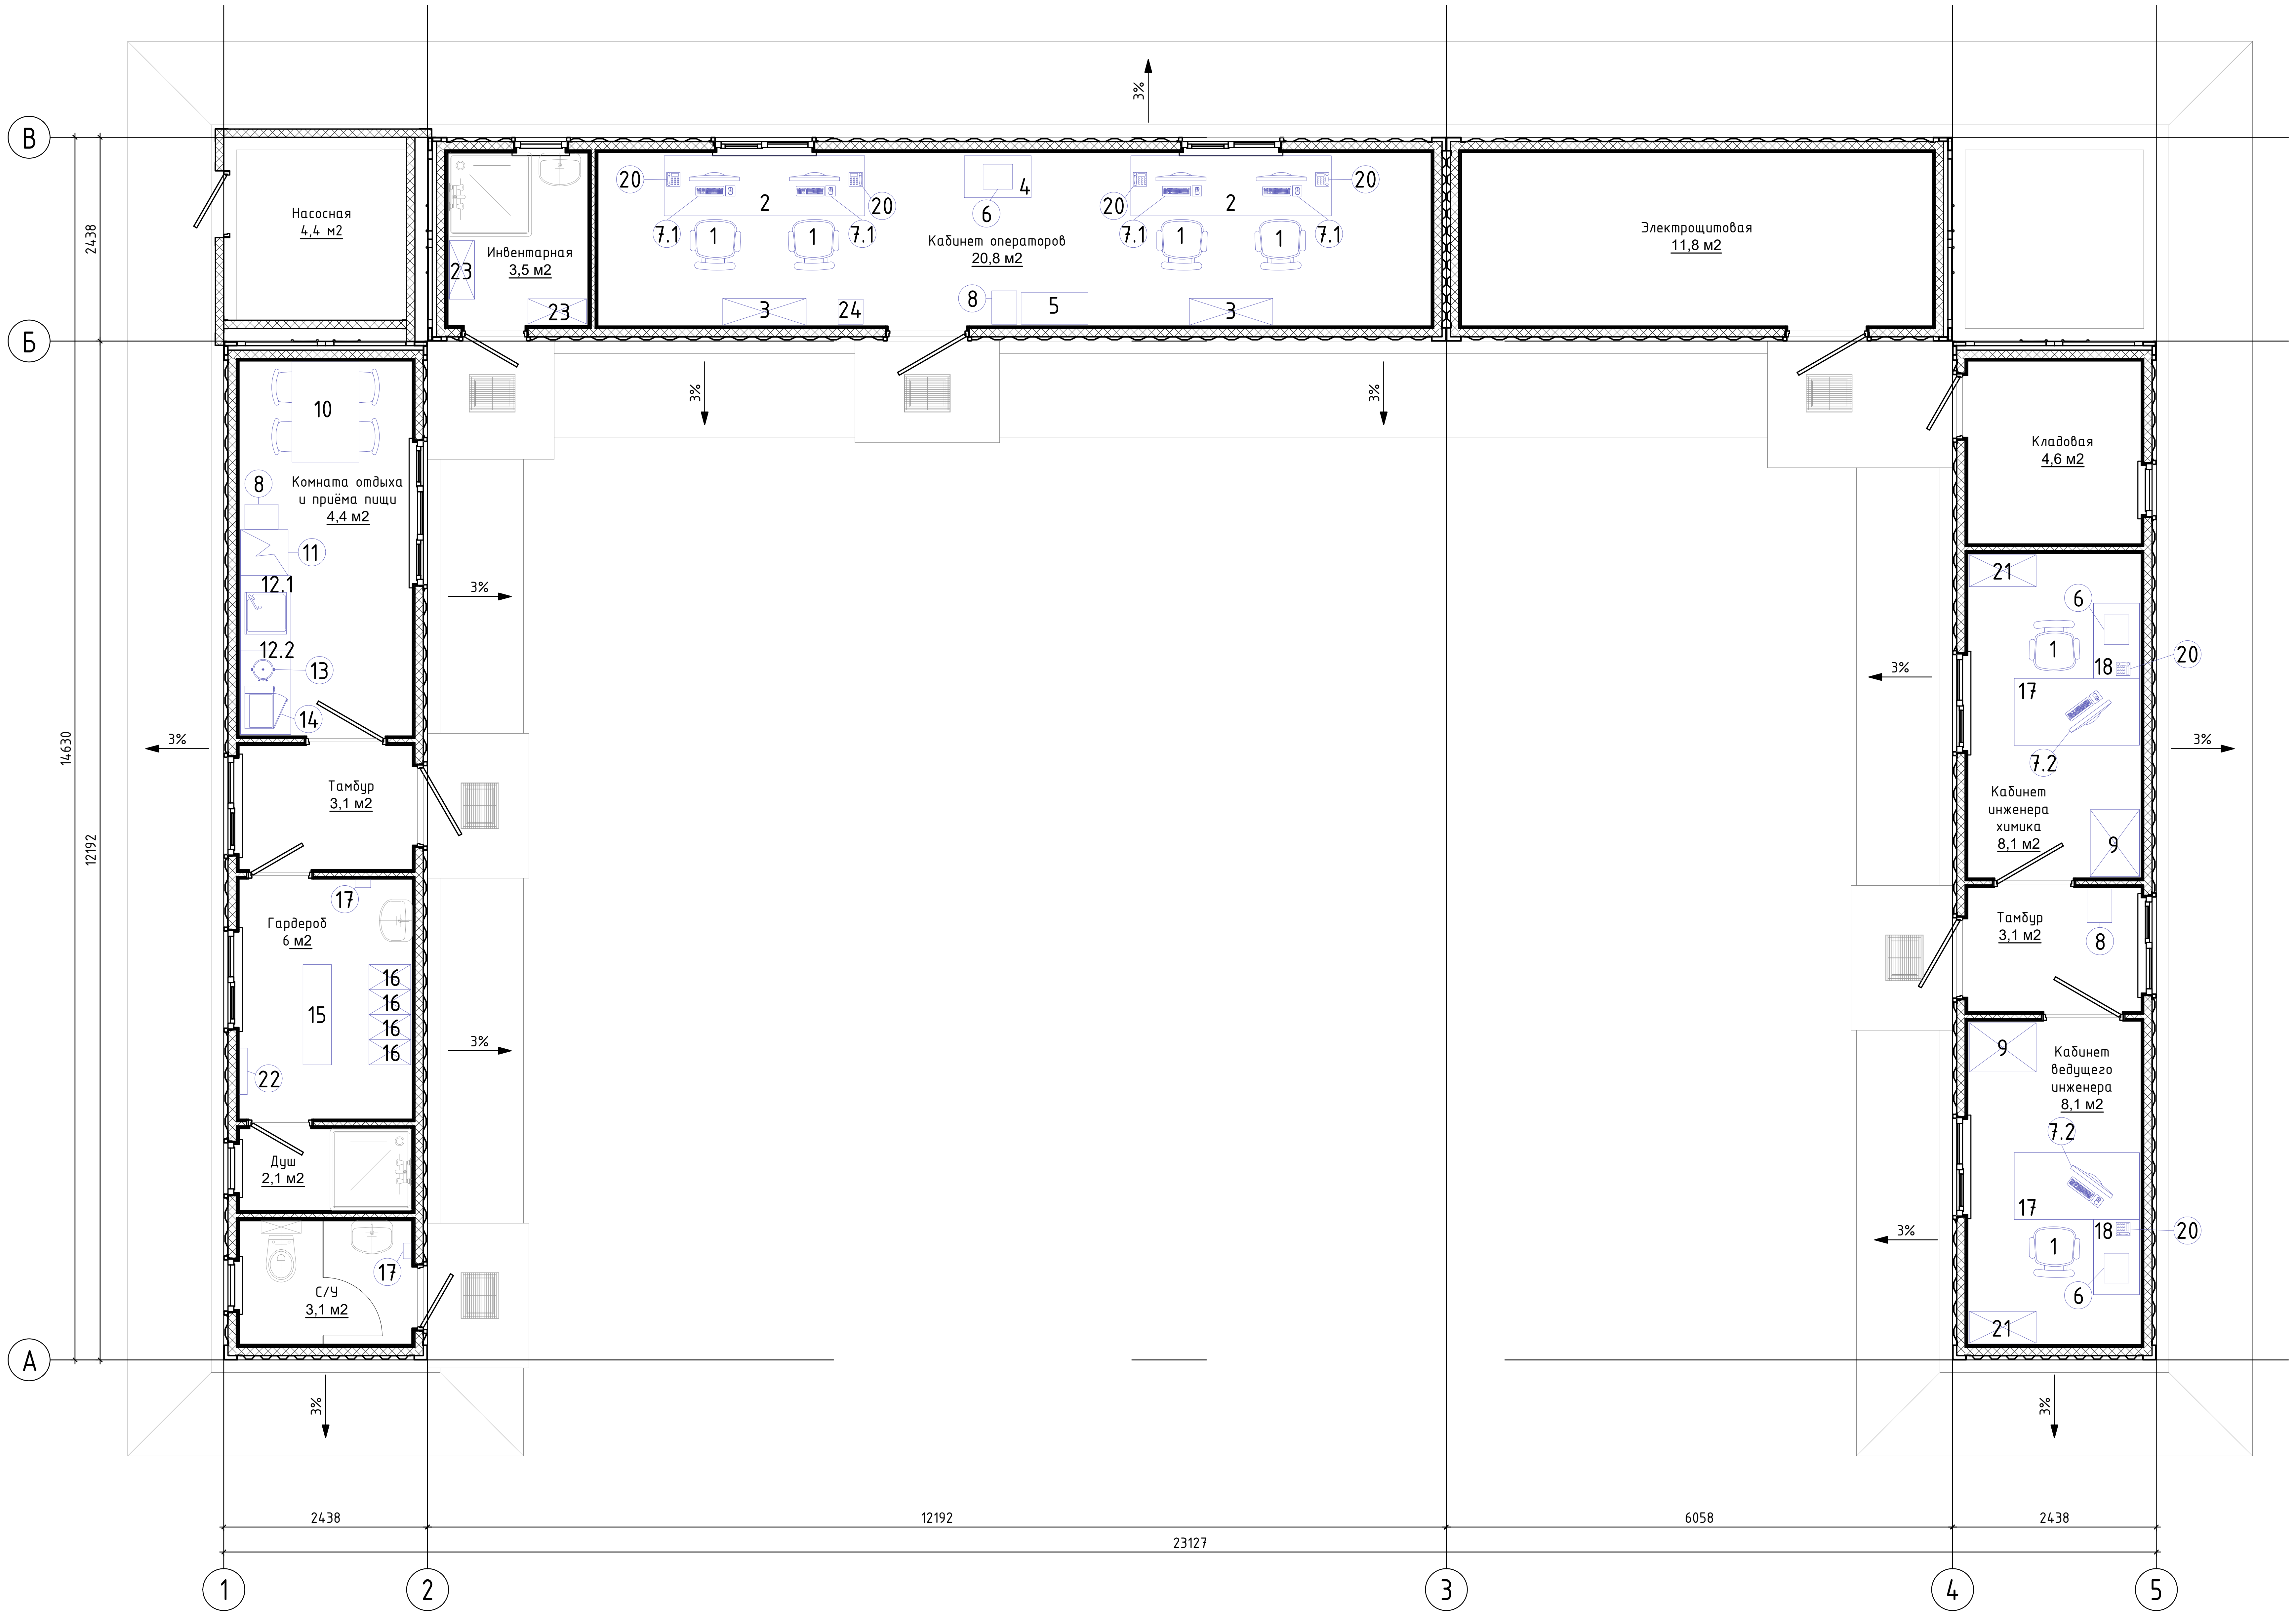

Насосная
4,4 м2
Инвентарная
3,5 м2
Кабинет операторов
20,8 м2
Электрощитовая
11,8 м2
Комната отдыха
и приёма пищи
4,4 м2
Тамбур
3,1 м2
Гардероб
6 м2
Душ
2,1 м2
С/У
3,1 м2
Кладовая
4,6 м2
Кабинет
инженера
химика
8,1 м2
Тамбур
3,1 м2
Кабинет
ведущего
инженера
8,1 м2
1
2
3
4
5
6
7.1
7.2
8
9
10
11
12.1
12.2
13
14
15
16
17
18
20
21
22
23
24
3%
В
Б
А
1
2
3
4
5
2438
12192
14630
2438
12192
6058
2438
23127

Примечание:
Номера позиций оборудования соответствуют номерам позиций данным в спецификации оборудования.

⑰ – Нумерация позиций для электрооборудования

9 – Нумерация позиций для мебели и инвентаря

A1	12.08.2026	Утверждено для строительства		
R1	07.08.2026	Выпущено для рассмотрения		
Рев.	Дата	Назначение ревизии	Проверил	Утвердил

ЗАКАЗЧИК: UTG UZTRANSGAZ
ГЕНЕРАЛЬНЫЙ ПОДРЯДЧИК: UET UZBEKENERGOTAMIR
ПОДРЯДЧИК: PBG Pro Build Generation
ГЕНЕРАЛЬНЫЙ ПРОЕКТИРОВЩИК: EAST WEST ENGINEERING

EWE0426-MGL1-PRE-054-PLA-801602-A1

«СТРОИТЕЛЬСТВО НОВЫХ НИТОК (УЧАСТКОВ) ГАЗОПРОВОДОВ «ГАЗЛИ – САРИМОЙ» И «АКЧАЛОК – ГАЗЛИ – НУКУС» ОБЩЕЙ ПРОТЯЖЕННОСТЬЮ НЕ МЕНЕЕ 275 КМ».

Изм.	Кол. уч.	Лист.	№док.	Подп.	Дата
ГИП		Схабицкий А.			08.2026
Нач.отд.		Юлдашев Х.			08.2026
Исполн.		Цой Р.			08.2026
Н. контр.		Схабицкий А.			08.2026

ГАЗОПРОВОД «ГАЗЛИ-САРИМОЙ» (54 КМ)

Стадия	Лист	Листов
РД	1	1

План расположения технологического оборудования

ООО "EAST-WEST Engineering"
г. Ташкент 2026г.

Формат А1

Взам. инв. №
Подпись и дата
Инв.№ подл.