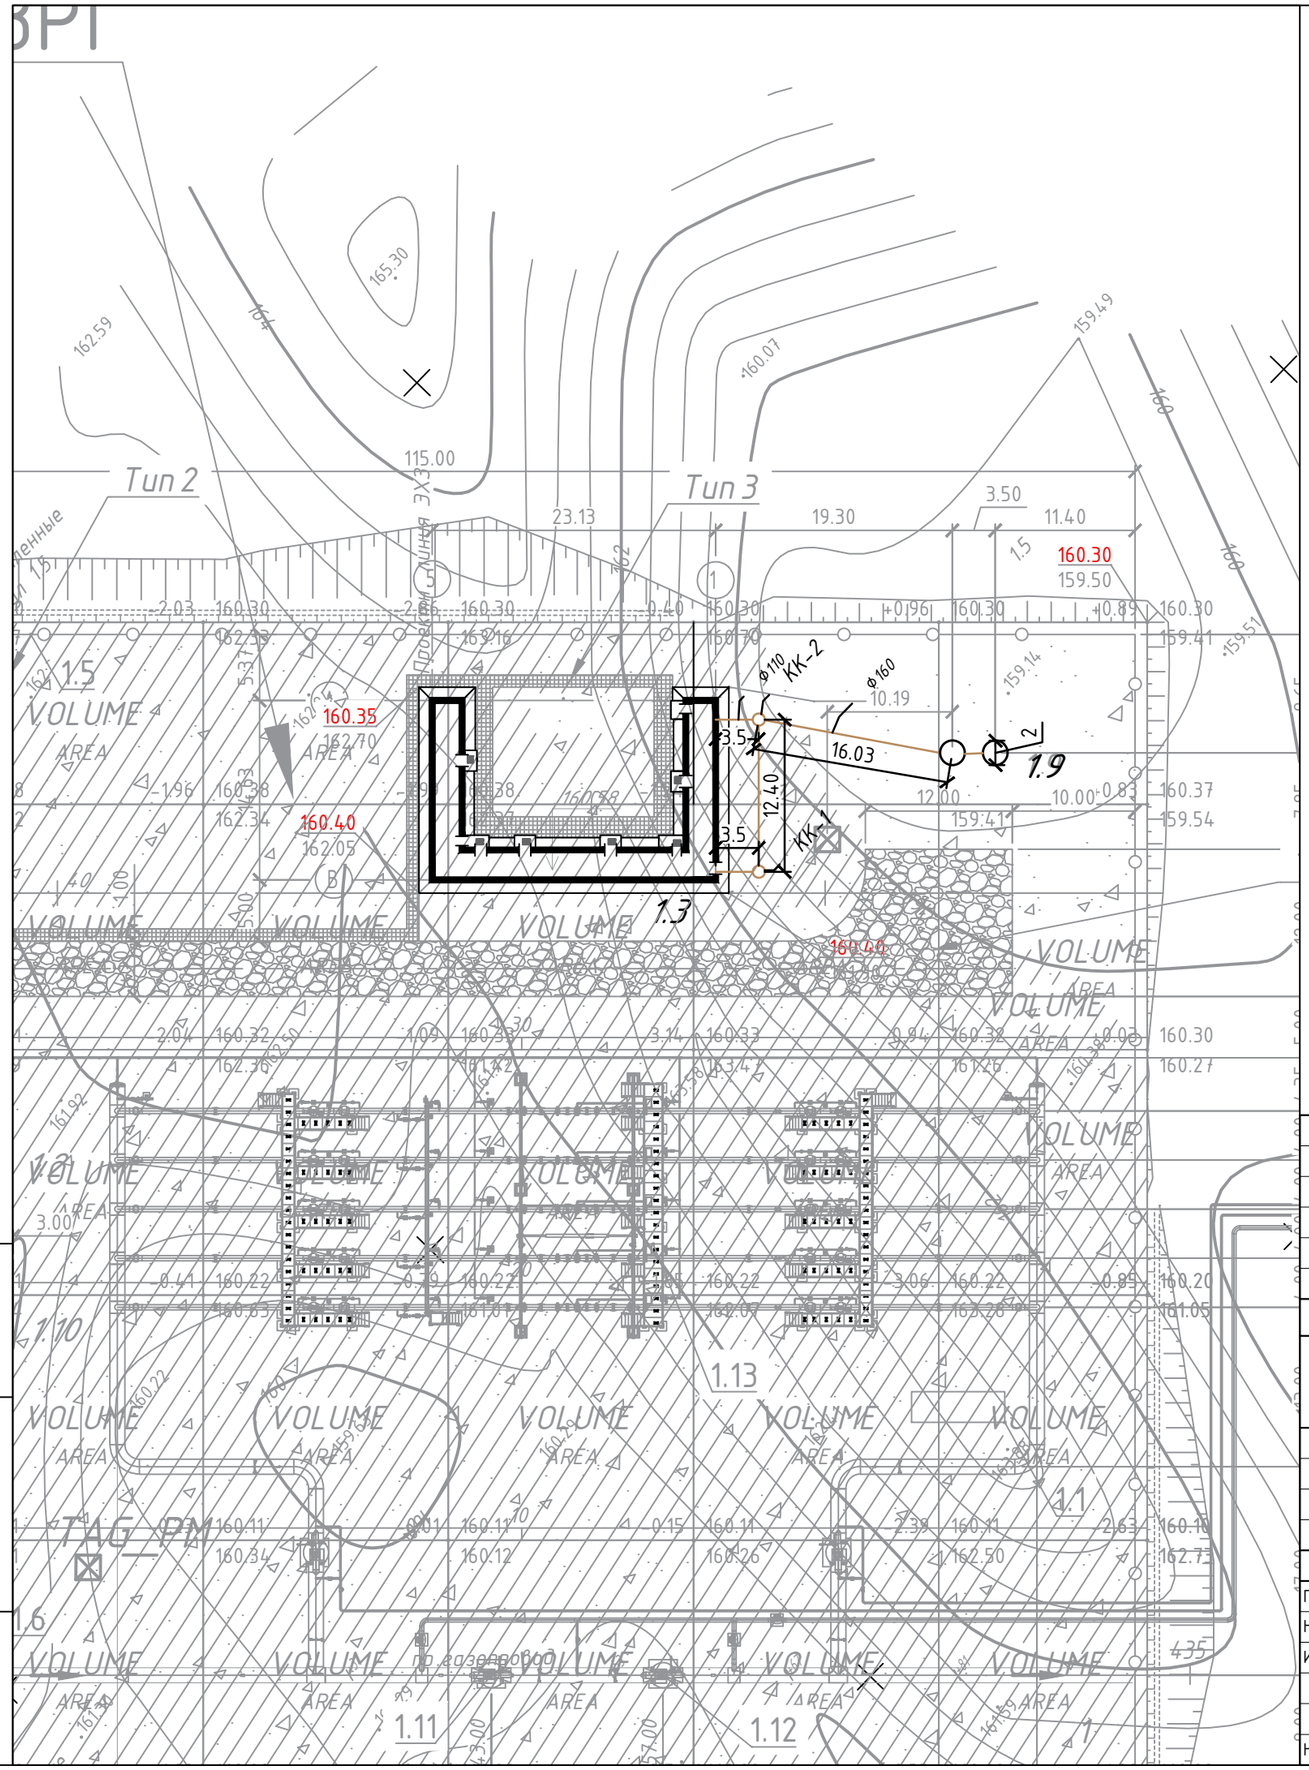


Примечание:

1. Все бетонные и железобетонные конструкции, предусмотренные проектом, выполнить из бетона на сульфатостойком цементе.

Условные обозначения :

———	Канализационный трубопровод
○ КК	Канализационный колодец
1.3	Здание операторной
1.9	Септик
	Рабочий объем – 11.3 м^3

Рев.	Дата	Назначение ревизии	Проверил	Утвердил
A1	07.10.2026	Выпущен для строительства	Вахобов Д.	Кирпичников С.
R1	19.08.2026	Выпущен для рассмотрения	Юткина И.	Схабицкий А.

ЗАКАЗЧИК: UTG | ГЕНЕРАЛЬНЫЙ ПОДРЯДЧИК: UET UZBEKISTAN ENERGY | ПОДРЯДЧИК: PBC Pro Build Generation | ГЕНЕРАЛЬНЫЙ ПРОЕКТИРОВЩИК: EAST WEST ENGINEERING

Изм.	Кол. уч.	Лист.	№док.	Подп.	Дата
ГИП		Кирпичников С.			07.10.26
Нач.отд.		Вахобов Д.			07.10.26
Исполн.		Абдурахмонов Ш			07.10.26
Н. контр.		Кирпичников С.			07.10.26

EWE0426-MGL1-WSS-054-PLA-801102-A1

«СТРОИТЕЛЬСТВО НОВЫХ НИТОК (УЧАСТКОВ) ГАЗОПРОВОДОВ «ГАЗЛИ – САРИМОЙ» И «АКЧАЛОК – ГАЗЛИ – НУКУС» ОБЩЕЙ ПРОТЯЖЕННОСТЬЮ НЕ МЕНЕЕ 275 КМ».

ГАЗОПРОВОД «ГАЗЛИ-САРИМОЙ» (54 КМ)

Стадия	Лист	Листов
РД	1	1

План с сетью К 1. М 1:500

ООО "EAST-WEST Engineering" г. Ташкент 2026г.

Взам. инв. №

Подпись и дата

Инв.№ подл.

Формат А3