ПРОДОЛЬНЫЙ ПРОФИЛЬ БЫТОВОЙ КАНАЛИЗАЦИИ

М 1:500 - по горизонтали
М 1:100 - по вертикали
М 1:100 - по вертикали
грунты

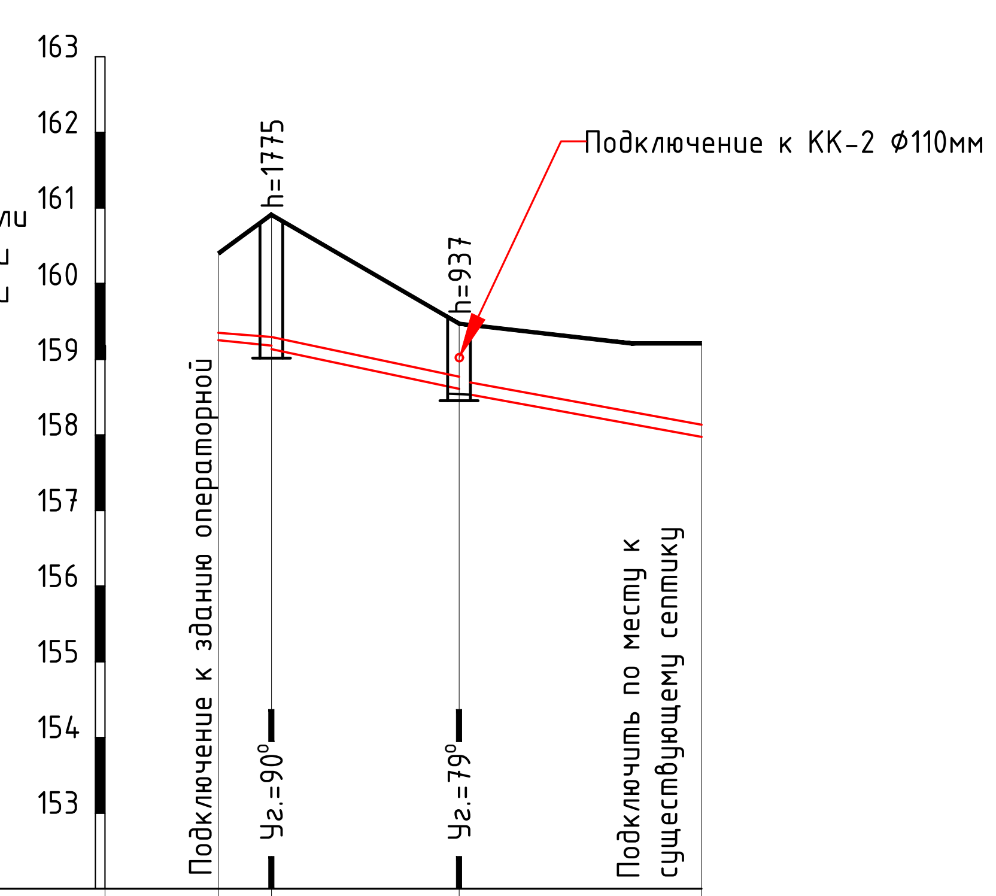
163
162
161
160
159
158
157
156
155
154
153
h=1775
h=937
Подключение к КК-2 Ø110мм
Подключение к зданию операторной
Уг.=90°
Уг.=79°
Подключить по месту к существующему септику

ОТМЕТКА НИЗА ТРУБЫ	159.25	159.14	158.61	158.53	157.97
ПРОЕКТНАЯ ОТМЕТКА ЗЕМЛИ	160.40	160.91	159.47		159.21
СУЩЕСТВУЮЩАЯ ОТМЕТКА ЗЕМЛИ	160.40	160.91	159.47		159.21
ДИАМЕТР ТРУБЫ И МАТЕРИАЛ	ПВХ Ø110мм		ПЭ Ø160мм		
ОСНОВАНИЕ	Песчаная подготовка				
УКЛОН / РАССТОЯНИЕ		0.02 / 3.5	0.043 / 12.4		0.037 / 14.8
РАССТОЯНИЕ		3.5	12.4		14.8
№ КОЛОДЦЕВ, ТОЧЕК УГЛОВ ПОВ.		КК-1	КК-2		
ИНЖЕНЕРНО-ГЕОЛОГИЧЕСКАЯ ХАРАКТЕРИСТИКА					

М 1:500 - по горизонтали
М 1:100 - по вертикали
М 1:100 - по вертикали
грунты

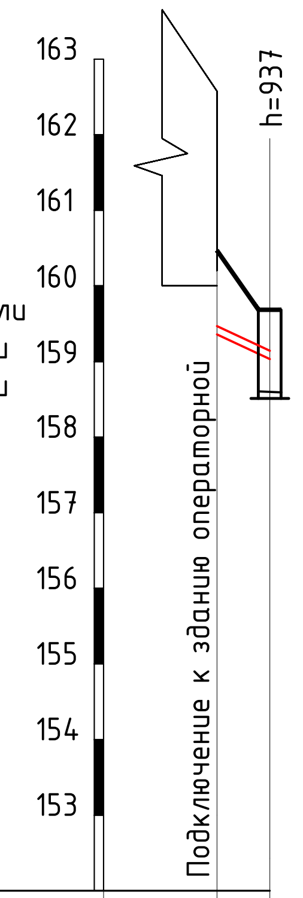
163
162
161
160
159
158
157
156
155
154
153
h=937
Подключение к зданию операторной

ОТМЕТКА НИЗА ТРУБЫ	159.36	159.03
ПРОЕКТНАЯ ОТМЕТКА ЗЕМЛИ	160.40	159.47
СУЩЕСТВУЮЩАЯ ОТМЕТКА ЗЕМЛИ	160.4	159.47
ДИАМЕТР ТРУБЫ И МАТЕРИАЛ		ПВХ Ø110мм
ОСНОВАНИЕ	Песчаная подготовка	
УКЛОН		0.09 / 3.5
РАССТОЯНИЕ		3.5
№ КОЛОДЦЕВ, ТОЧЕК УГЛОВ ПОВ.		КК-2
ИНЖЕНЕРНО-ГЕОЛОГИЧЕСКАЯ ХАРАКТЕРИСТИКА		

Схема круглого канализационного колодца

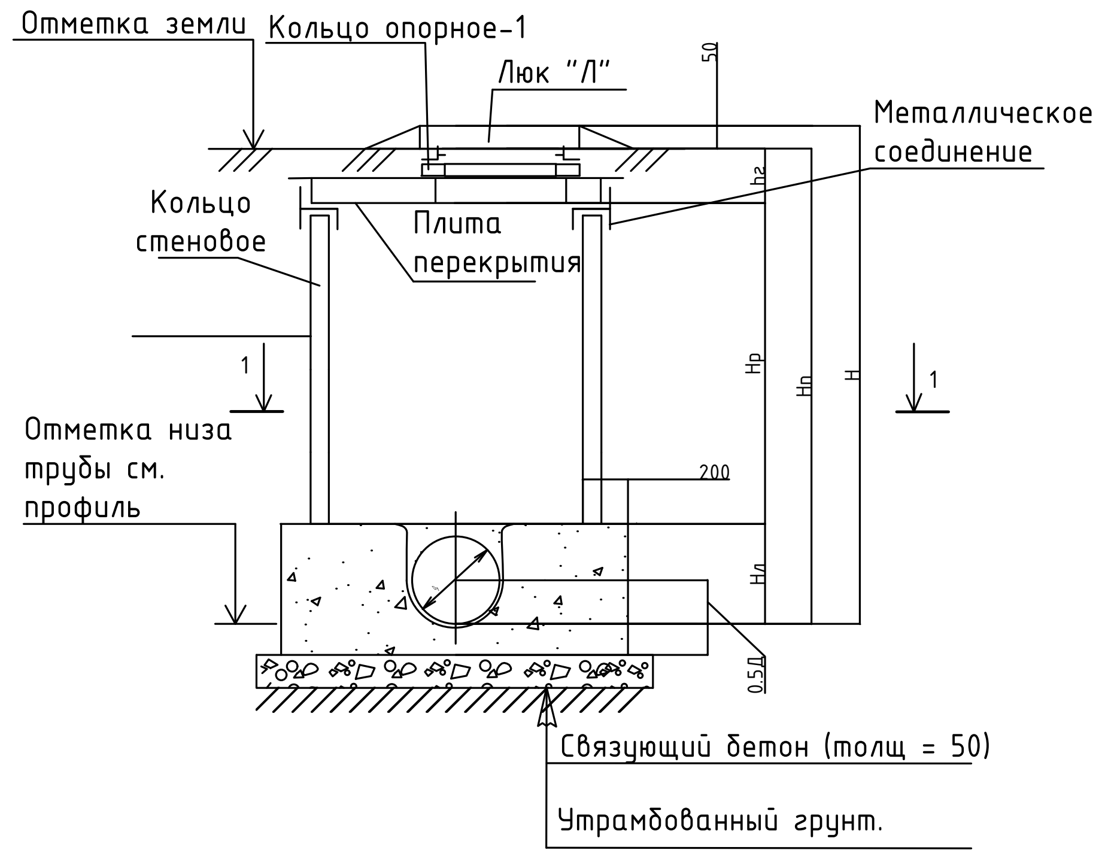
Отметка земли
Кольцо опорное-1
Люк "Л"
50
Металлическое соединение
Кольцо стеновое
Плита перекрытия
hг
Hр
Hп
H
1
1
Отметка низа трубы см. профиль
200
Hл
0.5Д
Связующий бетон (толщ = 50)
Утрамбованный грунт.

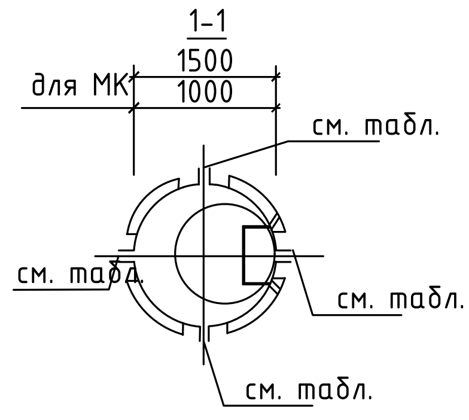
1-1
1500
для МК
1000
см. табл.
см. табл.
см. табл.
см. табл.

Схема двухкамерного септика с фильтрацией сточных вод в грунт

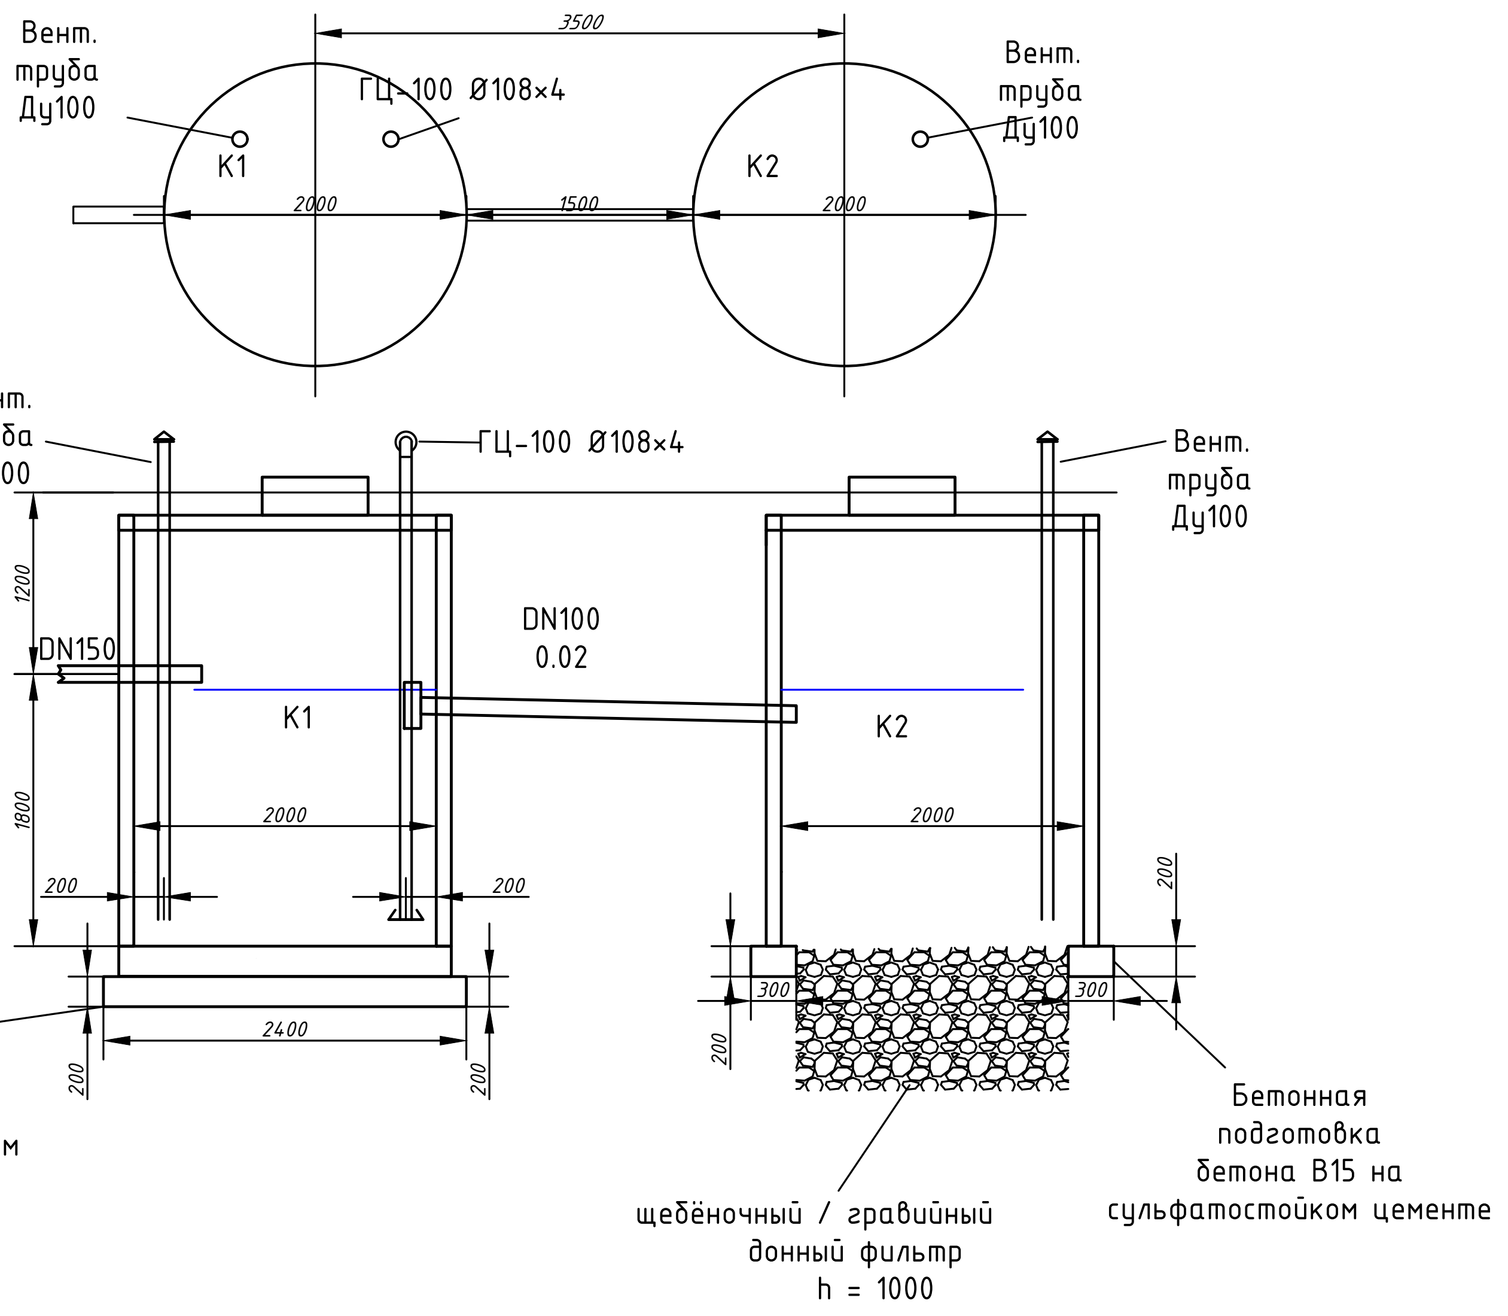
Вент. труба Ду100
ГЦ-100 Ø108×4
3500
К1
К2
Вент. труба Ду100
2000
1500
2000
Вент. труба Ду100
ГЦ-100 Ø108×4
Вент. труба Ду100
1200
DN150
DN100
0.02
К1
К2
1800
2000
2000
200
200
200
300
300
2400
200
200
200
Бетонная подготовка бетона В15 на сульфатостойком цементе
щебёночный / гравийный донный фильтр h = 1000
Бетонная подготовка бетона В15 на сульфатостойком цементе

КК-1

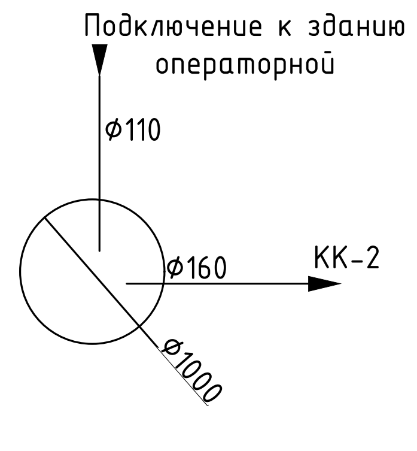
Подключение к зданию операторной
Ø110
Ø160
КК-2
Ø1000

КК-2

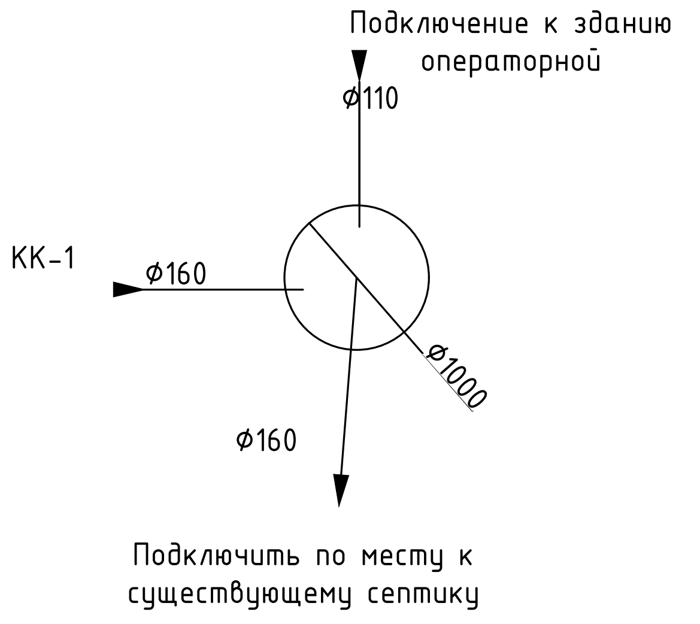
Подключение к зданию операторной
Ø110
КК-1
Ø160
Ø1000
Ø160
Подключить по месту к существующему септику

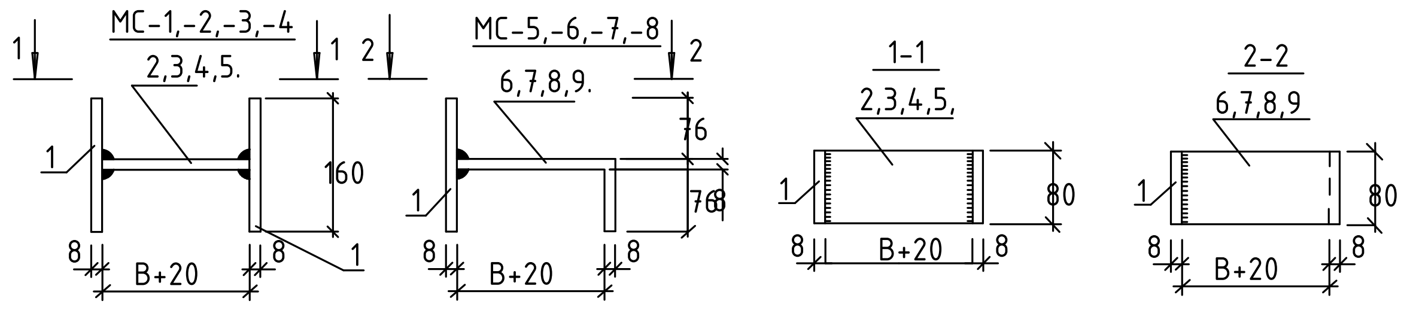
1
1
МС-1,-2,-3,-4
2,3,4,5.
1
160
1
8
8
В+20
2
2
МС-5,-6,-7,-8
6,7,8,9.
76
76
8
1
8
8
В+20
1-1
2,3,4,5,
1
80
8
8
В+20
2-2
6,7,8,9
1
80
8
8
В+20

Величина "В" принимается равной толщине сборного элемента и равна:
для МС-1,МС-5 - 70мм (диаметр сб.ж.б. колец 700мм)
для МС-2,МС-6 - 80мм (диаметр сб.ж.б. колец 1000мм)
для МС-3,МС-7 - 90мм (диаметр сб.ж.б. колец 1500мм)
для МС-4,МС-8 - 100мм (диаметр сб.ж.б. колец 2000мм)

Укладка труб в траншею с откосами

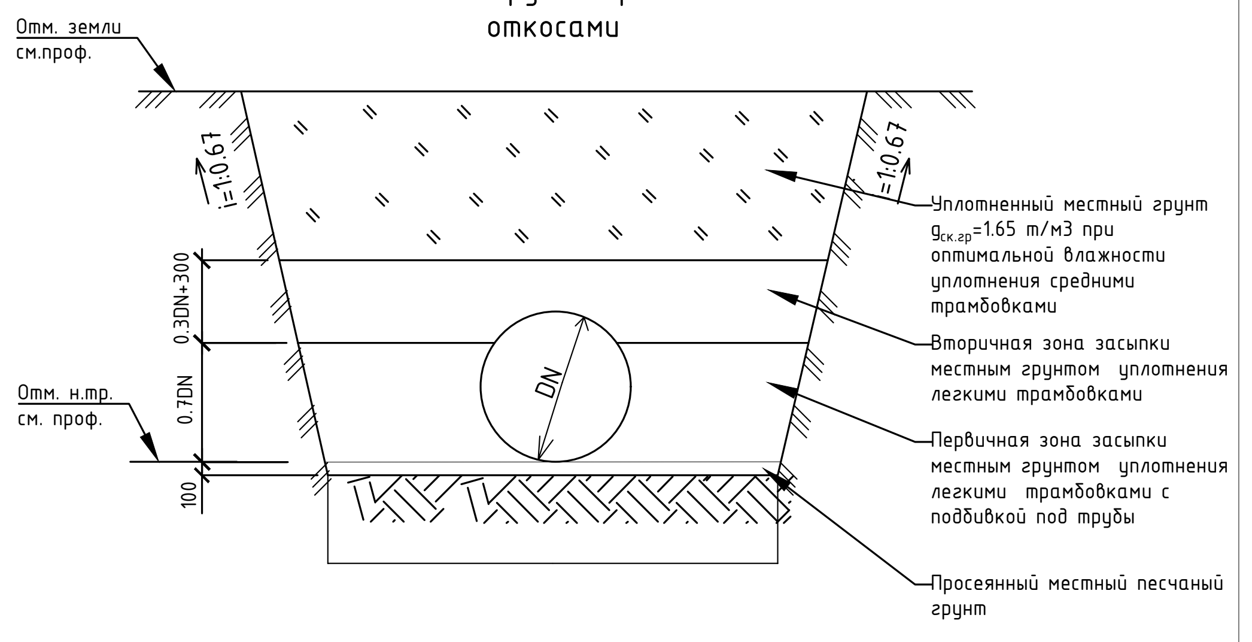
Отм. земли см.проф.
i=1:0.67
i=1:0.67
0.3DN+300
0.7DN
100
Отм. н.тр. см. проф.
DN
Уплотненный местный грунт $g_{ск.гр}$=1.65 т/м3 при оптимальной влажности уплотнения средними трамбовками
Вторичная зона засыпки местным грунтом уплотнения легкими трамбовками
Первичная зона засыпки местным грунтом уплотнения легкими трамбовками с подбивкой под трубы
Просеянный местный песчаный грунт

ТАБЛИЦА ОСНОВНЫХ ПОКАЗАТЕЛЕЙ КРУГЛЫХ КАНАЛИЗАЦИОННЫХ И ВОДОПРОВОДНЫХ КОЛОДЦЕВ

NN колодцев по проекту	Марка колодца	Отметка сущ.земли		Отметка низа трубы	Расстояние от низа трубы до дна колодца	Глубина лотка	Диаметр колодца	Высота Hр рабочей части,мм	Высота hг горловины, мм	Полная глубина колодца H,мм	Глубина колодца по профилю Hп,мм	Диаметр трубопровода мм				Строительные конструкции																								Люк "Л" по ГОСТ 3634-99, шт	Стремянка			Объем ж/б конструкции, м3
		Натуральная отметка земли		Dy / dy								I	II	III	IV	ПН10	ПН15	1ПП15-1	1ПП10-1	КС15-9	КС10-3	КС10-6	КС10-9	КО6	ПН20	КС20-6	КС20-9	1ПП20-1	КС7-9	Металлические соединительные элементы , шт					Сальники набивные.Серия 5.900-2, шт						Марка	Количество	Вес , кг.	
																														МС-2	МС-4	МС-5	МС-6	МС-8	dу=50	dу=80	dу=100	dу=150	dу=200					
КК1		160.91	160.91	159.14		200	1000	1500	215	1775	1775	–	110	160	–	1	–	–	1	–	–	1	1	1	–	–	–	–	–	6	–	–	12	–	–	–	1	1	–	1	–	–	–	1.34
КК2		159.47	159.47	158.53		200	1000	600	350	937	937	160	–	110	160	1	–	–	1	–	–	1	–	1	–	–	–	–	–	–	–	–	12	–	–	–	1	2	–	1	–	–	–	1.34
Септик К1							2000	2100	280	1800	3000	–	–	160	110	–	–	–	–	–	–	–	–	1	1	2	1	1	–	–	12	–	–	12	–	–	1	1	–	1	–	–	–	2.46
Септик К2							2000	2100	280	1800	3000	–	–	110	–	–	–	–	–	–	–	–	–	1	–	2	1	1	–	–	12	–	–	12	–	–	1	–	–	1	–	–	–	2.46

Крепление лестницы для канализационного колодца

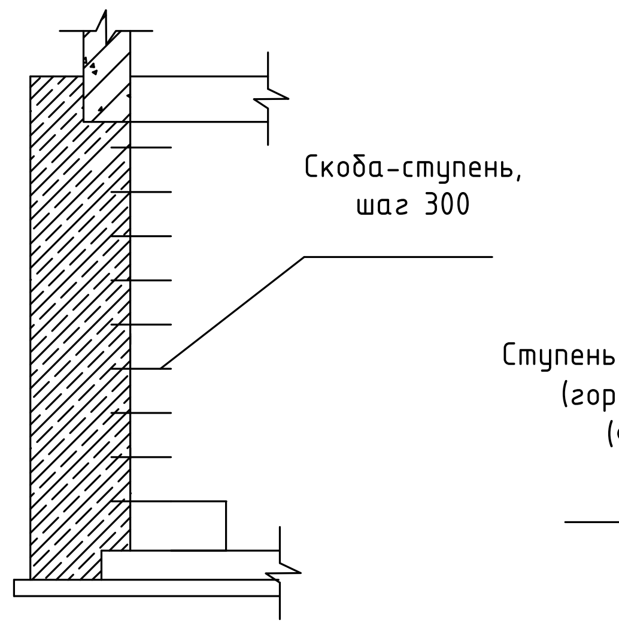
Скоба-ступень, шаг 300

Деталь скобы ступени верт. лестницы

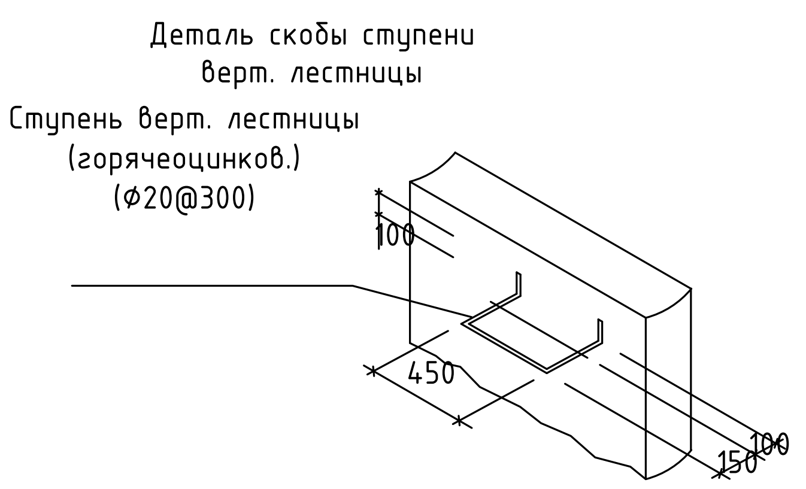
Ступень верт. лестницы (горячеоцинков.) (Ø20@300)
100
450
150
100

A1	07.10.2026	Выпущен для строительства	Вахобов Д.	Кирпичников С.
R1	19.08.2026	Выпущен для рассмотрения	Юткина И.	Схабицкий А.
Рев.	Дата	Назначение ревизии	Проверил	Утвердил

ЗАКАЗЧИК: UTG UZTRANSGAZ
ГЕНЕРАЛЬНЫЙ ПОДРЯДЧИК: UET UZBEKENERGOTAMIR
ПОДРЯДЧИК: PBG Pro Build Generation
ГЕНЕРАЛЬНЫЙ ПРОЕКТИРОВЩИК: EAST WEST ENGINEERING

EWE0426-MGL1-WSS-054-PRO-801103-A1

«СТРОИТЕЛЬСТВО НОВЫХ НИТОК (УЧАСТКОВ) ГАЗОПРОВОДОВ «ГАЗЛИ - САРИМОЙ» И «АКЧАЛОК - ГАЗЛИ - НУКУС» ОБЩЕЙ ПРОТЯЖЕННОСТЬЮ НЕ МЕНЕЕ 275 КМ».

Изм.	Кол. уч.	Лист.	№док.	Подп.	Дата
ГИП		Кирпичников С.			07.10.26
Нач.отд.		Вахобов Д.			07.10.26
Исполн.		Абдурахмонов Ш.			07.10.26
Н. контр.		Кирпичников С.			07.10.26

ГАЗОПРОВОД «ГАЗЛИ-САРИМОЙ» (54 КМ)

Стадия	Лист	Листов
РД	1	1

Продольный профиль сети К 1. Таблица круглых канализационных колодцев сети К 1

ООО "EAST-WEST Engineering"
г. Ташкент 2026г.

Формат А1

Взам. инв. №
Подпись и дата
Инв.№ подл.