
План и разрез систем ВК
(1:50)

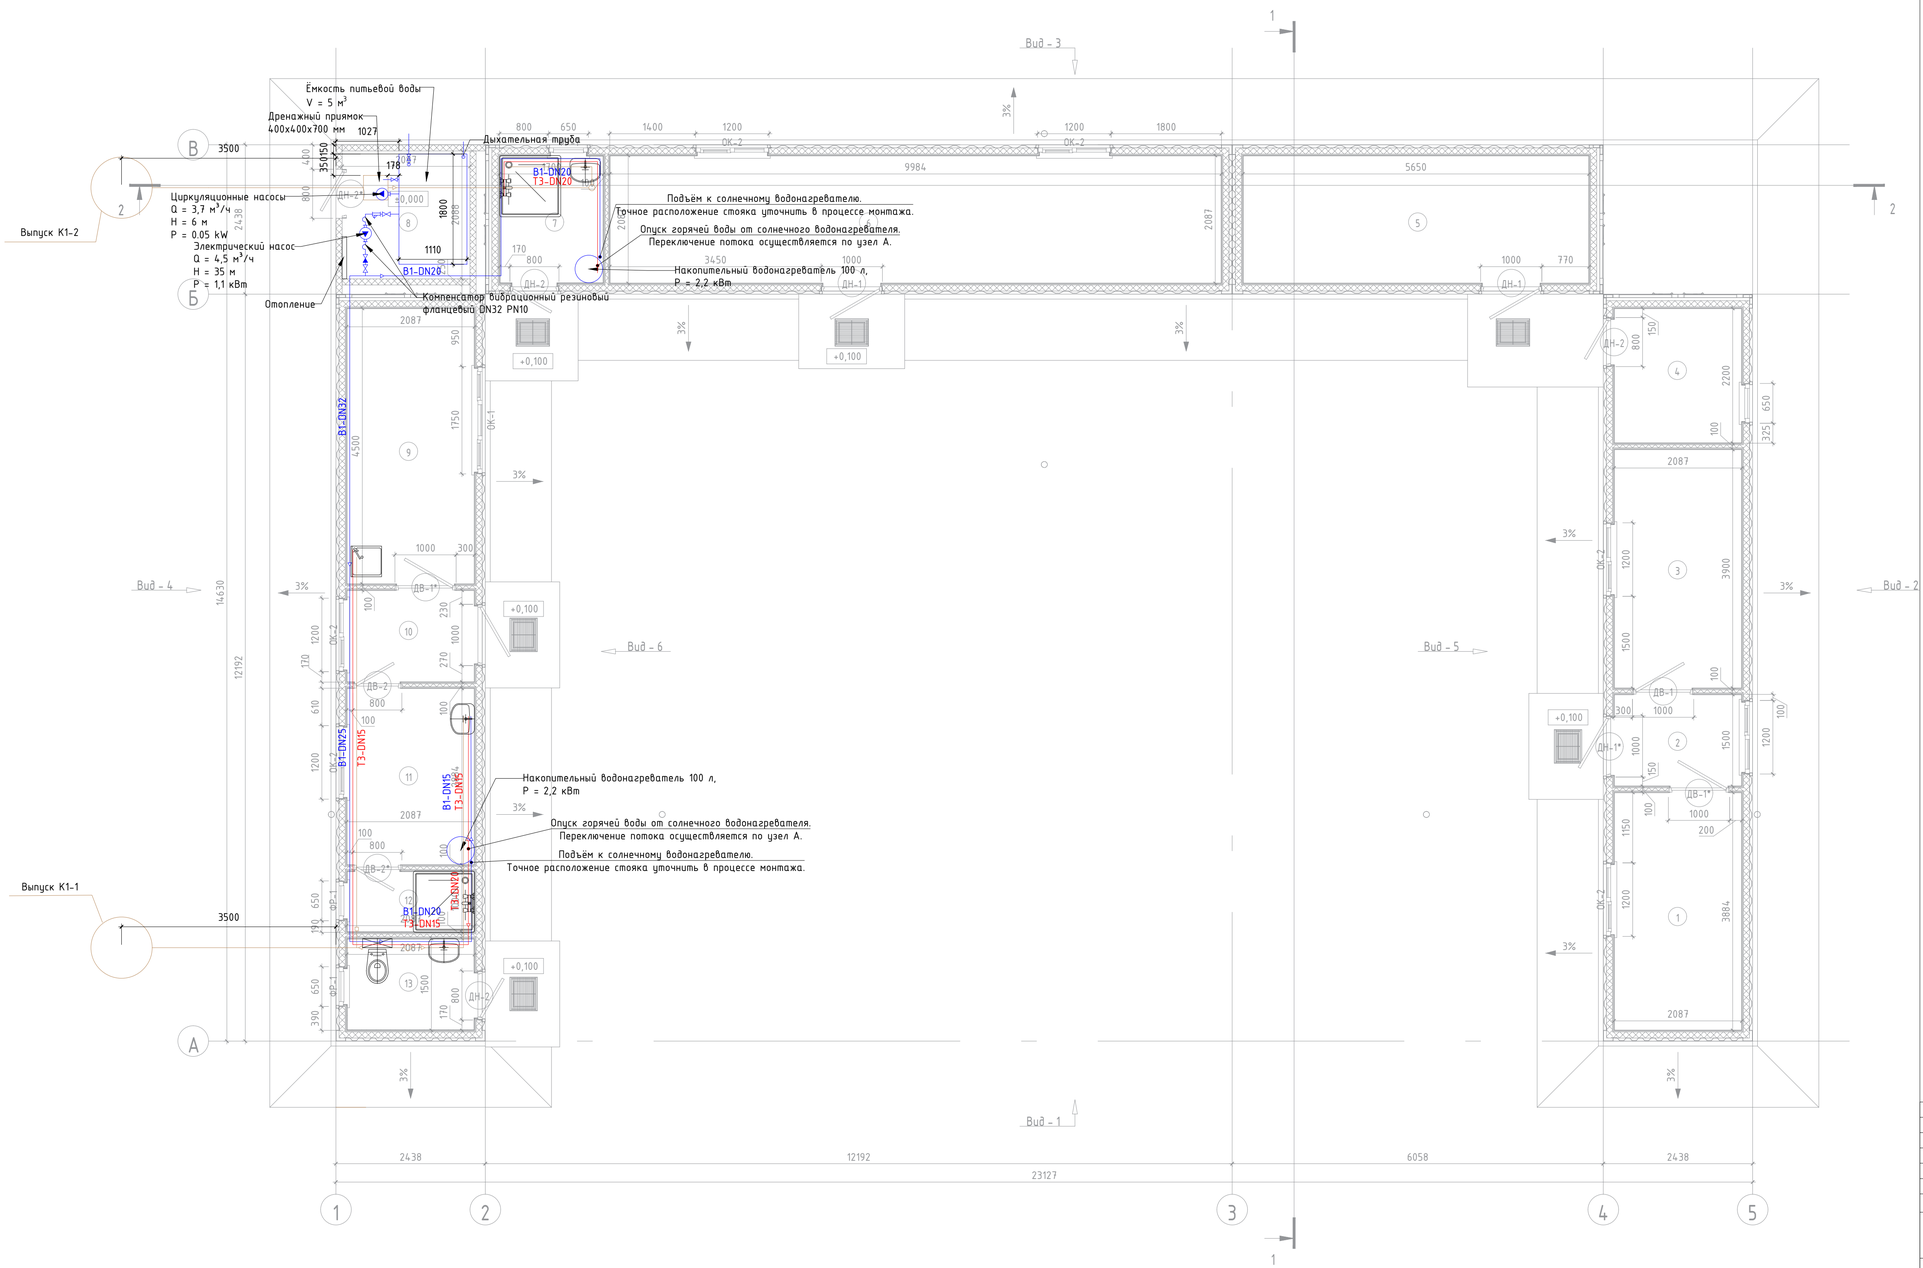


Примечание:

1. Все диаметры указаны внутренние условно проходные, согласно ГОСТ.
2. Все повороты 90° предусмотреть посредством двух полуотводов 45°
3. Все тройники косые – 45°
4. В настоящих чертежах отметка чистого пола +0.180 принята за ±0.000.

Условные обозначения :

	В1	Холодное водоснабжение (ХВС)
	К1	Хоз. бытовая канализация
	Т3	Горячее водоснабжение (ГВС)
	Ум	Умывальник
	Мк	Мойка
	Ун	Унитаз
	Пр	Прочистка
	Р	Ревизия
	Кр	Кран запорный шаровой

Узел А

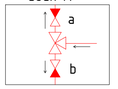

Узел автоматического переключения потока горячей воды трехходовым клапаном.

a – подача воды в накопительный водонагреватель (при T < +50 °C).
b – подача горячей воды к потребителям (при T ≥ +50 °C).

Рев.	Дата	Назначение ревизии	Проверил	Утвердил
А1	03.09.2026	Выпущен для строительства	Юткина И.	Скабицкий А.
R1	07.08.2026	Выпущен для рассмотрения	Юткина И.	Скабицкий А.

ЗАКАЗЧИК: ГенеральныйПодрядчик: ПОДРЯДЧИК: ГЕНЕРАЛЬНЫЙ ПРОЕКТИРОВЩИК: EAST WEST ENGINEERING

EWE0426-MGL1-WSS-054-PLA-801202-A1

«СТРОИТЕЛЬСТВО НОВЫХ НИТОК (УЧАСТКОВ) ГАЗОПРОВОДОВ «ГАЗЛИ – САРИМОЙ» И «АКЧАЛОК – ГАЗЛИ – НУКУС» ОБЩЕЙ ПРОТЯЖЕННОСТЬЮ НЕ МЕНЕЕ 275 КМ».

Изм.	Кол. уч.	Лист.	№док.	Подп.	Дата
ГИП		Скабицкий А.			03.09.26
Нач.отд.		Юткина И.			03.09.26
Исполн.		Абдурахманов Ш.			03.09.26
Н. контр.		Скабицкий А.			03.09.26

ГАЗОПРОВОД «ГАЗЛИ-САРИМОЙ» (54 КМ)

План с системами В 1, Т3, на отм . ±0.198

План с системой К 1 на отм . ±0.198


Стадия	Лист	Листов
РД	1	2

ООО "EAST-WEST Engineering"
г. Ташкент 2026г.

Взам. инв. №
Подпись и дата
Инв.№ подл.

Формат А1

План кровли
(1:100)

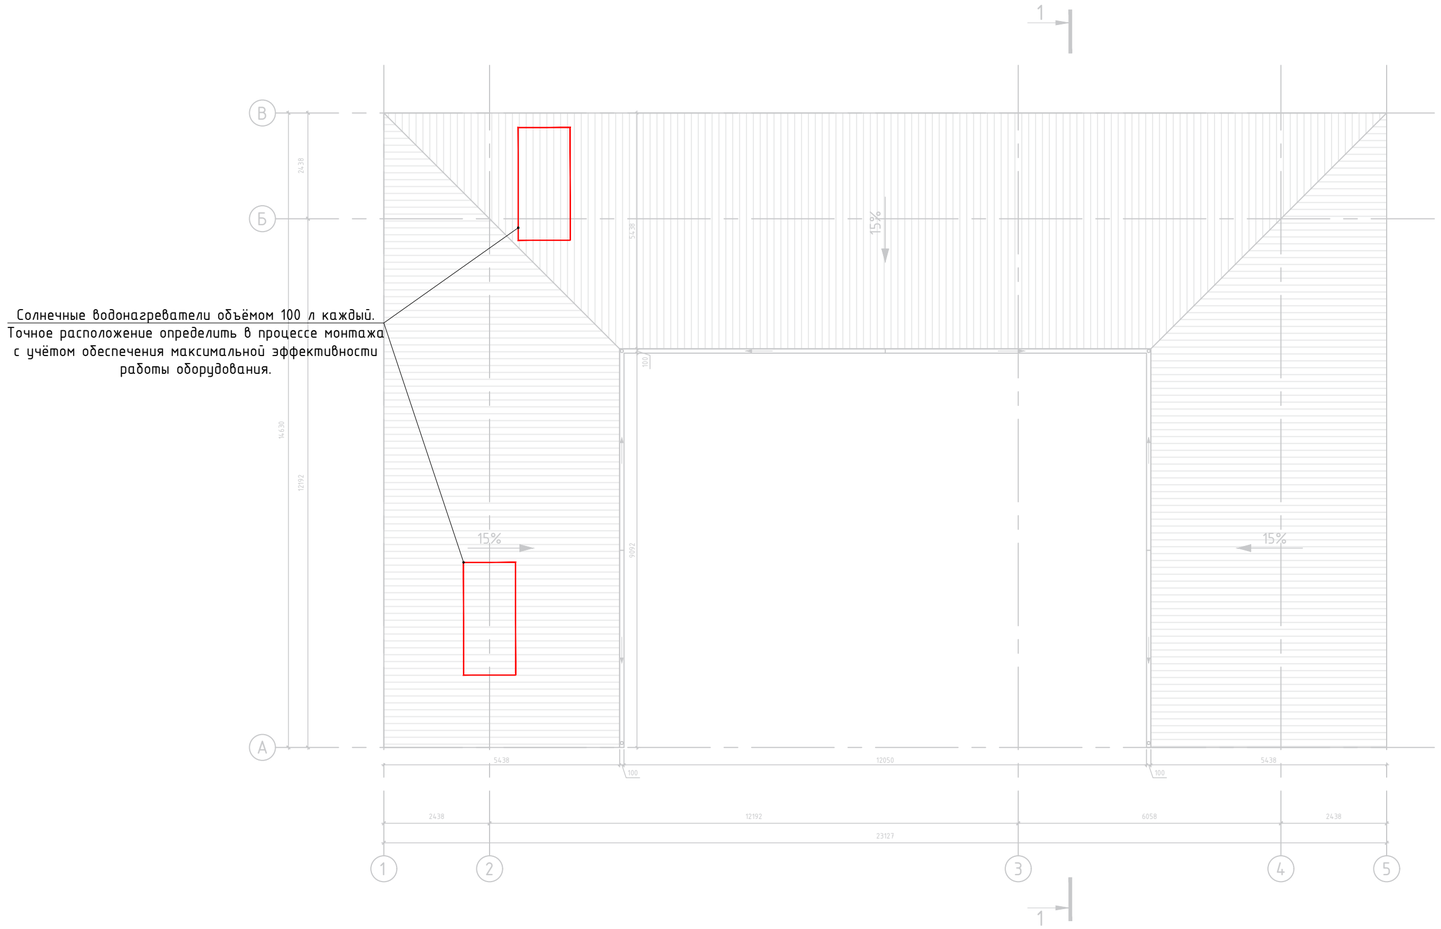

Солнечные водонагреватели объёмом 100 л каждый. Точное расположение определить в процессе монтажа с учётом обеспечения максимальной эффективности работы оборудования.


Примечание:

1. Все диаметры указаны внутренние условно проходные, согласно ГОСТ.
2. Все повороты 90° предусмотреть посредством двух полуотводов 45°
3. Все тройники косые - 45°
4. В настоящих чертежах отметка чистого пола +0.180 принята за ±0.000

Условные обозначения :

———	В1	Холодное водоснабжение (ХВС)
———	К1	Хоз. бытовая канализация
———	Т3	Горячее водоснабжение (ГВС)
	Ум	Умывальник
	Мк	Мойка
	Ун	Унитаз
	Пр	Прочистка
	Р	Ревизия
	Кр	Кран запорный шаровой

Узел А

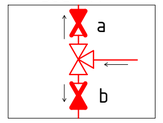

Узел автоматического переключения потока горячей воды трехходовым клапаном.

a - подача воды в накопительный водонагреватель (при T < +50 °C).
b - подача горячей воды к потребителям (при T ≥ +50 °C).

Рев.	Дата	Назначение ревизии	Проверил	Утвердил
А1	03.09.2026	Выпущен для строительства	Юткина И.	Схабицкий А.
R1	07.08.2026	Выпущен для рассмотрения	Юткина И.	Схабицкий А.

ЗАКАЗЧИК: UTG ГЕНЕРАЛЬНЫЙ ПОДРЯДЧИК: UET ПОДРЯДЧИК: PBG ГЕНЕРАЛЬНЫЙ ПРОЕКТИРОВЩИК: EAST WEST ENGINEERING

Изм.	Кол. уч.	Лист.	№док.	Подп.	Дата
ГИП		Схабицкий А.			03.09.26
Нач.отд.		Юткина И.			03.09.26
Исполн.		Абдурахманов Ш.			03.09.26
Н. контр.		Схабицкий А.			03.09.26

EWE0426-MGL1-WSS-054-PLA-801202-A1

«СТРОИТЕЛЬСТВО НОВЫХ НИТОК (УЧАСТКОВ) ГАЗОПРОВОДОВ «ГАЗЛИ - САРИМОЙ» И «АКЧАЛОК - ГАЗЛИ - НУКУС» ОБЩЕЙ ПРОТЯЖЕННОСТЬЮ НЕ МЕНЕЕ 275 КМ».

ГАЗОПРОВОД «ГАЗЛИ-САРИМОЙ» (54 КМ)

Стадия	Лист	Листов
РД	2	2

План с системами В 1, Т3, на отм . ±0.198
План с системой К 1 на отм . ±0.198

ООО "EAST-WEST Engineering"
г. Ташкент 2026г.

Взам. инв. №
Подпись и дата
Инв.№ подл.

Формат А2