Аксонометрическая схема системы водоснабжения

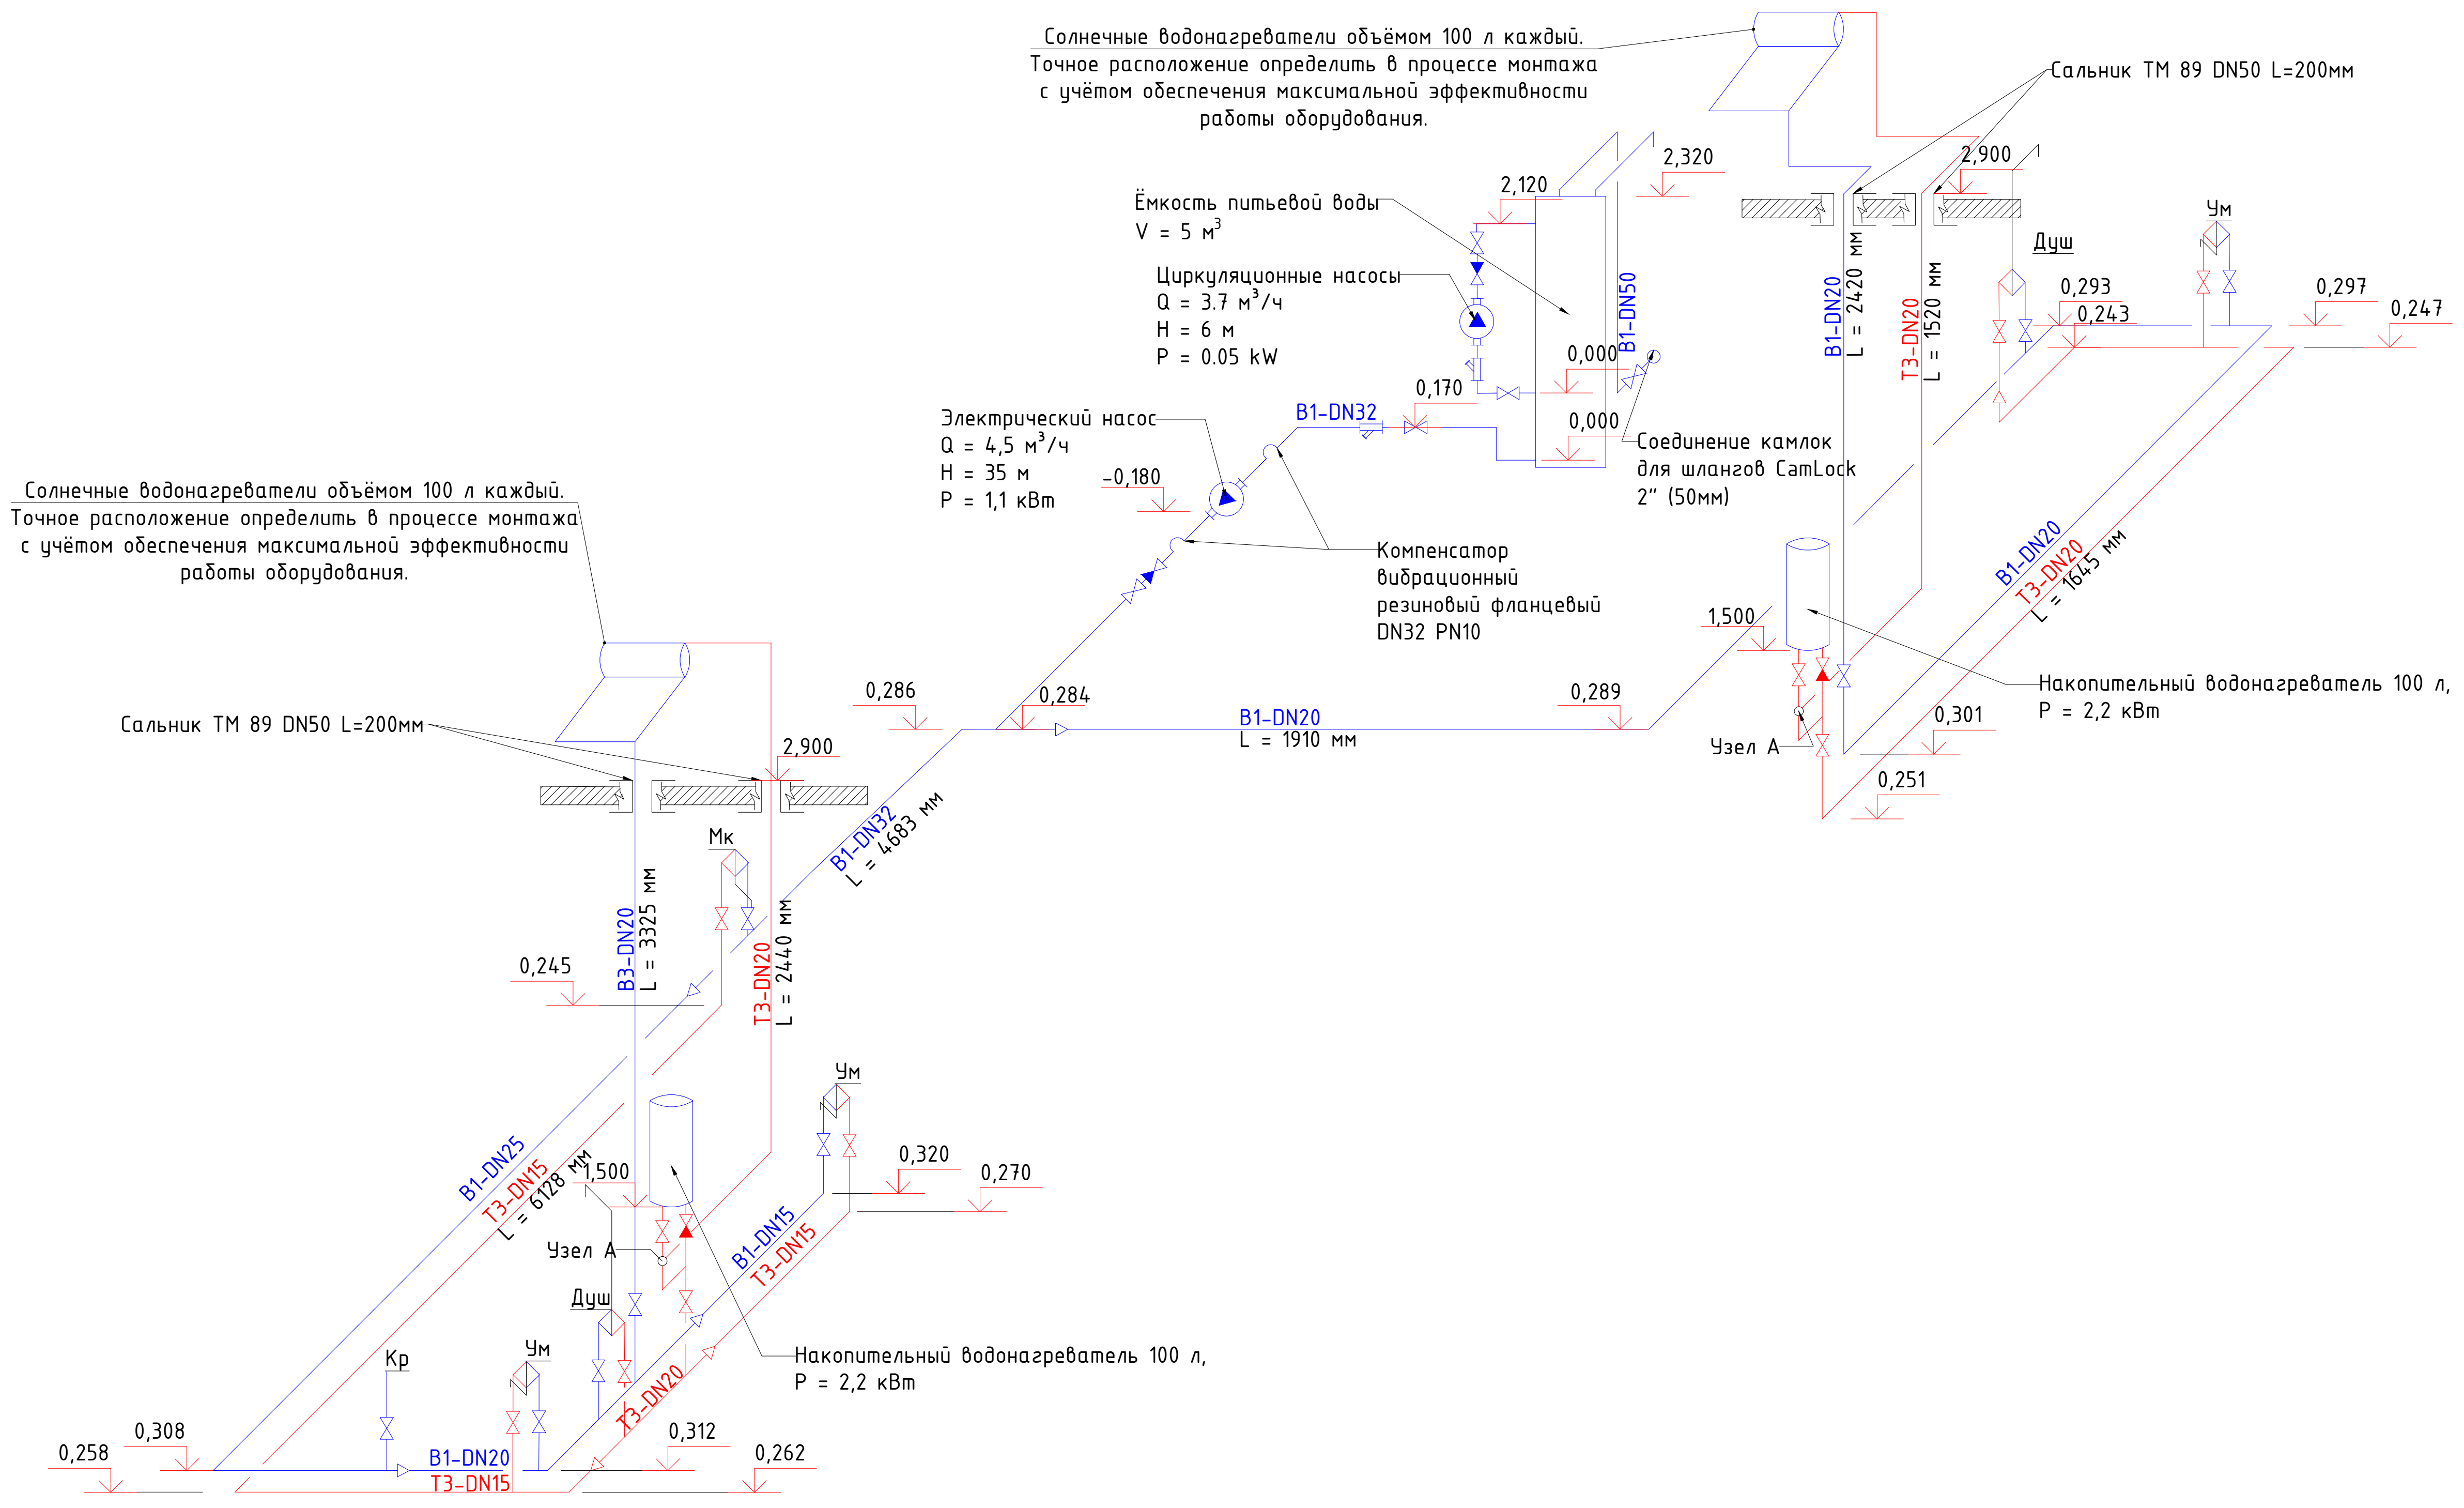
Солнечные водонагреватели объёмом 100 л каждый.
Точное расположение определить в процессе монтажа
с учётом обеспечения максимальной эффективности
работы оборудования.
Ёмкость питьевой воды
V = 5 м³
Циркуляционные насосы
Q = 3.7 м³/ч
H = 6 м
P = 0.05 kW
Электрический насос
Q = 4,5 м³/ч
H = 35 м
P = 1,1 кВт
Компенсатор
вибрационный
резиновый фланцевый
DN32 PN10
Соединение камлок
для шлангов CamLock
2" (50мм)
Сальник ТМ 89 DN50 L=200мм
Накопительный водонагреватель 100 л,
P = 2,2 кВт
Узел А
Душ
Ум
Мк
Кр
В1-DN50
В1-DN32
В1-DN32
L = 4683 мм
В1-DN20
L = 1910 мм
В1-DN20
L = 2420 мм
Т3-DN20
L = 1520 мм
В1-DN20
Т3-DN20
L = 1645 мм
В3-DN20
L = 3325 мм
Т3-DN20
L = 2440 мм
В1-DN25
Т3-DN15
L = 6128 мм
В1-DN15
Т3-DN15
Т3-DN20
В1-DN20
Т3-DN15
2,120
2,320
2,900
2,900
0,000
0,000
0,170
-0,180
0,286
0,284
0,289
1,500
0,301
0,251
0,293
0,243
0,297
0,247
0,245
1,500
0,320
0,270
0,308
0,258
0,312
0,262

Примечание:

1. Все диаметры указаны внутренние условно проходные, согласно ГОСТ.
2. Все повороты 90° предусмотреть посредством двух полуотводов 45°
3. Все тройники косые – 45°
4. В настоящих чертежах отметка чистого пола +0.180 принята за ±0.000.

Условные обозначения :

—	В1	Холодное водоснабжение (ХВС)
—	К1	Хоз. бытовая канализация
—	Т3	Горячее водоснабжение (ГВС)
	Ум	Умывальник
	Мк	Мойка
	Ун	Унитаз
	Пр	Прочистка
	Р	Ревизия
	Кр	Кран запорный шаровой

Узел А

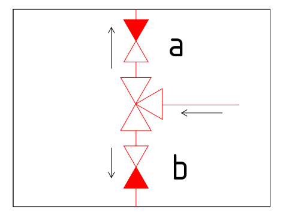

Узел автоматического переключения потока горячей воды трехходовым клапаном.

a – подача воды в накопительный водонагреватель (при T < +50 °C).
b – подача горячей воды к потребителям (при T ≥ +50 °C).

Аксонометрическая схема системы канализации

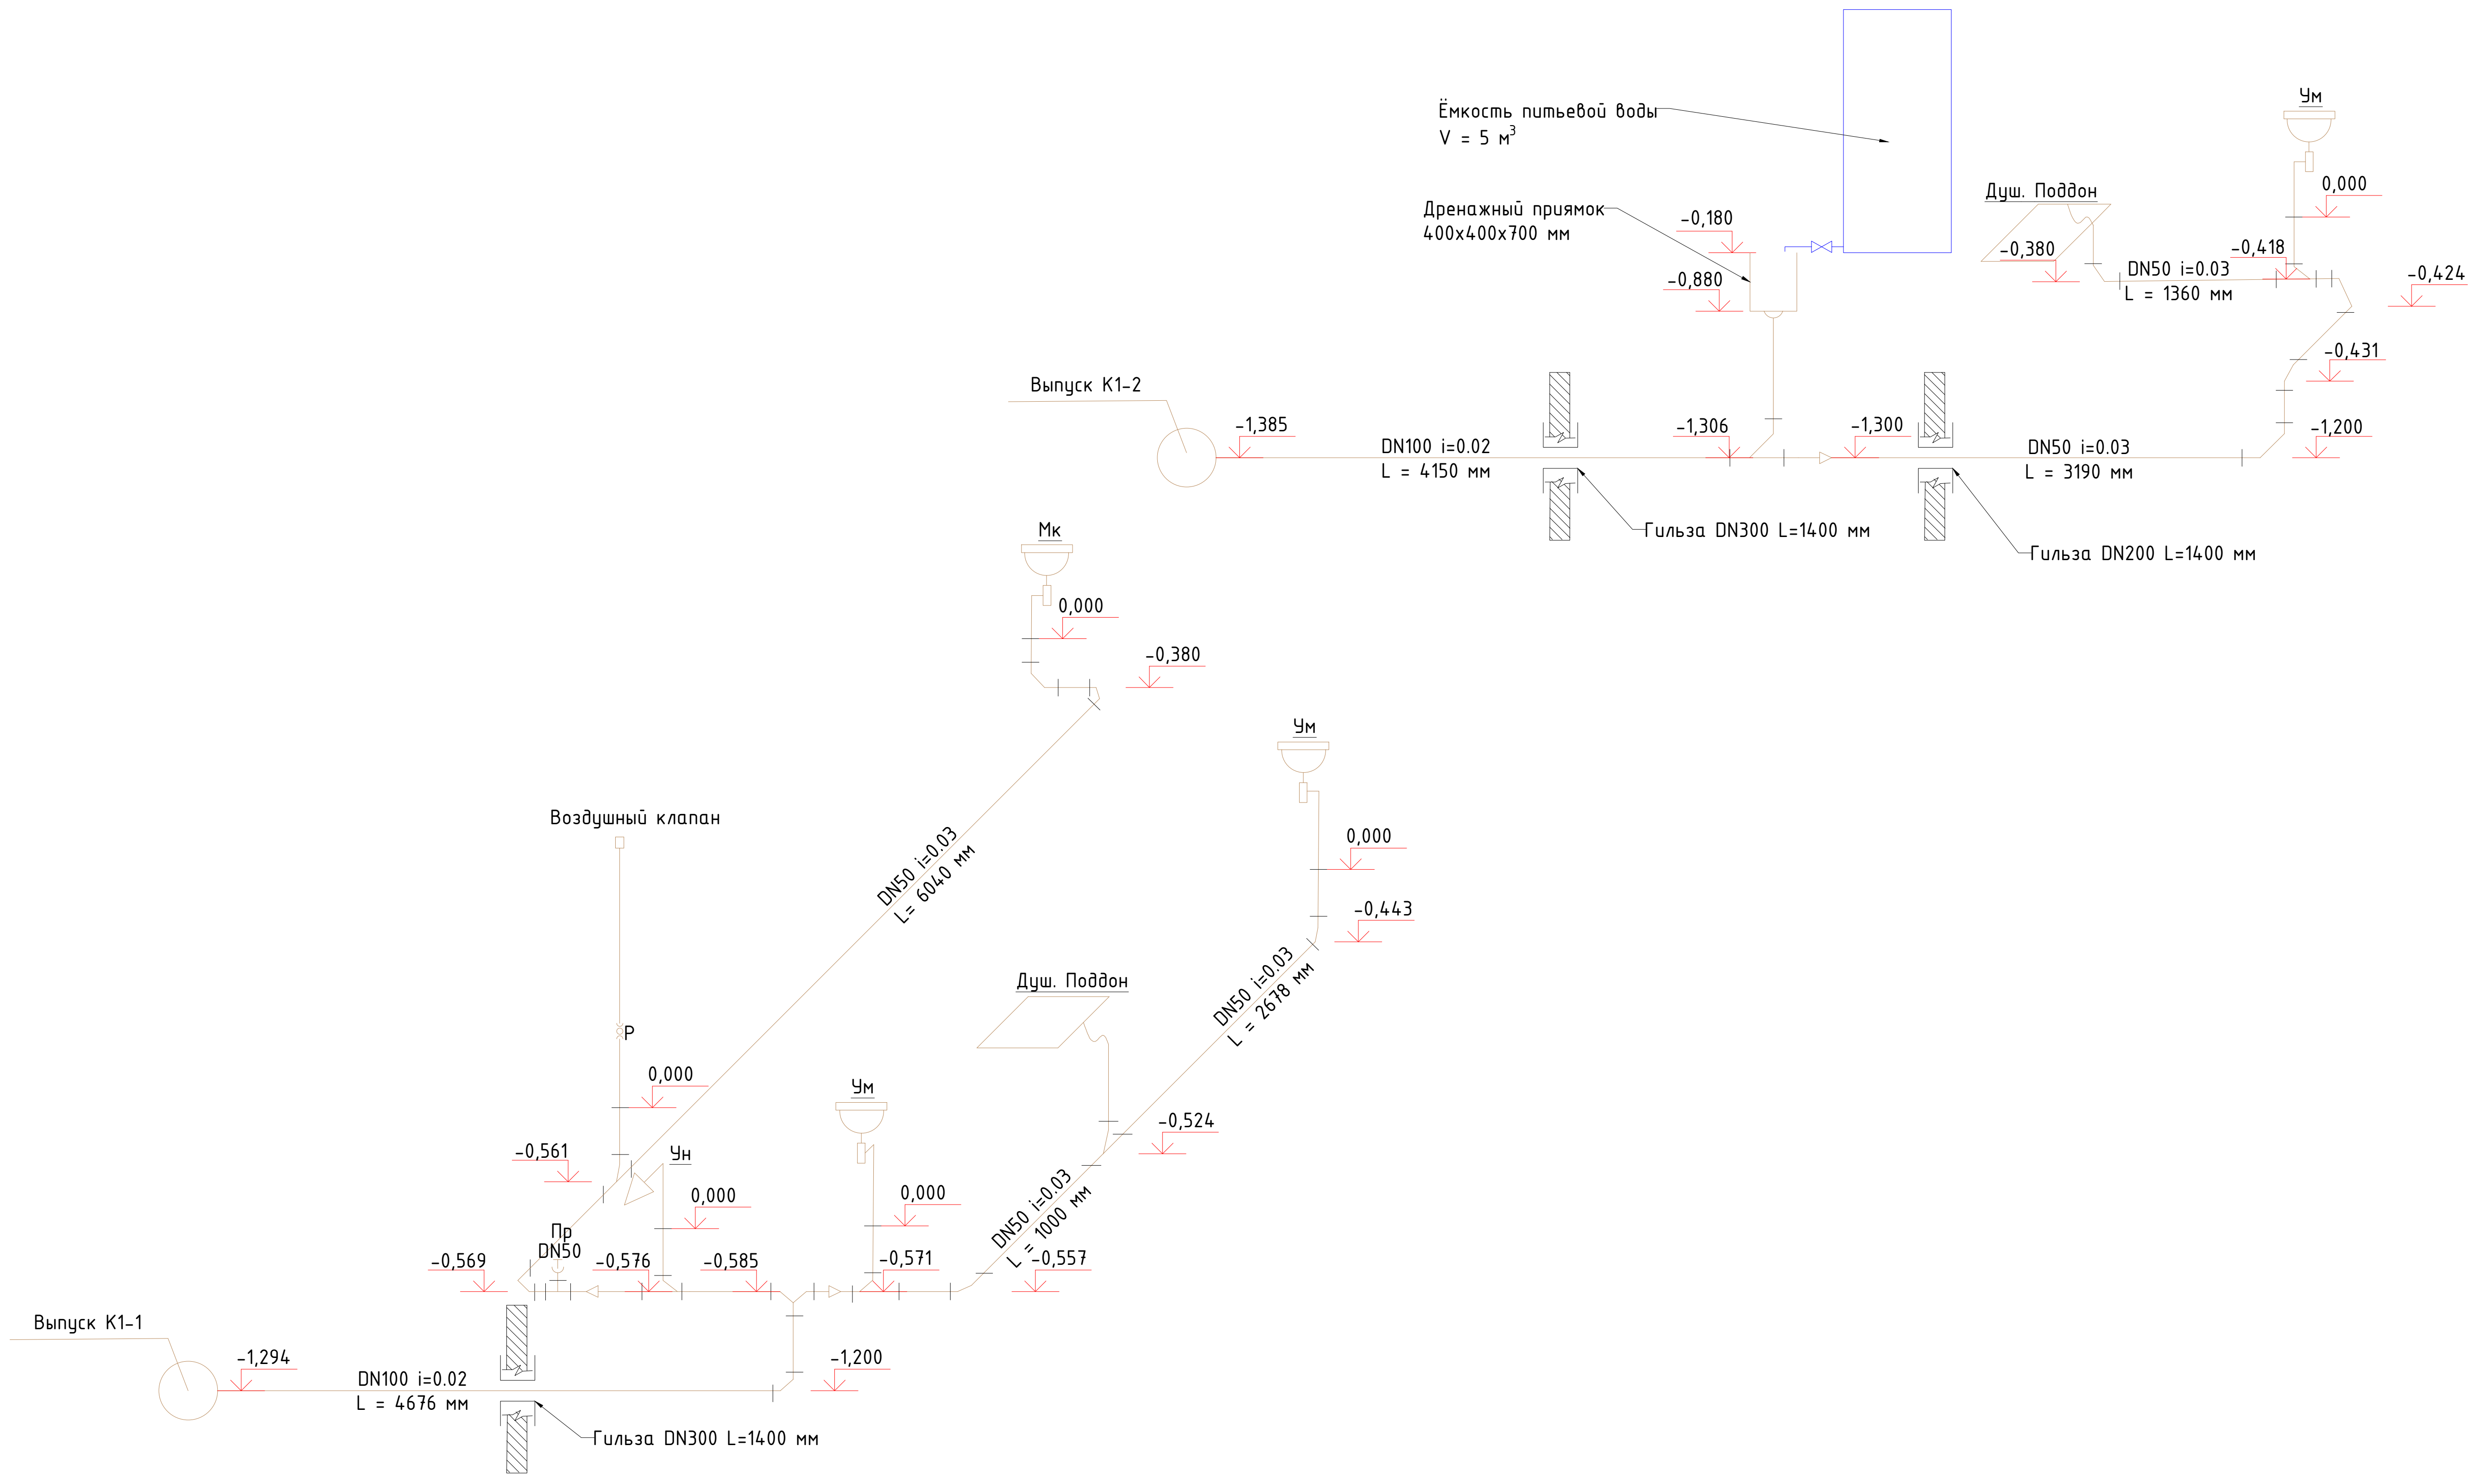
Ёмкость питьевой воды
V = 5 м³
Дренажный приямок
400x400x700 мм
Душ. Поддон
Ум
Мк
Ун
Пр
DN50
Р
Воздушный клапан
Выпуск К1-2
Выпуск К1-1
DN100 i=0.02
L = 4150 мм
DN50 i=0.03
L = 3190 мм
DN50 i=0.03
L = 1360 мм
DN50 i=0.03
L= 6040 мм
DN50 i=0.03
L = 2678 мм
DN50 i=0.03
L = 1000 мм
DN100 i=0.02
L = 4676 мм
Гильза DN300 L=1400 мм
Гильза DN200 L=1400 мм
Гильза DN300 L=1400 мм
-0,180
-0,880
-0,380
-0,418
0,000
-0,424
-0,431
-1,200
-1,385
-1,306
-1,300
0,000
-0,380
0,000
-0,443
-0,524
0,000
-0,561
0,000
0,000
-0,569
-0,576
-0,585
-0,571
-0,557
-1,294
-1,200

Взам. инв. №
Подпись и дата
Инв.№ подл.

Рев.	Дата	Назначение ревизии	Проверил	Утвердил
A1	03.09.2026	Выпущен для строительства	Юткина И.	Схабицкий А.
R1	07.08.2026	Выпущен для рассмотрения	Юткина И.	Схабицкий А.

ЗАКАЗЧИК: UTG UZTRANSGAZ
ГЕНЕРАЛЬНЫЙ ПОДРЯДЧИК: UET UZBEKENERGOTAMIR
ПОДРЯДЧИК: PBG Pro Build Generation
ГЕНЕРАЛЬНЫЙ ПРОЕКТИРОВЩИК: EAST WEST ENGINEERING

EWE0426-MGL1-WSS-054-SCM-801203-A1

«СТРОИТЕЛЬСТВО НОВЫХ НИТОК (УЧАСТКОВ) ГАЗОПРОВОДОВ «ГАЗЛИ – САРИМОЙ» И «АКЧАЛОК – ГАЗЛИ – НУКУС» ОБЩЕЙ ПРОТЯЖЕННОСТЬЮ НЕ МЕНЕЕ 275 КМ».

Изм.	Кол. уч.	Лист.	№док.	Подп.	Дата
ГИП		Схабицкий А.			03.09.26
Нач.отд.		Юткина И.			03.09.26
Исполн.		Абдурахмонов Ш.			03.09.26
Н. контр.		Схабицкий А.			03.09.26

ГАЗОПРОВОД «ГАЗЛИ-САРИМОЙ» (54 КМ)

Стадия	Лист	Листов
РД	1	1

Схема систем В1, Т3, К1

ООО "EAST-WEST Engineering"
г. Ташкент 2026г.

Формат А1