
План системы отопления
(1:50)

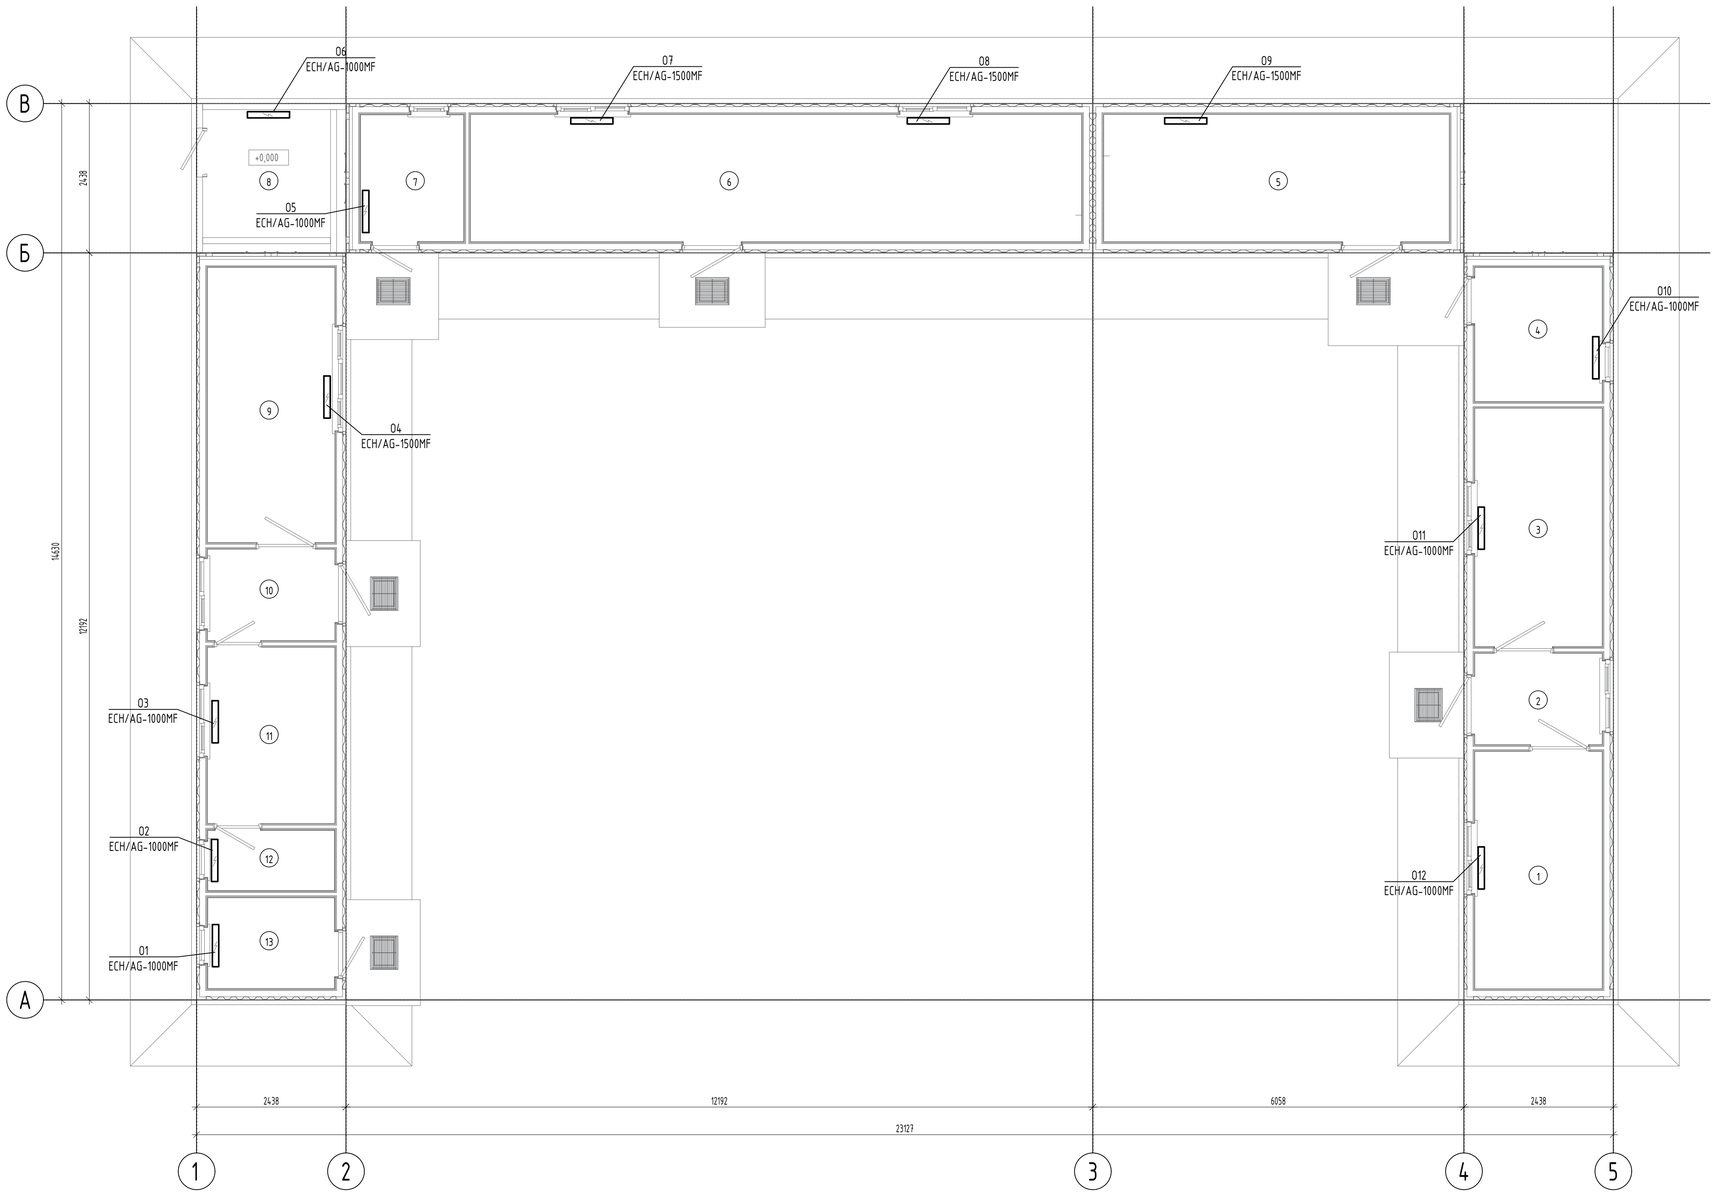

Экспликация помещений

№	Наименование	Площадь, м²	Кат. помещения
1	Кабинет ведущего инженера	8,10	?
2	Тамбур	3,10	?
3	Кабинет инженера химика	8,10	?
4	Кладовая	4,60	?
5	Электрощитовая	11,80	?
6	Кабинет операторов	20,80	?
7	Душ	3,50	–
8	Насосная	4,40	?
9	Комната отдыха и приема пищи	9,40	–
10	Тамбур	3,10	?
11	Гардероб	6,00	?
12	Душ	2,10	–
13	С/У	3,10	–

Условные обозначения:

О	Отопительный агрегат

Примечание

1. Все размеры даны в миллиметрах, если не указано иначе.
2. Электрический конвектор установить на отметке +0,300

Рев.	Дата	Назначение ревизии	Проверил	Утвердил
A1	03.09.2026	Выпущено для строительства		
R1	04.08.2026	Выпущено для рассмотрения		

ЗАКАЗЧИК: ГЕНЕРАЛЬНЫЙ ПОДРЯДЧИК: ПОДРЯДЧИК: ГЕНЕРАЛЬНЫЙ ПРОЕКТИРОВЩИК:

EWE0426-MGL1-HVA-054-DRW-800902-A1

«СТРОИТЕЛЬСТВО НОВЫХ НИТОК (УЧАСТКОВ) ГАЗОПРОВОДОВ «ГАЗЛИ – САРИМОЙ» И «АКЧАЛОК – ГАЗЛИ – НУКУС» ОБЩЕЙ ПРОТЯЖЕННОСТЬЮ НЕ МЕНЕЕ 275 КМ».

Изм.	Кол. уч.	Лист.	№док.	Подп.	Дата
ГИП		Схабицкий А.			3.09.26
Нач.отд.		Пак В.			3.09.26
Исполн.		Пак В.			3.09.26
Н. контр.		Схабицкий А.			3.09.26

ГАЗОПРОВОД «ГАЗЛИ-САРИМОЙ» (54 КМ)
ОПЕРАТОРНАЯ

Стадия	Лист	Листов
РД	1	1

План системы отопления
(1:50)

ООО "EAST-WEST Engineering"
г. Ташкент 2026г.

Взам. инв. №
Подпись и дата
Инв.№ подл.

Формат А1