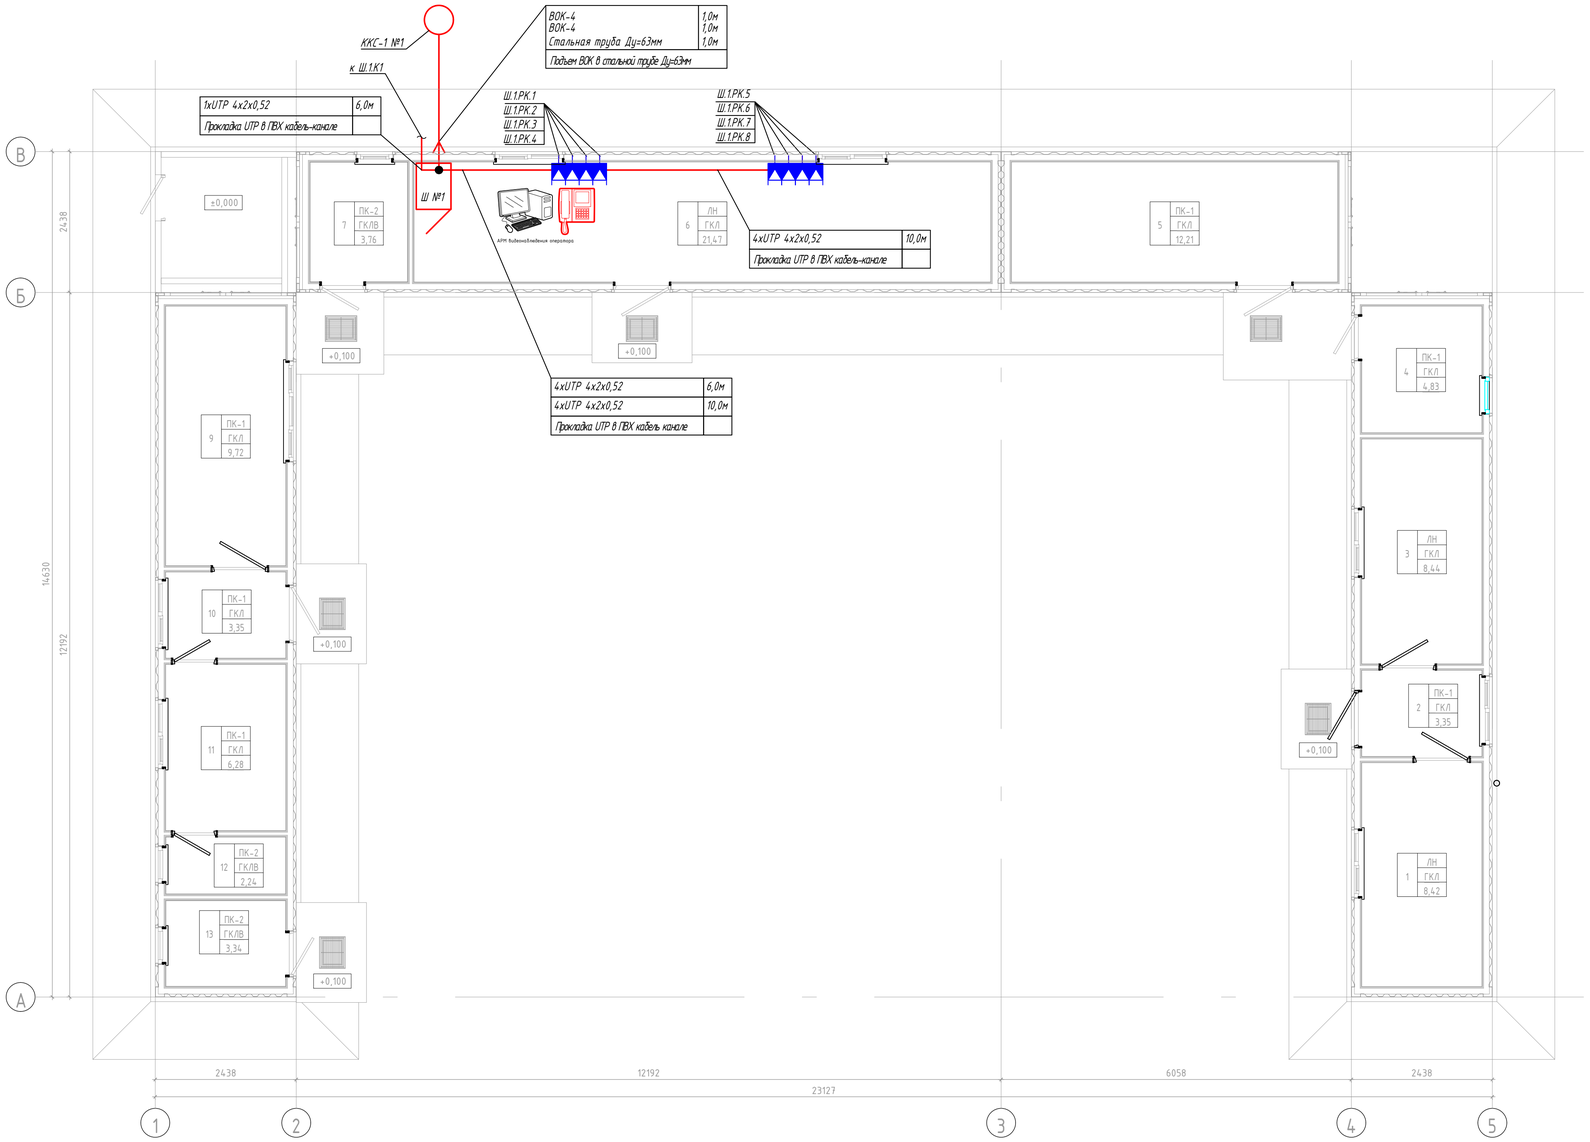


Экспликация помещений

№	Наименование	Площадь	Кат. помещения
1	Кабинет ведущего инженера	8.10 м²	?
2	Тамбур	3.13 м²	?
3	Кабинет инженера химика	8.14 м²	?
4	Кладовая	4.60 м²	?
5	Электрощитовая	5.84 м²	?
6	Кабинет операторов	20.94 м²	?
7	Душ	3.54 м²	–
8	Насосная	4.36 м²	?
9	Комната отдыха и приема пищи	9.40 м²	–
10	Тамбур	3.13 м²	?
11	Гардероб	6.00 м²	?
12	Душ	2.08 м²	А
13	С/У	3.13 м²	–

Система нумерации шкафов:

Ш №1
- Номер шкафа
- Шкаф телекоммуникационный

ПРИМЕЧАНИЯ:

1. Данный документ рассматривать совместно с документами:
   - EWE0426-MGL1-COS-054-COM-801301 Общие данные;
   - EWE0426-MGL1-COS-054-SCM-801302 Структурные схемы;
   - EWE0426-MGL1-COS-054-DRW-801304 Типовые монтажные чертежи
   - EWE0426-MGL1-COS-054-SCH-801305 Кабельный журнал;
   - EWE0426-MGL1-COS-054-SPC-801306 Спецификация оборудования и материалов.

УСЛОВНЫЕ ОБОЗНАЧЕНИЯ:

- Телекоммуникационный шкаф
- Кабельная трасса системы, проложенная кабель каналe

Рев.	Дата	Назначение ревизии	Проверил	Утвердил
R1	11.08.2026	Выпущено для рассмотрения		

ЗАКАЗЧИК: UTG SUSTAINABLE SOLUTIONS

ГЕНЕРАЛЬНЫЙ ПОДРЯДЧИК: UET CONSTRUCTION

ПОДРЯДЧИК: PBC

ГЕНЕРАЛЬНЫЙ ПРОЕКТИРОВЩИК: EAST WEST ENGINEERING

EWE0426-MGL1-COS-054-DRW-801303-R1

«СТРОИТЕЛЬСТВО НОВЫХ НИТОК (УЧАСТКОВ) ГАЗОПРОВОДОВ «ГАЗЛИ – САРИМОЙ» И «АКЧАЛОК – ГАЗЛИ – НУКУС» ОБЩЕЙ ПРОТЯЖЕННОСТЬЮ НЕ МЕНЕЕ 275 КМ»

ГАЗОПРОВОД «ГАЗЛИ-САРИМОЙ» (54 КМ) УЗРГ-D001

Изм.	Колуч.	Лист	№док.	Подпись	Дата
ГИП		Схабицкий А.			08.2026
Нач.отд.		Кабулова Е.			08.2026
Исполн.		Гальцев В.			08.2026
Н.контр.		Схабицкий А.			08.2026

План расположения оборудования и кабельных трасс

Стадия	Лист	Листов
РД	1	2


ООО "EAST-WEST Engineering" г. Ташкент 2026г

Взам. инв. №

Подпись и дата


Инв.№ подл.

Формат А3х3

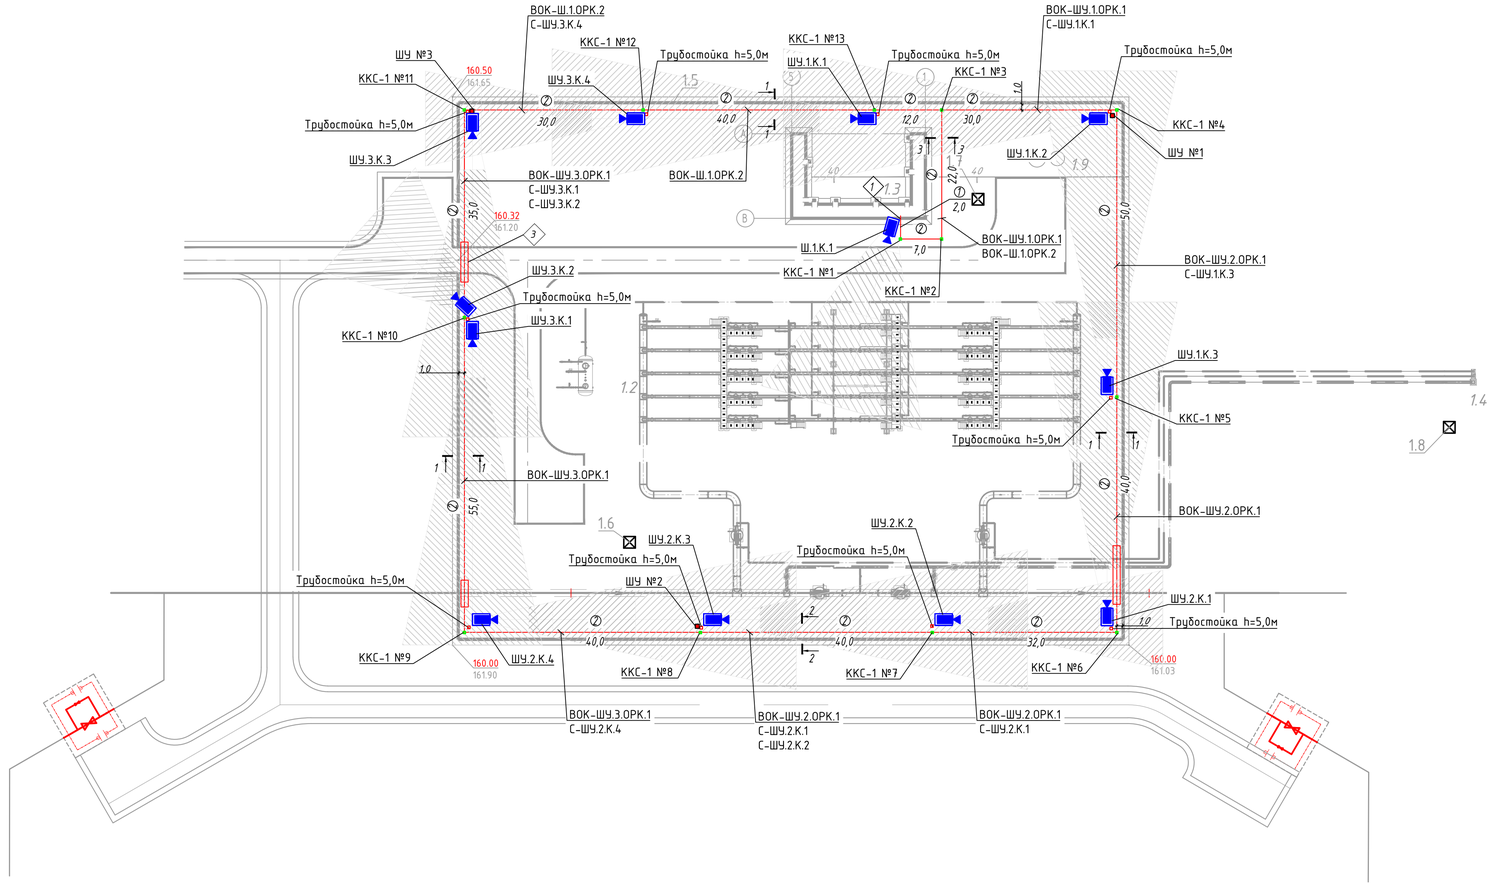

Экспликация зданий и сооружений

Номер на плане	Наименование	Примечание
1	Площадка УЗРГ	
1.1	Блок качества газа	
1.2	Площадка дренажной емкости V=25м3	
1.3	Операторная	
1.4	Продувочные свечи	
1.5	Сетчатое ограждение с воротами шир.4.5 м	
1.6	Прожекторная мачта ПМЖ-22.8	
1.7	Прожекторная мачта ПМЖ-22.8	
1.8	Молниеотвод МЖ-24.3	
1.9	Выгреб	

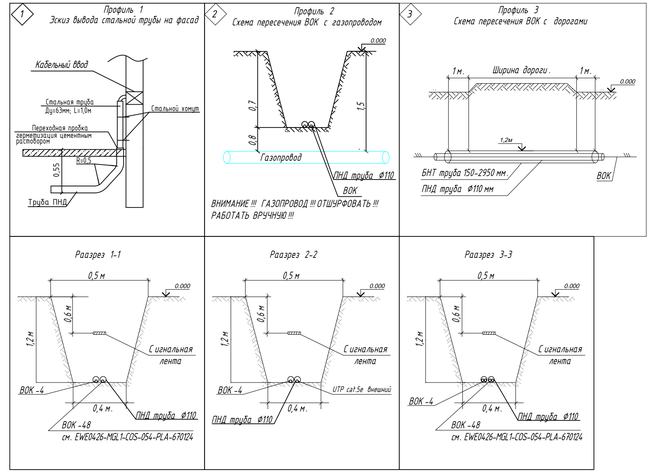

УСЛОВНЫЕ ОБОЗНАЧЕНИЯ:

- Проектируемая кабельная канализация связи
- Проектируемый кабельный колодец связи
- (1) Количество проектируемых каналов кабельной канализации связи
- 35,0 Длина пролёта кабельной канализации связи
- Камера видеонаблюдения наружной установки
- Шкаф уличный
- Опора видеонаблюдения (трубостойка)
- Зона обзора видеокамеры

Система нумерации шкафов: ШЧ №2 — Номер уличного шкафа; Шкаф уличный

Система нумерации камер: ШУ.2.К.1 — Номер камеры видеонаблюдения; Камера видеонаблюдения; Номер уличного шкафа; Шкаф уличный/номер позиции по генплану

ПРИМЕЧАНИЯ:

1. Данный документ рассматривать совместно с документами:
EWE0426-MGL1-COS-054-COM-801301 Общие данные;
EWE0426-MGL1-COS-054-SCM-801302 Структурные схемы;
EWE0426-MGL1-COS-054-DRW-801304 Типовые монтажные чертежи
EWE0426-MGL1-COS-054-SCH-801305 Кабельный журнал;
EWE0426-MGL1-COS-054-SPC-801306 Спецификация оборудования и материалов.

Изм.	Кол.	Лист	№док	Подпись	Дата	EWE0426-MGL1-COS-054-DRW-801303-R1	Лист 2

Инв. N подл. | Подп. и дата | Взам. инв. N

Формат А3х3