

Вид А

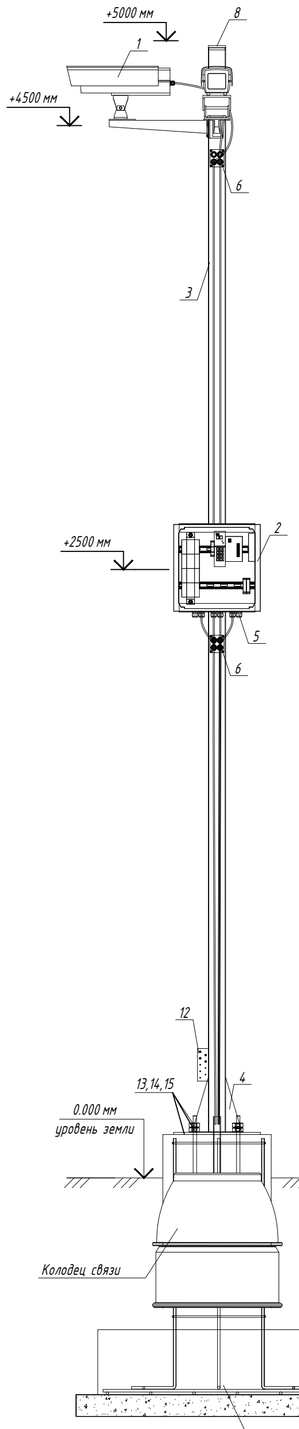


Фундамент ФМ-11 учтено в разделе (STR)
UZLE-78-450-SST-COM-170601

Вид Б

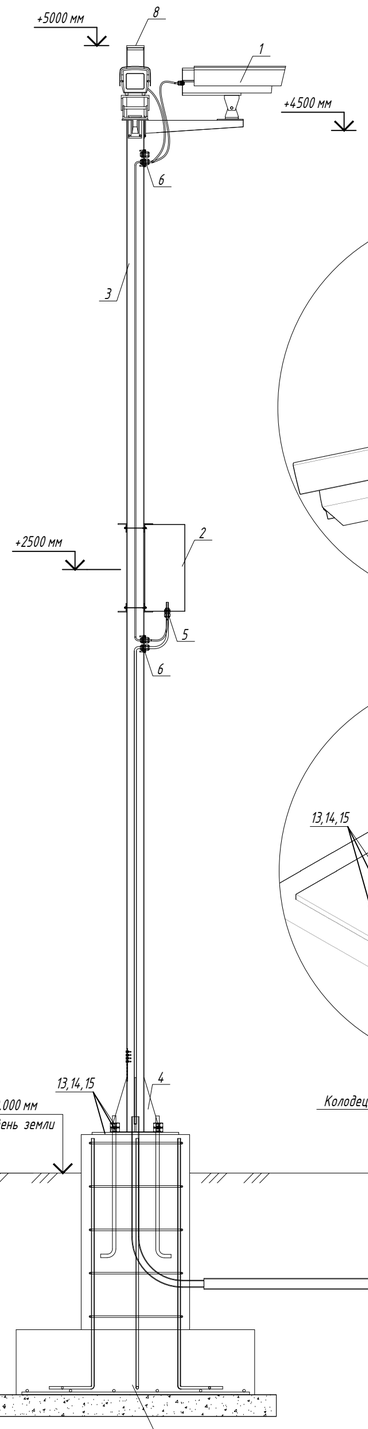


Фундамент ФМ-11 учтено в разделе (STR)
UZLE-78-450-SST-COM-170601

Фрагмент II

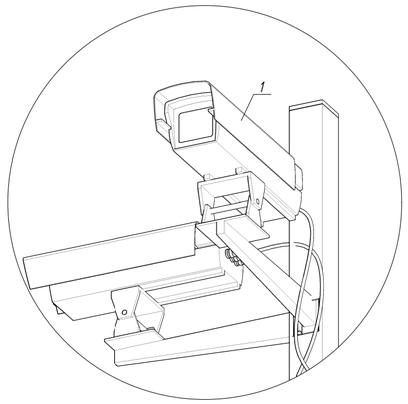

Фрагмент I

Общий вид

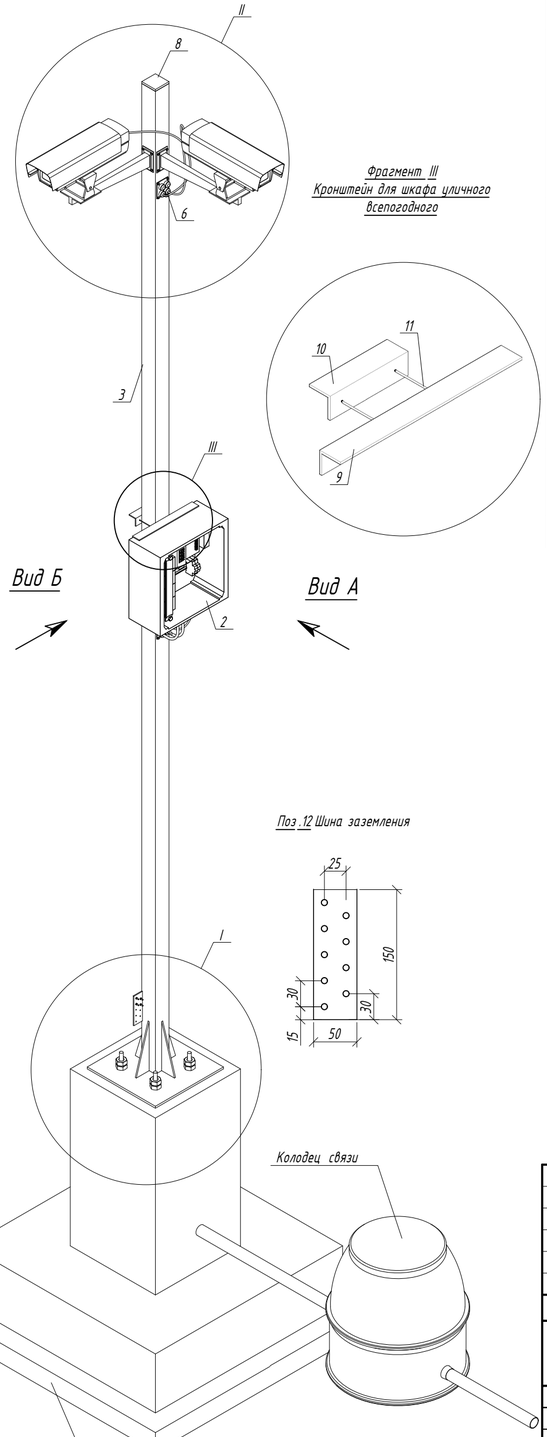

Фундамент ФМ-11 учтено в разделе (STR)
UZLE-78-450-SST-COM-170601

Вид Б

Вид А

Фрагмент III
Кронштейн для шкафа уличного всепогодного

Поз.12 Шина заземления

Спецификация оборудования и материалов

Поз	Обозначение	Наименование	Ед.изм	Кол.	Масса ед. кг	Примечание
		Оборудование				
1		Видеокамера в комплекте с кронштейном	шт.	2	-	
2		Шкаф уличный всепогодный	шт.	1	-	
		Детали				
3		Профильная труба 80х80х4 ГОСТ 8636-82 L=5000 мм	шт.	1	9.33	46.65
4		Косынка 75х250х4 ГОСТ 19903-74	шт.	4	0.589	2.3560
		Прочие изделия				
5		Кабельный уплотнитель М32х1,5 с контргайкой (D кабеля 15-22 мм, IP68)	шт.	6	-	
6		Кабельный ввод пластиковый на (4 ввода)	шт.	2		
7		Болт с гайкой и шайбой М4х20 ГОСТ 7798-70, ГОСТ 5915-70	к-т	9	0,0027	0.0243
8		Пластиковая заглушка квадратная для профильной трубы 80 х 80	шт.	1	-	
9		Уголок 40х40х4 ГОСТ 8509-93 L=350 мм	шт.	2	0.847	1.694
10		Уголок 40х40х4 ГОСТ 8509-93 L=150 мм	шт.	2	0.282	0.564
11		Шпилька резьбовая М 10 в комплекте с гайкой и шайбой	к-т	4		
12		Лист 50х150х4 ГОСТ 19903-74	шт.	1	0.235	0.235
13		Лист 400х400х10 ГОСТ 19903-74	шт.	1	31.4	31.40
14		Гайка шестигранная М 16 ГОСТ 5927-70	шт.	8	0.0376	0.30
15		Шайба увеличенная м 16 ГОСТ 6958-78	шт.	8	0,0403	0.32

Примечание:

1. Данный документ рассматривать совместно с документами:
   EWE0426-MGL1-COS-054-COM-801301 Общие данные;
   EWE0426-MGL1-COS-054-SCM-801302 Структурные схемы;
   EWE0426-MGL1-COS-054-DRW-801303 План расположения оборудования и кабельных трасс
   EWE0426-MGL1-COS-054-SCH-801305 Кабельный журнал
   EWE0426-MGL1-COS-054-SPC-801306 Спецификация оборудования и материалов.
2. Трубостойки установить на фундаментные блоки ФМ-1. ФМ-1 учтены в строительной части проекта.
3. Монтаж камер и уличных шкафов выполнить в соответствии с инструкциями завода-изготовителя.
4. Предусмотреть монтаж уголка на трубостойку для установки уличных шкафов. Уголок к трубстойке закрепить по средине двумя саморезами.
5. Кабели проложить внутри трубостойки.
6. Разметка крепления определяется типом поставляемых устройств.
7. Все элементы креплений должны быть гальванизированными.
8. Внешний вид камер и уличных шкафов и колодцев связи показан условно.
9. Спецификация приведена для одной конструкции.
10. Высоту установки камер и уличных шкафов согласовать по месту с представителями Заказчика.

Рев.	Дата	Назначение ревизии	Проверил	Утвердил
R1	11.08.2026	Выпущено для рассмотрения		

ЗАКАЗЧИК: UTG UZTRANSGAZ | ГЕНЕРАЛЬНЫЙ ПОДРЯДЧИК: UET UZBEKENERGOTAME | ПОДРЯДЧИК: PBG Pro Build Generation | ГЕНЕРАЛЬНЫЙ ПРОЕКТИРОВЩИК: EAST WEST ENGINEERING

Изм.	Кол.уч.	Лист	№док.	Подпись	Дата	EWE0426-MGL1-COS-054-DRW-801304-R1		
						«СТРОИТЕЛЬСТВО НОВЫХ НИТОК (УЧАСТКОВ) ГАЗОПРОВОДОВ «ГАЗЛИ - САРИМОЙ» И «АКЧАЛОК - ГАЗЛИ - НУКУС» ОБЩЕЙ ПРОТЯЖЕННОСТЬЮ НЕ МЕНЕЕ 275 КМ»		
ГИП		Скабицкий А.			08.2026			
Нач.отд.		Кабулова Е.			08.2026	ГАЗОПРОВОД «ГАЗЛИ-САРИМОЙ» (54 КМ) УЗРГ-D001	Стадия	Лист	Листов
Исполн.		Гальцев В.			08.2026		РД		
Н.контр		Скабицкий А.			08.2026	Типовые монтажные чертежи	EAST WEST ENGINEERING	ООО "EAST-WEST Engineering" г. Ташкент 2026г.	

Взам. инв. № | Подпись и дата | Инв.№ подл.

Формат А3