
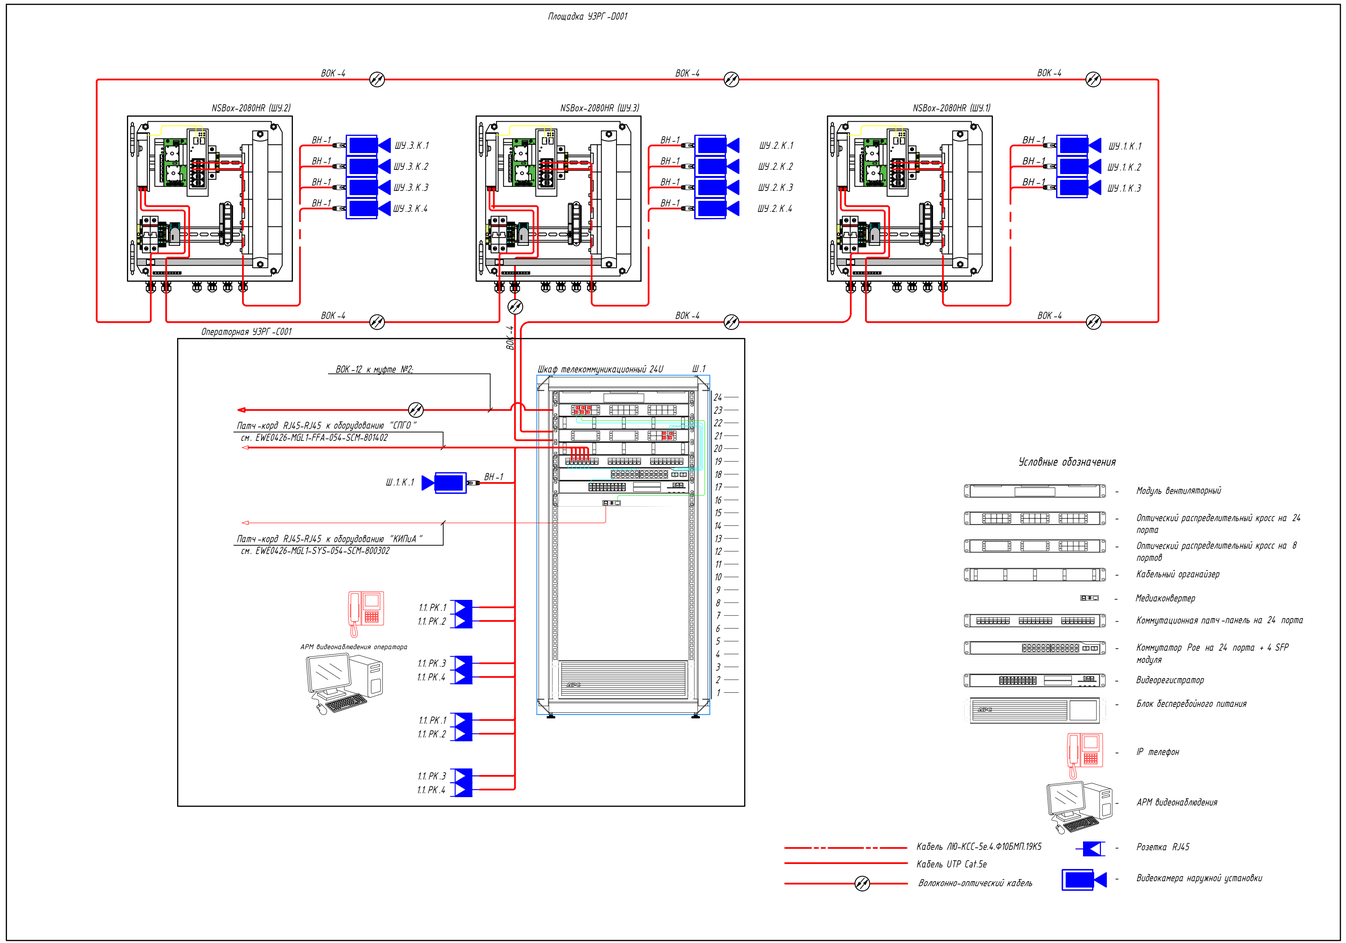


Схема разварки волокон ВОК на оптических кроссах.

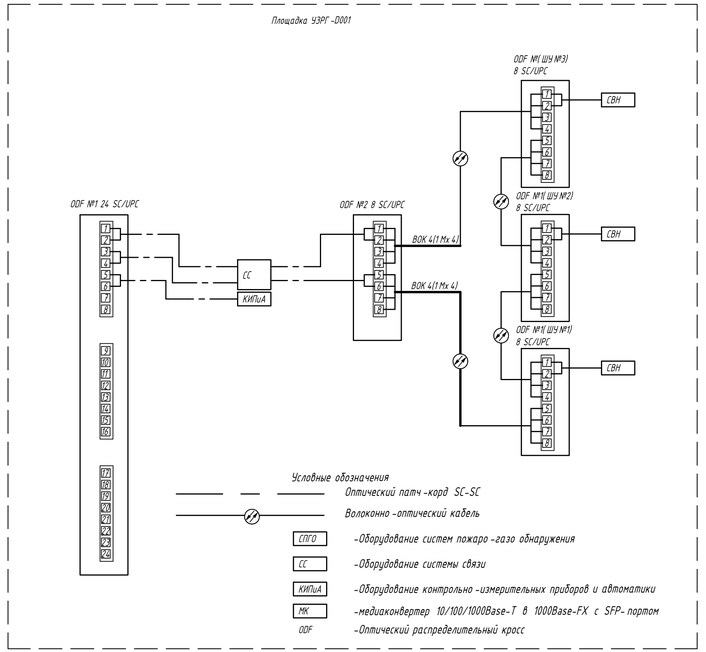

Примечания:

1. Данный документ рассматривать совместно с документами:
   EWE0426-MGL1-COS-054-COM-801301 Общие данные;
   EWE0426-MGL1-COS-054-DRW-801303 План расположения оборудования и кабельных трасс;
   EWE0426-MGL1-COS-054-DRW-801304 Типовые монтажные чертежи
   EWE0426-MGL1-COS-054-SCH-801305 Кабельный журнал;
   EWE0426-MGL1-COS-054-SPC-801306 Спецификация оборудования и материалов..
2. Оптический кабель оканчивается в ODF и является границей разделения проектирования.
3. SFP модули СКС и КИПиА и их тип должны быть учтены на втором этапе проекта SCADA Заказчиком.

Рев.	Дата	Назначение ревизии	Проверил	Утвердил
R1	11.08.2026	Выпущено для рассмотрения		

ЗАКАЗЧИК: UTG SUSTAINABLE INFRASTRUCTURE
ГЕНЕРАЛЬНЫЙ ПОДРЯДЧИК: UET CONSTRUCTION
ПОДРЯДЧИК: PBC
ГЕНЕРАЛЬНЫЙ ПРОЕКТИРОВЩИК: EAST WEST ENGINEERING

EWE0426-MGL1-COS-054-SCM-801302-R1

«СТРОИТЕЛЬСТВО НОВЫХ НИТОК (УЧАСТКОВ) ГАЗОПРОВОДОВ «ГАЗЛИ – САРИМОЙ» И «АКЧАЛОК – ГАЗЛИ – НУКУС» ОБЩЕЙ ПРОТЯЖЕННОСТЬЮ НЕ МЕНЕЕ 275 КМ»

ГАЗОПРОВОД «ГАЗЛИ-САРИМОЙ» (54 КМ) УЗРГ-D001

Изм.	Колуч.	Лист	№док.	Подпись	Дата
Гип		Схабицкий А.			08.2026
Нач.отд.		Кабулова Е.			08.2026
Испол.		Гальцев В.			08.2026
Н.контр.		Схабицкий А.			08.2026

Структурная схема

Стадия	Лист	Листов
РД	1	2


ООО "EAST-WEST Engineering"
г. Ташкент 2026г.

Взам. инв. №
Подпись и дата
Инв.№ подл.

Формат А3х3

Схема прокладки ВОЛС

Площадка УЗРГ -D001

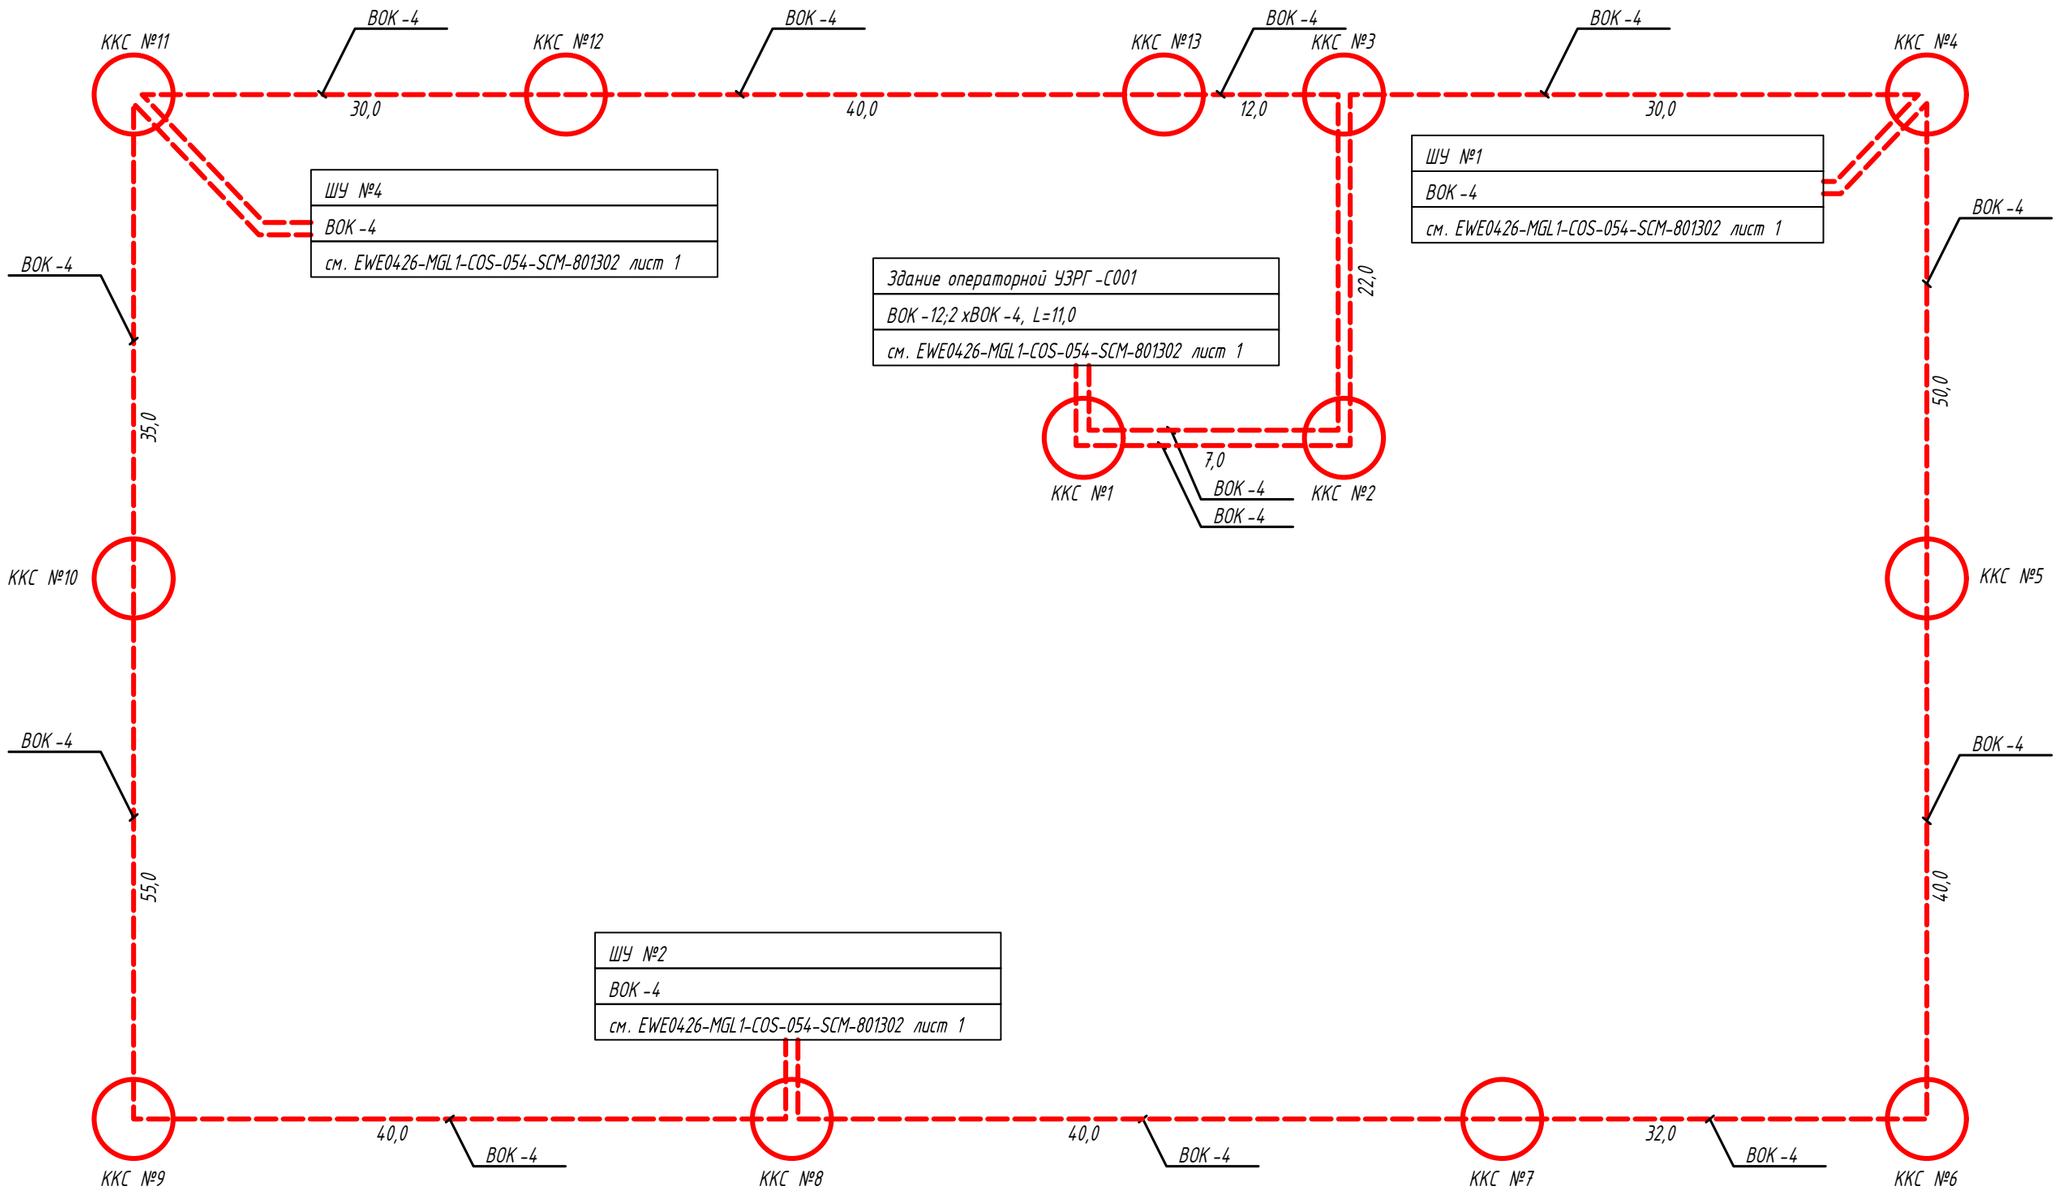

Условные обезначения:

Прокладка ВОК в проектируемой кабельной канализаации

Проектируемый колодец кабельной связи

Сокращения:

ВОК - волоконно -оптический кабель

ККС - кабельный колодец связи

УЗРГ - узел замера расхода газа

Изм.	Кол.	Лист	N°док.	Подпись	Дата	EWE0426-MGL1-COS-054-SCM-801302-R1	Лист 2

Взам. инв. N

Подп. и дата

Инв. N подл.

Формат А3