
Схема расположения фундаментов Фм 1. Схема расположения стоект Ст 1.
Схема расположения сеточных панелей



Разрез 1-1
(Траншея)

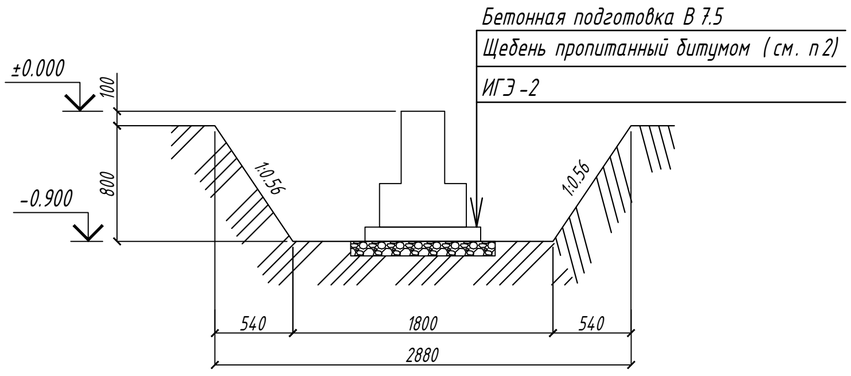

Ведомость элементов

Марка Поз.	Наименование	Кол. шт
	Фундамент Фм 1	137
	Стойка Ст 1	137
	Панель П 1	132
	Панель П 2	2
	Панель П 3	1
	Панель П 4	1
	Панель П 5 (ворота)	2

Объем разработки траншеи
1. *Объем траншеи - 778.75 м^3*
2. *Объем вывозимого грунта - 411.1 м^3*
3. *Объем грунта для обратной засыпки - 737.65 м^3*

Примечание
1. *Общие данные смотреть на листе EWE0426-MGL1-STR-054-COM-801701- A 1*
2. *Под монолитным фундаментом выполнить подготовку из бетона кл. В 7.5 толщиной 100 мм с уширением на 100 мм в каждую сторону от размеров подошвы фундамента. Под ним выполнить подготовку из щедня, вдавленного в грунт, толщиной 100 мм, с проливкой горячим битумом с выступом за боковые грани бетонной подготовки по 100 мм в каждую сторону.*
3. *Этот лист смотреть совместно с листами 801703, 801704, 801705*
4. *Траншею разработать согласно данному чертежу*

Рев.	Дата	Назначение ревизии	Проверил	Утвердил
A1	20.10.26	Выпущено для строительства		
R1	09.26	Выпущено для рассмотрения		

ЗАКАЗЧИК: UTG UZBEKNEFTEGAZ ГЕНЕРАЛЬНЫЙ ПОДРЯДЧИК: UET ПОДРЯДЧИК: PBG ГЕНЕРАЛЬНЫЙ ПРОЕКТИРОВЩИК: EAST WEST ENGINEERING

Изм.	Кол.уч.	Лист	№ док.	Подп.	Дата
ГИП		Кирпичников			10.26
Нач.отдела		Каршиев			10.26
Разраб.		Мамешов			10.26
Проверил		Каршиев			10.26
Н. контр.		Кирпичников			10.26

EWE0426-MGL1-STR-054-DRW-801702-A1

«СТРОИТЕЛЬСТВО НОВЫХ НИТОК (УЧАСТКОВ) ГАЗОПРОВОДОВ «ГАЗЛИ - САРИМОЙ» И «АКЧАЛОК - ГАЗЛИ - НУКУС» ОБЩЕЙ ПРОТЯЖЕННОСТЬЮ НЕ МЕНЕЕ 275 КМ».

ГАЗОПРОВОД "ГАЗЛИ-САРИМОЙ" (54 КМ)

Стадия	Лист	Листов
РД	1	1

Схема расположения фундаментов Фм 1. Схема расположения стоект Ст 1. Схема расположения сеточных панелей

ООО "EAST-WEST Engineering"
г. Ташкент 2026г.

Взам.инв. N | Подп. и дата | Инв.N подл.

Формат А 1