


Фундамент Фм 1

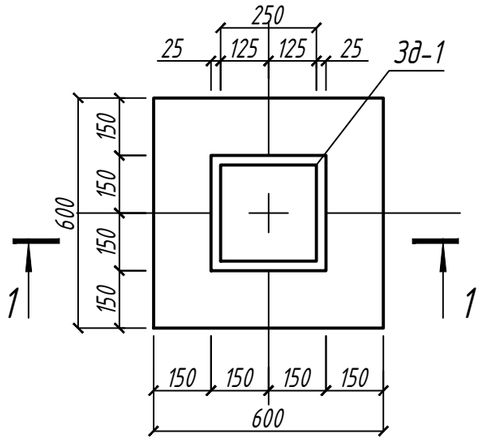


Закладная деталь Зд-1

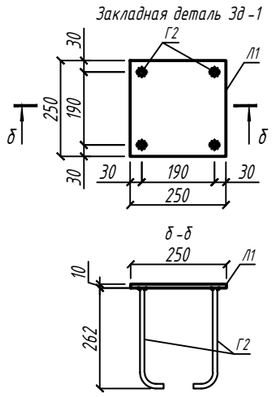


а-а

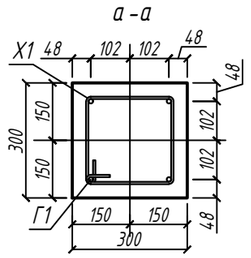




Разрез 1-1

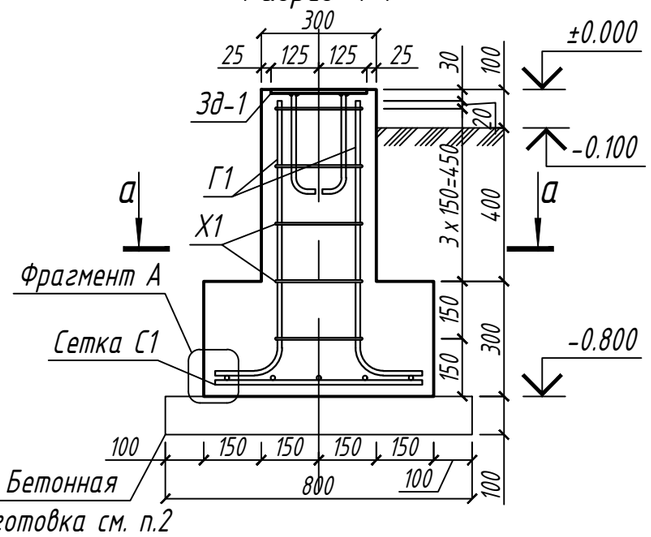

Сетка горизонтальная С 1

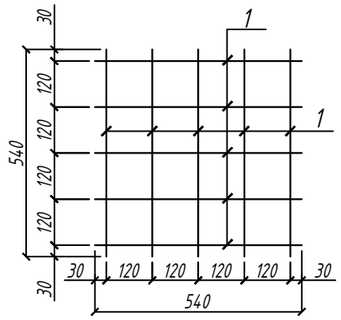

Ведомость деталей

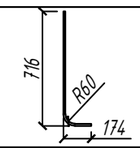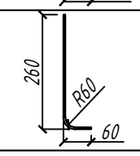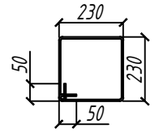Поз.	Эскиз
Г 1	
Г 2	
X 1	

Все размеры даны по внешнем граням детали

Спецификация элементов

Марка Поз.	Обозначение	Наименование		Кол. шт	Масса ед., кг	Прим.
		Фундамент Фм 1 (на 1 шт.)				
		Сборочные единицы				
С 1	см. данный лист	Горизонтальная сетка С 1		1	4.79	4.79
Зд-1	см. данный лист	Закладная деталь Зд-1		1	6.05	6.05
		Детали				
Г 1	см. данный лист	ГОСТ 34028-2016 ⌀12 А400	L=890 мм	4	0.79	3.16
Х 1	см. данный лист	ГОСТ 34028-2016 ⌀6 А240	L=1020 мм	5	0.23	1.13
		Сетка С 1				
1	см. данный лист	ГОСТ 34028-2016 ⌀12 А400	L=540 мм	10	0.48	4.79
		Закладная деталь Зд-1				
Л 1	см. данный лист	ГОСТ 19903-2015 -t10 250x250		1	4.91	4.91
Г 2	см. данный лист	ГОСТ 34028-2016 ⌀12 А400	L=320 мм	4	0.28	1.14
		Материал				
	см. данный лист	ГОСТ 26633-2010 Бетон В 25		0.2		$м^3$
	см. данный лист	ГОСТ 26633-2010 Бетон В 7.5		0.1		$м^3$
	см. данный лист	Щебень пропитанный битумом		0.1		$м^3$
	см. данный лист	Гидроизоляция в 2 слоя		2.6		$м^2$

Примечание

1. Общие данные смотреть на листе EWE0426-MGL1-STR-054-COM-801701- А 1
2. Под монолитным фундаментом выполнить подготовку из бетона кл. В 7.5 толщиной 100 мм с уширением на 100 мм в каждую сторону от размеров подошвы фундамента. Под ним выполнить подготовку из щебня, вдавленного в грунт, толщиной 100 мм, с проливкой горячим битумом с выступом за боковые грани бетонной подготовки по 100 мм в каждую сторону.
3. Обмазать поверхность фундамента гидроизоляцией в 2 слоя

Рев.	Дата	Назначение ревизии	Проверил	Утвердил
А1	20.10.26	Выпущено для строительство		
R1	09.26	Выпущено для рассмотрения		

ЗАКАЗЧИК: UTG UZTRANSGAZ | ГЕНЕРАЛЬНЫЙ ПОДРЯДЧИК: UET UZBEKENERGOTAMIR | ПОДРЯДЧИК: PBG Pro Build Generation | ГЕНЕРАЛЬНЫЙ ПРОЕКТИРОВЩИК: EAST WEST ENGINEERING

Изм.	Кол.уч.	Лист	№ док.	Подп.	Дата
ГИП		Кирпичников			10.26
Нач.отдела		Каршиев			10.26
Разраб.		Мамешов			10.26
Проверил		Каршиев			10.26
Н. контр.		Кирпичников			10.26

EWE0426-MGL1-STR-054-DRW-801703-A1

«СТРОИТЕЛЬСТВО НОВЫХ НИТОК (УЧАСТКОВ) ГАЗОПРОВОДОВ «ГАЗЛИ - САРИМОЙ» И «АКЧАЛОК - ГАЗЛИ - НУКУС» ОБЩЕЙ ПРОТЯЖЕННОСТЬЮ НЕ МЕНЕЕ 275 КМ».

ГАЗОПРОВОД "ГАЗЛИ-САРИМОЙ" (54 КМ)

Стадия	Лист	Листов
РД	1	1

Фундамент Фм 1

ООО "EAST-WEST Engineering" г. Ташкент 2026г.

Взам.инв.N | Подп. и дата | Инв.N подл.

Формат А3