

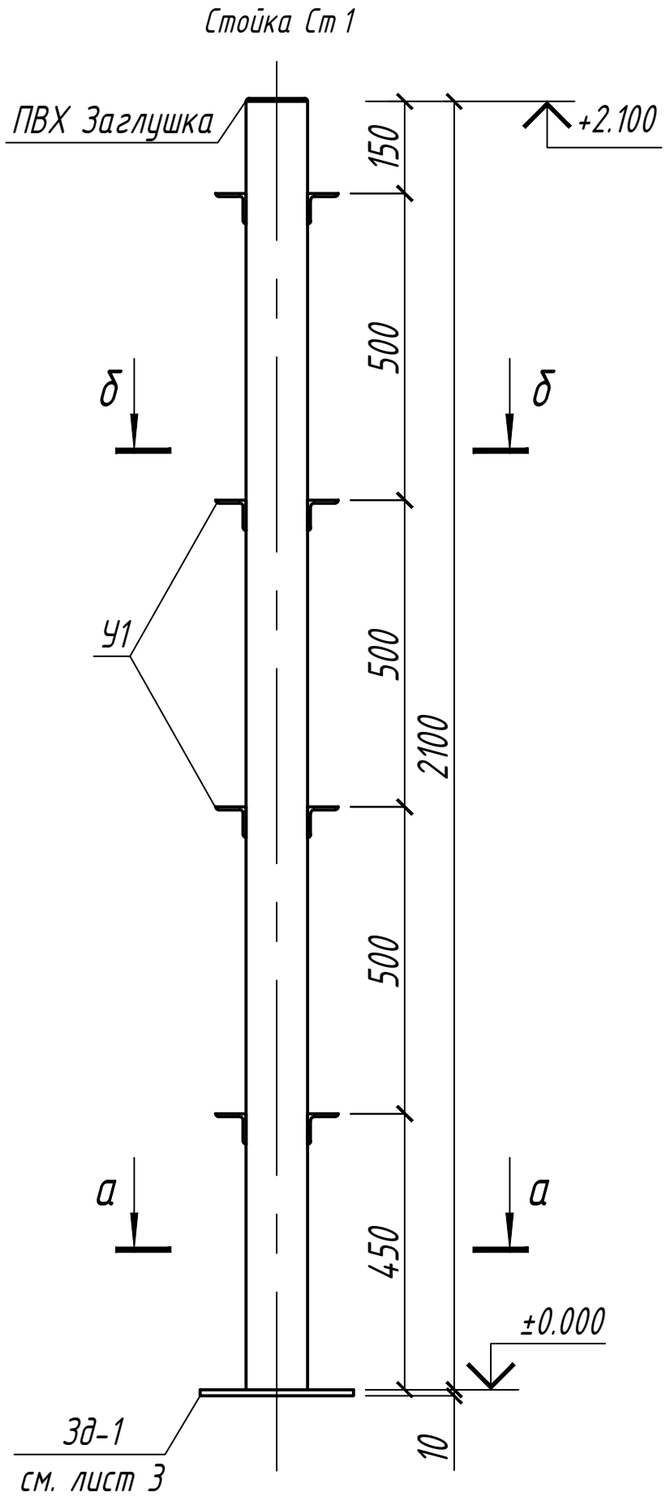


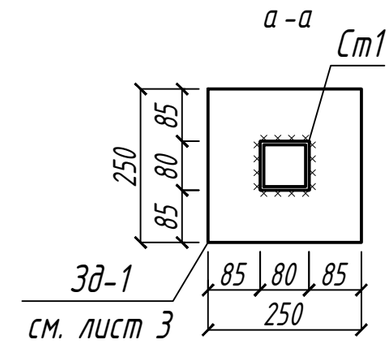

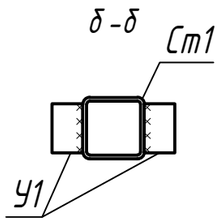

Ведомость элементов

Марка элемента	Сечение			Усилие для прикрепления			Наименование или марка металла	Примечание
	Эскиз	Поз.	Состав	Q, тс	N, тс	M, тс*м		
Ст 1			80х80х4				С255	
У 1			50х50х4				С255	

Спецификация элементов

Марка Поз.	Обозначение	Наименование	Кол. шт	Масса ед., кг	Прим.
		Материал			
		Эмаль ПФ -115 (1 слой)	96.0		$м^2$

Примечание

1. Общие данные смотреть на листе EWE0426-MGL1-STR-054-COM-801701-R1
2. Сварку производить электродами типа Э42А по ГОСТ 9467-75. Высоту швов принять равной наименьшей толщине свариваемых элементов, длину - по длине примыкания. Длину шва выполнять по всей длине свариваемых элементов.
3. Все металлические конструкции окрасить эмалью ПФ -115 ГОСТ 6465-76 за два раза по грунтовке ГФ -021 ГОСТ 25129-82 за один раз

Рев.	Дата	Назначение ревизии	Проверил	Утвердил
A1	20.10.26	Выпущено для строительство		
R1	09.26	Выпущено для рассмотрения		

ЗАКАЗЧИК: UTG UZTRANSGAZ | ГЕНЕРАЛЬНЫЙ ПОДРЯДЧИК: UET UZBEKENERGOTAMIR | ПОДРЯДЧИК: PBG Pro Build Generation | ГЕНЕРАЛЬНЫЙ ПРОЕКТИРОВЩИК: EAST WEST ENGINEERING

Изм.	Кол.уч.	Лист	№ док.	Подп.	Дата			
ГИП		Кирпичников			10.26	EWE0426-MGL1-STR-054-DRW-801704-A1		
Нач.отдела		Каршиев			10.26	«СТРОИТЕЛЬСТВО НОВЫХ НИТОК (УЧАСТКОВ) ГАЗОПРОВОДОВ «ГАЗЛИ - САРИМОЙ» И «АКЧАЛОК - ГАЗЛИ - НУКУС» ОБЩЕЙ ПРОТЯЖЕННОСТЬЮ НЕ МЕНЕЕ 275 КМ».		
Разраб.		Мамешов			10.26	ГАЗОПРОВОД "ГАЗЛИ-САРИМОЙ" (54 КМ)	Стадия: РД	Лист: 1 / Листов: 1
Проверил		Каршиев			10.26	Стойка Ст 1	EAST WEST ENGINEERING	ООО "EAST-WEST Engineering" г. Ташкент 2026г.
Н. контр.		Кирпичников			10.26			

Взам.инв.N | Подп. и дата | Инв.N подл.

Формат А3