Панель П1

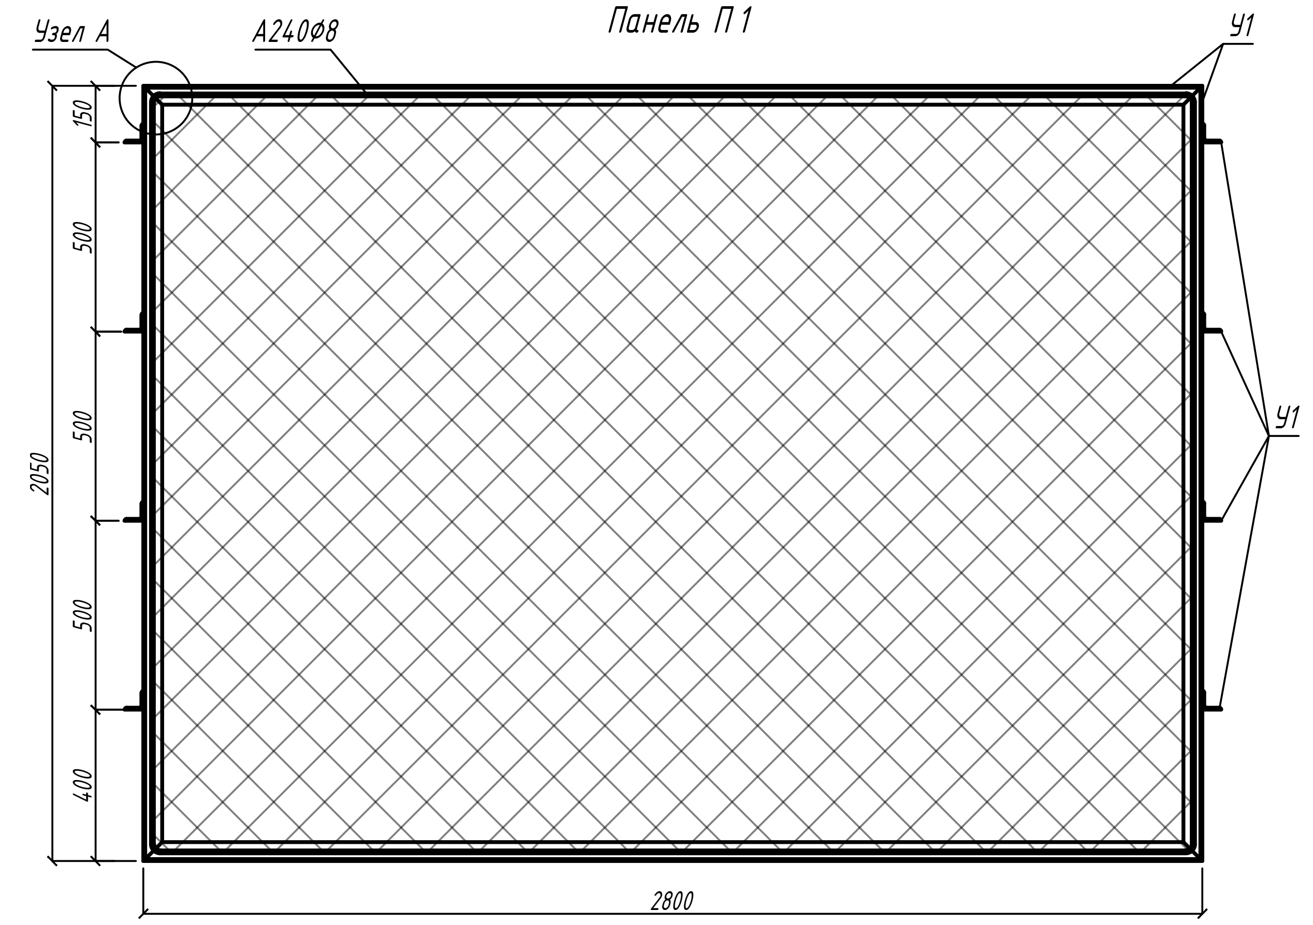
Узел А
А240Ф8
У1
У1
150
500
500
500
400
2050
2800

Панель П4

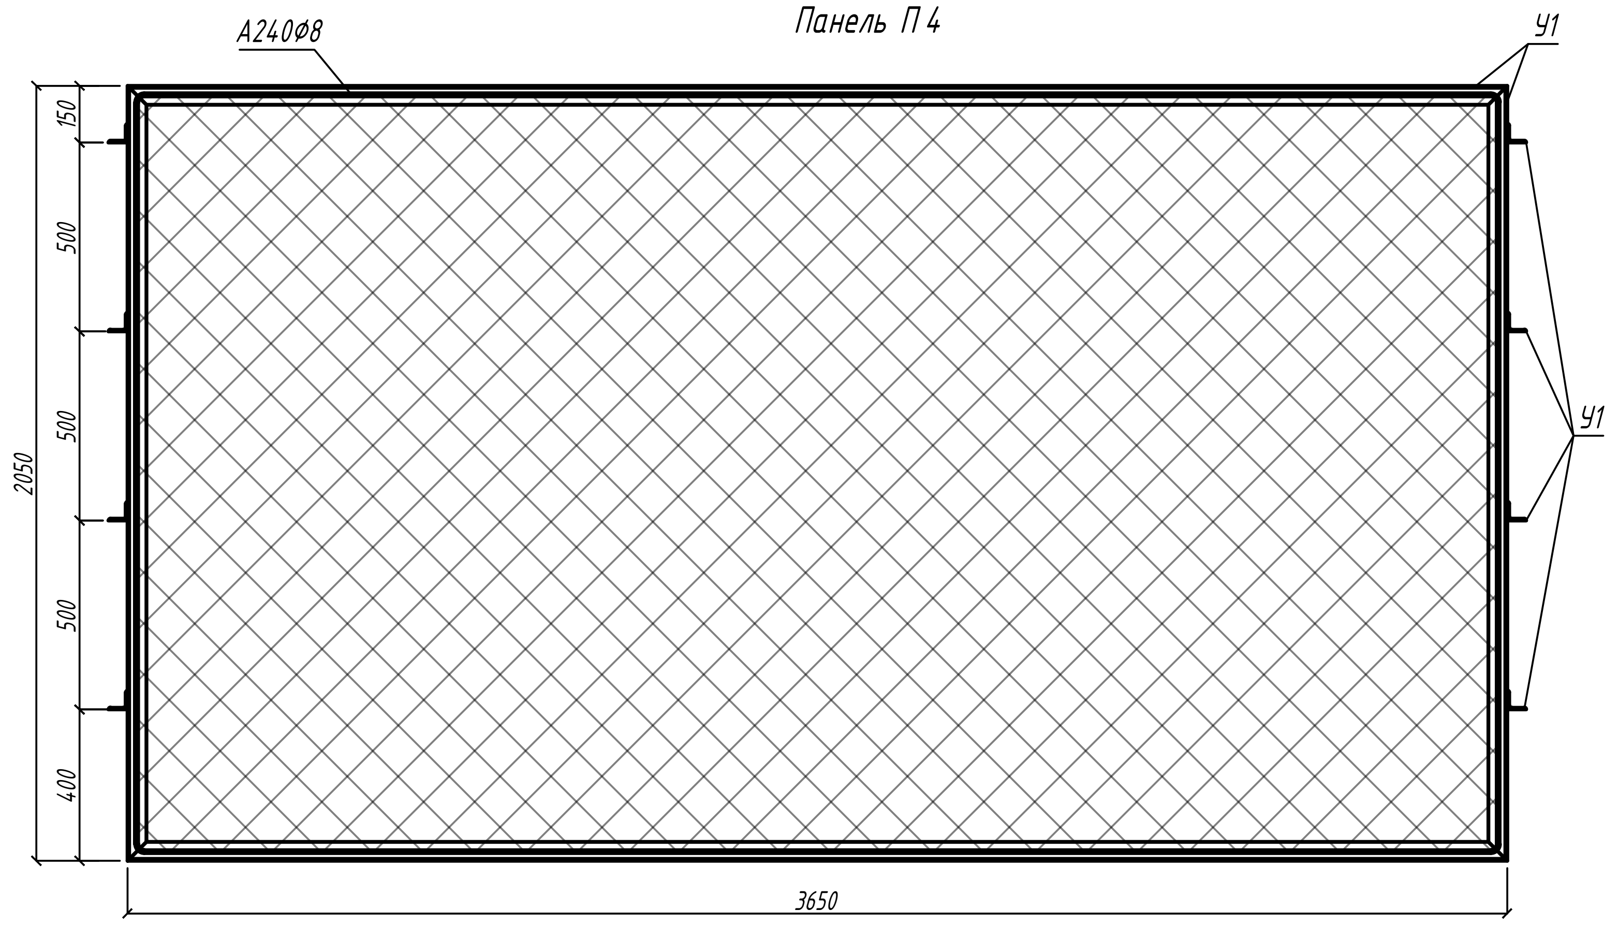
А240Ф8
У1
У1
150
500
500
500
400
2050
3650

Панель П2

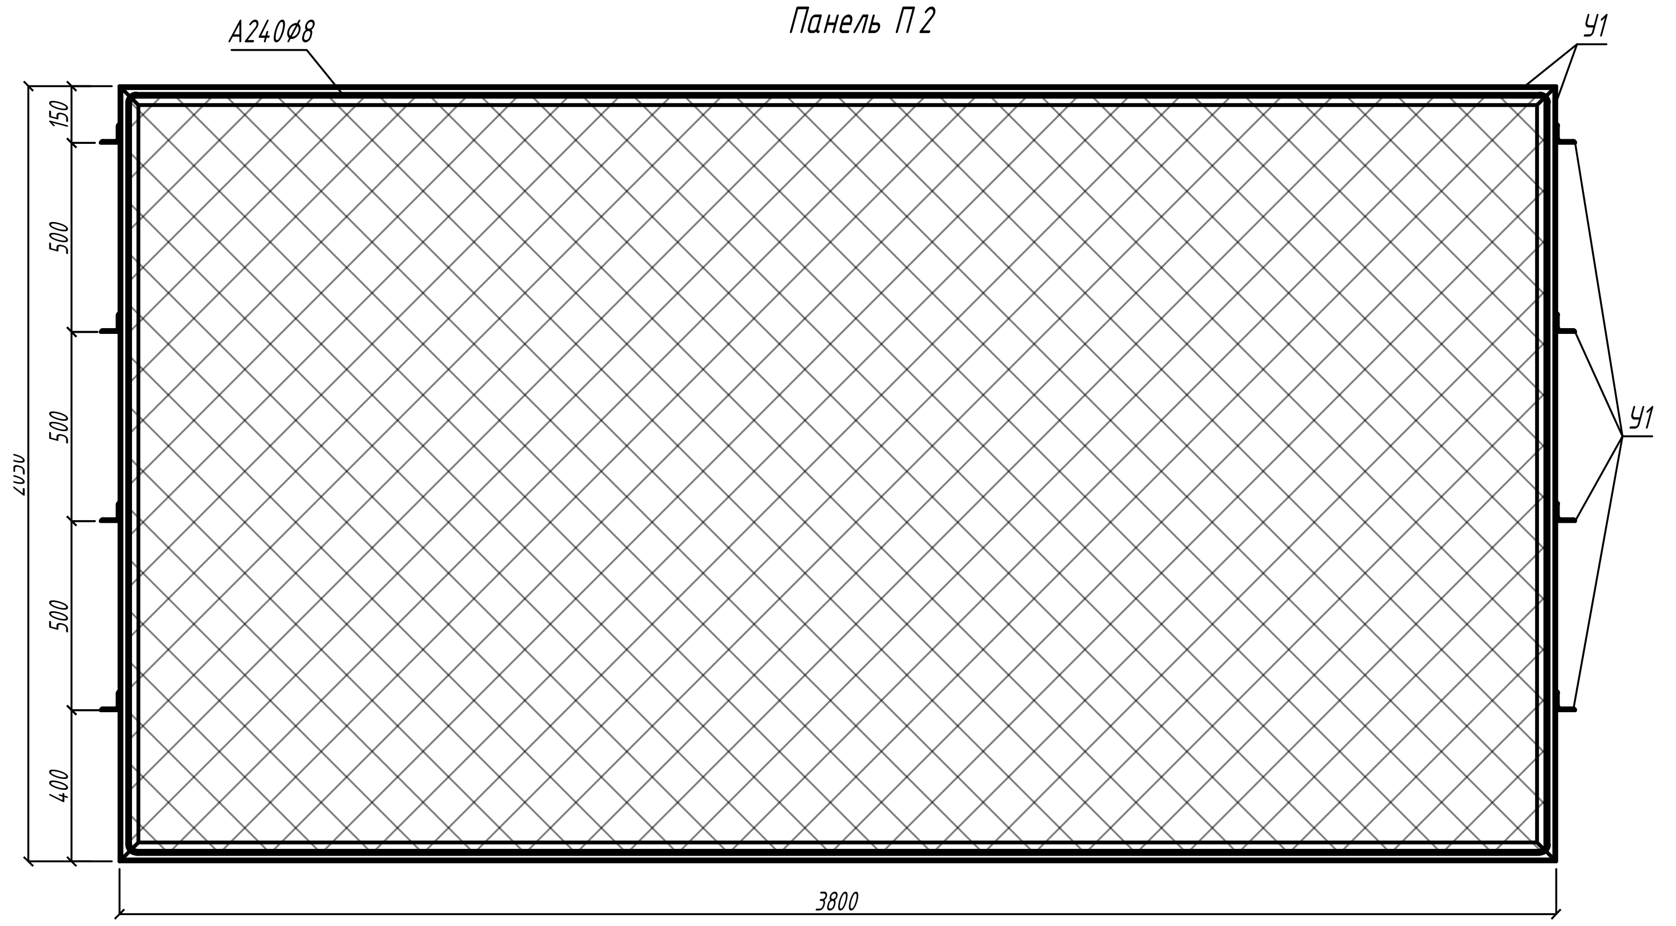
А240Ф8
У1
У1
150
500
500
500
400
2050
3800

Панель П5
(ворота)

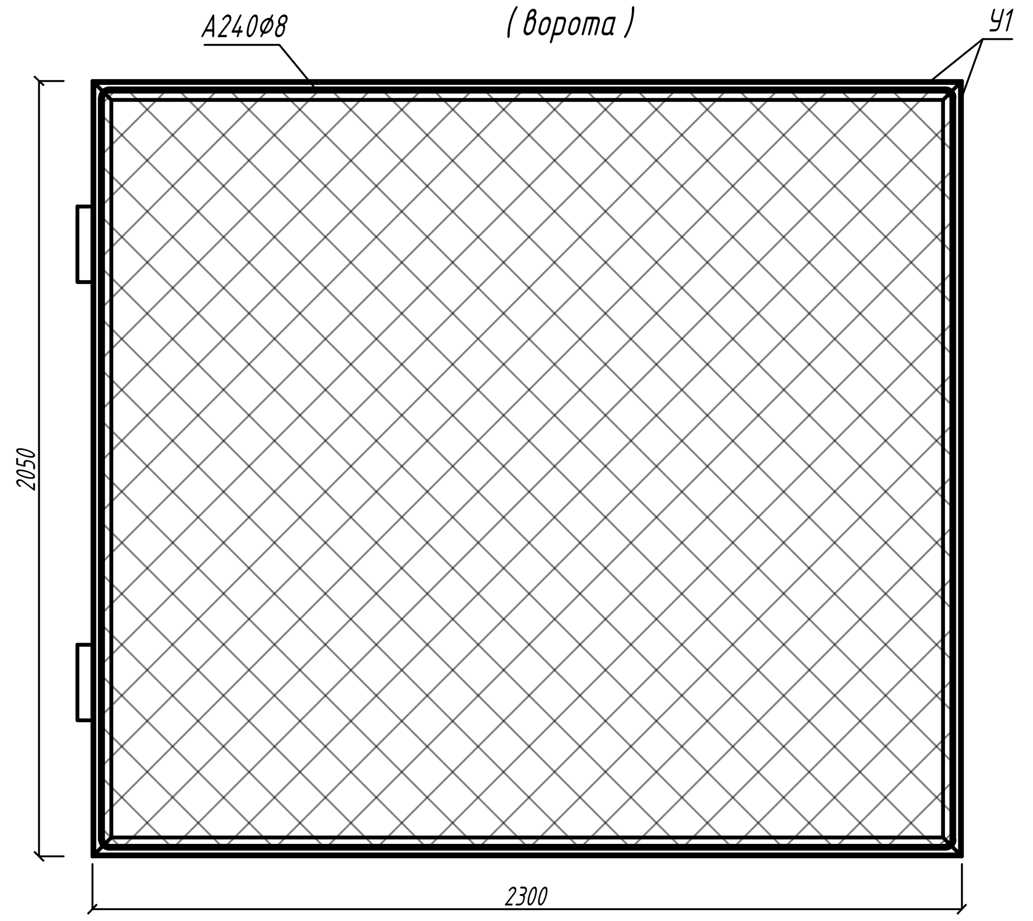
А240Ф8
У1
2050
2300

Панель П3

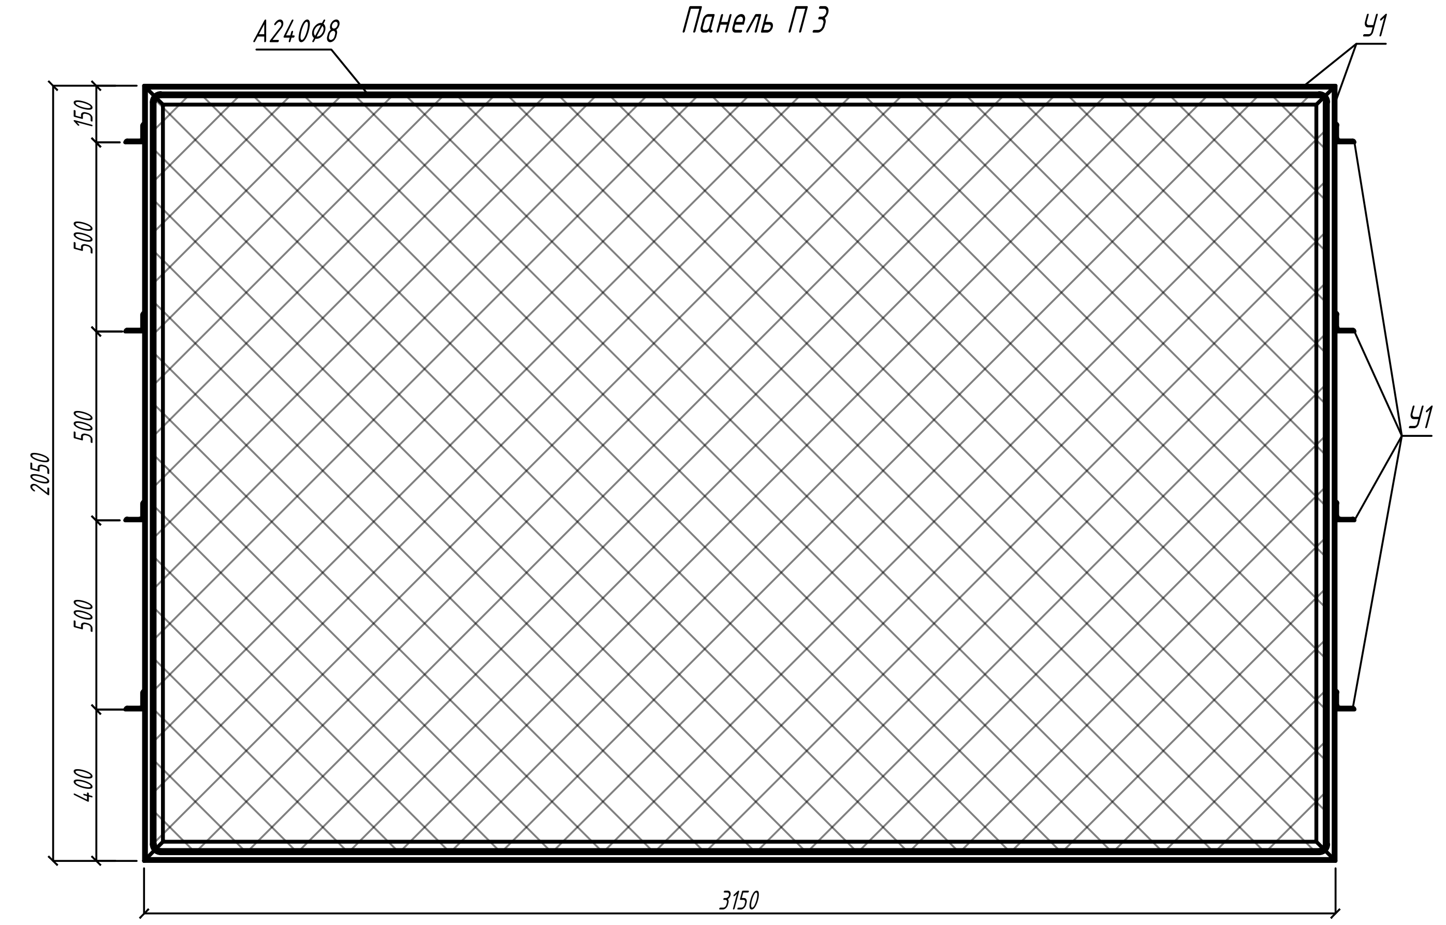
А240Ф8
У1
У1
150
500
500
500
400
2050
3150

Узел А

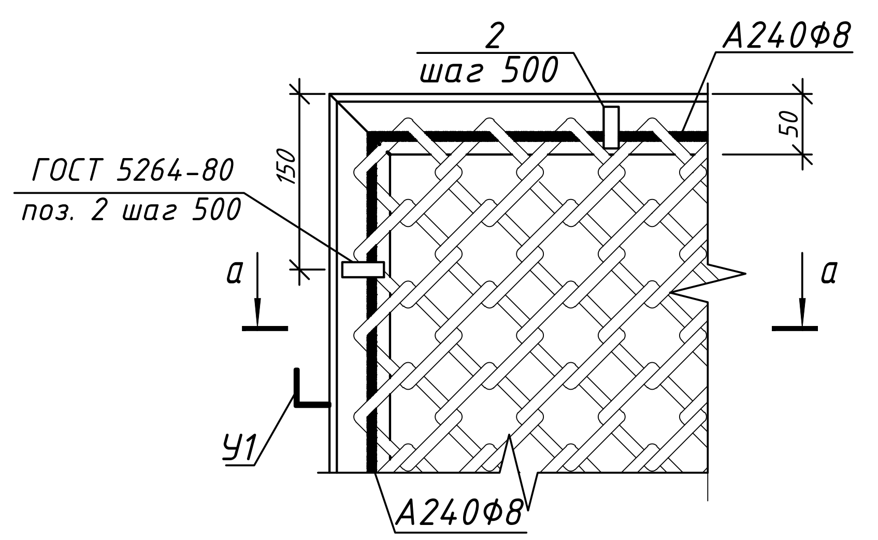
2
шаг 500
А240Ф8
ГОСТ 5264-80
поз. 2 шаг 500
150
50
а
а
У1
А240Ф8

а-а

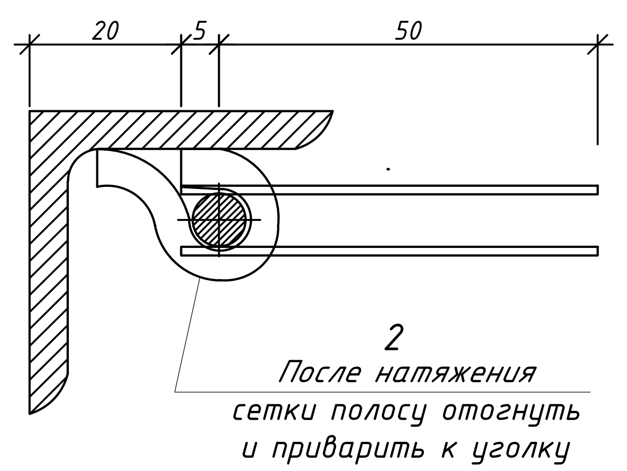
20
5
50
2
После натяжения
сетки полосу отогнуть
и приварить к уголку

Ведомость элементов

Марка элемента	Сечение			Усилие для прикрепления			Наименование или марка металла	Примечание
	Эскиз	Поз.	Состав	Q, тс	N, тс	M, тс*м		
У1			50х50х4				С255	
2	(bxh) 50 x 30		-t4				С255	

Спецификация элементов

Марка Поз.	Обозначение	Наименование		Кол. шт	Масса ед., кг	Прим.
		Детали				
	см. данный лист	ГОСТ 34028-2016 Ф8 А240	L=1000 мм	1359	0.39	535.97

Спецификация металлопроката

Наименование профиля ГОСТ, ТУ	Наименование или марка металла ГОСТ, ТУ	Обозначение и размер профиля, мм	N п.п.	Масса металла по элементам конструкций, т			Общая масса, т
				Стойки	Ограждение	Прочее	
1	2	3	4	5	6	7	8
Гнутые замкнутые сварные профили квадратного сечения	С 255 ГОСТ 30245-2012	80 x 4	1	2.68			2.68
			2				
Всего профиля			3	2.680			2.68
Уголки стальные горячекатаные равнополочные ГОСТ 8509-93	С 255 ГОСТ 27772-2015	∟ 50 x 4	4	2.67	4.15		6.82
Всего профиля			5	2.67	4.15		6.82
Прокат листовой горячекатаный ГОСТ 19903-2015	С 255 ГОСТ 27772-2015	-t4	6	0.12			
Всего профиля			7	0.12			
Всего масса			8	5.47	4.15		9.62

Примечание

1. Общие данные смотреть на листе EWE0426-MGL1-STR-054-COM-801701-R1
2. Сварку производить электродами типа Э42А по ГОСТ 9467-75. Высоту швов принять равной наименьшей толщине свариваемых элементов, длину - по длине примыкания. Длину шва выполнять по всей длине свариваемых элементов.

Рев.	Дата	Назначение ревизии	Проверил	Утвердил
A1	20.10.26	Выпущено для строительство		
R1	09.26	Выпущено для рассмотрения		

ЗАКАЗЧИК: UTG UZTRANSGAZ

ГЕНЕРАЛЬНЫЙ ПОДРЯДЧИК: UET UZBEKENERGOTAMIR

ПОДРЯДЧИК: PBG Pro Build Generation

ГЕНЕРАЛЬНЫЙ ПРОЕКТИРОВЩИК: EAST WEST ENGINEERING

EWE0426-MGL1-STR-054-DRW-801705-A1

«СТРОИТЕЛЬСТВО НОВЫХ НИТОК (УЧАСТКОВ) ГАЗОПРОВОДОВ «ГАЗЛИ - САРИМОЙ» И «АКЧАЛОК - ГАЗЛИ - НУКУС» ОБЩЕЙ ПРОТЯЖЕННОСТЬЮ НЕ МЕНЕЕ 275 КМ».

Изм.	Кол.уч.	Лист	№ док.	Подп.	Дата
ГИП		Кирпичников			10.26
Нач.отдела		Каршиев			10.26
Разраб.		Мамешов			10.26
Проверил		Каршиев			10.26
Н. контр.		Кирпичников			10.26

ГАЗОПРОВОД "ГАЗЛИ-САРИМОЙ" (54 КМ)

Стадия	Лист	Листов
РД	1	1

Сеточная панель П1, П2, П3, П4, П5

EAST WEST ENGINEERING
ООО "EAST-WEST Engineering"
г. Ташкент 2026г.

Формат А3х3

Взам. инв. N

Подп. и дата

Инв. N подл.