

Операторная. План этажа на отм.±0,000.
М 1:50

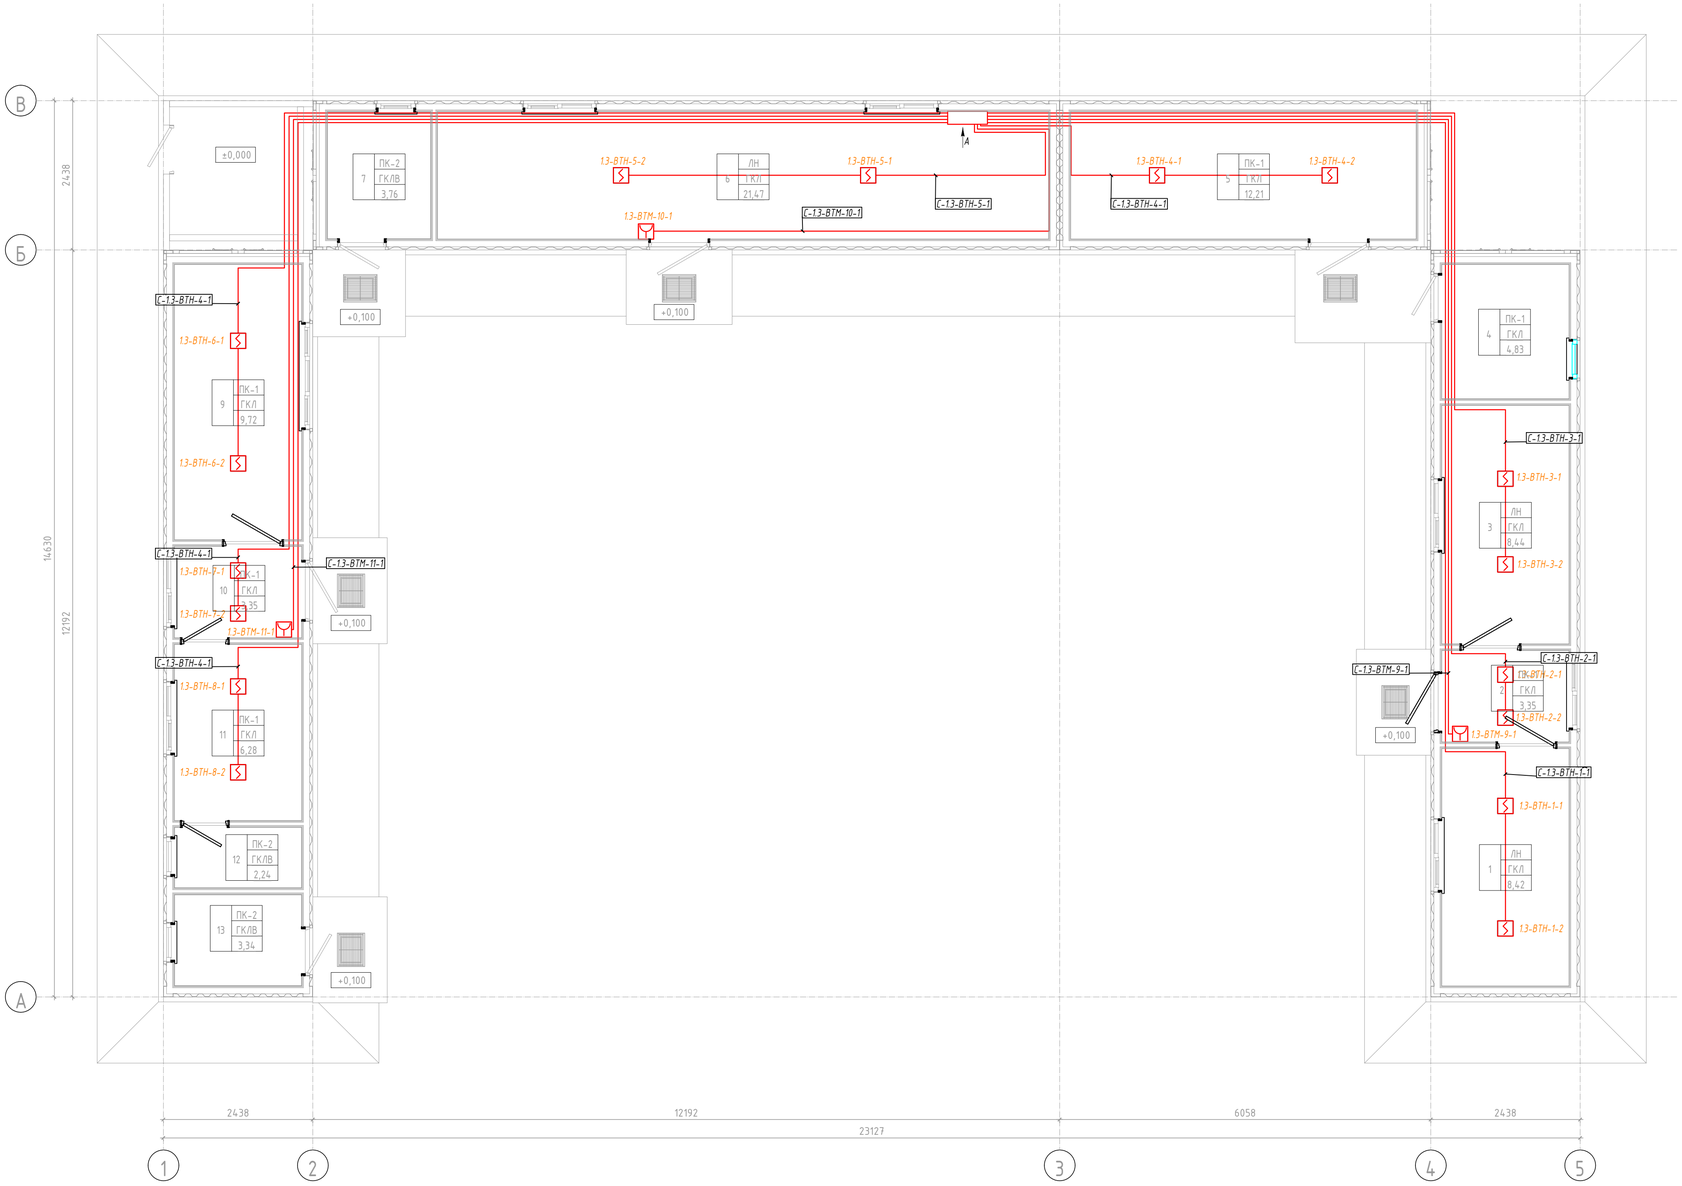

Экспликация помещений

№	Наименования	Площадь	Кат. помещения
1	Кабинет ведущего инженера	8.10 м²	?
2	Тамбур	3.13 м²	?
3	Кабинет инженера химика	8.14 м²	?
4	Кладовая	4.60 м²	?
5	Электрощитовая	5.84 м²	?
6	Кабинет операторов	20.94 м²	?
7	Душ	3.54 м²	–
8	Насосная	4.36 м²	?
9	Комната отдыха и приема пищи	9.40 м²	–
10	Тамбур	3.13 м²	?
11	Гардероб	6.00 м²	?
12	Душ	2.08 м²	А
13	С/У	3.13 м²	–

Эскиз расположения оборудования СПГО на стене.
А (1:10)

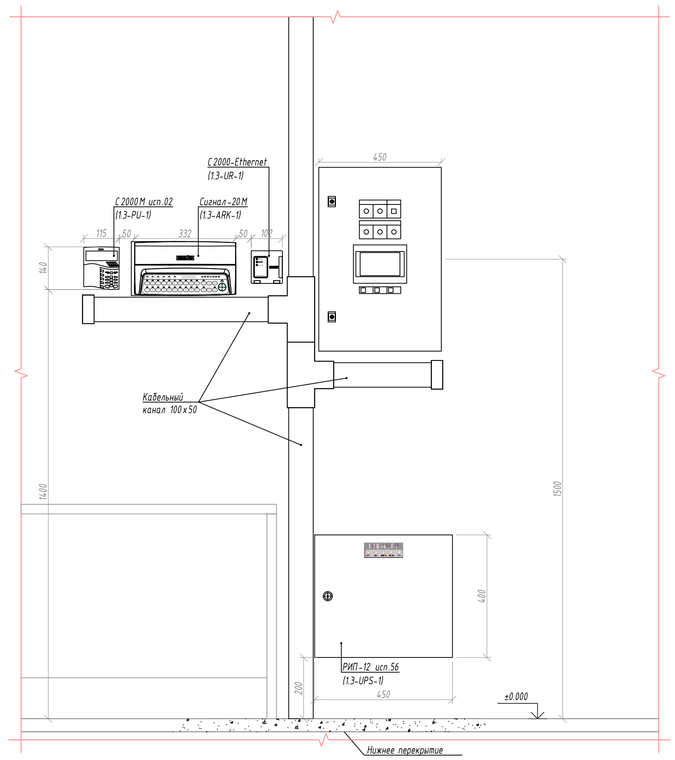

Спецификация

Поз.	Обозначение	Наименование	Кол.	Примечание
1.3-PU-1	С 2000 М исп.02	Пульт контроля и управления охранно-пожарный	1	
1.3-ARK-1	Сигнал-20М	Прибор приёмно-контрольный и управления охранно-пожарный	1	
1.3-UPS-1	РИП-12 исп.56 (РИП-12-6/80М3-Р-RS)	Резервированный источник питания	1	
1.3-UR-1	С 2000-ETHERNET	Преобразователь интерфейсов RS-485/RS-232 в Ethernet	1	
1.3-ВТН-Х-Х	ДИП-31	Извещатель пожарный дымовой оптико-электронный пороговый	12	
1.3-ВТМ-Х-Х	ИПР 513-3М	Извещатель пожарный ручной электроконтактный	3	
1.3-BIALS-Х-Х	ОПОП 124-7, 12В	Оповещатель охранно-пожарный свето-звуковой	3	
1.3-SC-1	УК-ВК исп.12	Устройство коммутационное	1	
1.3-JB-1	Ecoplast JBS210 (43066HF)	Коробка огнестойкая Е60-Е90	1	

Условные обозначения

№ п/п	Обозначение графич.	Обозначение букв.	Наименование
1		1.3-SC-1	Устройство коммутационное
2		1.3-ВТН-Х	Извещатель пожарный дымовой оптико-электронный пороговый
3		1.3-ВТМ-Х	Извещатель пожарный ручной
4		1.3-BIALS-Х	Оповещатель охранно-пожарный комбинированный свето-звуковой
5		1.3-JB-1	Коробка соединительная
		ШС	Кабельная линия ШС
		12VDC	Кабельная линия 12В
		RS-485	Кабельная линия RS-485

Структура буквенно-цифровой части обозначения извещателей и оповещателей

XX - ВТН - Х - Х
- № извещателя в ШС
- №ШС
- Буквенное обозначение типа извещателя
- №ПКОП согласно №здания по ГП

Структура буквенно-цифровой части обозначения прочего оборудования

XX - ARK - Х
- Порядковый номер оборудования
- Буквенное обозначение типа оборудования
- Место установки оборудования (номер здания по ГП)

Структура буквенно-цифровой части обозначения трассы ШС

XX-ВТН-Х-Х / XX-ВТН-Х-Х
- Конец трассы
- Начало трассы

Изм.	Кол.уч.	Лист	№док.	Подпись	Дата
R1					05.08.2026
Рев.		Дата	Назначение ревизии		Проверил / Утвердил

ЗАКАЗЧИК: UTG INTERNATIONAL
ГЕНЕРАЛЬНЫЙ ПОДРЯДЧИК: UET
ПОДРЯДЧИК: PBG
ГЕНЕРАЛЬНЫЙ ПРОЕКТИРОВЩИК: EAST WEST ENGINEERING

EWE0426-MGL1-FFA-054-DRW-801403-R1

«СТРОИТЕЛЬСТВО НОВЫХ НИТОК (УЧАСТКОВ) ГАЗОПРОВОДОВ «ГАЗЛИ – САРИМОЙ» И «АКЧАЛОК – ГАЗЛИ – НУКУС» ОБЩЕЙ ПРОТЯЖЕННОСТЬЮ НЕ МЕНЕЕ 275 КМ»

ГАЗОПРОВОД «ГАЗЛИ-САРИМОЙ» (54 КМ) УЗРГ-D001

Стадия	Лист	Листов
РД	1	3

План расположения оборудования и кабельных трасс


ГИП	Скабицкий А.		08.2026
Нач.отд.	Кабулова Е.		08.2026
Испол.	Гальцев В.		08.2026
Н.контр.	Скабицкий А.		08.2026

ООО "EAST-WEST Engineering"
г. Ташкент 2026г.

Взам. инв.№ | Подпись и дата | Инв.№ подл.

Формат А1


Операторная. План этажа на отм.±0,000.
М 1:50

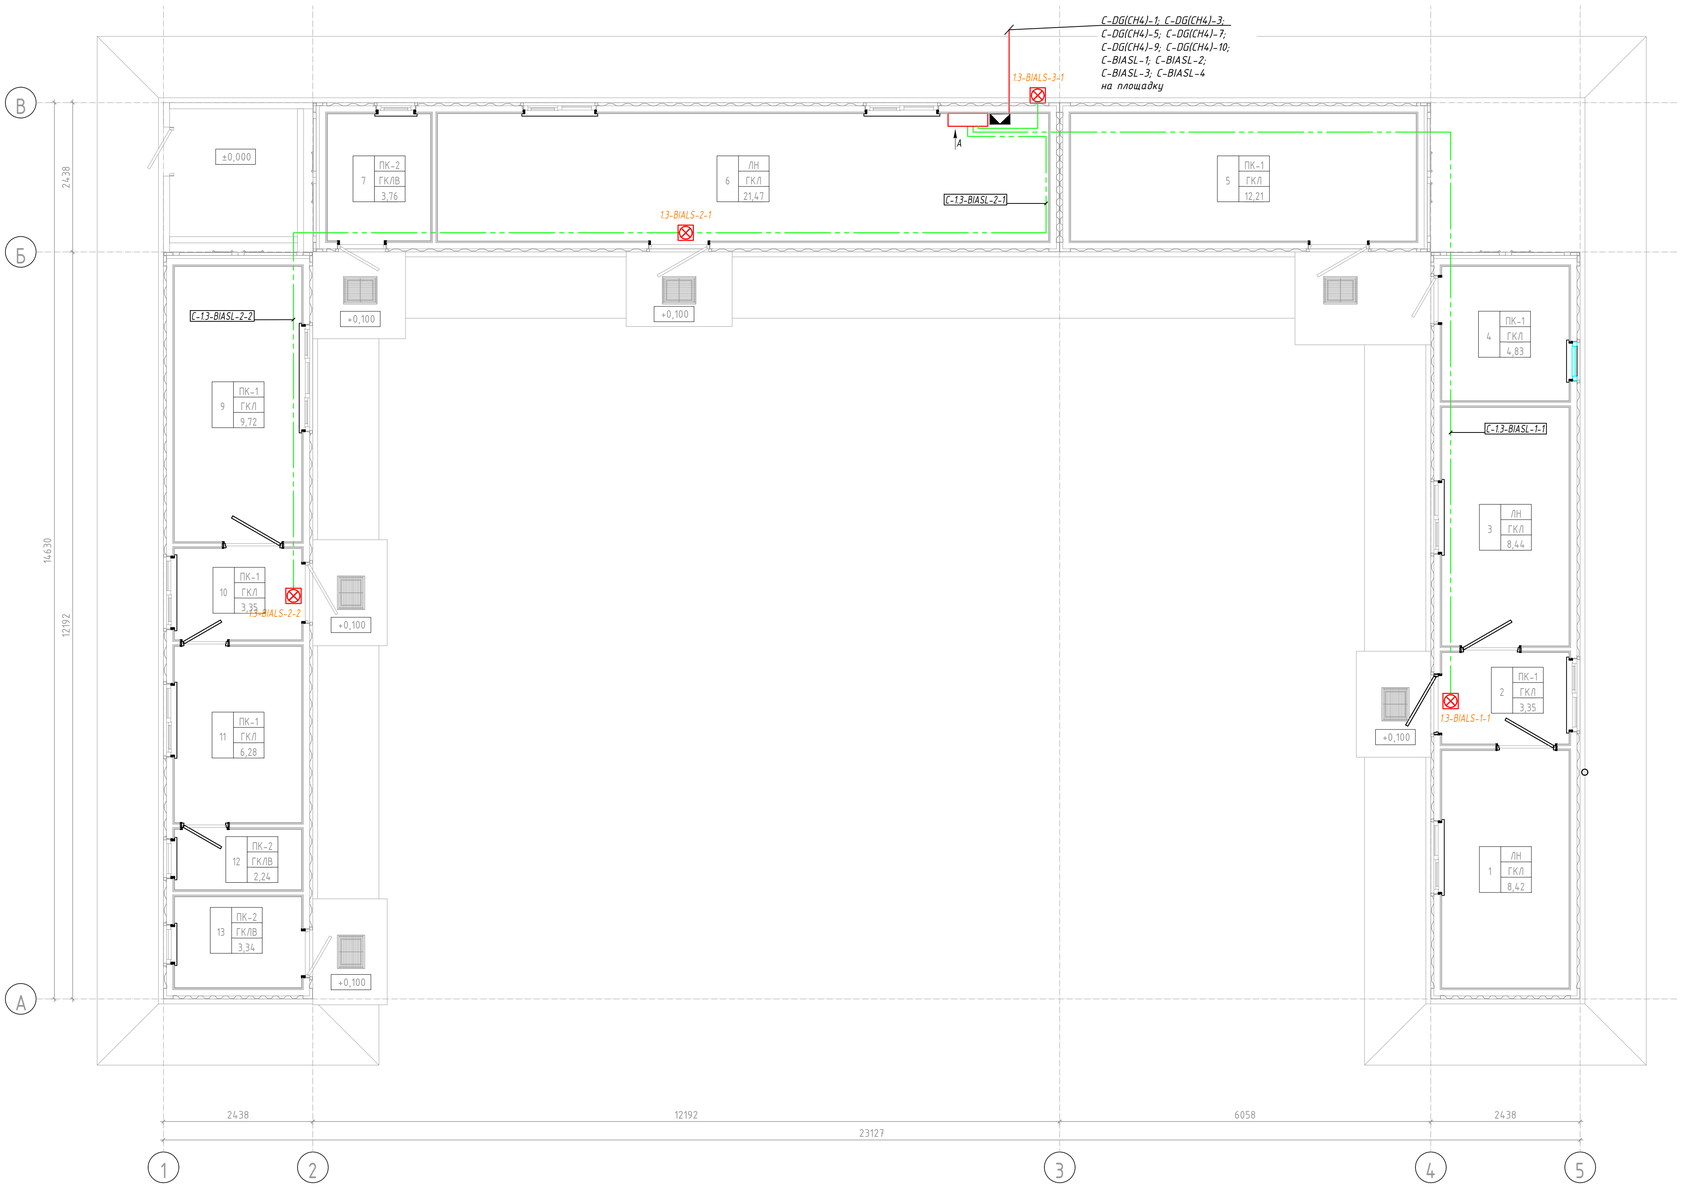

Экспликация помещений

№	Наименования	Площадь	Кат. помещения
1	Кабинет ведущего инженера	8.10 м²	?
2	Тамбур	3.13 м²	?
3	Кабинет инженера химика	8.14 м²	?
4	Кладовая	4.60 м²	?
5	Электрощитовая	5.84 м²	?
6	Кабинет операторов	20.94 м²	?
7	Душ	3.54 м²	–
8	Насосная	4.36 м²	?
9	Комната отдыха и приема пищи	9.40 м²	–
10	Тамбур	3.13 м²	?
11	Гардероб	6.00 м²	?
12	Душ	2.08 м²	А
13	С/У	3.13 м²	–

Эскиз расположения оборудования СПГО на стене.
А (1:10)

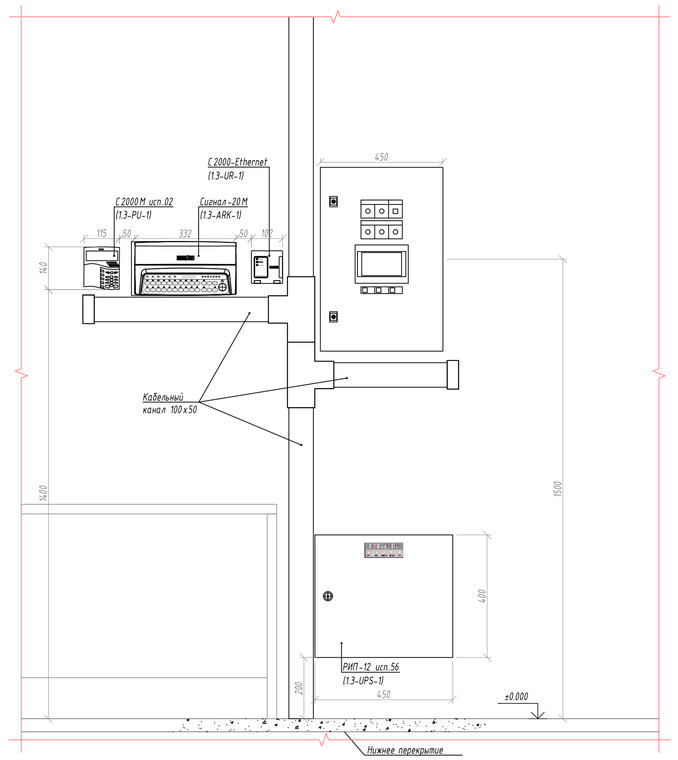

Спецификация

Поз.	Обозначение	Наименование	Кол.	Примечание
1.3-PU-1	С 2000М исп.02	Пульт контроля и управления охранно-пожарный	1	
1.3-ARK-1	Сигнал-20М	Прибор приёмно-контрольный и управления охранно-пожарный	1	
1.3-UPS-1	РИП-12 исп.56 (РИП-12-6/80М3-Р-RS)	Резервированный источник питания	1	
1.3-UR-1	С 2000-ETHERNET	Преобразователь интерфейсов RS-485/RS-232 в Ethernet	1	
1.3-ВТН-Х-Х	ДИП-31	Извещатель пожарный дымовой оптико-электронный пороговый	12	
1.3-ВТМ-Х-Х	ИПР 513-3М	Извещатель пожарный ручной электроконтактный	3	
1.3-BIALS-Х-Х	ОПОП 124-7, 12В	Оповещатель охранно-пожарный свето-звуковой	3	
1.3-SC-1	УК-ВК исп.12	Устройство коммутационное	1	
1.3-JB-1	Ecoplast JBS210 (43066HF)	Коробка огнестойкая Е60-Е90	1	

Условные обозначения

№ п/п	Обозначение графич.	Обозначение букв.	Наименование
1		1.3-SC-1	Устройство коммутационное
2		1.3-ВТН-Х	Извещатель пожарный дымовой оптико-электронный пороговый
3		1.3-ВТМ-Х	Извещатель пожарный ручной
4		1.3-BIALS-Х	Оповещатель охранно-пожарный комбинированный свето-звуковой
5		1.3-JB-1	Коробка соединительная
		ШС	Кабельная линия ШС
		12VDC	Кабельная линия 12В
		RS-485	Кабельная линия RS-485

Структура буквенно-цифровой части обозначения извещателей и оповещателей

XX-ВТН-Х-Х
- XX — № ППКОП согласно № здания по ГП
- ВТН — Буквенное обозначение типа извещателя
- Х — № ШС
- Х — № извещателя в ШС

Структура буквенно-цифровой части обозначения прочего оборудования

XX-ARK-Х
- XX — Место установки оборудования (номер здания по ГП)
- ARK — Буквенное обозначение типа оборудования
- Х — Порядковый номер оборудования

Структура буквенно-цифровой части обозначения трассы ШС


XX-ВТН-Х-Х / XX-ВТН-Х-Х
- XX-ВТН-Х-Х — Начало трассы
- XX-ВТН-Х-Х — Конец трассы

Взам. инв. N | Подп. и дата | Инв. N подл.

Изм.	Кол.	Лист	№док.	Подпись	Дата	EWE0426-MGL1-FFA-054-DRW-801403-R1	Лист 2

Формат А1


Площадка УЭРГ.
М 1:250

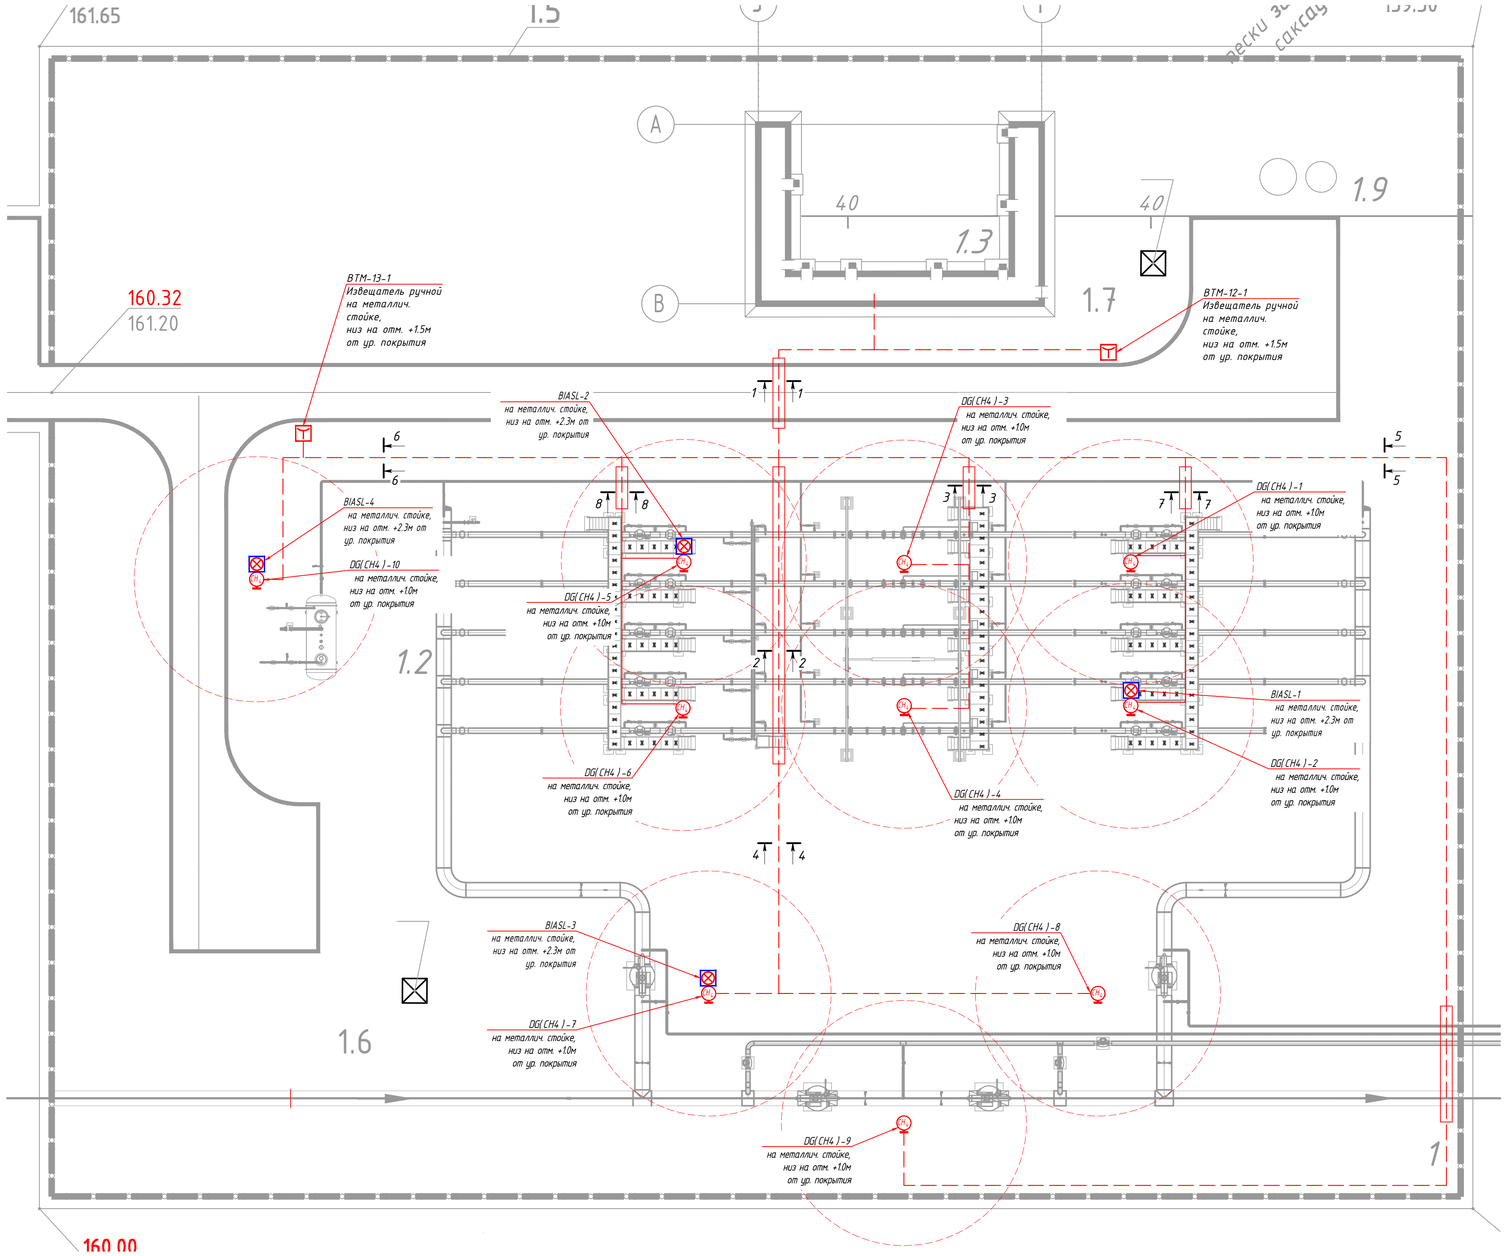


Экспликация зданий и сооружений

Номер на плане	Наименование	Примечание
1	Площадка УЭРГ	
1.1	Блок качества газа	
1.2	Площадка дренажной емкости V=25м3	
1.3	Операторная	
1.4	Продувочные свечи	
1.5	Сетчатое ограждение с воротами шир.4.5 м	
1.6	Прожекторная мачта ПМЖ-22.8	
1.7	Прожекторная мачта ПМЖ-22.8	
1.8	Молниеотвод МЖ-24.3	
1.9	Выгреб	


5-5 (1:20)

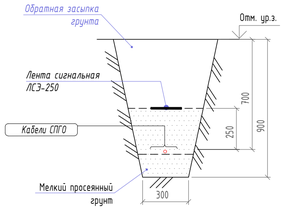


6-6 (1:20)

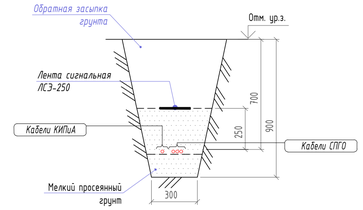

7-7 (1:20)

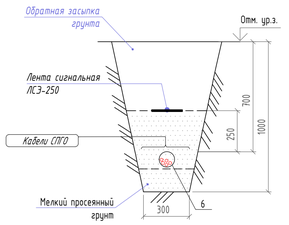


8-8 (1:20)

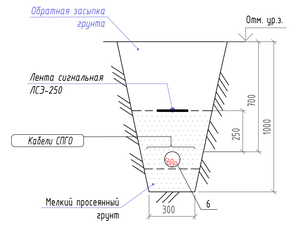


Условные обозначения

№ п/п	Обозначение		Наименование
	Графич.	Букв.	
1		13-SC-1	Устройство коммутационное
2		DGI(CH4)-X	Извещатель пожарный дымовой оптико-электронный пороговый
3		BTM-X	Извещатель пожарный ручной
4		BIALS-X	Оповещатель охранно-пожарный комбинированный свето-звуковой
		ШС	Кабельная линия ШС
		12VDC	Кабельная линия 12В
		RS-485	Кабельная линия RS-485


1-1 (1:20)

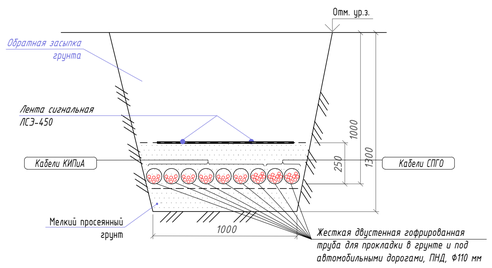


2-2 (1:20)

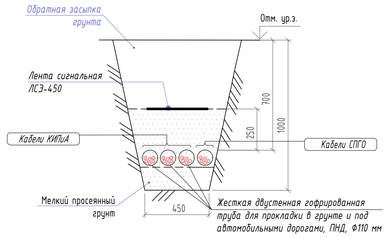

3-3 (1:20)

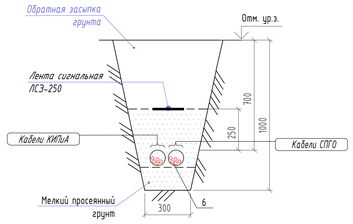

4-4 (1:20)

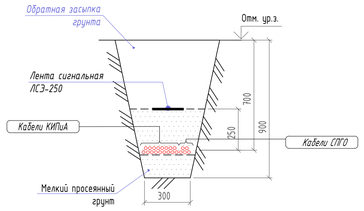

1. Оборудование установить на стойках предусмотренных в чертеже EWE0426-MGL1-FFA-054-SCM-801505

Изм.	Кол.	Лист	№док.	Подпись	Дата	EWE0426-MGL1-FFA-054-DRW-801403-R1	Лист 3

Взам. инв. N | Подп. и дата | Инв. N подл.

Формат А1