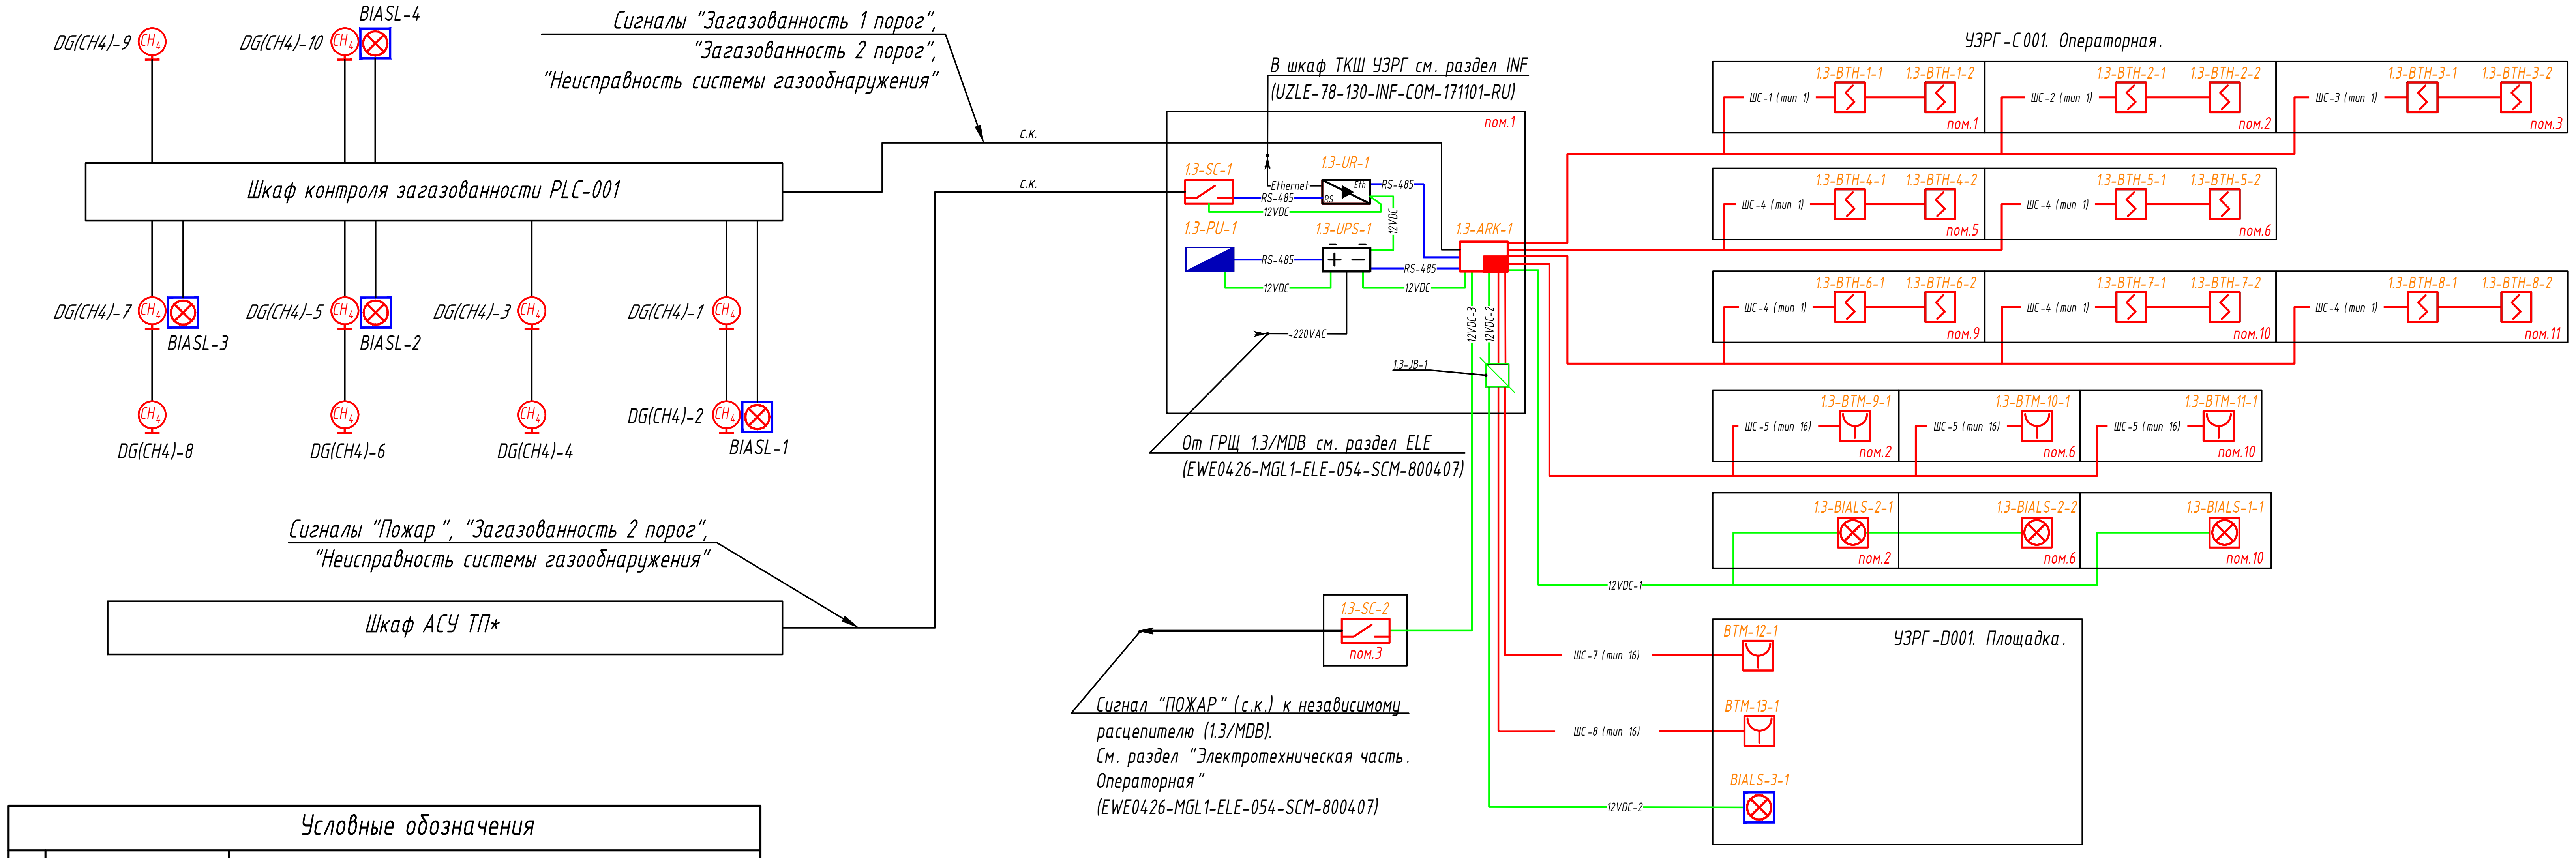

Структура буквенно-цифровой
части обозначения прочего оборудования

XX - ARK - X
- X — Порядковый номер оборудования
- ARK — Буквенное обозначение типа оборудования
- XX — Место установки оборудования (номер здания по ГП)

Структура буквенно-цифровой
части обозначения извещателей и оповещателей

XX- BTH - X - X
- X — № извещателя в ШС
- X — № ШС
- BTH — Буквенное обозначение типа извещателя
- XX — № ППКОП согласно № здания по ГП

Условные обозначения

№ п/п	Обозначение		Наименование
	Графич.	Букв.	
1	◪	1.3-PU-1	Пульт контроля и управления охранно-пожарный
2	▣	1.3-ARK-1	Прибор приёмно-контрольный охранно-пожарный
3	+ –	1.3-UPS-1	Источник питания 12В
4	RS Eth	1.3-UR-1	Преобразователь интерфейсов RS-485/RS-232 в Ethernet
5		1.3-SC-2	Устройство коммутационное
6		1.3-SC-1	Блок сигнально пусковой
7		1.3-BTH-X	Извещатель пожарный дымовой оптико-электронный пороговый
8		1.3-BTM-X	Извещатель пожарный ручной
9	⊗	1.3-BIALS-X	Оповещатель охранно-пожарный комбинированный свето-звуковой
10	⊗	1.3-BIALS-X	Оповещатель охранно-пожарный комбинированный свето-звуковой взрывозащищенный
11	CH4	DG(CH4)-X	Газоанализатор метана (датчик загазованности)
12	☒	1.3-JB-1	Коробка соединительная
13	—	ШС	Кабельная линия ШС
14	—	12VDC	Кабельная линия 12В
15	—	RS-485	Кабельная линия RS-485

Примечание:

Данный лист читать совместно с листами:

1. План расположения оборудования и кабельных трасс EWE0426-MGL1-FFA-054-DRW-801403
2. Схема электрических соединений EWE0426-MGL1-FFA-054-SCM-801404

* - оборудование не учитываемое данным комплектом чертежей.

Рев.	Дата	Назначение ревизии	Проверил	Утвердил
R1	05.08.2026	Выпущено для рассмотрения		

ЗАКАЗЧИК: UTG UZTRANSGAZ
ГЕНЕРАЛЬНЫЙ ПОДРЯДЧИК: UET UZBEKENERGOTAMIR
ПОДРЯДЧИК: PBG Pro Build Generation
ГЕНЕРАЛЬНЫЙ ПРОЕКТИРОВЩИК: EAST WEST ENGINEERING

EWE0426-MGL1-FFA-054-SCM-801402-R1

«СТРОИТЕЛЬСТВО НОВЫХ НИТОК (УЧАСТКОВ) ГАЗОПРОВОДОВ «ГАЗЛИ - САРИМОЙ» И «АКЧАЛОК - ГАЗЛИ - НУКУС» ОБЩЕЙ ПРОТЯЖЕННОСТЬЮ НЕ МЕНЕЕ 275 КМ»

Изм.	Кол.уч.	Лист	№док.	Подпись	Дата
ГИП		Схабицкий А.			08.2026
Нач.отд.		Кабулова Е.			08.2026
Исполн.		Гальцев В.			08.2026
Н.контр		Схабицкий А.			08.2026

ГАЗОПРОВОД «ГАЗЛИ-САРИМОЙ» (54 КМ)
УЗРГ-D001

Стадия	Лист	Листов
РД	1	1

Структурная схема.

EAST WEST ENGINEERING
ООО "EAST-WEST Engineering"
г. Ташкент 2026г.

Взам. инв. №
Подпись и дата
Инв.№ подл.

Формат А4х3