## Переход №1. Вид I – I

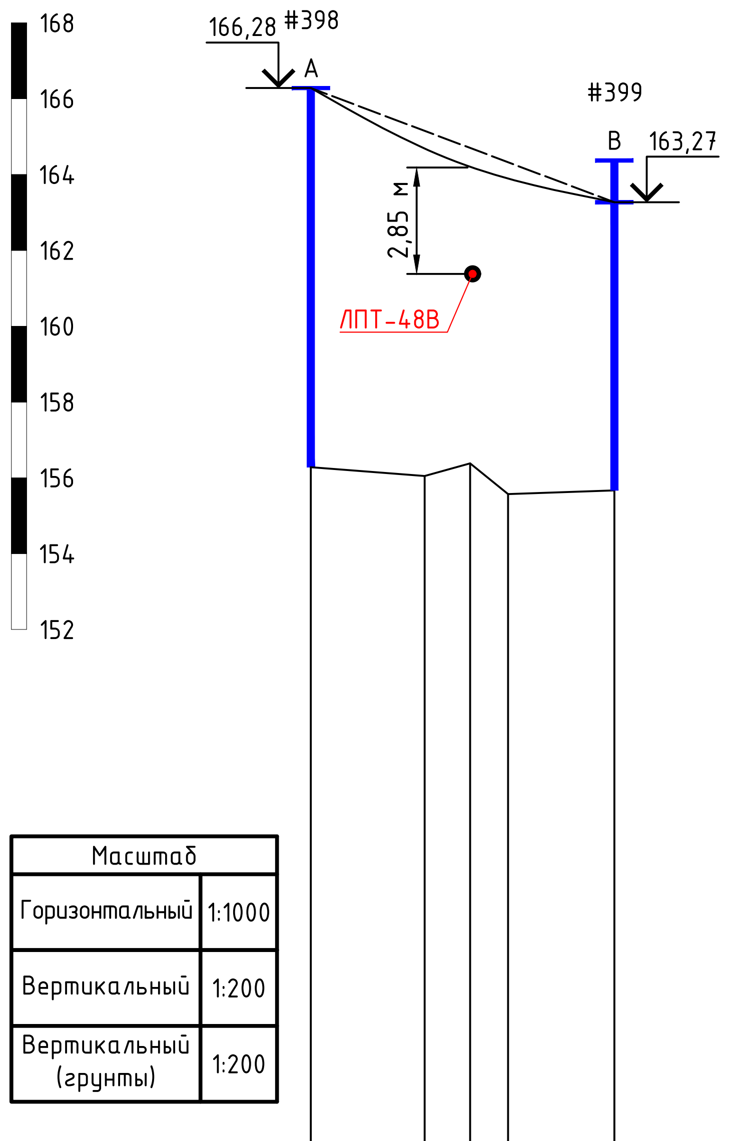

168
166
164
162
160
158
156
154
152
166,28
#398
A
#399
B
163,27
2,85 м
ЛПТ-48В

| Масштаб | |
|---|---|
| Горизонтальный | 1:1000 |
| Вертикальный | 1:200 |
| Вертикальный (грунты) | 1:200 |

| | | | | | |
|---|---|---|---|---|---|
| Отметки профиля | 156.28 | 156.05 | 156.38 | 155.57 | 155.67 |
| Расстояние, м | 15.0 | 6.0 | 5.0 | 14.0 | |
| Пикетаж | | | | | |
| Абрис | 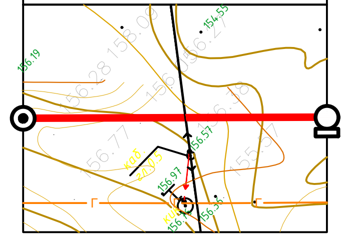 | | | | |

## Переход №2. Вид I – I

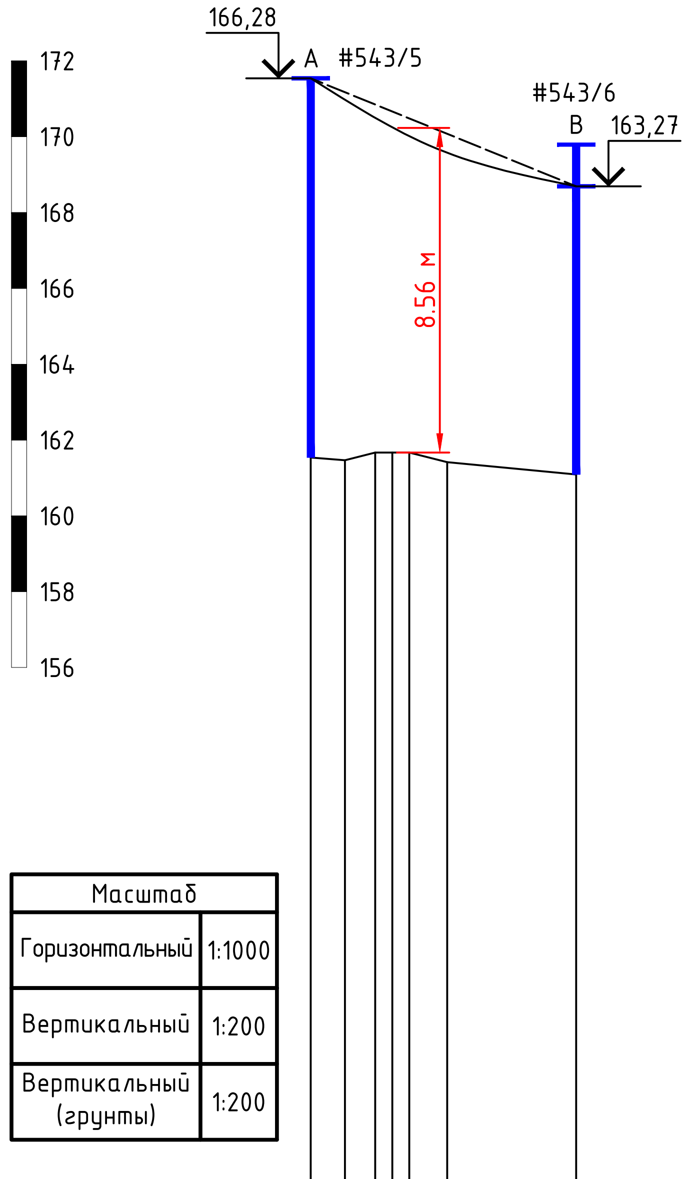

172
170
168
166
164
162
160
158
156
166,28
A
#543/5
#543/6
B
163,27
8.56 м

| Масштаб | |
|---|---|
| Горизонтальный | 1:1000 |
| Вертикальный | 1:200 |
| Вертикальный (грунты) | 1:200 |

| | | | |
|---|---|---|---|
| Отметки профиля | 161.54 | 161.67 | 161.09 |
| Расстояние, м | 35.0 | | |
| Пикетаж | | | |
| Абрис | 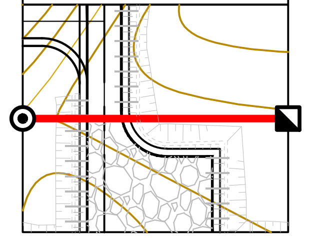 | | |

## Переход №3. Вид I – I

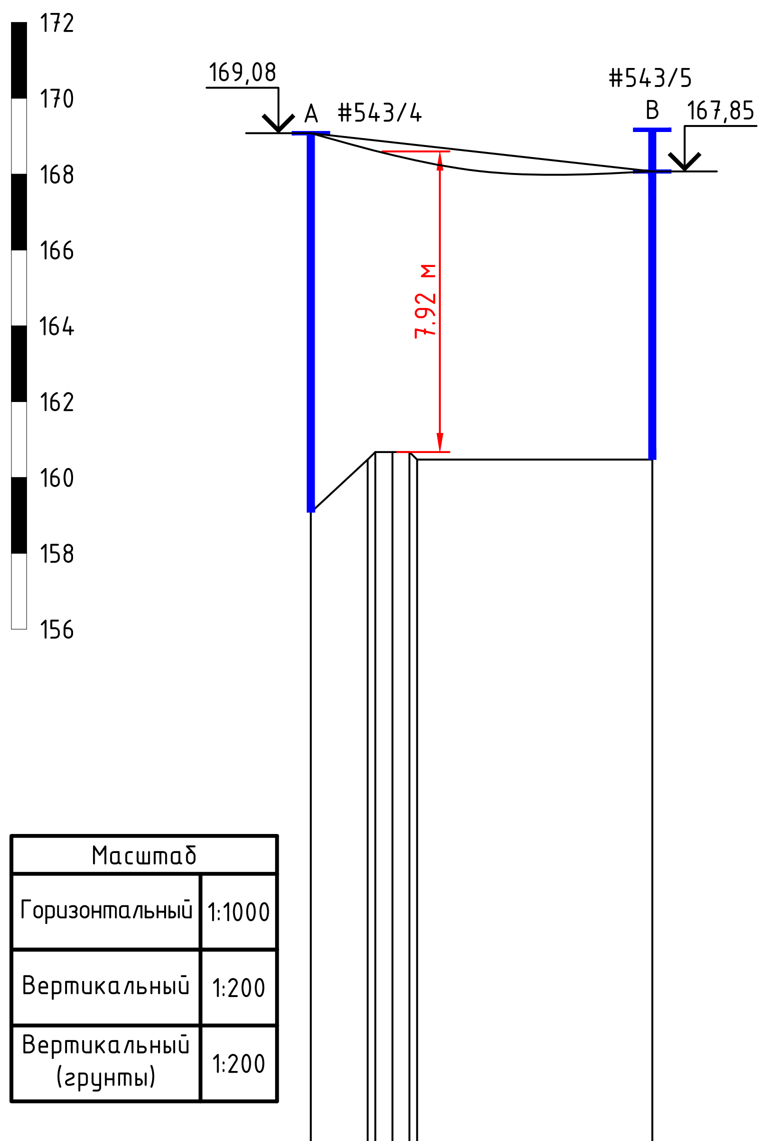

172
170
168
166
164
162
160
158
156
169,08
A
#543/4
#543/5
B
167,85
7.92 м

| Масштаб | |
|---|---|
| Горизонтальный | 1:1000 |
| Вертикальный | 1:200 |
| Вертикальный (грунты) | 1:200 |

| | | | |
|---|---|---|---|
| Отметки профиля | 159.08 | 160.67 | 160.45 |
| Расстояние, м | 45.0 | | |
| Пикетаж | | | |
| Абрис | 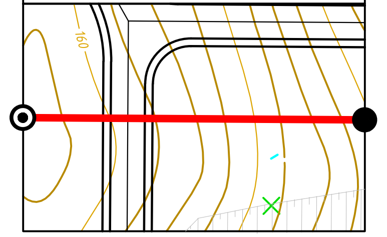 | | |

| Рев. | Дата | Назначение ревизии | Проверил | Утвердил |
|---|---|---|---|---|
| A1 | 14.10.2026 | Утверждено для строительства | | |
| R1 | 24.09.2026 | Выпущено для рассмотрения | | |

ЗАКАЗЧИК: UTG UZTRANSGAZ «TRANSGAZINJINIRING»

ГЕНЕРАЛЬНЫЙ ПОДРЯДЧИК: UET UZBEKENERGOTAMIR

ПОДРЯДЧИК: PBG Pro Build Generation

ГЕНЕРАЛЬНЫЙ ПРОЕКТИРОВЩИК: EAST WEST ENGINEERING

# EWE0426-MGL1-ELE-054-DRW-680204-A1

«СТРОИТЕЛЬСТВО НОВЫХ НИТОК (УЧАСТКОВ) ГАЗОПРОВОДОВ «ГАЗЛИ – САРИМОЙ» И «АКЧАЛОК – ГАЗЛИ – НУКУС» ОБЩЕЙ ПРОТЯЖЕННОСТЬЮ НЕ МЕНЕЕ 275 КМ».

| Изм. | Кол.уч. | Лист | №док. | Подпись | Дата |
|---|---|---|---|---|---|
| ГИП | | Кирпичников С. | | | 10.2026 |
| Провер. | | Гимранов Т. | | | 10.2026 |
| Исполн. | | Озеров В. | | | 10.2026 |
| Н. контр. | | Кирпичников С. | | | 10.2026 |

ГАЗОПРОВОД «ГАЗЛИ-САРИМОЙ» (54 КМ)

| Стадия | Лист | Листов |
|---|---|---|
| РД | 1 | 1 |

Профили переходов ВЛ через автодороги

EAST WEST ENGINEERING

ООО "EAST-WEST Engineering"
г. Ташкент 2026г.