Однолинейная схема проектируемой ВЛ-6 кВ ЭХЗ

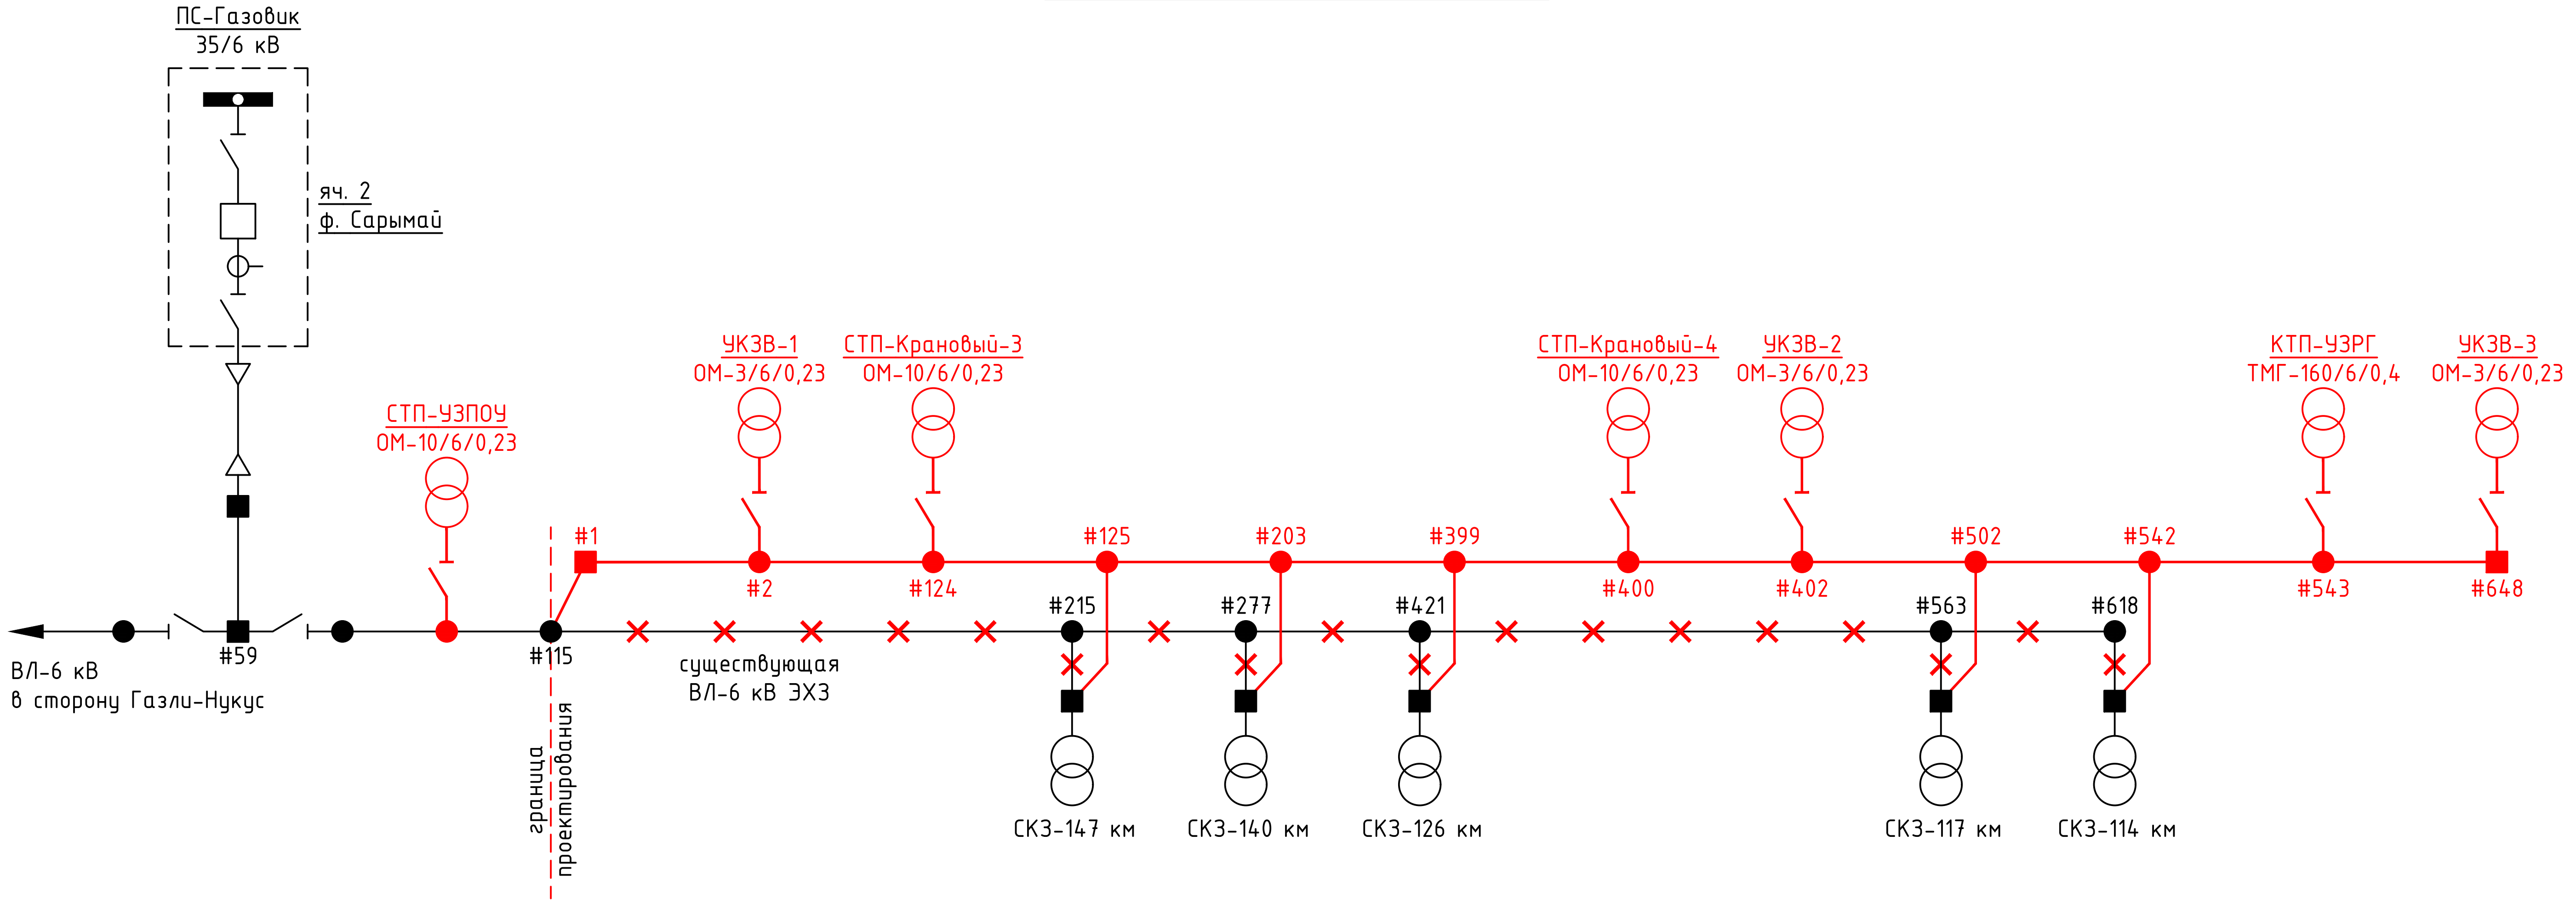

Рев.	Дата	Назначение ревизии	Проверил	Утвердил
A1	14.10.2026	Выпущено для рассмотрения		
R1	24.09.2026	Выпущено для рассмотрения		

ЗАКАЗЧИК: UZTRANSGAZ «TRANSGAZINJINIRING»
ГЕНЕРАЛЬНЫЙ ПОДРЯДЧИК: UZBEKENERGOTAMIR
ПОДРЯДЧИК: PBG Pro Build Generation
ГЕНЕРАЛЬНЫЙ ПРОЕКТИРОВЩИК: EAST WEST ENGINEERING

EWE0426-MGL1-ELE-054-DRW-680205-A1

«СТРОИТЕЛЬСТВО НОВЫХ НИТОК (УЧАСТКОВ) ГАЗОПРОВОДОВ «ГАЗЛИ – САРИМОЙ» И «АКЧАЛОК – ГАЗЛИ – НУКУС» ОБЩЕЙ ПРОТЯЖЕННОСТЬЮ НЕ МЕНЕЕ 275 КМ».

Изм.	Кол.уч.	Лист	№док.	Подпись	Дата
ГИП		Кирпичников С.			10.2026
Провер.		Гимранов Т.			10.2026
Исполн.		Озеров В.			10.2026
Н. контр.		Кирпичников С.			10.2026

ГАЗОПРОВОД «ГАЗЛИ-САРИМОЙ» (54 КМ)

Стадия	Лист	Листов
РД	1	1

Однолинейная схема проектируемой ВЛ

ООО "EAST-WEST Engineering"
г. Ташкент 2026г.