


Фундамент ФОМ1
Вид сверху. М 1:25

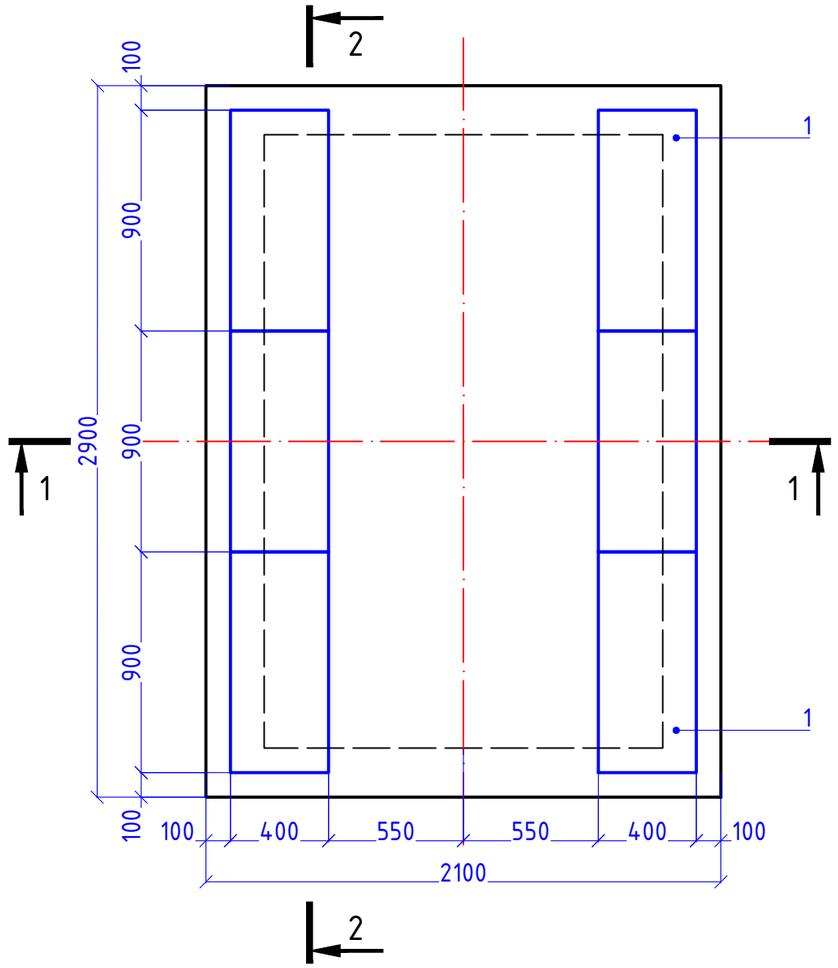

1 – 1. М 1:25

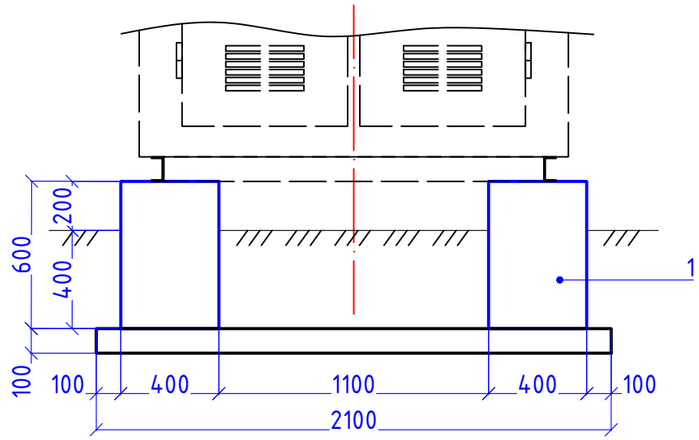

2 – 2. М 1:25

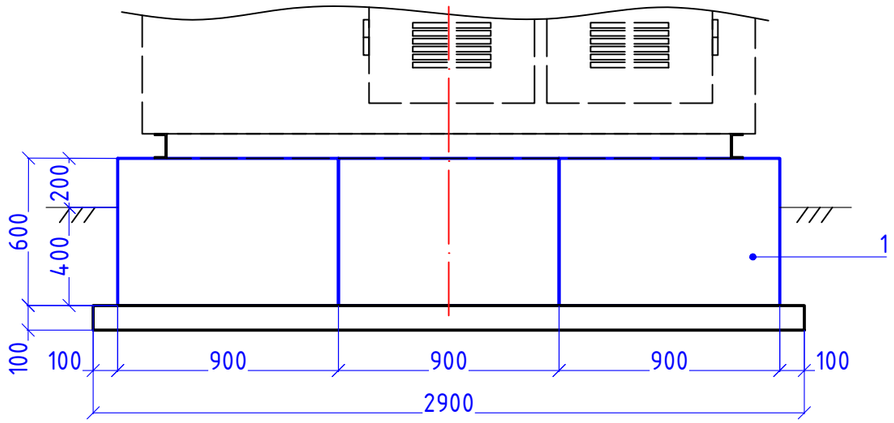

Спецификация элементов

№ п.п	Обозначение	Наименование	Ед. изм.	Кол-во	Масса кг	Примечание
		Заводские изделия				
1	ГОСТ 13579-2018	ФБС 9.4.6-Т	шт	6		
		Материалы				
2		Подготовка из бетона В7,5	$м^3$	0,6		
4	ГОСТ 28778-90	Распорный болт М16х150	шт	4	0.192	
4		Гидроизоляция фундамента	$м^2$	12,8		

1. Антикоррозионную защиту боковых поверхностей железобетонных конструкций, соприкасающихся с грунтом, а также верха бетонной подготовки выполнить путем нанесения двух слоев полимерного покрытия на основе лака ХП-734 в два слоя по ГОСТ 52165-2003 толщиной 25 мкм.
2. Крепление оборудования к ФБС выполнить с помощью болтов типа БСР М16х150.

Рев.	Дата	Назначение ревизии	Проверил	Утвердил
A1	14.10.2026	Утверждено для строительства		
R1	24.09.2026	Выпущено для рассмотрения		

ЗАКАЗЧИК: UTG UZTRANSGAZ | ГЕНЕРАЛЬНЫЙ ПОДРЯДЧИК: UET UZBEKENERGOTAMIR | ПОДРЯДЧИК: PBG Pro Build Generation | ГЕНЕРАЛЬНЫЙ ПРОЕКТИРОВЩИК: EAST WEST ENGINEERING

EWE0426-MGL1-ELE-054-DRW-680213-A1

«СТРОИТЕЛЬСТВО НОВЫХ НИТОК (УЧАСТКОВ) ГАЗОПРОВОДОВ «ГАЗЛИ – САРИМОЙ» И «АКЧАЛОК – ГАЗЛИ – НУКУС» ОБЩЕЙ ПРОТЯЖЕННОСТЬЮ НЕ МЕНЕЕ 275 КМ».

Изм.	Кол.уч.	Лист	№док.	Подпись	Дата
ГИП		Кирпичников С.			10.2026
Провер.		Гимранов Т.			10.2026
Исполн.		Озеров В.			10.2026
Н. контр.		Кирпичников С.			10.2026

ГАЗОПРОВОД «ГАЗЛИ-САРИМОЙ» (54 КМ)

Стадия	Лист	Листов
РД	1	1

Фундамент под КТПКм.
Виды. Спецификация

ООО "EAST-WEST Engineering"
г. Ташкент 2026г.