Поз.	Опросные параметры	Параметр
1	Тип подстанции	КТПКм
2	Количество КТП, шт	1
3	Мощность силового трансформатора, кВА	160
4	Класс напряжения ВН, кВ	6.3
5	Сочетание вводов ВН-НН	ВН-В(воздушный), НН-К(кабельный)
6	Узел установки разъединителя 6 кВ в комплекте	нет
7	Защита от перенапряжений, ВН	ОПН-6/6.3/2-УХЛ1
8	Защита от перенапряжений, НН	ОПН-П-0,4/0,45 УХЛ1
9	Тип силового трансформатора	ТМГ
10	Схема соединений обмоток трансформатора	Δ/Yн-11
11	Трансформатор в комплекте поставки КТПКм	да
12	Обмотки трансформатора	Медные
13	Трансформаторное масло	Ингибиторного типа
14	Учет электроэнергии 0,4кВ	да
15	Счетчик трансформаторного включения	да
16	Трансформатор тока	ТОП-0,66 250/5, 0.5S
17	Измерение тока и напряжения	да
18	АСКУЭ	да
19	Наличие блока управления освещением	нет
20	Поддон под аварийный слив масла	да
21	Климатическое исполнение и степень защиты	УХЛ1, IP54
22	Навесные замки	да
23	Габаритные размеры (ДхШхВ), мм	1800x1600x4500*


Окраска всех элементов КТП, нанесение корпоративных, информационных надписей и знаков безопасности КТП выполняется в соответствии с ПУЭ и внутренними регламентами Заказчика. Корпоративные и информационные знаки должны наноситься таким образом, чтобы не затруднять восприятие друг друга

(*) Размеры ориентировочные, уточняются у завода-изготовителя

(**) Разъединитель QS1 устанавливается на отдельно стоящей опоре (опора с разъединителем учтены спецификацией оборудования основного объема проекта)

Обозначение на схеме	Наименование электроаппарата	Марка, характеристики
QS1**	Разъединитель трехполюсный наружной установки с заземляющими ножами	не комплектно с КТП
FV1...FV3	Ограничитель перенапряжения высоковольтный на напряжение 6 кВ	ОПН-6/6.3/2-УХЛ1
FU1...FU3	Предохранитель высоковольтный трансформаторный	ПКТ-101-6-31.5-20
T	Трансформатор силовой маслонаполненный герметичный	ТМГ-160/6/0,4 кВ УХЛ1
QF1	Выключатель автоматический трехполюсный	ВА-99М ЗР 250/250
FV4...FV6	Ограничитель перенапряжения низковольтный на напряжение 0,4 кВ	ОПН-П-0,4/0,45У1
PV	Вольтметр 0...500В	Ц42704
PA	Амперметр 0...250А	
PIK	Прибор учета электроэнергии микропроцессорный трансформаторного включения, с интерфейсами RS485, MODBus, DLMS, учет активной/реактивной энергии	CE308 230/380В 5(10)А 0,5S или аналог
TA1...TA3	Трансформатор тока	ТОП-0,66 250/5, 0,5S
SF1.1...SF1.6	Выключатель автоматический четырехполюсный	ВА99М 4Р ВА47-63 2Р


Типовая однолинейная схема подстанции

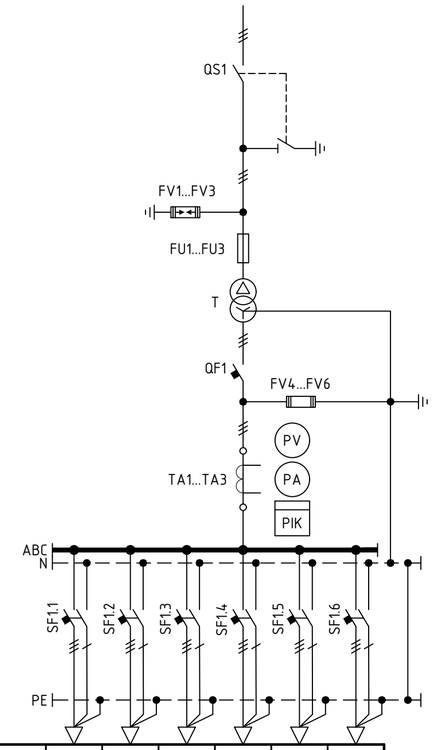

№ АВ по схеме/	SF1.1	SF1.2	SF1.3	SF1.4	SF1.5	SF91.6
Тип АВ	ВА-99М	ВА-99М	ВА-99М	ВА-99М	ВА47-63	ВА47-63
Кол-во полюсов	4р	4р	4р	4р	2р	2р
Номинальный ток, А	250	100	100	100	63	63
Ток расцепителя, А	160	63	63	63	40	40
Назначение						

Габаритные размеры КТП

Вид спереди

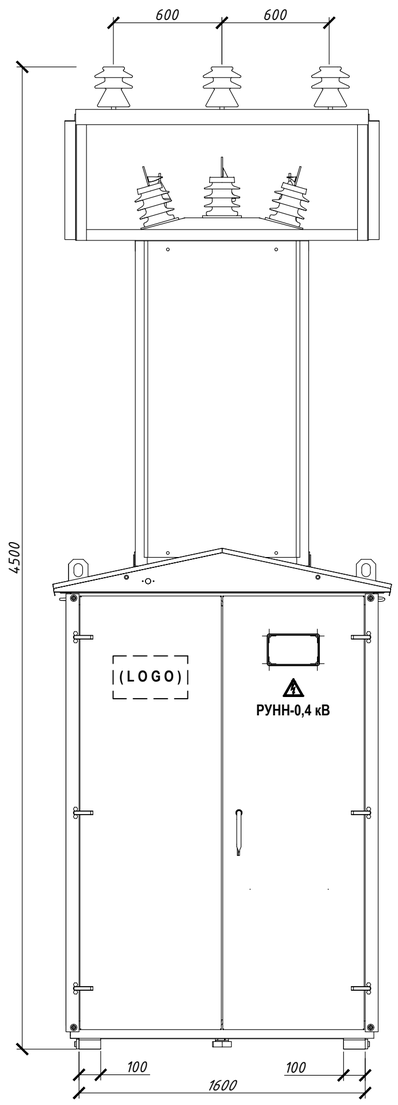

Рев.	Дата	Назначение ревизии	Проверил	Утвердил
A1	13.10.2026	Утверждено для строительства		
R1	24.09.2026	Выпущено для рассмотрения		

ЗАКАЗЧИК: UTG UZTRANSGAZ | ГЕНЕРАЛЬНЫЙ ПОДРЯДЧИК: UET UZBEKENERGOTAMIR | ПОДРЯДЧИК: PBG Pro Build Generation | ГЕНЕРАЛЬНЫЙ ПРОЕКТИРОВЩИК: EAST WEST ENGINEERING

EWE0426-MGL1-ELE-054-DSH-680211-A1

«СТРОИТЕЛЬСТВО НОВЫХ НИТОК (УЧАСТКОВ) ГАЗОПРОВОДОВ «ГАЗЛИ – САРИМОЙ» И «АКЧАЛОК – ГАЗЛИ – НУКУС» ОБЩЕЙ ПРОТЯЖЕННОСТЬЮ НЕ МЕНЕЕ 275 КМ».

Изм.	Кол.уч.	Лист	№док.	Подпись	Дата			
ГИП		Кирпичников С.			10.2026	ГАЗОПРОВОД «ГАЗЛИ-САРИМОЙ» (54 КМ)	Стадия	Лист	Листов
Провер.		Гимранов Т.			10.2026		РД	1	1
Исполн.		Озеров В.			10.2026				
Н. контр.		Кирпичников С.			10.2026	Опросный лист на комплектную трансформаторную подстанцию КТПКм	EAST WEST ENGINEERING	ООО "EAST-WEST Engineering" г. Ташкент 2026г.	

Формат A2