

Общий вид столбового трансформаторного пункта Вид спереди

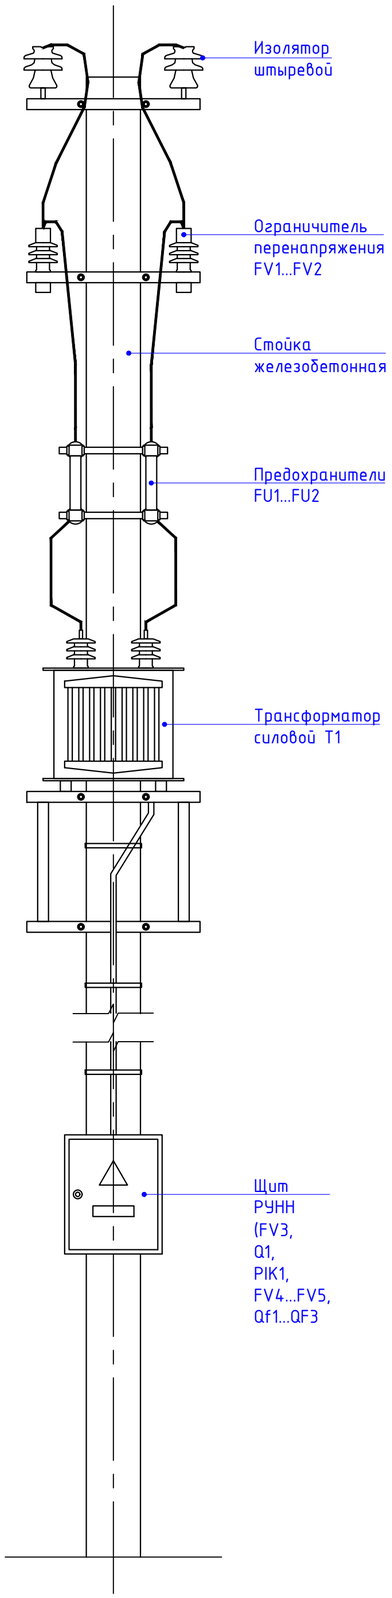

Обозначение на схеме	Наименование электроаппарата	Марка, характеристики
QS1**	Разъединитель трехполюсный наружной установки с заземляющими ножами	не комплектно с КТП
FV1...FV2	Ограничитель перенапряжения высоковольтный на напряжение 6 кВ	ОПН-6/6.3/2-УХЛ1
FU1...FU2	Предохранитель высоковольтный трансформаторный	ПКТ-101-6-0,5-20
T1	Трансформатор силовой маслонаполненный герметичный	ОМГ-10/6/0,23 кВ УХЛ1
FV3	Предохранитель пробивной	комплектно с трансформатором
Q1	Переключатель врубной	40А
FV4...FV5	Устройство защиты от импульсных перенапряжений Iimp-12.5kA, In=20kA, Un=275V	УЗИП Т1+Т2 (1+1)
PIK1	Прибор учета электроэнергии микропроцессорный прямого включения, с интерфейсами RS485, MODBus, DLMS, учет активной энергии	CE208 230В 10(60)А 0,5S или аналог
QF1...4	Выключатель автоматический двухполюсный	ВА47-63 2Р 32А

Типовая однолинейная схема подстанции

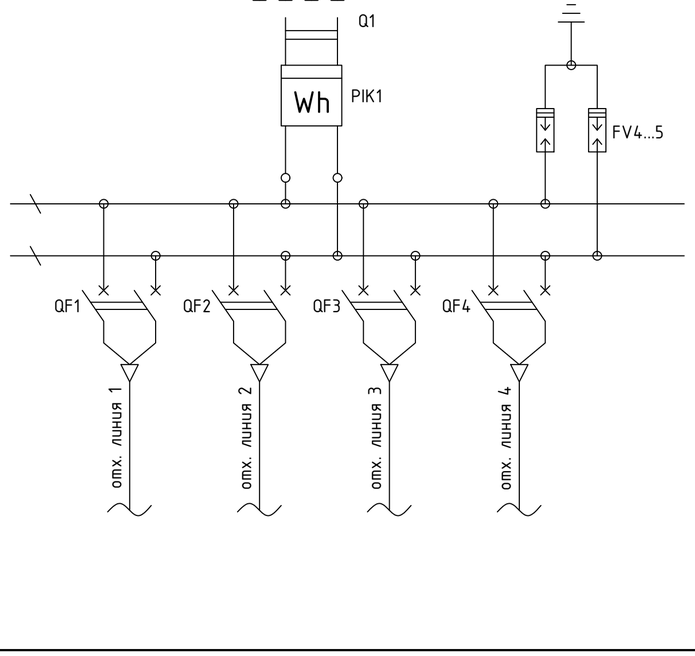

Поз.	Опросные параметры	Параметр
1	Тип подстанции	СТП
2	Количество КТП, шт	3
3	Мощность силового трансформатора, кВА	10
4	Класс напряжения ВН, кВ	6.3
5	Сочетание вводов ВН-НН	ВН-В(воздушный), НН-К(кабельный)
6	Узел установки разъединителя 6 кВ в комплекте	нет
7	Защита от перенапряжений, ВН	ОПН-6/6.3/2-УХЛ1
8	Защита от перенапряжений, НН	УЗИП Т1+Т2 (1+1)
9	Тип силового трансформатора	ОМГ
10	Схема соединений обмоток трансформатора	1/1-0
11	Трансформатор в комплекте поставки СТП	да
12	Обмотки трансформатора	Медные
13	Трансформаторное масло	Ингибиторного типа
14	Учет электроэнергии 0,4кВ	да
15	Счетчик трансформаторного включения	нет
16	Трансформатор тока	-
17	Измерение тока и напряжения	нет
18	АСКУЭ	да
19	Наличие блока управления освещением	нет
21	Климатическое исполнение и степень защиты	УХЛ1, IP54
22	Навесные замки	да
23	Габаритные размеры (ДхШхВ), мм	(*)

Окраска всех элементов СТП, нанесение корпоративных, информационных надписей и знаков безопасности СТП выполняется в соответствии с ПУЭ и внутренними регламентами Заказчика. Корпоративные и информационные знаки должны наноситься таким образом, чтобы не затруднять восприятие друг друга

(*) Размеры ориентировочные, уточняются у завода-изготовителя

(**) Разъединитель QS1 устанавливается на отдельно стоящей опоре (опора с разъединителем учтены спецификацией оборудования основного объема проекта)

Рев.	Дата	Назначение ревизии	Проверил	Утвердил
A1	13.10.2026	Утверждено для строительства		
R1	24.09.2026	Выпущено для рассмотрения		

ЗАКАЗЧИК: UTG UZTRANSGAZ | ГЕНЕРАЛЬНЫЙ ПОДРЯДЧИК: UET UZBEKENERGOTAMIR | ПОДРЯДЧИК: PBG Pro Build Generation | ГЕНЕРАЛЬНЫЙ ПРОЕКТИРОВЩИК: EAST WEST ENGINEERING

Изм.	Кол.уч.	Лист	№док.	Подпись	Дата	
ГИП		Кирпичников С.			10.2026	EWE0426-MGL1-ELE-054-DSH-680212-A1
Провер.		Гимранов Т.			10.2026	«СТРОИТЕЛЬСТВО НОВЫХ НИТОК (УЧАСТКОВ) ГАЗОПРОВОДОВ «ГАЗЛИ - САРИМОЙ» И «АКЧАЛОК - ГАЗЛИ - НУКУС» ОБЩЕЙ ПРОТЯЖЕННОСТЬЮ НЕ МЕНЕЕ 275 КМ».
Исполн.		Озеров В.			10.2026	ГАЗОПРОВОД «ГАЗЛИ-САРИМОЙ» (54 КМ)
Н. контр.		Кирпичников С.			10.2026	Опросной лист на столбовой трансформаторный пункт СТП-10/6/0,23

Стадия	Лист	Листов
РД	1	1

EAST WEST ENGINEERING | ООО "EAST-WEST Engineering" г. Ташкент 2026г.

Формат А2