


Фрагмент №1. ПК0+00 – ПК25+00
М 1:10000

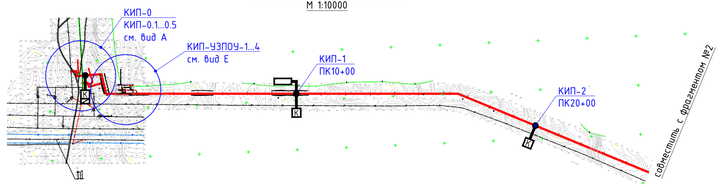


Фрагмент №2. ПК25+00 – ПК66+00
М 1:10000

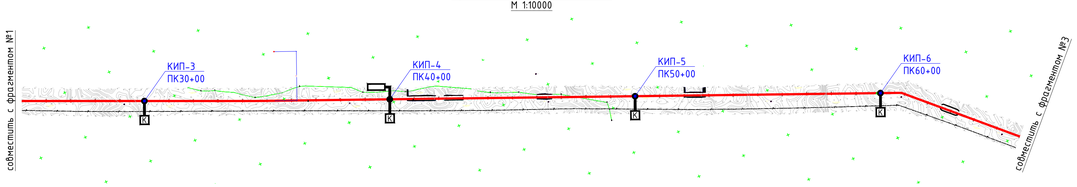

Фрагмент №3. ПК66+00 – ПК147+00
М 1:10000

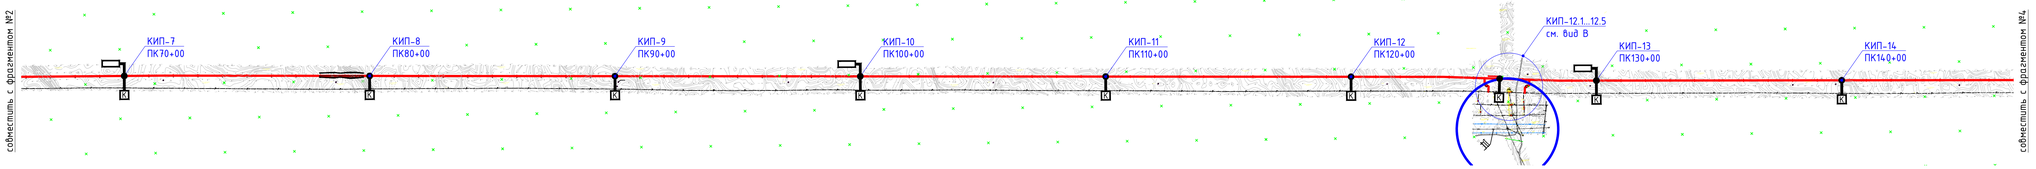

Фрагмент №4. ПК147+00 – ПК228+00
М 1:10000

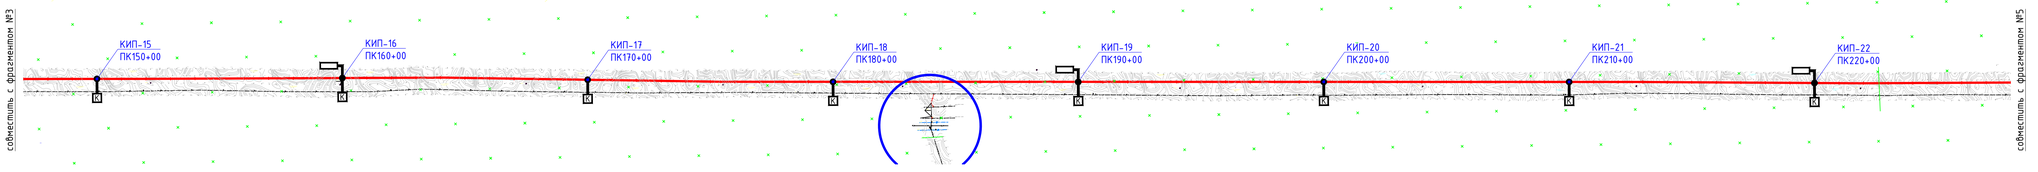

Условные графические обозначения:

- Контрольно-измерительный пункт
- Контрольно-измерительный пункт, совмещенный с блоком диодно-резисторным
- Протектор магниевый

Примечания:

Стойки КИПов, устанавливаемых на крановых узлах, монтировать на расстоянии не менее 2 м. от ограждения кранового узла. Пикетаж данных КИПов при этом считать по строительной длине перемычки
Подробные чертежи крановых узлов см. технологический раздел
Установку стоек КИПов в точках дренажа станций катодной защиты и глубинных анодных заземлителей см. отдельные чертежи EWE0426-MGL1-ECP-054-PLA-680103...680105
Типовые чертежи установки стоек КИПов для различных сооружений см. документы EWE0426-MGL1-ECP-054-PLA-680107...680112
Ведомость расстановки КИПов см. документ EWE0426-MGL1-ECP-054-PLA-680106

Рев.	Дата	Назначение ревизии	Проверил	Утвердил
A1	29.09.2026	Утверждено для строительства		
R1	14.09.2026	Выпущено для рассмотрения		

ЗАКАЗЧИК: | ГЕНЕРАЛЬНЫЙ ПОДРЯДЧИК: UET | ПОДРЯДЧИК: PBC | ГЕНЕРАЛЬНЫЙ ПРОЕКТИРОВЩИК: EAST WEST ENGINEERING

EWE0426-MGL1-ECP-054-DRW-680102-A1


«СТРОИТЕЛЬСТВО НОВЫХ НИТОК (УЧАСТКОВ) ГАЗОПРОВОДОВ «ГАЗЛИ – САРИМОЙ» И «АКЧАЛОК – ГАЗЛИ – УЗБЕКИСТАН» ОБЩЕЙ ПРОТЯЖЕННОСТЬЮ НЕ МЕНЕЕ 275 КМ».

Изм.	Кол.уч.	Лист	№док.	Подпись	Дата		
ГИП		Кирпичников С.			09.2026	ГАЗОПРОВОД «ГАЗЛИ-САРИМОЙ» (54 КМ)	
Провер.		Гимранов Т.			09.2026		
Исполн.		Озеров В.			09.2026		
Н. контр.		Кирпичников С.			09.2026	Ситуационный план газопровода с размещением средств ЭХЗ. 1:10000	


Стадия	Лист	Листов
РД	1	3

ООО "EAST-WEST Engineering"
г. Ташкент 2026г.


Фрагмент №5. ПК228+00 – ПК347+00
М 1:10000

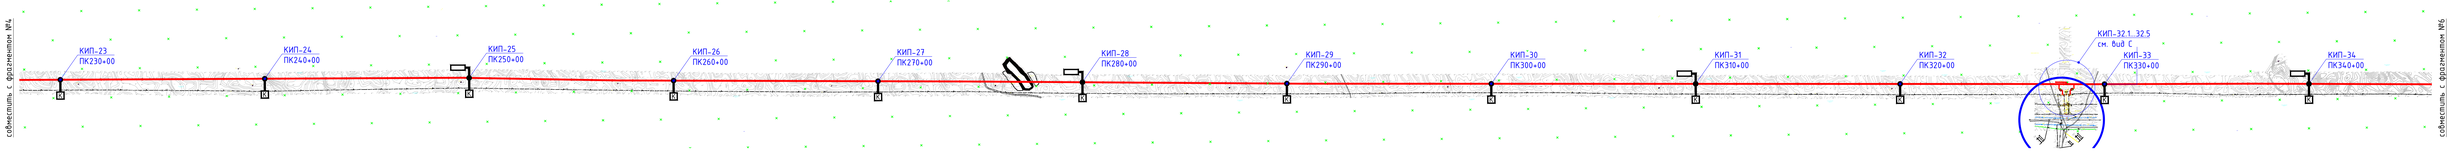

Фрагмент №6. ПК347+00 – ПК448+00
М 1:10000

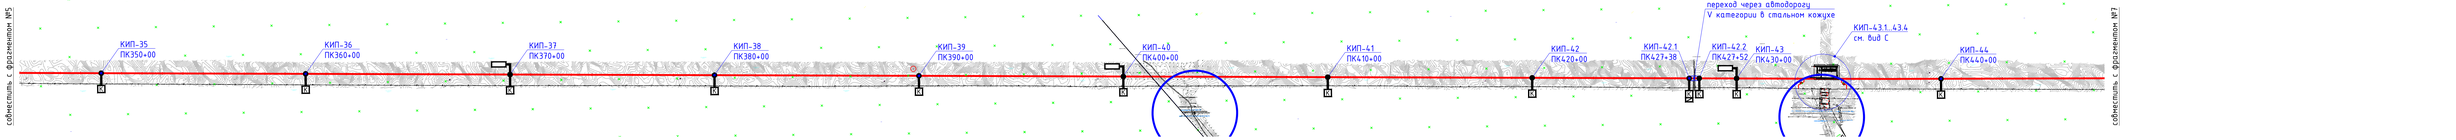

Фрагмент №7. ПК448+00 – ПК541+00
М 1:10000

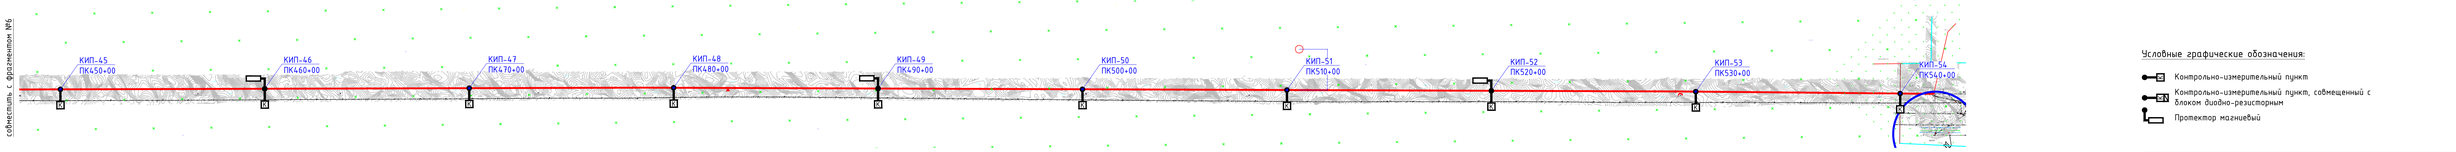


Условные графические обозначения:


- Контрольно-измерительный пункт
- Контрольно-измерительный пункт, совмещенный с блоком диодно-резисторным
- Протектор магниевый

Изм.	Кол.уч.	Лист	№ док.	Подпись	Дата	EWE0426-MGL1-ECP-054-DRW-680102-A1	Лист 2	


Вид А. М 1:1000

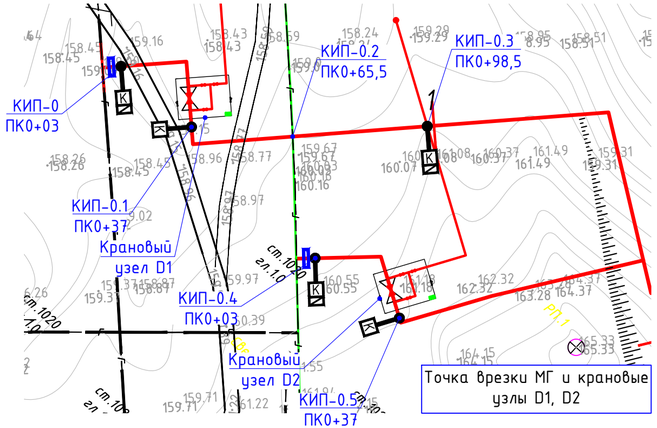


Вид В. М 1:1000

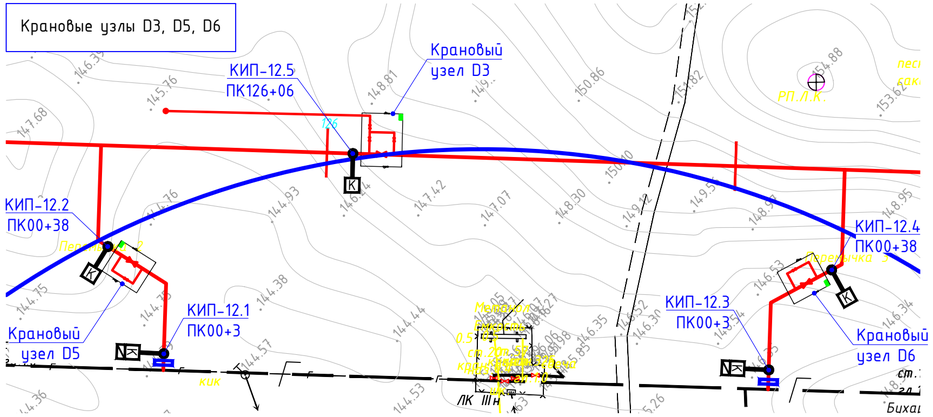


Вид С. М 1:1000

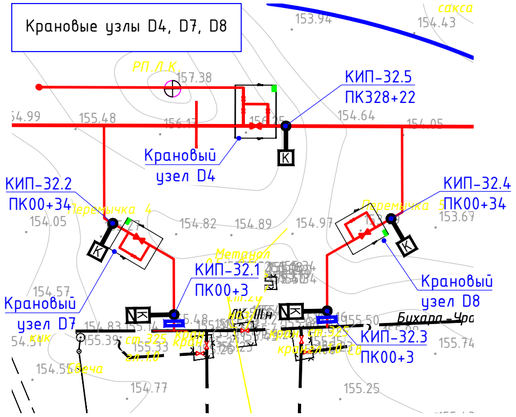

Вид D. М 1:1000

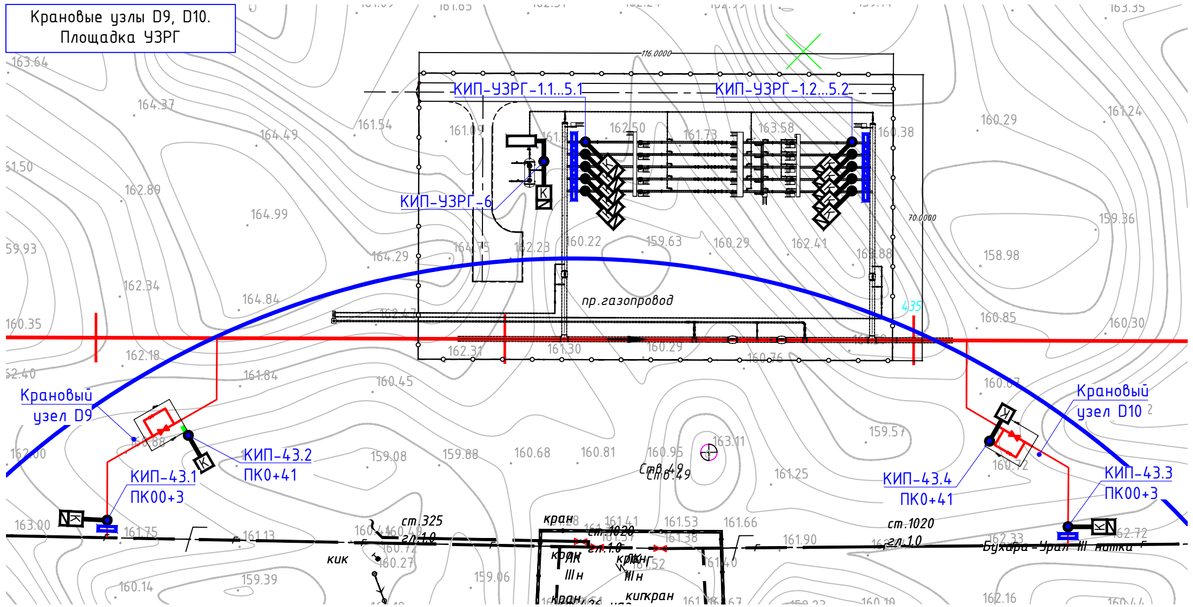

Вид Е. М 1:1000

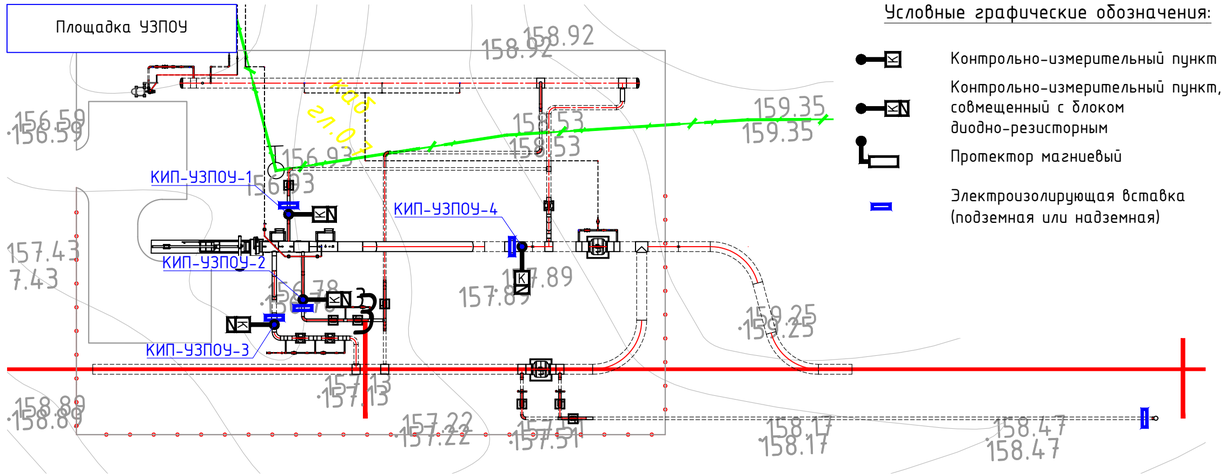

Условные графические обозначения:

- Контрольно-измерительный пункт
- Контрольно-измерительный пункт, совмещенный с блоком диодно-резисторным
- Протектор магниевый
- Электроизолирующая вставка (подземная или надземная)

Изм.	Колуч.	Лист	№ док.	Подпись	Дата	EWE0426-MGL1-ECP-054-DRW-680102-A1	Лист 3