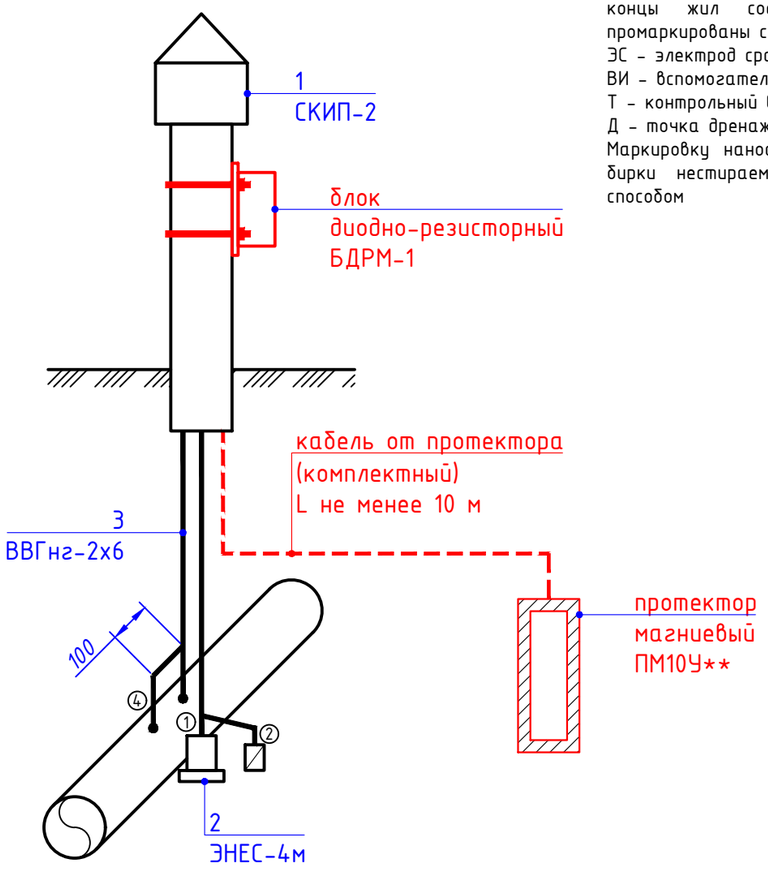


Все силовые и измерительные клеммы КИПа должны быть пронумерованы, а концы жил соединительных кабелей промаркированы следующим образом:
ЭС – электрод сравнения
ВИ – вспомогательный электрод
Т – контрольный вывод к трубопроводу
Д – точка дренажа
Маркировку наносить на маркировочные бирки нестираемым лаком либо иным способом

Спецификация элементов

№ п.п	Обозначение	Наименование	Ед. изм.	Кол-во	Масса кг	Примечание
1	СКИП-2-6-0-2,0 УХЛ1 (СКИП-2Б-6-0-2,0 УХЛ1)**	Стойка контрольно-измерительного пункта, высотой 2 м., силовых клемм – 6, измерительных клемм – 0	шт	1	29,0	
2	ЭНЕС-4М	Электрод сравнения неполяризующийся медносульфатный с датчиком потенциала	шт	1	5,5	
3	ВВГнг(А)-2х6 мм^2	Кабель силовой с медными жилами, с изоляцией и оболочкой из ПВХ пластиката, на напряжение до 1 кВ	м	3		
4	ТУТ-12/6	Трубка термоусаживаемая на напряжение до 1 кВ	м	0,25		
5	ТМЛ 6-6-4	Наконечник медный луженый на кабель сечением 6 мм^2	шт	2		
6	ПМ10У**	Протектор магниевый	шт	1		врем. защита
7	БДРМ-10-2-11-К-УХЛ1**	Блок диодно-резисторный	шт	1		врем. защита

Примечания: провод от электрода сравнения до клеммных зажимов КИПа входит в комплект поставки электрода сравнения

(*) Установить съемную перемычку между клеммами датчика потенциала (вспомогательного электрода) и клеммами кабелей, присоединенных к трубопроводу. На период производства замеров поляризационных потенциалов перемычка снимается.


(**) На период строительства для временной защиты трубопровода предусмотреть магниевые протекторы типа ПМ10У. Протекторы устанавливаются на трассовых КИПах через каждые 3 км по проектируемому трубопроводу. Протекторы закапываются со стороны трубопровода, противоположной той, с которой устанавливается электрод сравнения, в предварительно вырытый шурф с подсыпкой привозным грунтом с низким удельным электрическим сопротивлением (к примеру, глинозем). Подробные мероприятия по установке и активации протектора см. техническую документацию на окончательно выбранную марку протектора.

При оформлении заказа на протекторы у завода-изготовителя длину контактного провода определить не менее 10 м


В случае, если по результатам замеров защитный ток протектора составляет менее 0,015 А, необходимо предусматривать групповые установки протекторов. При этом расчетное количество протекторов, необходимое для защиты участка трубопровода, следует увеличивать в 1,3 – 1,4 раза

После окончания строительства, перед проведением пусконаладочных работ и вводе трубопровода в эксплуатацию контактные жилы протектора необходимо отключить от клемм КИПа (3) и заизолировать

Схема подключения клеммных терминалов КИП

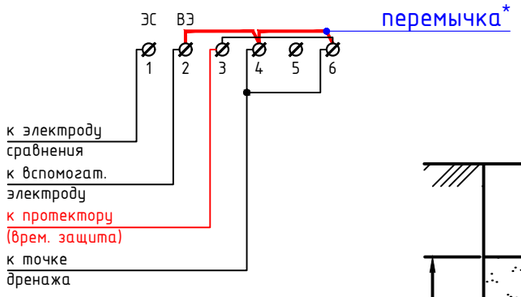

Эскиз установки электрода сравнения и протектора

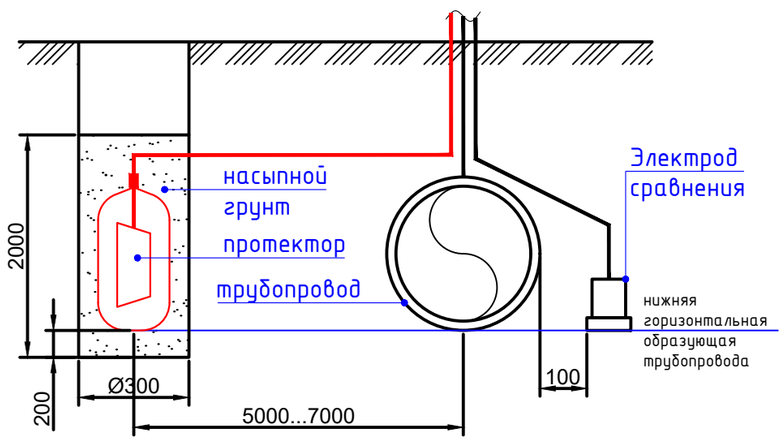

A2	22.09.2026	Утверждено для строительства		
A1	06.08.2026	Утверждено для строительства		
R1	13.08.2026	Выпущено для рассмотрения		
Рев.	Дата	Назначение ревизии	Проверил	Утвердил

ЗАКАЗЧИК: UTG UZTRANSGAZ ГЕНЕРАЛЬНЫЙ ПОДРЯДЧИК: UET UZBEKENERGOTAMIR ПОДРЯДЧИК: PBG Pro Build Generation ГЕНЕРАЛЬНЫЙ ПРОЕКТИРОВЩИК: EAST WEST ENGINEERING

Изм.	Кол.уч.	Лист	№док.	Подпись	Дата
ГИП		Кирпичников С.			09.2026
Провер.		Гимранов Т.			09.2026
Исполн.		Озеров В.			09.2026
Н. контр.		Кирпичников С.			09.2026

EWE0426-MGL1-ECP-054-DRW-680107-A2

«СТРОИТЕЛЬСТВО НОВЫХ НИТОК (УЧАСТКОВ) ГАЗОПРОВОДОВ «ГАЗЛИ – САРИМОЙ» И «АКЧАЛОК – ГАЗЛИ – НУКУС» ОБЩЕЙ ПРОТЯЖЕННОСТЬЮ НЕ МЕНЕЕ 275 КМ».

ГАЗОПРОВОД «ГАЗЛИ-САРИМОЙ» (54 КМ)

Стадия	Лист	Листов
РД	1	1

Установка контрольно-измерительного прибора на трубопроводе

ООО "EAST-WEST Engineering"
г. Ташкент 2026г.