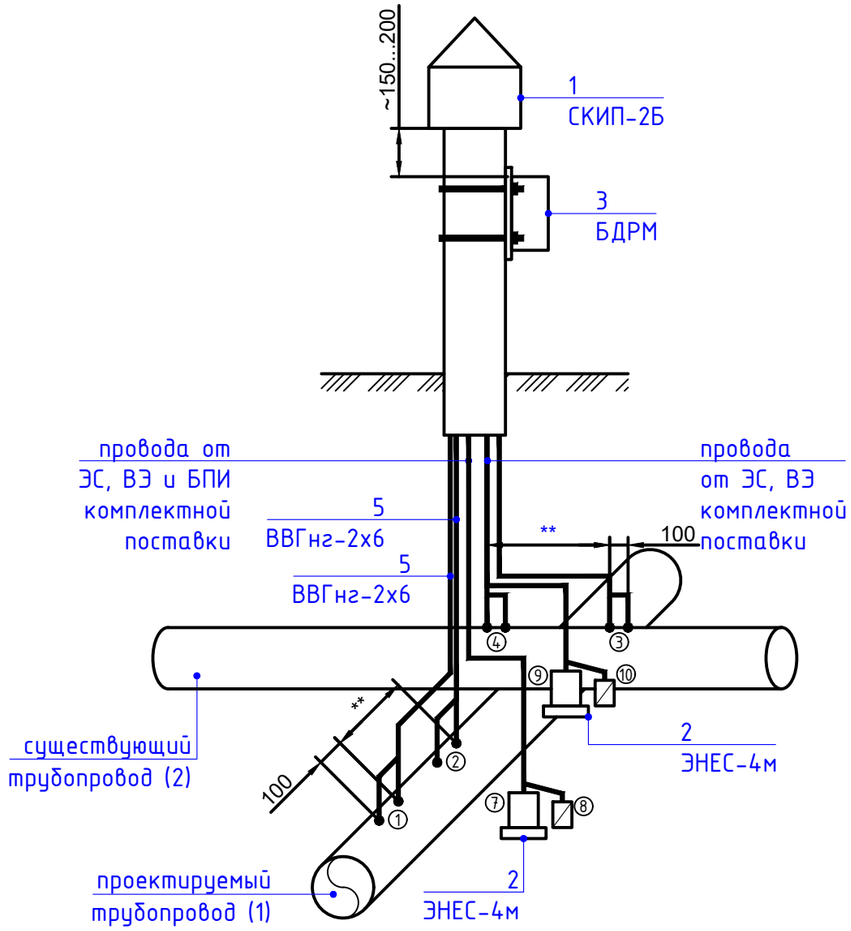


Все силовые и измерительные клеммы КИПа должны быть пронумерованы, а концы жил соединительных кабелей промаркированы следующим образом:
ЭС – электрод сравнения
ВИ – вспомогательный электрод
Т – контрольный вывод к трубопроводу
Д – точка дренажа
Маркировку наносить на маркировочные бирки нестираемым лаком либо иным способом


Спецификация элементов

№ п.п	Обозначение	Наименование	Ед. изм.	Кол-во	Масса кг	Примечание
1	СКИП-2Б-6-6-2,0 УХЛ1	Стойка контрольно-измерительного пункта, высотой 2 м., силовых клемм – 6, измерительных клемм – 6, с возможностью установки диодно-резисторного блока	шт	1	29,0	
2	ЭНЕС-4М	Электрод сравнения неполяризующийся медносульфатный с датчиком потенциала	шт	2	5,5	
3	БДРМ-1	Блок диодно-резисторный	шт	1		
4	ВВГнг(А)-2х6 мм^2	Кабель силовой с медными жилами, с изоляцией и оболочкой из ПВХ пластиката, на напряжение до 1 кВ	м	20		
5	ТУТ-12/6	Трубка термоусаживаемая на напряжение до 1 кВ	м	1		
6	ТМЛ 6-6-4	Наконечник медный луженый на кабель сечением 6 мм^2	шт	8		


Примечания:
1. Провод от электрода сравнения до клеммных зажимов КИПа входит в комплект поставки электрода сравнения
2. На период производства измерений электроизолирующих свойств на изолирующей вставке клеммы 2-8 и 4-10 размыкаются

(*) Установить съемные перемычки между клеммами датчика потенциала (вспомогательного электрода) и клеммами кабелей, присоединенных к трубопроводу. На период производства замеров поляризационных потенциалов перемычки снимаются.
(**) Не менее 3х диаметров трубопровода

Схема подключения клеммных терминалов КИП

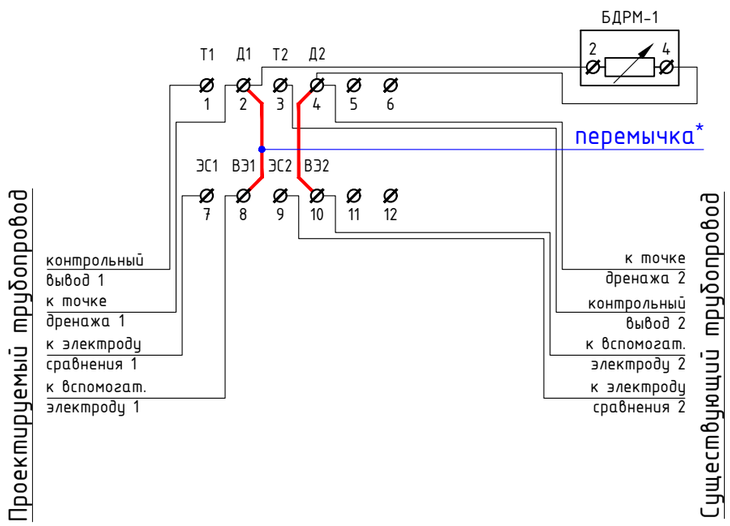

Эскиз установки электрода сравнения

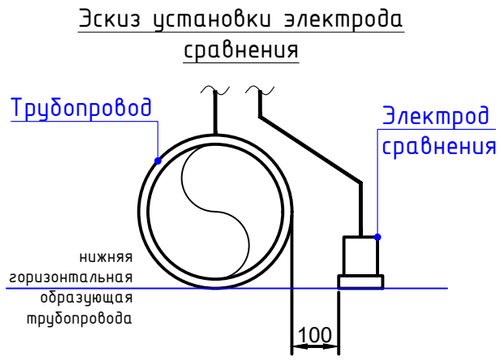

Рев.	Дата	Назначение ревизии	Проверил	Утвердил
A2	22.09.2026	Утверждено для строительства		
A1	06.08.2026	Утверждено для строительства		
R1	13.08.2026	Выпущено для рассмотрения		

ЗАКАЗЧИК: UTG UZTRANSGAZ | ГЕНЕРАЛЬНЫЙ ПОДРЯДЧИК: UET UZBEKENERGOTAMIR | ПОДРЯДЧИК: PBG Pro Build Generation | ГЕНЕРАЛЬНЫЙ ПРОЕКТИРОВЩИК: EAST WEST ENGINEERING

EWE0426-MGL1-ECP-054-DRW-680108-A2

«СТРОИТЕЛЬСТВО НОВЫХ НИТОК (УЧАСТКОВ) ГАЗОПРОВОДОВ «ГАЗЛИ – САРИМОЙ» И «АКЧАЛОК – ГАЗЛИ – НУКУС» ОБЩЕЙ ПРОТЯЖЕННОСТЬЮ НЕ МЕНЕЕ 275 КМ».

Изм.	Кол.уч.	Лист	№док.	Подпись	Дата			
ГИП		Кирпичников С.			09.2026	ГАЗОПРОВОД «ГАЗЛИ-САРИМОЙ» (54 КМ)	Стадия	Лист	Листов
Провер.		Гимранов Т.			09.2026		РД	1	1
Исполн.		Озеров В.			09.2026				
Н. контр.		Кирпичников С.			09.2026	Установка контрольно-измерительного прибора на пересечении с трубопроводом	EAST WEST ENGINEERING	ООО "EAST-WEST Engineering" г. Ташкент 2026г.	