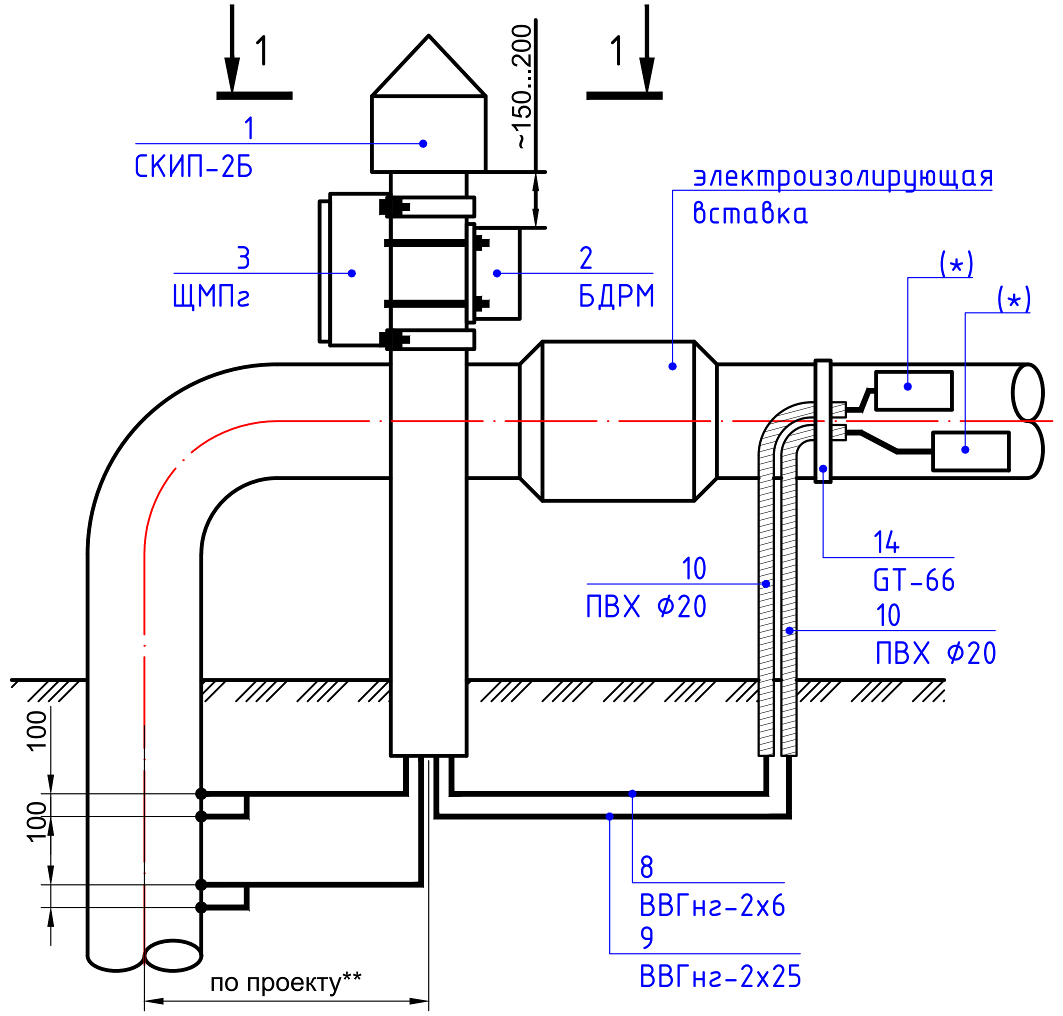

Спецификация элементов

№ п.п	Обозначение	Наименование	Ед. изм.	Кол -во	Масса кг	Примечание
1	СКИП-2Б-6-0-2,0 УХЛ1	Стойка контрольно-измерительного пункта, высотой 2 м., силовых клемм – 6, измерительных клемм – 0, с возможностью установки диодно-резисторного блока	шт	1	29,0	
2	БДРМ-10-2-11-К-УХЛ1	Блок диодно-резисторный	шт	1		
3	ЩМПг-40х21х15 У1	Щит металлический с монтажной панелью герметичный IP54	шт	1		
4	ШС-50-0,5	Шунт измерительный	шт	1		
5	ВРА1-1-11600-00 УХЛ1	Выключатель врубной	шт	1		
6	ИП-3	Искровой промежуток	шт	1		
7	ТВ-4504	Клеммный терминал	шт	1		
8	ВВГнг(А)-2х6 мм^2	Кабель силовой с медными жилами, с изоляцией и оболочкой из ПВХ пластиката, на напряжение до 1 кВ	м	10		
9	ВВГнг(А)-2х25 мм^2	То же	м	10		
10	РЗ-ЦП-20	Металлорукав стальной оцинкованный с ПВХ-покрытием диаметром 20 мм	м	4		
11	ТУТ-12/6	Трубка термоусаживаемая на напряжение до 1 кВ	м	1		
12	ТМЛ 6-6-4	Наконечник медный луженый на кабель сечением 6 мм^2	шт	4		
13	ТМЛ 25-10-8	Наконечник медный луженый на кабель сечением 25 мм^2	шт	4		
14	GT-66	Крепежная лента из стекловолокна	м	1,5		
15	К107ц	Полоса перфорированная оцинкованная L=400	шт	2		
16	ГОСТ 7798-70*	Болт М8х50.58.096	шт	4	0.031	
17	ГОСТ 5915-70*	Гайка М8.5.096	шт	8	0.011	
18	ГОСТ 11371-78*	Шайба 8.01.09	шт	4	0.004	

Все силовые и измерительные клеммы КИПа должны быть пронумерованы, а концы жил соединительных кабелей промаркированы следующим образом:
ЭС - электрод сравнения
ВИ - вспомогательный электрод
Т - контрольный вывод к трубопроводу
Д - точка дренажа
Маркировку наносить на маркировочные бирки нестираемым лаком либо иным способом

Схема электрических соединений

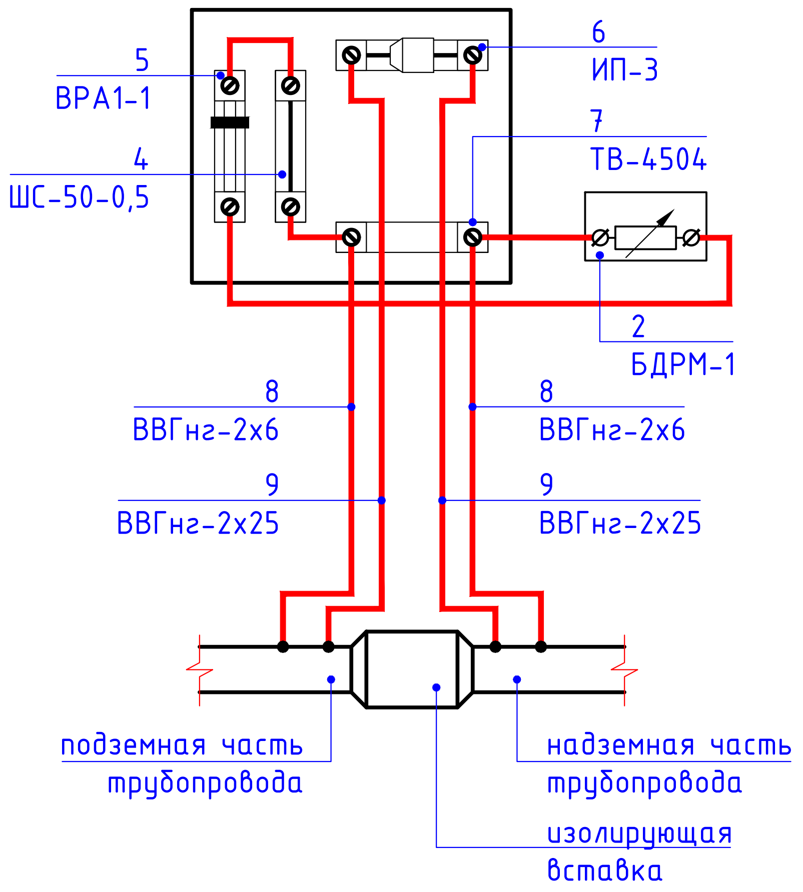

Вид 1 - 1
(установленный БДРМ не показан)

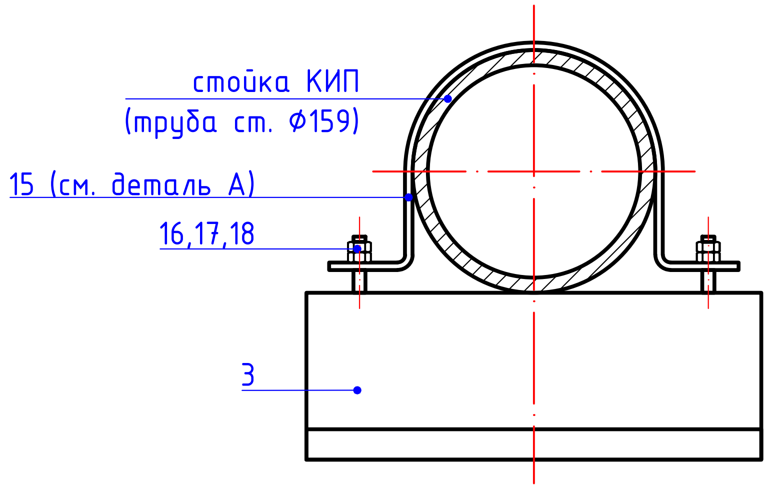

Поз. 15

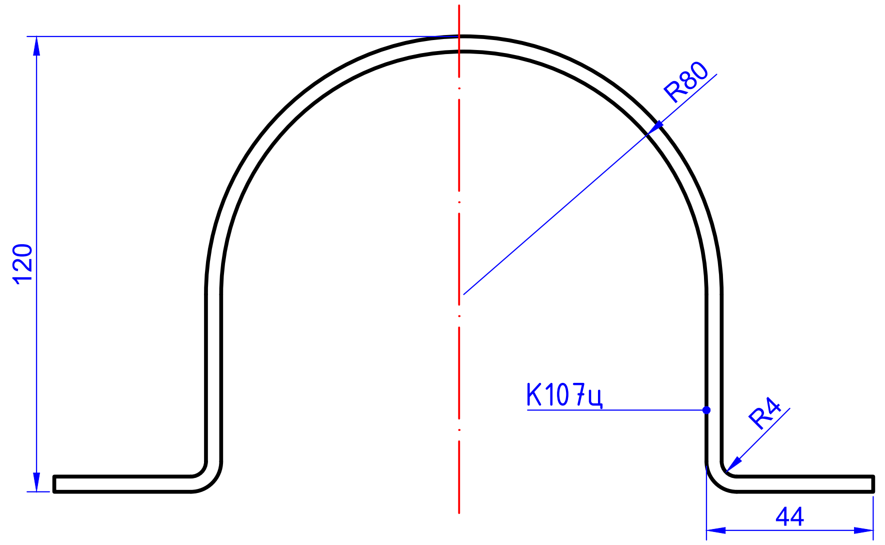

Примечания:

(*) Технологию и спецификацию на узлы присоединения кабелей к трубопроводу термитной сваркой см. документ EWE0426-MGL1-ECP-054-DRW-680113
(**) Расстояния от подъема трубопровода до СКИПа и от СКИПа до электроизолирующей вставки уточнять по чертежам технологического раздела

Рев.	Дата	Назначение ревизии	Проверил	Утвердил
A3	02.10.2026	Утверждено для строительства		
A2	22.09.2026	Утверждено для строительства		
A1	06.08.2026	Утверждено для строительства		
R1	13.08.2026	Выпущено для рассмотрения		

ЗАКАЗЧИК: UTG UZTRANSGAZ «TRANSGAZINJINIRING»
ГЕНЕРАЛЬНЫЙ ПОДРЯДЧИК: UET UZBEKENERGOTAMIR
ПОДРЯДЧИК: PBG Pro Build Generation
ГЕНЕРАЛЬНЫЙ ПРОЕКТИРОВЩИК: EAST WEST ENGINEERING

EWE0426-MGL1-ECP-054-DRW-680109-A3

«СТРОИТЕЛЬСТВО НОВЫХ НИТОК (УЧАСТКОВ) ГАЗОПРОВОДОВ «ГАЗЛИ – САРИМОЙ» И «АКЧАЛОК – ГАЗЛИ – НУКУС» ОБЩЕЙ ПРОТЯЖЕННОСТЬЮ НЕ МЕНЕЕ 275 КМ».

Изм.	Кол.уч.	Лист	№док.	Подпись	Дата
ГИП		Кирпичников С.			09.2026
Провер.		Гимранов Т.			09.2026
Исполн.		Озеров В.			09.2026
Н. контр.		Кирпичников С.			09.2026

ГАЗОПРОВОД «ГАЗЛИ-САРИМОЙ» (54 КМ)

Стадия	Лист	Листов
РД	1	1

Установка контрольно-измерительного прибора на надземном изолирующем соединении

EAST WEST ENGINEERING
ООО "EAST-WEST Engineering"
г. Ташкент 2026г.