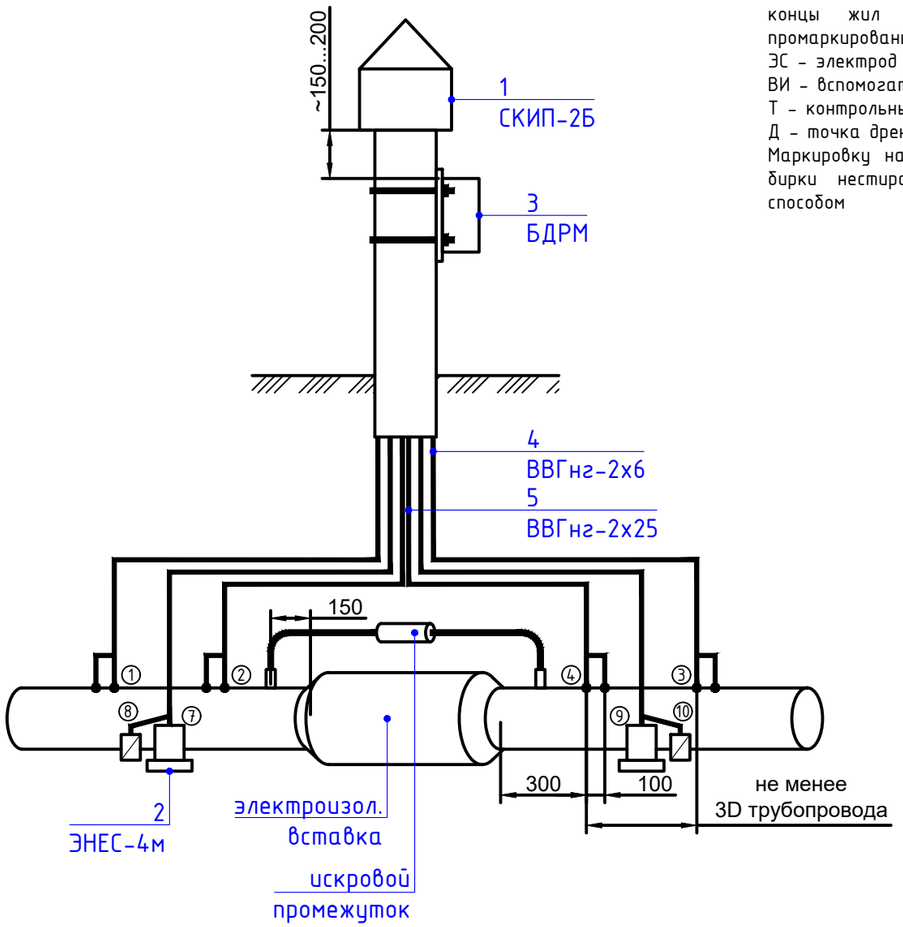


Все силовые и измерительные клеммы КИПа должны быть пронумерованы, а концы жил соединительных кабелей промаркированы следующим образом:
ЭС – электрод сравнения
ВИ – вспомогательный электрод
Т – контрольный вывод к трубопроводу
Д – точка дренажа
Маркировку наносить на маркировочные бирки нестираемым лаком либо иным способом


Спецификация элементов

№ п.п	Обозначение	Наименование	Ед. изм.	Кол-во	Масса кг	Примечание
1	СКИП-2Б-6-6-2,0 УХЛ1	Стойка контрольно-измерительного пункта, высотой 2 м., силовых клемм – 6, измерительных клемм – 6, с возможностью установки диодно-резисторного блока	шт	1	29,0	
2	ЭНЕС-4М	Электрод сравнения неполяризующийся медносульфатный с датчиком потенциала	шт	2	5,5	
3	БДРМ-10-2-11-К-УХЛ1	Блок диодно-резисторный	шт	1		
4	ВВГнг(А)-2х6 мм^2	Кабель силовой с медными жилами, с изоляцией и оболочкой из ПВХ пластиката, на напряжение до 1 кВ	м	14		
5	ВВГнг(А)-2х25 мм^2	То же	м	6		
6	ТУТ-12/6	Трубка термоусаживаемая на напряжение до 1 кВ	м	1		
7	ТМЛ 6-6-4	Наконечник медный луженый на кабель сечением 6 мм^2	шт	4		
8	ТМЛ 25-10-8	Наконечник медный луженый на кабель сечением 25 мм^2	шт	4		


Примечания:
1. Провод от электрода сравнения до клеммных зажимов КИПа входит в комплект поставки электрода сравнения
2. На период производства измерений электроизолирующих свойств на изолирующей вставке клеммы 2-8 и 4-10 размыкаются

(*) Установить съемные перемычки между клеммами датчика потенциала (вспомогательного электрода) и клеммами кабелей, присоединенных к трубопроводу. На период производства замеров поляризационных потенциалов перемычки снимаются.

Схема подключения клеммных терминалов КИП

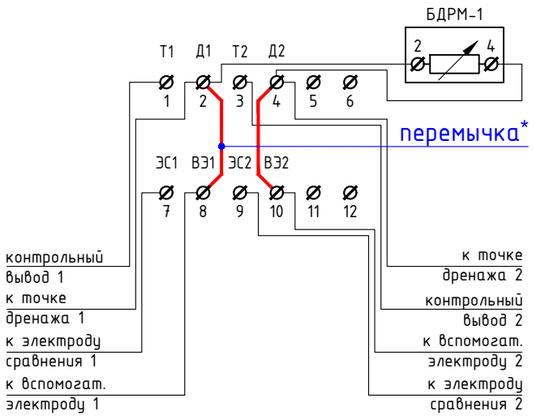

Эскиз установки электрода сравнения

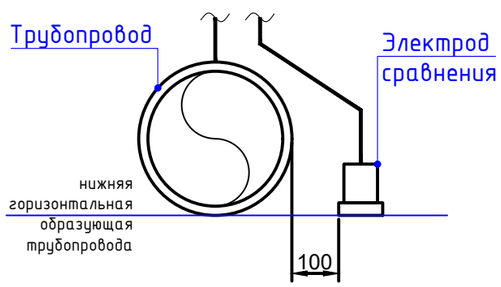

Рев.	Дата	Назначение ревизии	Проверил	Утвердил
A2	22.09.2026	Утверждено для строительства		
A1	06.08.2026	Утверждено для строительства		
R1	13.08.2026	Выпущено для рассмотрения		

ЗАКАЗЧИК: UTG UZTRANSGAZ «TRANSGAZLINIRING»
ГЕНЕРАЛЬНЫЙ ПОДРЯДЧИК: UET ÖZBEKENERGOTAMIR
ПОДРЯДЧИК: PBG Pro Build Generation
ГЕНЕРАЛЬНЫЙ ПРОЕКТИРОВЩИК: EAST WEST ENGINEERING

Изм.	Кол.уч.	Лист	№док.	Подпись	Дата
ГИП		Кирпичников С.			09.2026
Провер.		Гимранов Т.			09.2026
Исполн.		Озеров В.			09.2026
Н. контр.		Кирпичников С.			09.2026

EWE0426-MGL1-ECP-054-DRW-680110-A2

«СТРОИТЕЛЬСТВО НОВЫХ НИТОК (УЧАСТКОВ) ГАЗОПРОВОДОВ «ГАЗЛИ – САРИМОЙ» И «АКЧАЛОК – ГАЗЛИ – НУКУС» ОБЩЕЙ ПРОТЯЖЕННОСТЬЮ НЕ МЕНЕЕ 275 КМ».

ГАЗОПРОВОД «ГАЗЛИ-САРИМОЙ» (54 КМ)

Стадия	Лист	Листов
РД	1	1

Установка контрольно-измерительного прибора на ВЭИ

EAST WEST ENGINEERING

ООО "EAST-WEST Engineering"
г. Ташкент 2026г.