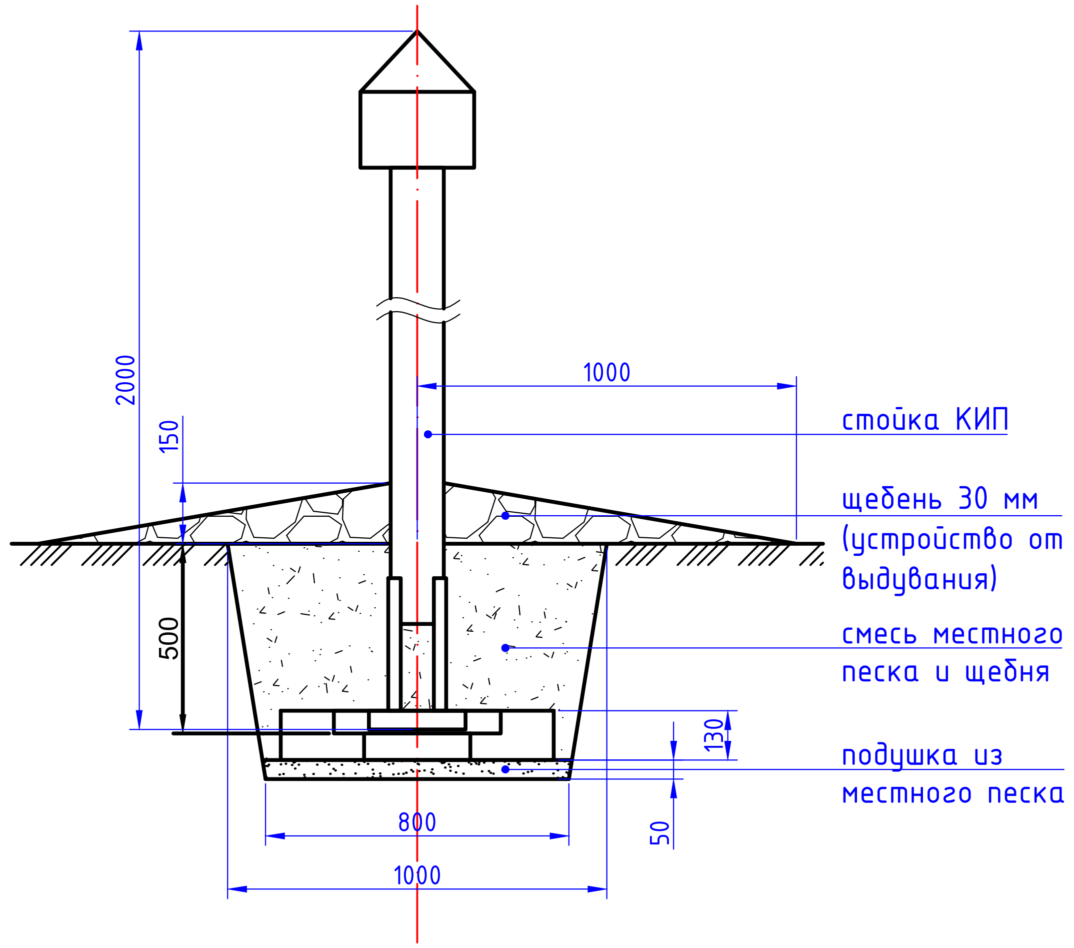
2000
150
500
1000
130
50
800
1000
стойка КИП
щебень 30 мм
(устройство от выдувания)
смесь местного песка и щебня
подушка из местного песка

A

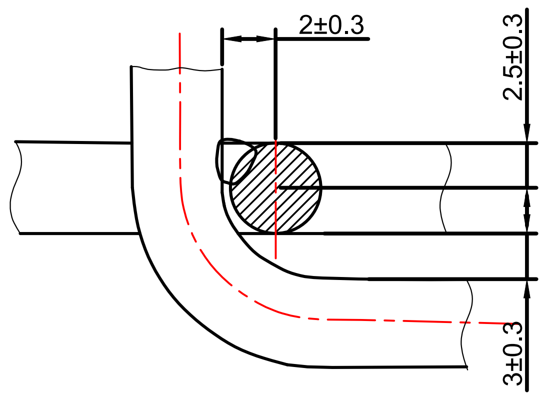

Подушка

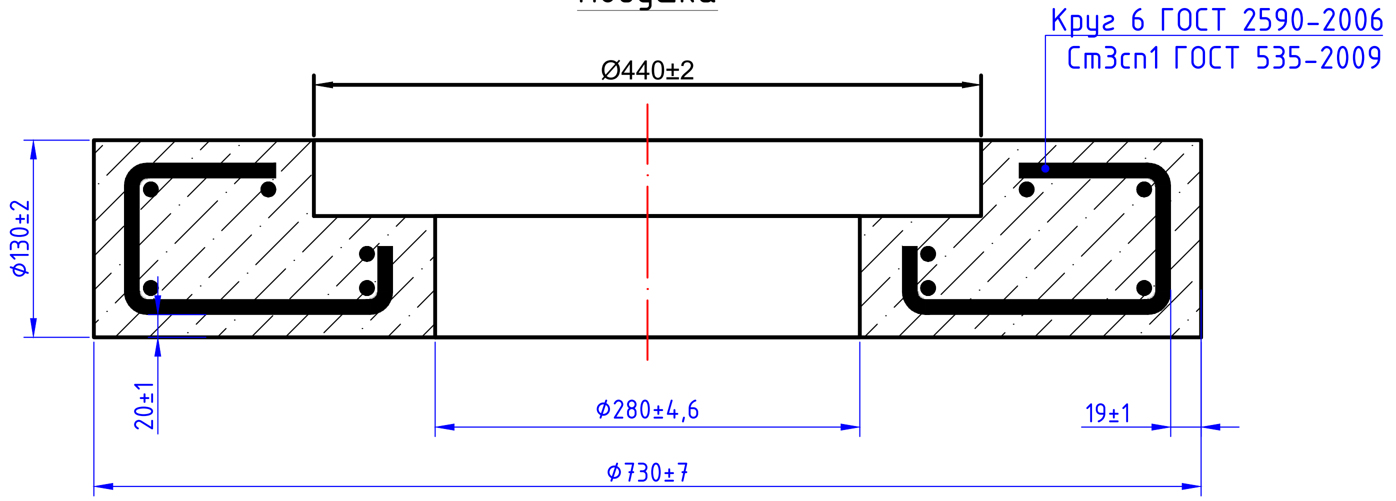

Каркас для подушки

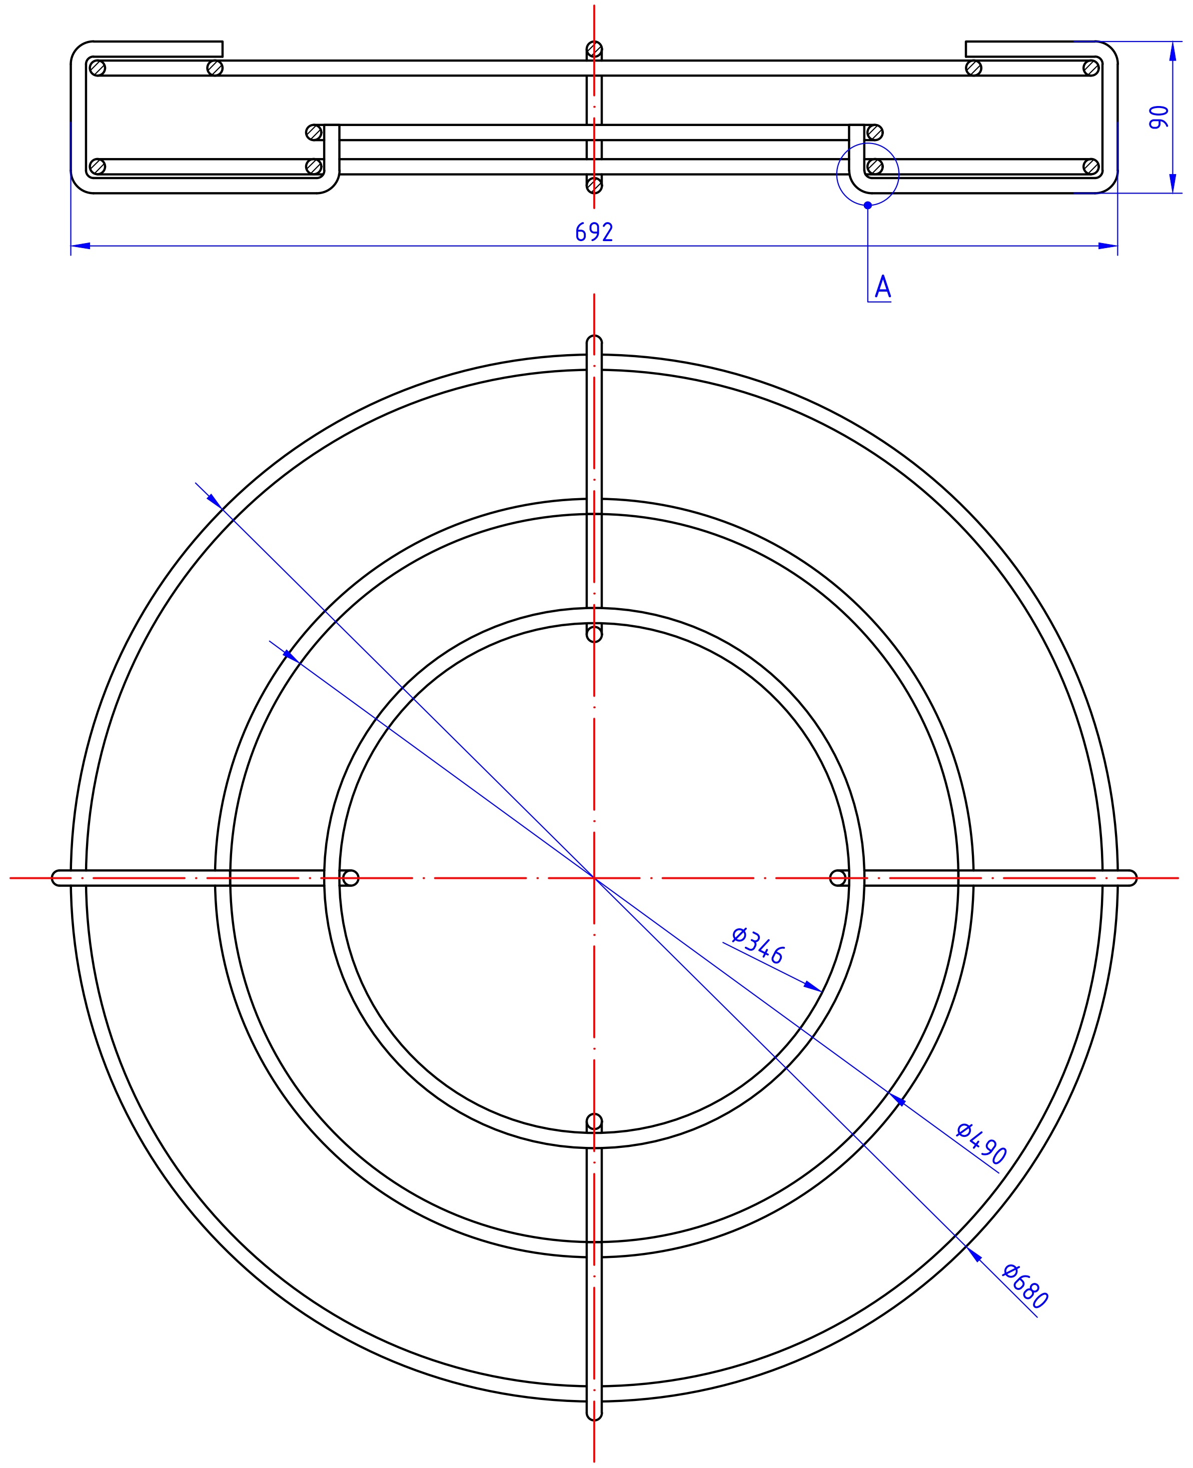

Спецификация элементов

№ п.п	Обозначение	Наименование	Ед. изм.	Кол -во	Масса кг	Примечание
1	В-6 ГОСТ 2590-2006 Ст1сп1 ГОСТ 53525-2009	Сталь круглая Ø10 мм	м	10		
2	ГОСТ 26633-2015	Бетон класса В10	$м^3$	0,03		
3	МБ-50	Мастика гидроизоляционная	кг	2,20		
4	ГОСТ 8267-93	Щебень фракцией 30 мм	$м^3$	0,10	1700	
5		Табличка информационная	шт	1		компл. с КИПом
6		Рытье/обратная засыпка котлована под установку СКИПа	$м^3$	0,42 0,37		
7		Устройство песчаной подушки из местного песка	$м^3$	0,05		
8		Устройство защиты из щебня вручную	$м^2$	3,10		
9		Устройство гидроизоляции фундамента за 2 раза	$м^2$	2,20		

Примечания:

Сварку производить электродами Э42А согласно ГОСТ5264-80

Перед установкой подушки на песчаную подсыпку и стойки КИПа произвести гидроизоляцию подушки мастикой за 2 раза
КИП устанавливается над осью магистрального газопровода со смещением от нее не далее 0,2 м от точки подключения к магистральному газопроводу контрольных проводов

Каждый КИП снабжается информационной табличкой. На табличке атмосферостойкой краской должна быть нанесена информация:
- обозначение магистрального газопровода
- диаметр, глубина залегания
- порядковый номер КИПа
- информация об эксплуатирующей организации

Размеры и конечное содержание таблички определяются эксплуатирующей организацией по согласованию с Заказчиком

Рев.	Дата	Назначение ревизии	Проверил	Утвердил
A1	06.08.2026	Утверждено для строительства		
R1	13.07.2026	Выпущено для рассмотрения		

ЗАКАЗЧИК: UTG UZTRANSGAZ «TRANSGAZINJINIRING»
ГЕНЕРАЛЬНЫЙ ПОДРЯДЧИК: UET UZBEKENERGOTAMIR
ПОДРЯДЧИК: PBG Pro Build Generation
ГЕНЕРАЛЬНЫЙ ПРОЕКТИРОВЩИК: EAST WEST ENGINEERING

EWE0426-MGL1-ECP-054-DRW-680113-A1

«СТРОИТЕЛЬСТВО НОВЫХ НИТОК (УЧАСТКОВ) ГАЗОПРОВОДОВ «ГАЗЛИ – САРИМОЙ» И «АКЧАЛОК – ГАЗЛИ – НУКУС» ОБЩЕЙ ПРОТЯЖЕННОСТЬЮ НЕ МЕНЕЕ 275 КМ».

Изм.	Кол.уч.	Лист	№док.	Подпись	Дата
ГИП		Схабицкий А.			08.2026
Провер.		Гимранов Т.			08.2026
Исполн.		Озеров В.			08.2026
Н. контр.		Схабицкий А.			08.2026

ГАЗОПРОВОД «ГАЗЛИ-САРИМОЙ» (54 КМ)

Стадия	Лист	Листов
РД	1	1

Узел закрепления стойки КИПа на бетонной подушке. Устройство защиты от выдувания в подвижных песках

EAST WEST ENGINEERING
ООО "EAST-WEST Engineering"
г. Ташкент 2026г.