



Глубинный анодный заземлитель ЭХ3.052-05
Общий вид

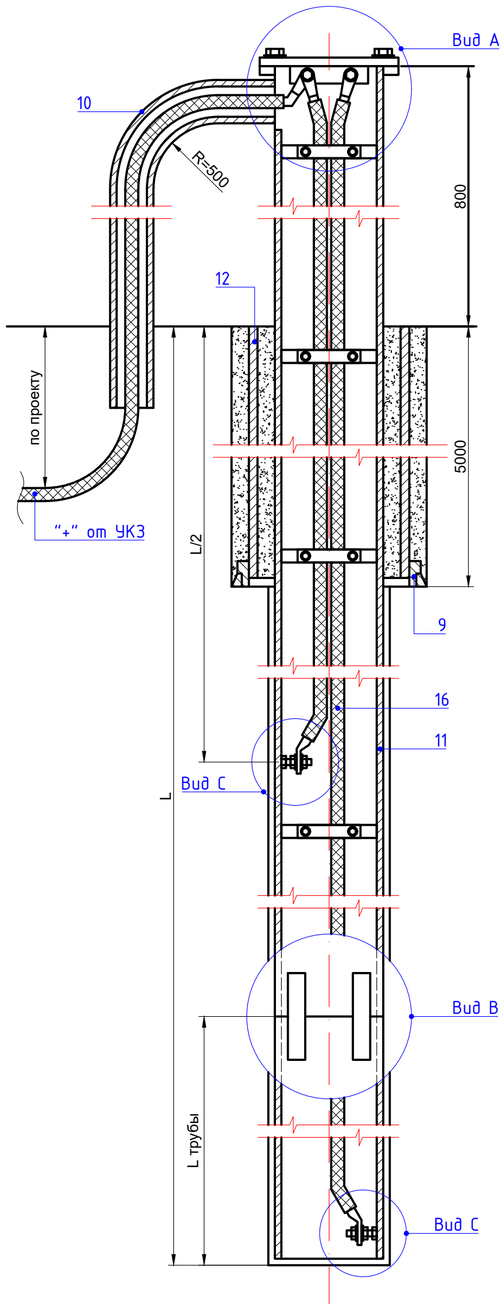


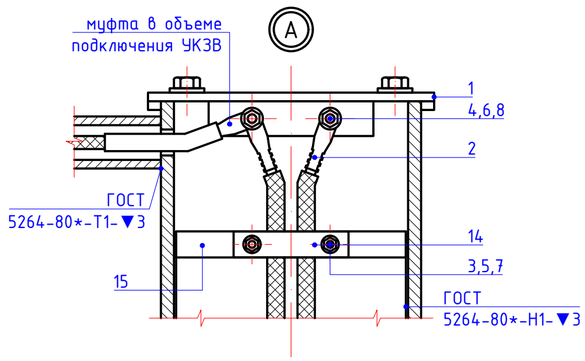

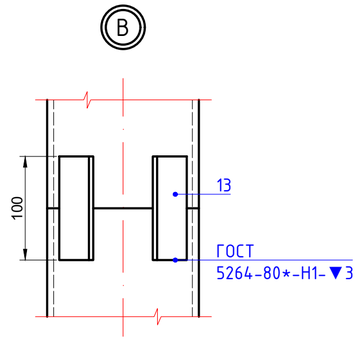


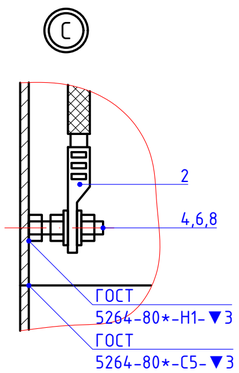

Оголовок ОГ-2

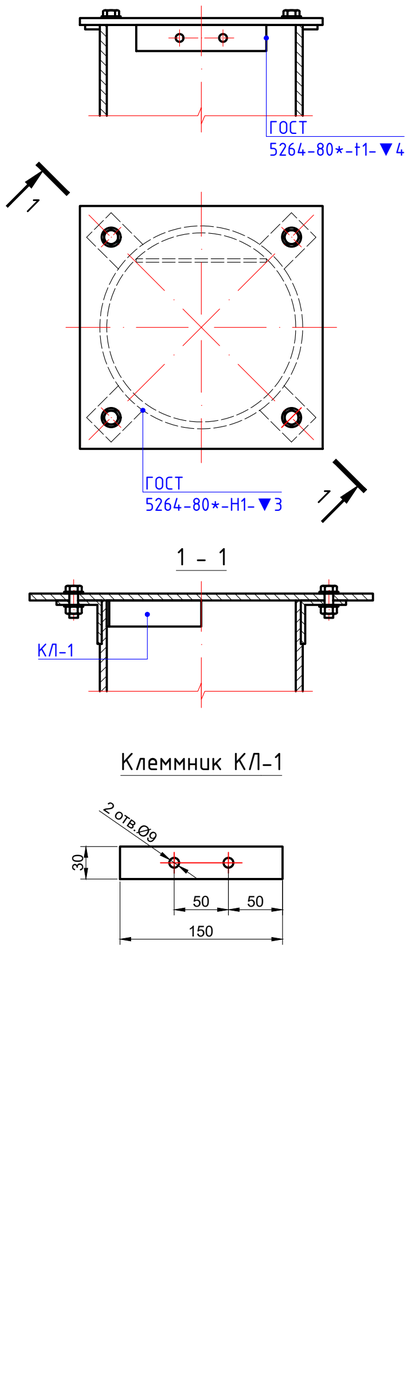

Клеммник КЛ-1

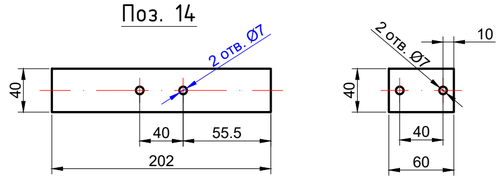

Спецификация элементов

№ п.п	Обозначение	Наименование	Ед. изм.	Кол-во	Масса кг	Примечание
		Анодный заземлитель ЭХ3.052-05				
1	ЭХ3.055	Оголовок глубинного анодного заземлителя ОГ-2	шт	1	1.27	
2	ГОСТ 9581-80*	Наконечник ТМЛ-35-8-9	шт	4	0.012	
3	ГОСТ 7798-70*	Болт М6х16.58.096	шт	24	0.006	
4	ГОСТ 7798-70*	Болт М10х30.58.096	шт	5	0.011	
5	ГОСТ 5915-70*	Гайка М65.096	шт	24	0.002	
6	ГОСТ 5915-70*	Гайка М105.096	шт	5	0.011	
7	ГОСТ 11371-78*	Шайба 6.01.09	шт	24	0.001	
8	ГОСТ 11371-78*	Шайба 10.01.09	шт	10	0.009	
9		Башмак забивной под трубу Ф377х7	шт	1	44	
10	ГОСТ 3262-75*	Труба 40х3,5	м	1,5	2,39	
11		Труба 219х8 ГОСТ 1074-76* / Д ГОСТ 1075-80*	м	75,8	29,79	
12		Труба 377х7 ГОСТ 1074-76* / Д ГОСТ 1075-80*	м	5	47,2	
13		Полоса 8х30 ГОСТ 103-76* / Ст ГОСТ 535-88*	м	3,6	47,2	
14		Полоса 4х30 ГОСТ 103-76* / Ст3 ГОСТ 535-88* L = 210	кг	31,8		
15		Полоса 4х30 ГОСТ 103-76* / Ст3 ГОСТ 535-88* L = 60	кг	9,1		
16	ГОСТ 16442-80*	Кабель силовой с медными жилами и пластмассовой изоляцией ВВГ-0,66 1х35 мм^2	м	114		уточнить по месту
17	ГОСТ 1581-78	Портландцемент тампонажный	кг	20		
18	ГОСТ 9812-74*	Битум БНИ-IV-3	кг	1		
19		Коксо-минеральный активатор среднедисперсный КМА(с)	м^3	2,735	2188	
		Оголовок ОГ-2				
1		Крышка К-2	шт	1	0.72	
2		Чеголок	шт	4	0.057	
3	Полоса 4х40 ГОСТ 103-76* / Ст ГОСТ 535-88*	Клеммник КЛ-1	шт	1	0.16	
4	ГОСТ 7798-70*	Болт М10х30.58.096	шт	4	0.031	
5	ГОСТ 5915-70*	Гайка М10.5.096	шт	4	0.011	
6	ГОСТ 11371-78*	Шайба 10.01.09	шт	8	0.004	

Примечания

Затрубное пространство заполняется коксо-минеральным активатором (КМА)
Ведомость объемов работ на ГАЗ см. документы EWE0426-MGL1-ECP-054-DRW-680120...121

Рев.	Дата	Назначение ревизии	Проверил	Утвердил
A2	25.09.2026	Утверждено для строительства		
A1	*06.09.2026*	Утверждено для строительства		
R1	13.08.2026	Выпущено для рассмотрения		

ЗАКАЗЧИК: UTG UZTRANSGAZ | ГЕНЕРАЛЬНЫЙ ПОДРЯДЧИК: UET UZBEKENERGOTAMIR | ПОДРЯДЧИК: PBG Pro Build Generation | ГЕНЕРАЛЬНЫЙ ПРОЕКТИРОВЩИК: EAST WEST ENGINEERING

EWE0426-MGL1-ECP-054-DRW-680115-A2

«СТРОИТЕЛЬСТВО НОВЫХ НИТОК (УЧАСТКОВ) ГАЗОПРОВОДОВ «ГАЗЛИ – САРИМОЙ» И «АКЧАЛОК – ГАЗЛИ – НУКУС» ОБЩЕЙ ПРОТЯЖЕННОСТЬЮ НЕ МЕНЕЕ 275 КМ».

Изм.	Кол.уч.	Лист	№док.	Подпись	Дата
ГИП		Кирпичников С.			09.2026
Провер.		Гимранов Т.			09.2026
Исполн.		Озеров В.			09.2026
Н. контр.		Кирпичников С.			09.2026

ГАЗОПРОВОД «ГАЗЛИ-САРИМОЙ» (54 КМ)

Стадия	Лист	Листов
РД	1	1

Глубинный анодный заземлитель. Сборочный чертеж. Спецификация

ООО "EAST-WEST Engineering" г. Ташкент 2026г.