

План расположения заземляющего устройства

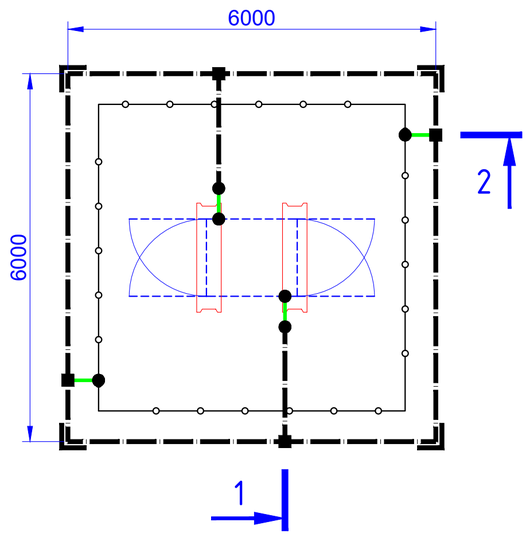


Спецификация элементов

№ п.п	Обозначение	Наименование	Ед. изм.	Кол-во	Масса кг	Примечание
1		Полоса $\frac{5x40\ ГОСТ\ 103-76*}{Ст3\ ГОСТ\ 535-88*}$	м	32		
2		Уголок $\frac{63x63x5\ ГОСТ\ 8509-93*}{Ст3\ ГОСТ\ 535-88*}$ L=5000	шт	4		
3	ПЗ-25-400	Перемычка заземляющая медная	шт	5		
4	ГОСТ 7798-70*	Болт М12х40.58.096	шт	8	0.031	
5	ГОСТ 5915-70*	Гайка М12.5.096	шт	16	0.011	
6	ГОСТ 11371-78*	Шайба 12.01.09	шт	8	0.004	
7		Рытье/обратная засыпка траншеи под горизонтальный заземлитель	$м^3$	6,3		
8		Прокладка стали полосовой в траншее	м	30		
9		Забивка вертикальных заземлителей из стали угловой в грунт	шт	5		

Разрез 1 – 1

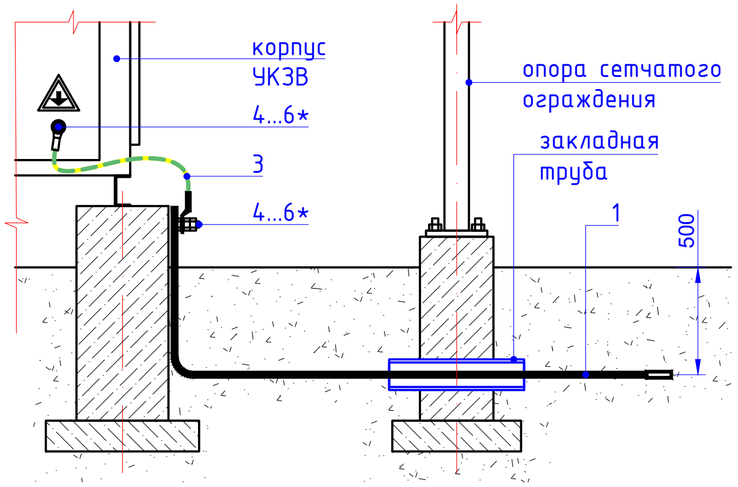

Разрез 2 – 2

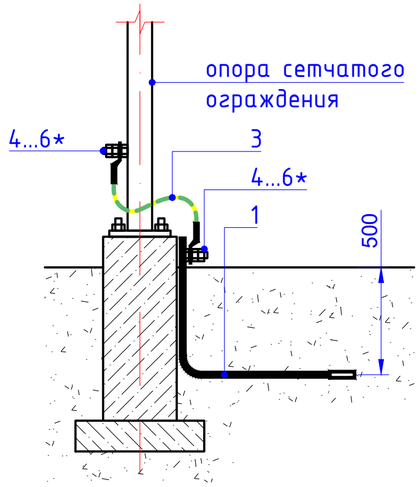

Рев.	Дата	Назначение ревизии	Проверил	Утвердил
A1	02.10.2026	Утверждено для строительства		
R1	29.09.2026	Выпущено для рассмотрения		

ЗАКАЗЧИК: UTG UZTRANSGAZ «TRANSGAZLINIXRING» ГЕНЕРАЛЬНЫЙ ПОДРЯДЧИК: UET ÖZBEKENERGOTAMIR ПОДРЯДЧИК: PBG Pro Build Generation ГЕНЕРАЛЬНЫЙ ПРОЕКТИРОВЩИК: EAST WEST ENGINEERING

Изм.	Кол.уч.	Лист	№док.	Подпись	Дата
ГИП		Кирпичников С.			10.2026
Провер.		Гимранов Т.			10.2026
Исполн.		Озеров В.			10.2026
Н. контр.		Кирпичников С.			10.2026

EWE0426-MGL1-ECP-054-DRW-680116-A1

«СТРОИТЕЛЬСТВО НОВЫХ НИТОК (УЧАСТКОВ) ГАЗОПРОВОДОВ «ГАЗЛИ – САРИМОЙ» И «АКЧАЛОК – ГАЗЛИ – НУКУС» ОБЩЕЙ ПРОТЯЖЕННОСТЬЮ НЕ МЕНЕЕ 275 КМ».

ГАЗОПРОВОД «ГАЗЛИ-САРИМОЙ» (54 КМ)

Стадия	Лист	Листов
РД	1	1

Заземляющее устройство УКЗВ

ООО "EAST-WEST Engineering"
г. Ташкент 2026г.