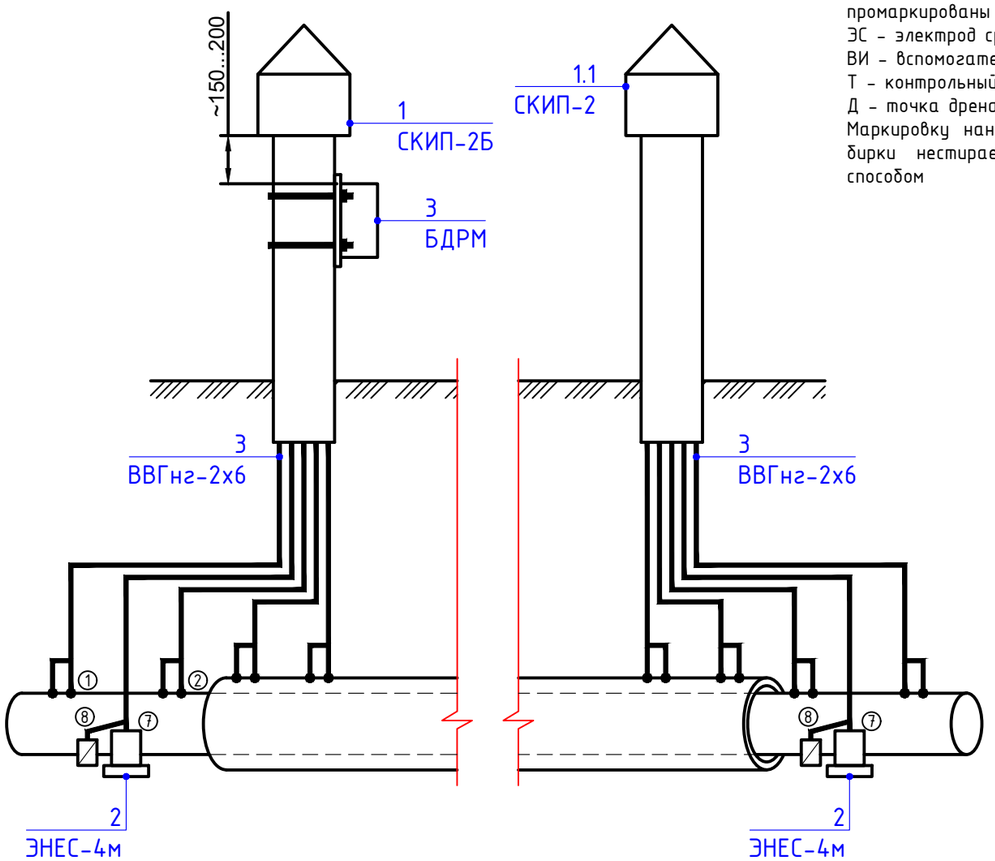


Все силовые и измерительные клеммы КИПа должны быть пронумерованы, а концы жил соединительных кабелей промаркированы следующим образом:
ЭС – электрод сравнения
ВИ – вспомогательный электрод
Т – контрольный вывод к трубопроводу
Д – точка дренажа
Маркировку наносить на маркировочные бирки нестираемым лаком либо иным способом

Спецификация элементов


№ п.п	Обозначение	Наименование	Ед. изм.	Кол-во	Масса кг	Примечание
1	СКИП-2Б-6-6-2,0 УХЛ1	Стойка контрольно-измерительного пункта, высотой 2 м., силовых клемм – 6, измерительных клемм – 6, с возможностью установки диодно-резисторного блока	шт	1	29,0	
1.1	СКИП-2-6-6-2,0 УХЛ1	Стойка контрольно-измерительного пункта, высотой 2 м., силовых клемм – 6, измерительных клемм – 6	шт	1	29,0	
2	ЭНЕС-4М	Электрод сравнения неполяризующийся медносульфатный с датчиком потенциала	шт	2	5,5	
3	БДРМ-10-2-11-К-УХЛ1	Блок диодно-резисторный	шт	1		
4	ВВГнг(А)-2х6 мм^2	Кабель силовой с медными жилами, с изоляцией и оболочкой из ПВХ пластиката, на напряжение до 1 кВ	м	24		
5	ТУТ-12/6	Трубка термоусаживаемая на напряжение до 1 кВ	м	2		
6	ТМЛ 6-6-4	Наконечник медный луженый на кабель сечением 6 мм^2	шт	16		

Примечания:
1. Провод от электрода сравнения до клеммных зажимов КИПа входит в комплект поставки электрода сравнения
2. На период производства измерений электроизолирующих свойств на изолирующей вставке клеммы 2-8 и 4-10 размыкаются


(*) Установить съемные перемычки между клеммами датчика потенциала (вспомогательного электрода) и клеммами кабелей, присоединенных к трубопроводу. На период производства замеров поляризационных потенциалов перемычки снимаются.
(**) Не менее 3х диаметров трубопровода

При установке СКИПов с обеих сторон кожуха установка БДРМ для регулировки защитного тока производится только с одной стороны

Схема подключения клеммных терминалов КИП

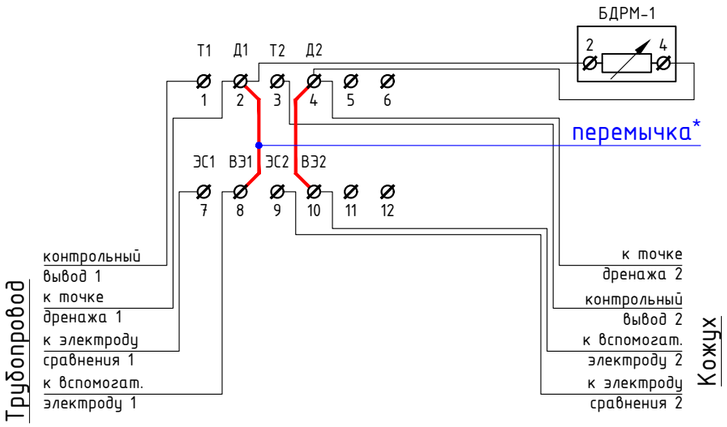

Эскиз установки электрода сравнения

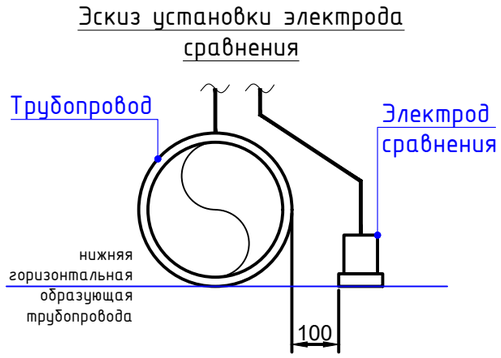

Рев.	Дата	Назначение ревизии	Проверил	Утвердил
A1	25.09.2026	Утверждено для строительства		
R1	13.08.2026	Выпущено для рассмотрения		

ЗАКАЗЧИК: UTG UZTRANSGAZ | ГЕНЕРАЛЬНЫЙ ПОДРЯДЧИК: UET UZBEKENERGOTAMIR | ПОДРЯДЧИК: PBG Pro Build Generation | ГЕНЕРАЛЬНЫЙ ПРОЕКТИРОВЩИК: EAST WEST ENGINEERING

Изм.	Кол.уч.	Лист	№док.	Подпись	Дата
ГИП		Кирпичников С.			09.2026
Провер.		Гимранов Т.			09.2026
Исполн.		Озеров В.			09.2026
Н. контр.		Кирпичников С.			09.2026

EWE0426-MGL1-ECP-054-DRW-680124-A1

«СТРОИТЕЛЬСТВО НОВЫХ НИТОК (УЧАСТКОВ) ГАЗОПРОВОДОВ «ГАЗЛИ – САРИМОЙ» И «АКЧАЛОК – ГАЗЛИ – НУКУС» ОБЩЕЙ ПРОТЯЖЕННОСТЬЮ НЕ МЕНЕЕ 275 КМ».

ГАЗОПРОВОД «ГАЗЛИ-САРИМОЙ» (54 КМ)

Стадия	Лист	Листов
РД	1	1

Установка контрольно-измерительного прибора на трубопроводе и защитном кожухе

EAST WEST ENGINEERING
ООО "EAST-WEST Engineering"
г. Ташкент 2026г.