Схема расположения фундаментов

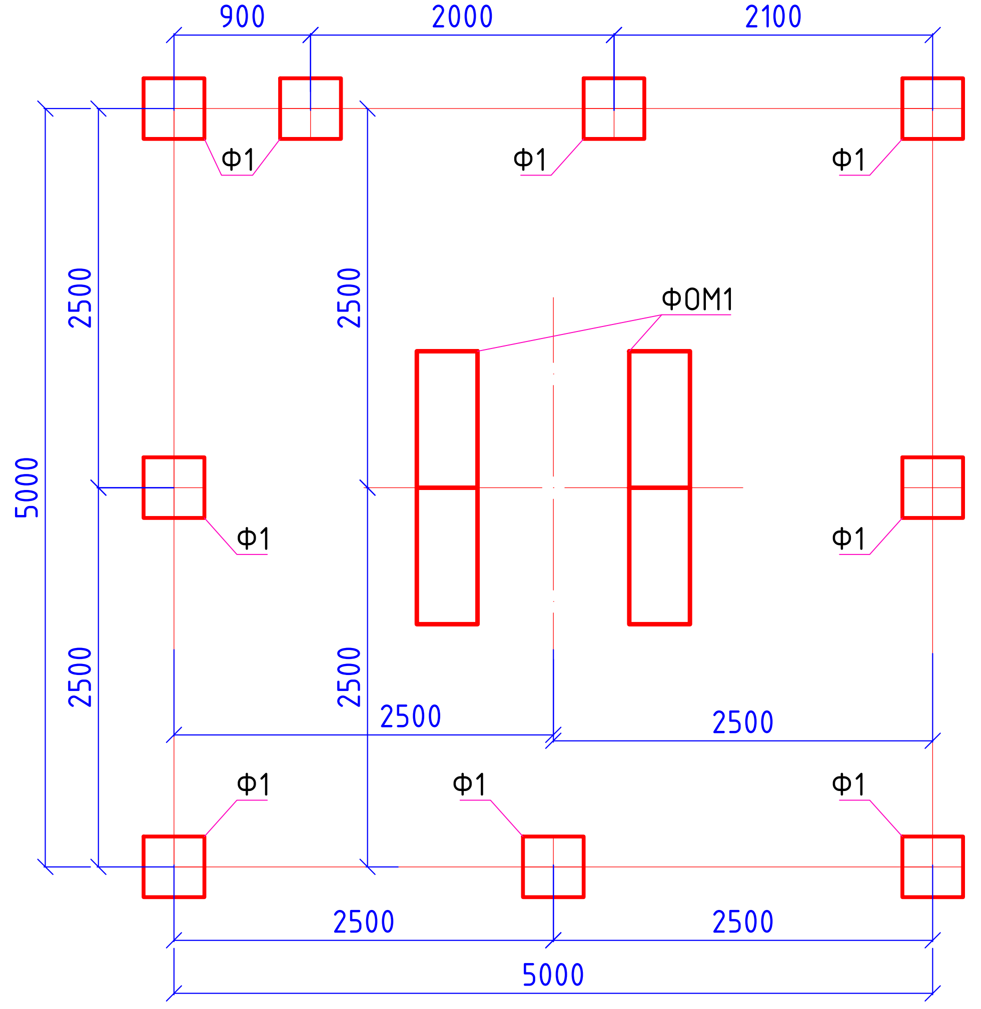

Фундамент ФОМ1

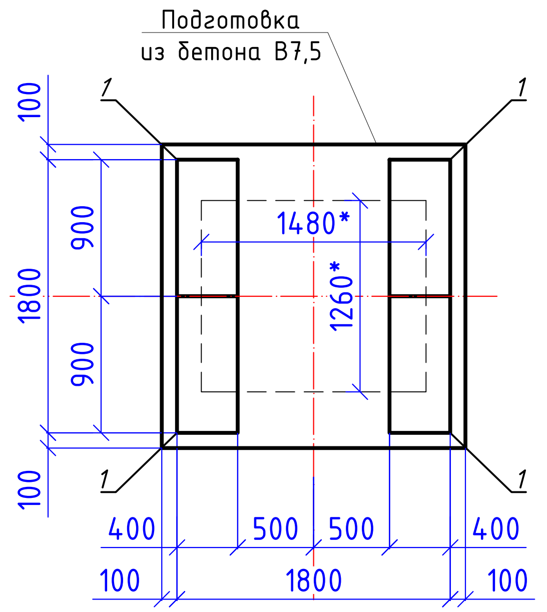

1 – 1

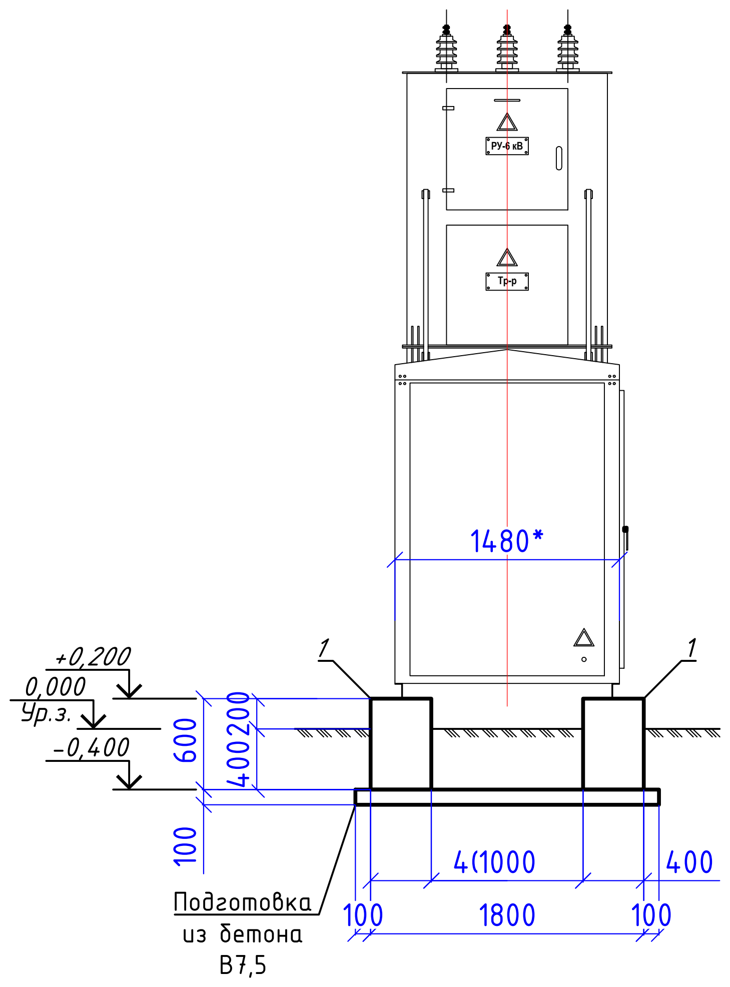

2 – 2

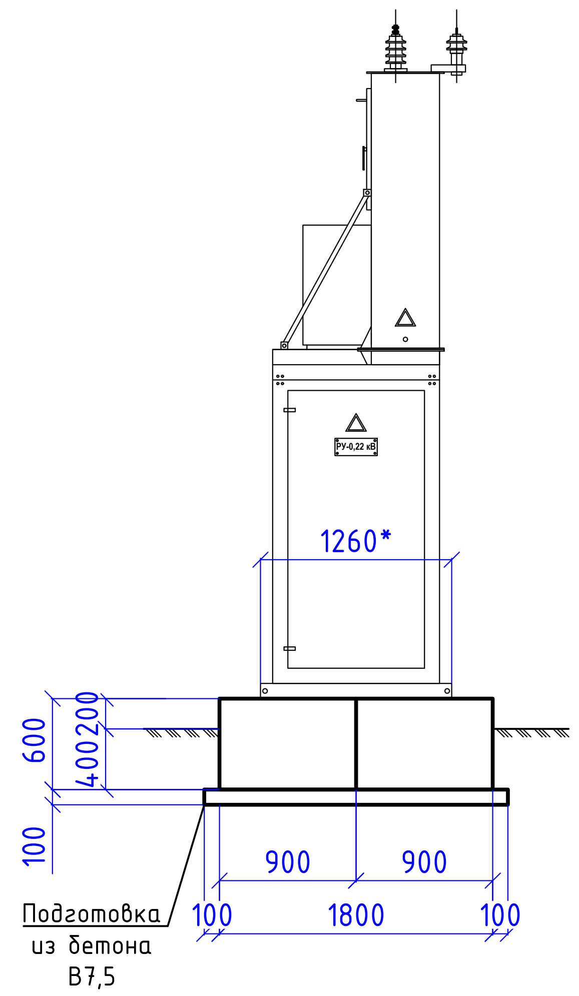

Фундамент Ф1

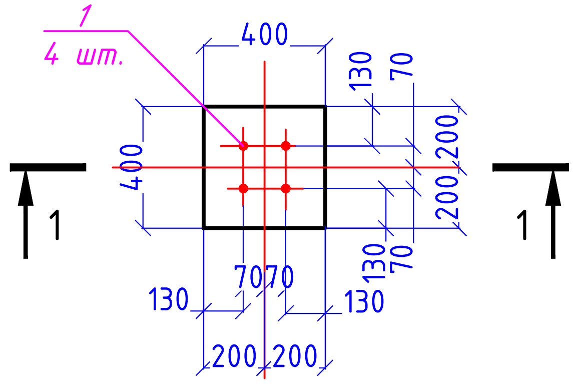

1 – 1

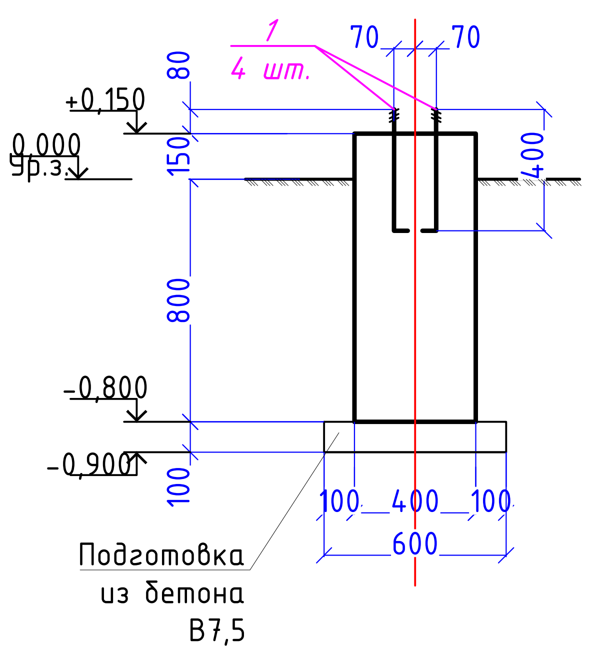

Спецификация элементов

№ п.п	Обозначение	Наименование	Ед. изм.	Кол -во	Масса кг	Примечание
		Фундамент Ф1				расход на 1 ед.
1	ГОСТ 24379.1-2012	Болт1.1. М12х400 ВСт3кп	шт	4	0,44	
		Материалы				
2		Бетон кл. В15 F50 W8	$м^3$	0,152		
3		Подготовка из бетона В7,5	$м^3$	0,04		
4		Гидроизоляция фундамента	$м^2$	1,64		
		Фундамент ФОМ1				
1	ГОСТ 13579-2018	ФБС 9.4.6-Т	шт	4		
		Материалы				
2		Подготовка из бетона В7,5	$м^3$	0,4		
3	ГОСТ 28778-90	Распорный болт М16х150	шт	4	0.192	
4		Гидроизоляция фундамента	$м^2$	8,16		

Примечания:

Антикоррозионную защиту боковых поверхностей железобетонных конструкций, соприкасающихся с грунтом, а также верха бетонной подготовки выполнить путем нанесения двух слоев полимерного покрытия на основе лака ХП-734 в два слоя по ГОСТ 52165-2003 толщиной 25 мкм.

Крепление оборудования к ФБС выполнить с помощью болтов типа БСР М16х150.

Рев.	Дата	Назначение ревизии	Проверил	Утвердил
A1	02.10.2026	Выпущено для рассмотрения		
R1	29.09.2026	Выпущено для рассмотрения		

ЗАКАЗЧИК: UTG UZTRANSGAZ «TRANSGAZINJINIRING»
ГЕНЕРАЛЬНЫЙ ПОДРЯДЧИК: UET UZBEKENERGOTAMIR
ПОДРЯДЧИК: PBG Pro Build Generation
ГЕНЕРАЛЬНЫЙ ПРОЕКТИРОВЩИК: EAST WEST ENGINEERING

EWE0426-MGL1-ECP-054-DRW-680125-A1

«СТРОИТЕЛЬСТВО НОВЫХ НИТОК (УЧАСТКОВ) ГАЗОПРОВОДОВ «ГАЗЛИ – САРИМОЙ» И «АКЧАЛОК – ГАЗЛИ – НУКУС» ОБЩЕЙ ПРОТЯЖЕННОСТЬЮ НЕ МЕНЕЕ 275 КМ».

Изм.	Кол.уч.	Лист	№док.	Подпись	Дата
ГИП		Кирпичников С.			10.2026
Провер.		Гимранов Т.			10.2026
Исполн.		Озеров В.			10.2026
Н. контр.		Кирпичников С.			10.2026

ГАЗОПРОВОД «ГАЗЛИ-САРИМОЙ» (54 КМ)

Стадия	Лист	Листов
РД	1	1

Схема расположения фундаментов для УКЗВ. Спецификация

EAST WEST ENGINEERING
ООО "EAST-WEST Engineering"
г. Ташкент 2026г.