Структура условного обозначения УКЗВ при его заказе

УКЗВ-А-6-3,0-1-УХЛ1-БДРМ-В

Модель устр-ва	Регулировка устройства	Напряжение сети, кВ	Выходная мощность, кВ	Количество станций КЗ, шт	Климатическое исполнение	Комплектация блоком БАР или БСЗ (БДРМ)	Присоединение к питающей линии (верхний/нижний ввод)
УКЗВ-	А	6	3,0	1	УХЛ1	БДРМ	В

№ п.п	Наименование параметра	Значение параметра	Примечание
1	Количество комплектов УКЗВ, шт	3	
2	Мощность силового трансформатора, кВА	6,3	
3	Номинальное напряжение на высокой стороне, кВ	6,3	
4	Номинальное напряжение на низкой стороне, кВ	0,23	
5	Количество фаз питающей сети, шт	1	
6	Частота питающей сети, Гц	50	
7	Условие обслуживания главных цепей	одностворонее	
8	Условие обслуживания вторичных цепей	одностворонее	
9	Расположение кабельных вводов	снизу	
10	Исполнение контейнера	антивандальное	
11	Степень защиты оболочки	IP54	
12	Тип выпрямителя	ИПКЗ-М-РА-3,0	
13	Мощность выпрямителя, кВт	3,0	
14	Способ управления	автоматический, ручной	
15	Диапазоны регулировки выходных параметров СКЗ		
16	– по току, А (в режиме I / режиме II)	0…48 / 0…	
17	– по напряжению, В (в режиме I / режиме II)	0…48 / 0…98	
18	Диапазон регулировки суммарного потенциала, В	– (0,5 … 3,5)	
19	Диапазон регулировки поляризационного потенциала, В	– (0,8 … 1,2)	
20	Модуль защиты от импульсных перенапряжений	да	
21	Тип системы телемеханики	согласовать с заказчиком	
22	Протокол обмена данными с системой телемеханики	ModBUS RTU	см. прим.
23	Интерфейс связи с системой телемеханики	RS485/USB	см. прим.
24	Устройство связи	3G/4G/GSM/GPRS-модем	см. прим.
25	Интерфейс связи	RS485	см. прим.
26	Учет электроэнергии	да, Энергомера CE207 R7 230В, 10(100)А 0,5S	или аналог

Габаритные чертеж УКЗВ. Вид спереди

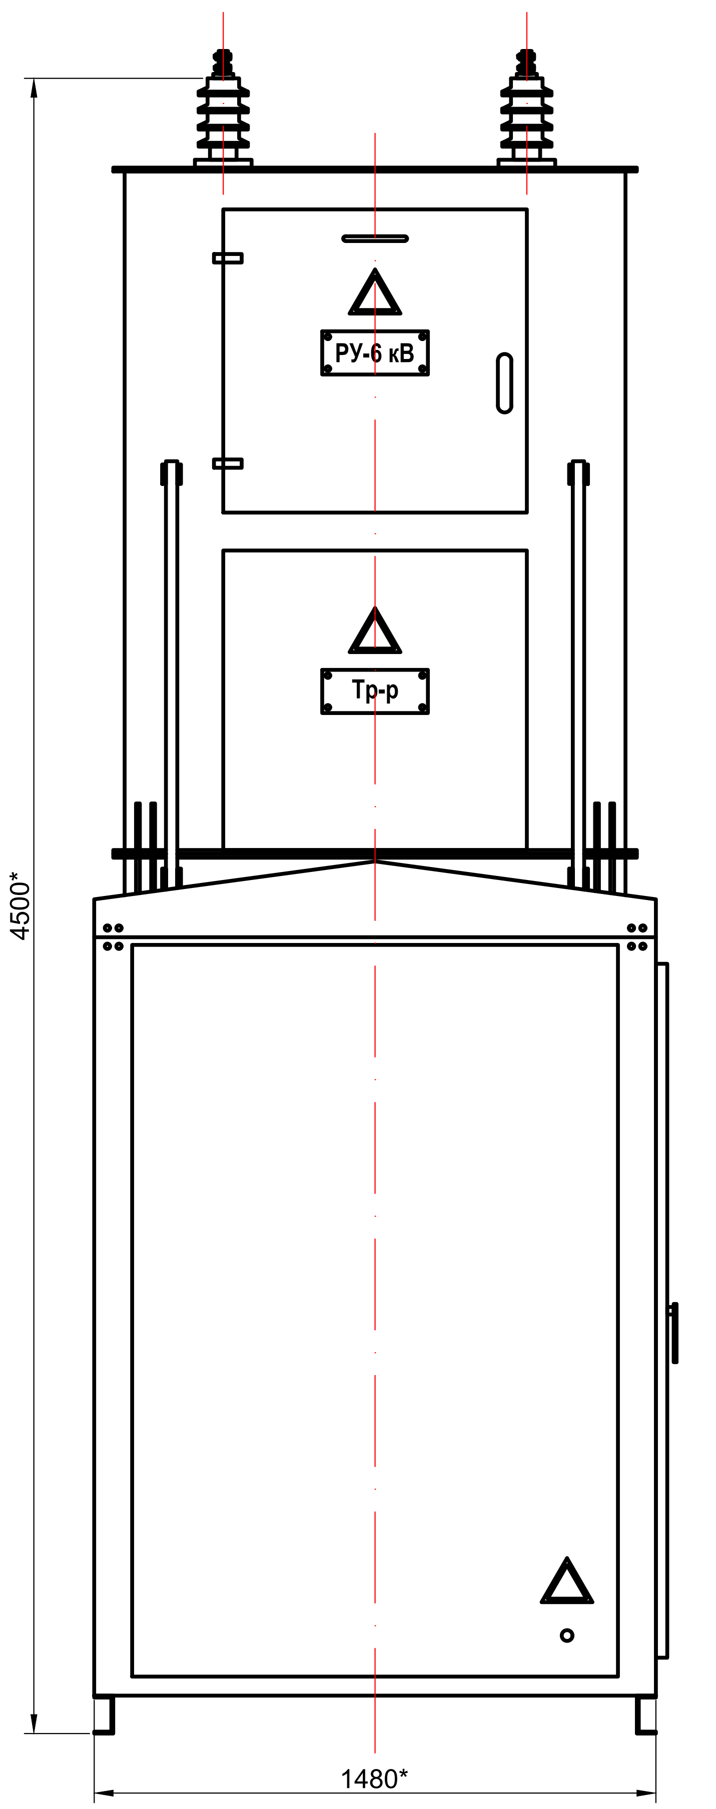

Габаритные чертеж УКЗВ. Вид сбоку

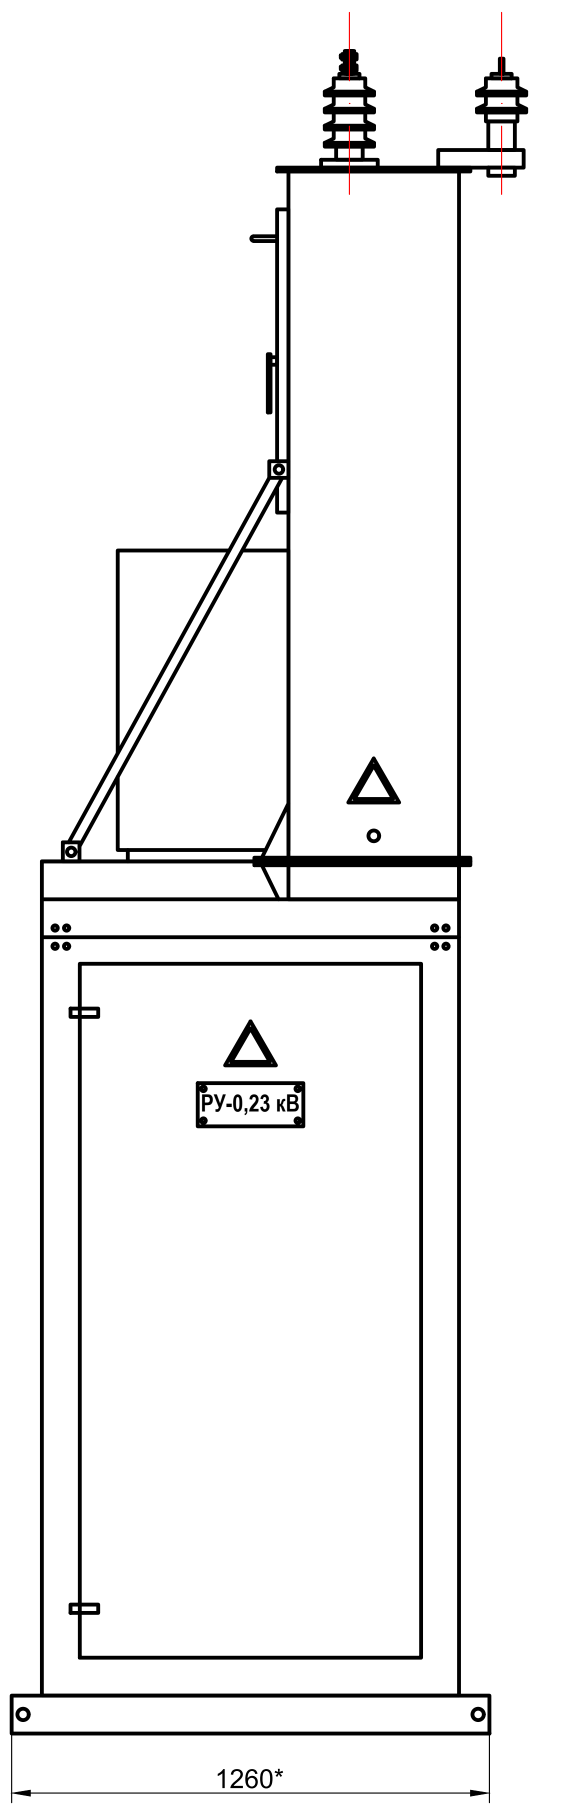

Примечания:

(*) Размеры приведены для справки. Конкретные размеры необходимо уточнить у конечного Поставщика

Окраска всех элементов КТП, нанесение корпоративных, информационных надписей и знаков безопасности КТП выполняется в соответствии с Правилами устройства электроустановок, ГОСТ 12.4.026-76 и внутренними регламентами Заказчика. Корпоративные и информационные знаки должны наноситься таким образом, чтобы не затруднять восприятие друг друга.

Устройства и интерфейс связи с системами АСУЭ и АСКУЭ принять по типу существующих на участке устройств катодной защиты. Конкретные тип и системы связи определить совместно с эксплуатирующей организацией.

Совместную работу с устройством телемеханики обеспечить через оптический интерфейс по протоколу Modbus TCP.
Для подключения оптического одномодового кабеля Заказчика (Fiber Optic Single Mode) предусмотреть в шкафу УКЗВ оптический кросс. SFP-модуль предусматривает Заказчик.

Рев.	Дата	Назначение ревизии	Проверил	Утвердил
A3	02.10.2026	Утверждено для строительства		
A2	22.09.2026	Утверждено для строительства		
A1	06.08.2026	Утверждено для строительства		
R1	13.08.2026	Выпущено для рассмотрения		

ЗАКАЗЧИК: UTG UZTRANSGAZ «TRANSGAZINJINIRING»
ГЕНЕРАЛЬНЫЙ ПОДРЯДЧИК: UET UZBEKENERGOTAMIR
ПОДРЯДЧИК: PBG Pro Build Generation
ГЕНЕРАЛЬНЫЙ ПРОЕКТИРОВЩИК: EAST WEST ENGINEERING

EWE0426-MGL1-ECP-054-DSH-680122-A3

«СТРОИТЕЛЬСТВО НОВЫХ НИТОК (УЧАСТКОВ) ГАЗОПРОВОДОВ «ГАЗЛИ – САРИМОЙ» И «АКЧАЛОК – ГАЗЛИ – НУКУС» ОБЩЕЙ ПРОТЯЖЕННОСТЬЮ НЕ МЕНЕЕ 275 КМ».

Изм.	Кол.уч.	Лист	№док.	Подпись	Дата
ГИП		Кирпичников С.			10.2026
Провер.		Гимранов Т.			10.2026
Исполн.		Озеров В.			10.2026
Н. контр.		Кирпичников С.			10.2026

ГАЗОПРОВОД «ГАЗЛИ-САРИМОЙ» (54 КМ)

Стадия	Лист	Листов
РД	1	1

Опросной лист на устройство распределительное катодной защиты

EAST WEST ENGINEERING
ООО "EAST-WEST Engineering"
г. Ташкент 2026г.