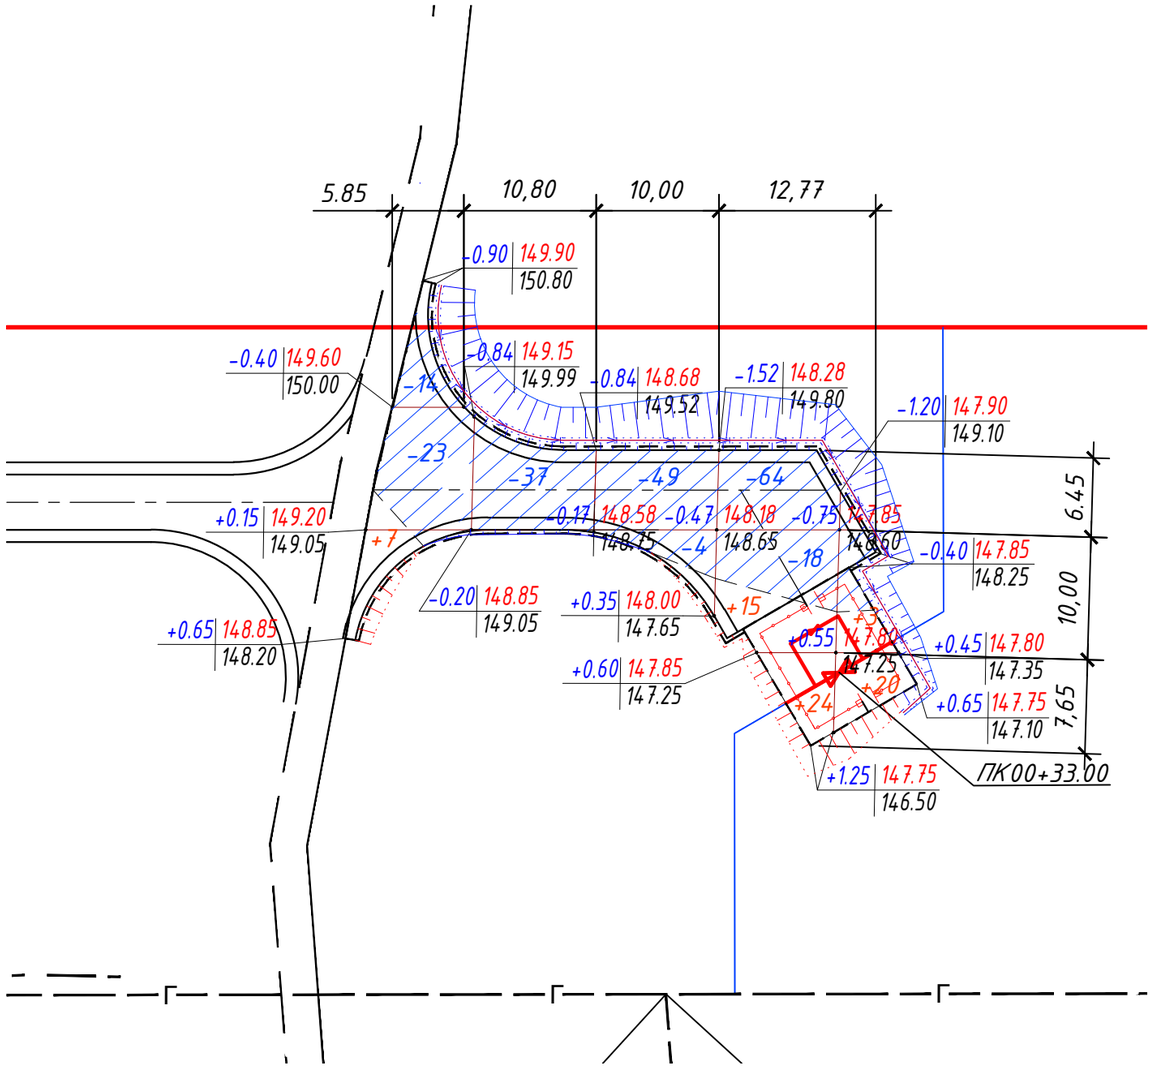


Итого,м3							Всего,м3	
	Насыпь (+)	+7	--	--	+15	+23		+45
	Выемка (-)	-37	-37	-53	-82	--		-209

Примечания:

При составлении настоящего чертежа были использованы :
1. Сетка картограммы привязана линейно к пикету ПК 00+33.00.
2. Сетка квадратов объёмы земляных масс разбита на ячейки размерами 10х10м.
3. Производство земляных работ вести в соответствии с требованиями КР 02.01.

Условные обозначения:

+104	объем насыпи в м³
+1.68 | 146.41 / 144.73	рабочая отм. | проектная отм. / отм.сущ.рельефа
-3	объем выемки в м³
	откосы насыпи
	откосы выемки

Ведомость объемов земляных масс

Наименование грунта	Количество, м³		Примечание
	Насыпь (+)	Выемка (-)	
1. Грунт планировки территории	45	209	
2. Вытесненный грунт, в т.ч. при устройстве:			
а) автодорожных покрытий		135	
б) покрытий площадок		9	
в) водоотводной канавы		32	
г) плодородной почвы на участках насыпи			
д) плодородной почвы на участках выемки			
3. Замена растительного грунта на участках насыпи			
4. Грунт для устройства откосов насыпи	10		
5. Грунт для устройства откосов выемки		20	
6. Поправка на уплотнение	5.5		
Всего пригодного грунта	60.5	405	
7. Избыток пригодного грунта	344.5		
8. Плодородный грунт, всего в т.ч.:		159	
а) Используемый для озеленения территории			
б) Избыток плодородного грунта	159		
(рекультивация земель)			
9. Итого перерабатываемого грунта	564	564	

* С учетом плодородного грунта.
** В карьере. Общая площадь картограммы = 530 м2

Рев.	Дата	Назначение ревизии	Проверил	Утвердил
A1	04.09.2026	Выпущено для строительства		
R1	28.07.2026	Выпущено для рассмотрения		

ЗАКАЗЧИК: UTG UZTRANSGAZ | ГЕНЕРАЛЬНЫЙ ПОДРЯДЧИК: UET UZBEKENERGOTAMIR | ПОДРЯДЧИК: PBG Pro Build Generation | ГЕНЕРАЛЬНЫЙ ПРОЕКТИРОВЩИК: EAST WEST ENGINEERING

Изм.	Кол.уч.	Лист	№док.	Подпись	Дата
ГИП		Схабицкий А.			09.2026
Нач.отд.		Нигманова Н.			09.2026
Исполн.		Нигманова Н.			09.2026
Н.контр		Схабицкий А.			09.2026

EWE0426-MGL1-GLT-054-DRW-750104-A1

«СТРОИТЕЛЬСТВО НОВЫХ НИТОК (УЧАСТКОВ) ГАЗОПРОВОДОВ «ГАЗЛИ - САРИМОЙ» И «АКЧАЛОК - ГАЗЛИ - НУКУС» ОБЩЕЙ ПРОТЯЖЕННОСТЬЮ НЕ МЕНЕЕ 275 км».

ГАЗОПРОВОД «ГАЗЛИ-САРИМОЙ» (54 км)

Генеральный план и транспорт.

Стадия	Лист	Листов
РД	1	1

КУП-D6.
План земляных масс М 1:500

ООО "EAST-WEST Engineering" г. Ташкент 2026 г.

Взам. инв.№ | Подпись и дата | Инв. № подл

Формат / Format A3