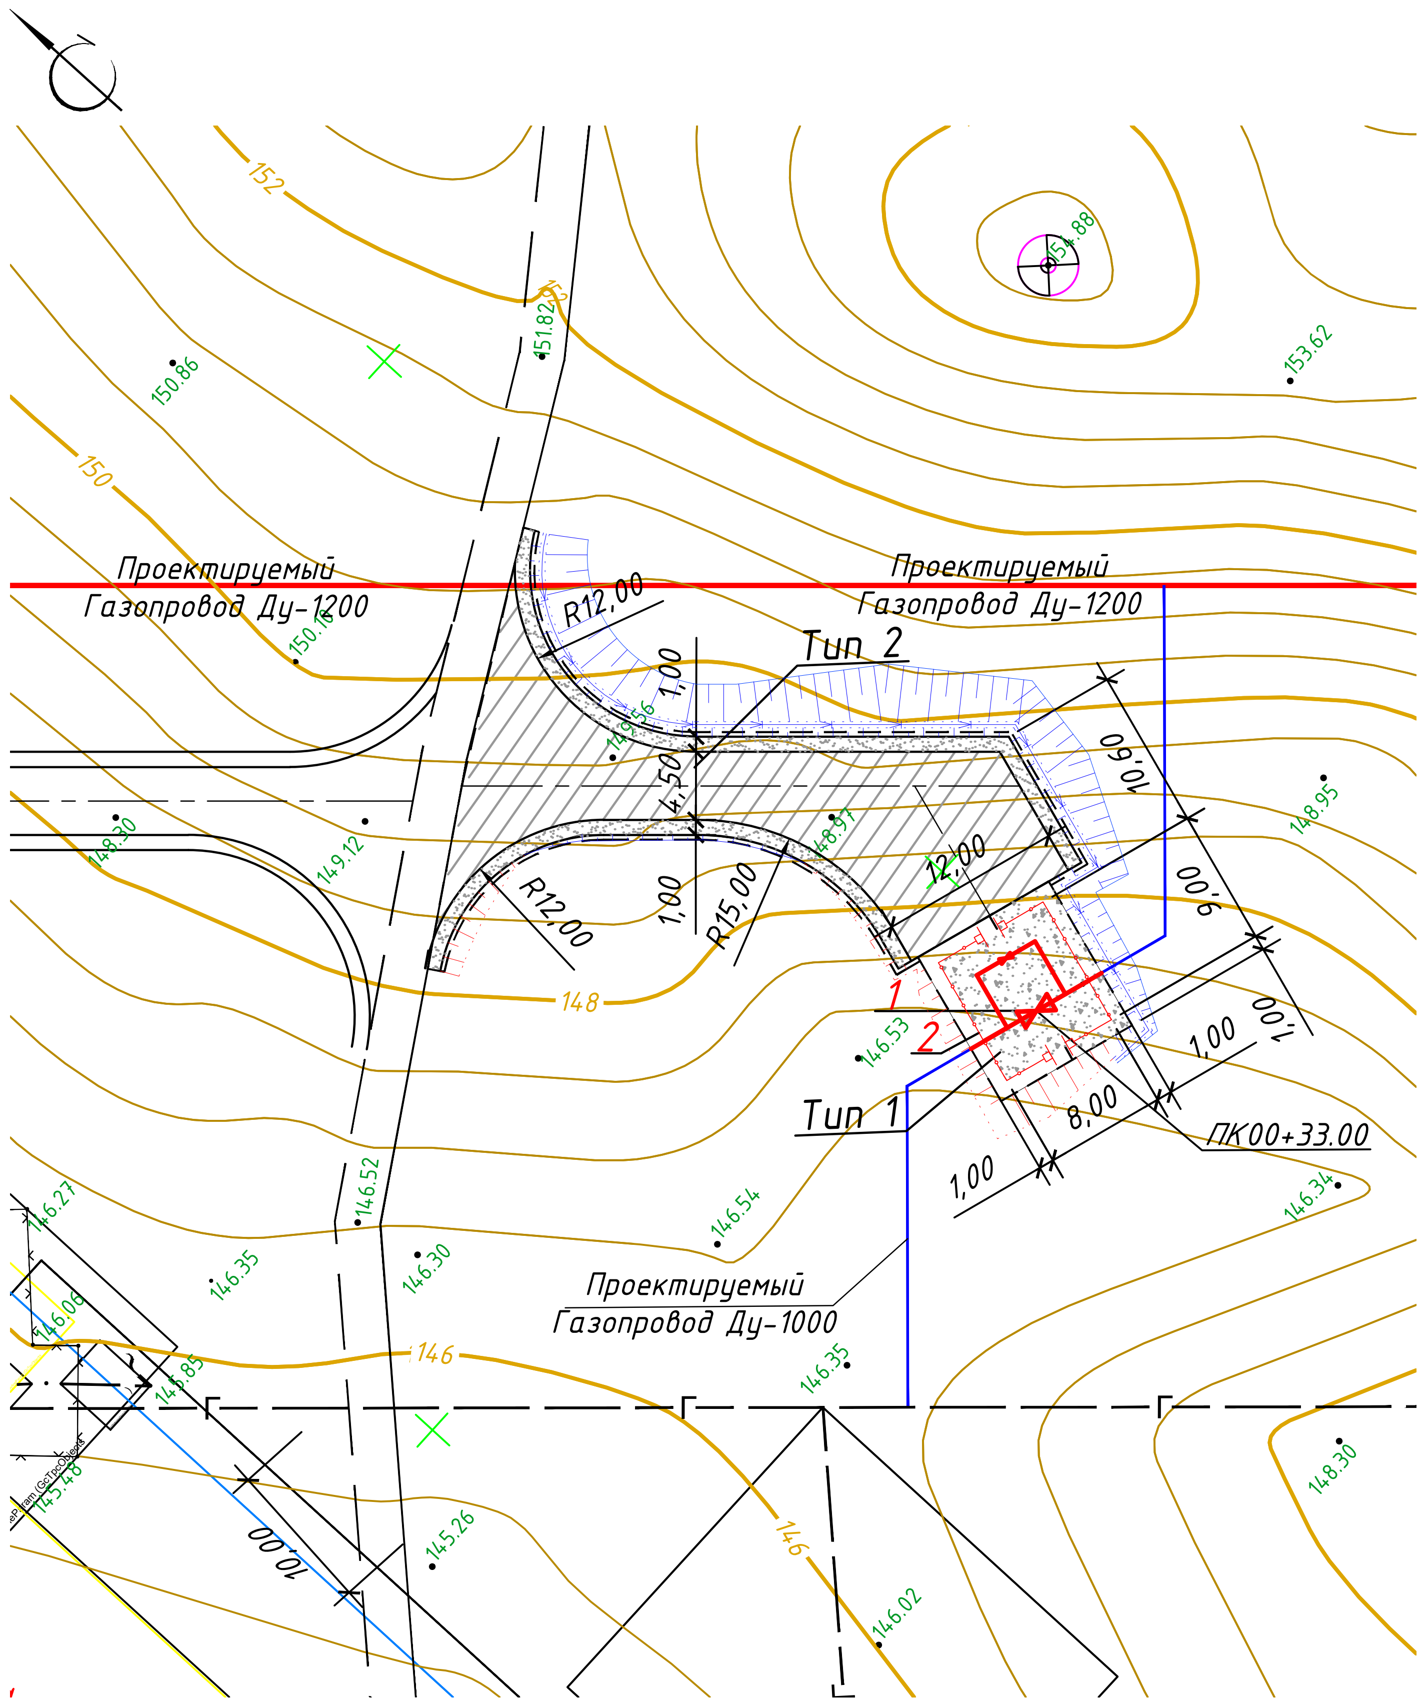
152
150
148
146
151.82
150.86
154.88
153.62
150.16
149.56
148.97
148.95
148.30
149.12
146.53
146.54
146.34
146.27
146.35
146.52
146.30
146.06
145.85
145.48
146.35
145.26
146.02
148.30
Проектируемый
Газопровод Ду-1200
Проектируемый
Газопровод Ду-1200
Проектируемый
Газопровод Ду-1000
R12,00
R12,00
R15,00
1,00
4,50
1,00
12,00
10,60
9,00
1,00
1,00
8,00
1,00
10,00
Тип 2
Тип 1
1
2
ПК00+33.00

Тип 1

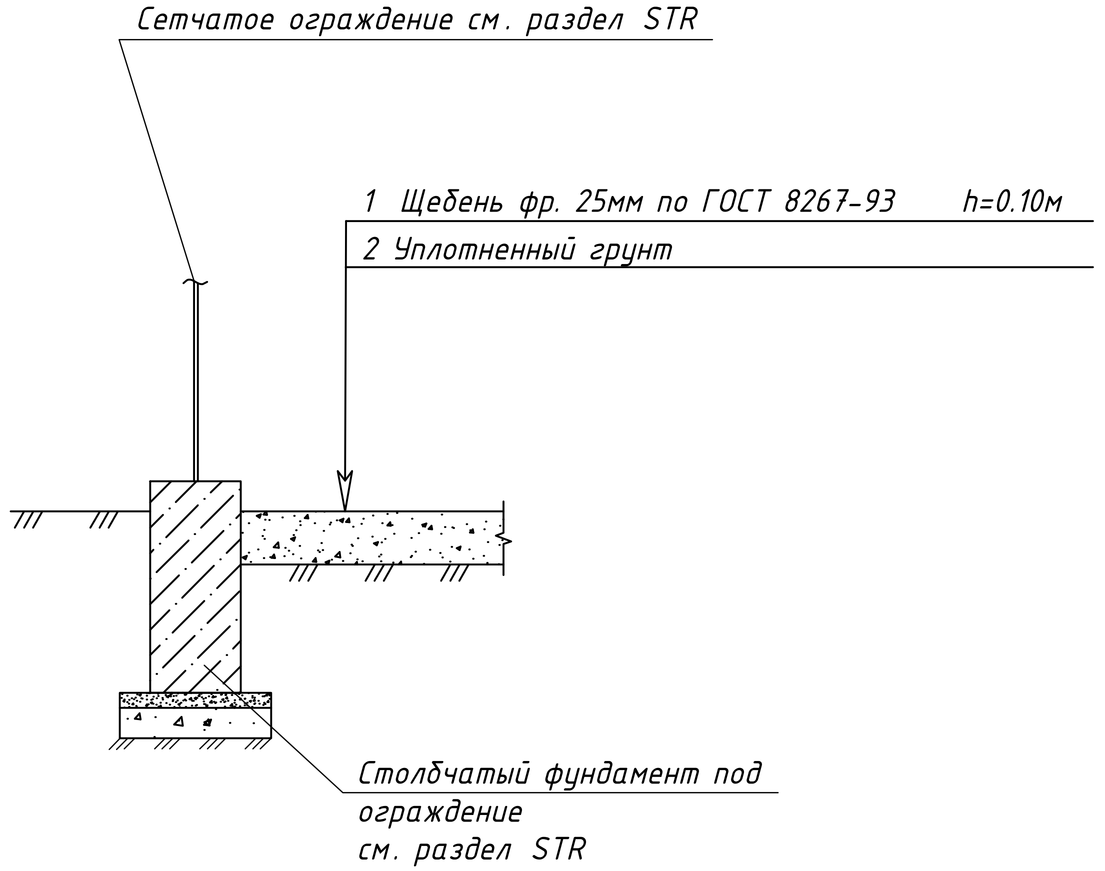
Сетчатое ограждение см. раздел STR
1 Щебень фр. 25мм по ГОСТ 8267-93 h=0.10м
2 Уплотненный грунт
Столбчатый фундамент под ограждение см. раздел STR

Тип 2

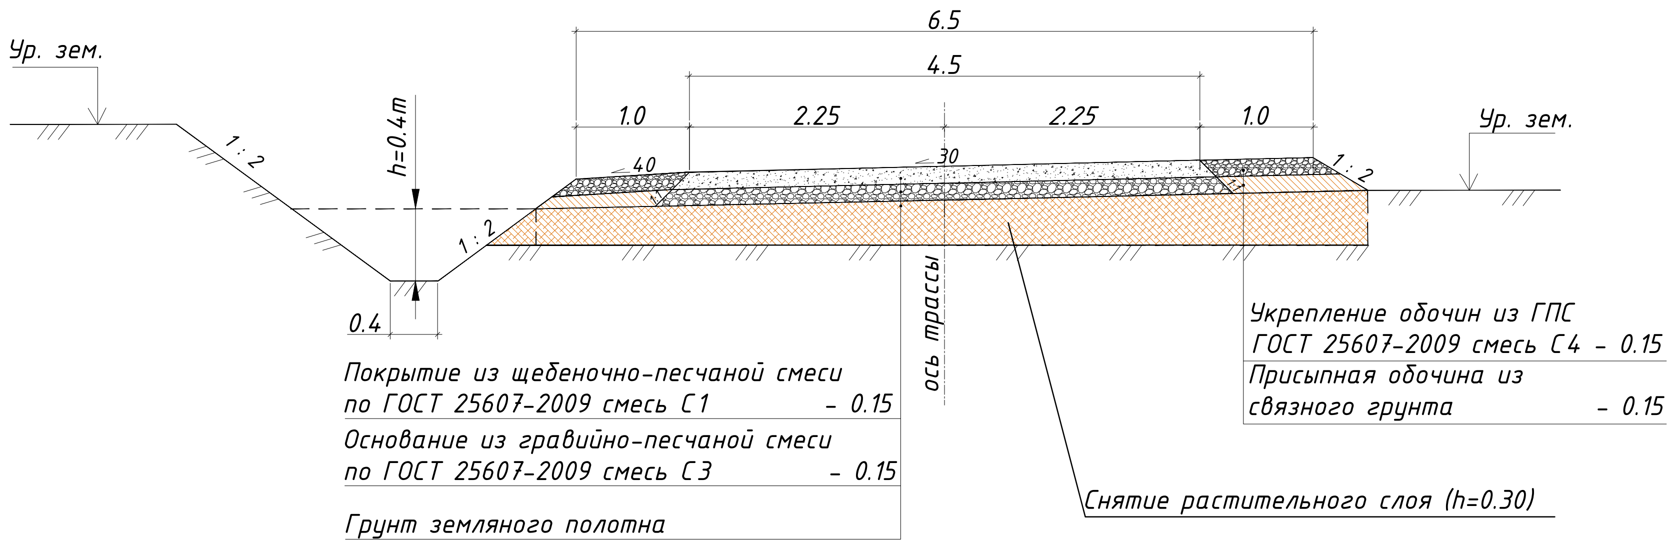
6.5
4.5
1.0
2.25
2.25
1.0
40
30
1 : 2
1 : 2
1 : 2
h=0.4m
0.4
Ур. зем.
Ур. зем.
ось трассы

Покрытие из щебеночно-песчаной смеси по ГОСТ 25607-2009 смесь С1 – 0.15

Основание из гравийно-песчаной смеси по ГОСТ 25607-2009 смесь С3 – 0.15

Грунт земляного полотна

Укрепление обочин из ГПС ГОСТ 25607-2009 смесь С4 – 0.15

Присыпная обочина из связного грунта – 0.15

Снятие растительного слоя (h=0.30)

Экспликация зданий и сооружений

Номер на плане	Наименование	Примечание
1	Крановый узел Ду 1000	
2	Ограждение сетчатое	

Ведомость тротуаров, дорожек и площадок

Тип	Обозначение	Наименование	Ед. изм.	Примечание
		Покрытие площадки		
1	▨	Покрытие из щебня по ГОСТ 8267-93, h=0.10	м²	90
		Покрытие проездов		
2	▨	Покрытие из щебеночно-песчаной смеси по ГОСТ 25607-2009 смесь С1 h=0,15 м Основание из гравийно-песчаной смеси по ГОСТ 25607-2009 смесь С3 h=0,15 м	м²	350.0
		Укрепление обочин из ГПС ГОСТ 25607-2009 смесь С4 h=0,15 м	м²	100.0

Примечания:

При составлении настоящего чертежа были использованы :
1. Материалы топографо-геодезической съемки, предоставлены АО "O'ZLITINEFTGAZ".
2. Система координат местная. Высотные отметки даны в Балтийской системе.
3. Размеры даны в метрах.
4. Площадка кранового узла КУП-D6 привязана линейно к пикету ПК 00+33.00.
5. Данный лист смотри совместно с листами разделов PIL, PRE, ELE, STR, SYS.
6. Детальный план кранового узла см. EWE0426-MGL1-PRE-054-DRW-750203.

Взам. инв. №
Подпись и дата
Инв.№ подл.

Рев.	Дата	Назначение ревизии	Проверил	Утвердил
A2	07.10.2026	Выпущено для строительства		
A1	04.09.2026	Выпущено для строительства		
R1	28.07.2026	Выпущено для рассмотрения		

ЗАКАЗЧИК: UTG UZTRANSGAZ
ГЕНЕРАЛЬНЫЙ ПОДРЯДЧИК: UET UZBEKENERGOTAMIR
ПОДРЯДЧИК: PBG Pro Build Generation
ГЕНЕРАЛЬНЫЙ ПРОЕКТИРОВЩИК: EAST WEST ENGINEERING

EWE0426-MGL1-GLT-054-DRW-750106-A2

«СТРОИТЕЛЬСТВО НОВЫХ НИТОК (УЧАСТКОВ) ГАЗОПРОВОДОВ «ГАЗЛИ – САРИМОЙ» И «АКЧАЛОК – ГАЗЛИ – НУКУС» ОБЩЕЙ ПРОТЯЖЕННОСТЬЮ НЕ МЕНЕЕ 275 км».

Изм.	Кол.уч.	Лист	№ док.	Подпись	Дата
ГИП		Кирпичников С.			10.2026
Нач.отд.		Нигманова Н.			10.2026
Исполн.		Нигманова Н.			10.2026
Н.контр		Кирпичников С.			10.2026

ГАЗОПРОВОД «ГАЗЛИ-САРИМОЙ» (54 км)
Генеральный план и транспорт.

Стадия	Лист	Листов
РД	1	1

КУП-D6.
План благоустройства территории
М 1:500

EAST WEST ENGINEERING
ООО "EAST-WEST Engineering"
г. Ташкент 2026 г.

Формат / Format A4x3