
Линейный крановый узел КУП-D6.
План 1 (1:50)

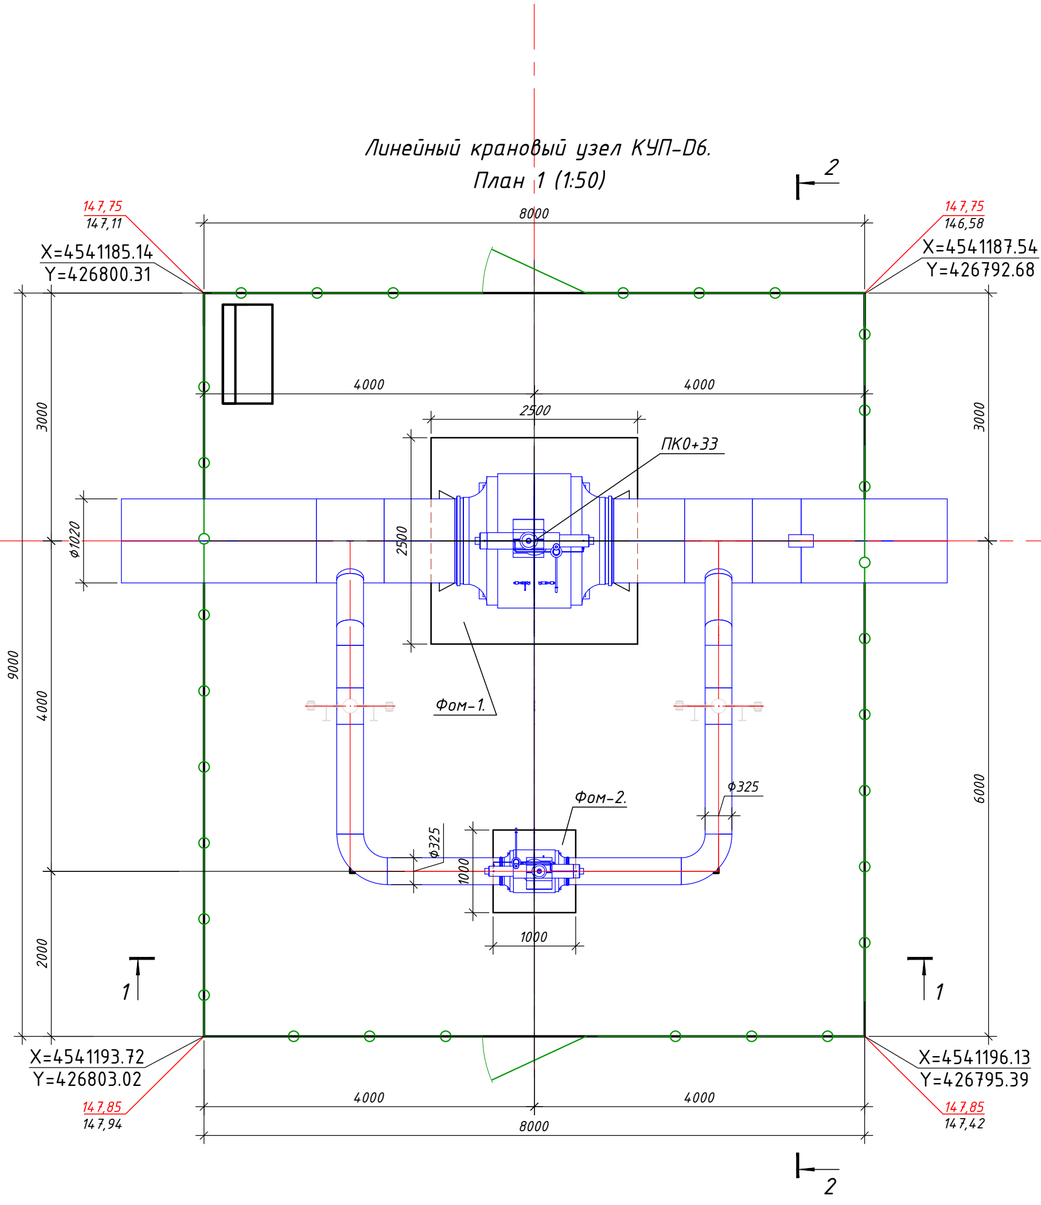

Спецификация элементов

Марка Поз.	Обозначение	Наименование	Кол. шт.	Масса ед.кг	Примеч.
		Линейный крановый узел КУП-D6.			
Фом-1	EWE0426-MGL1-STR-054-DRW-750504	Фундамент оборудования, монолитный Фом-1	1		
Фом-2	EWE0426-MGL1-STR-054-DRW-750505	Фундамент оборудования, монолитный Фом-2	1		

Внимание!
От отметки 147,600 предусмотреть насыпь до спланированных, планировочных отметок земли на территории кранового узла КУП-D6 – 147,75 и 147,85, данная насыпь учтена в части проекта Генерального плана (ГП).

Примечание:
1. *Установка кранового узла КУП-D6 (Ду1000) расположена на ПК0+33 трассы проектной перемычки № 3 газопровода, продольный профиль перемычки ПК0 – ПК0+64.*

Условные обозначения:

147.85 – *Отметка спланированной поверхности земли*

147.42 – *Отметка существующей поверхности земли*

A1	09.09.2026	Выпущено для строительства			
R1	29.07.2026	Выпущено для рассмотрения			
Рев	Дата	Назначение ревизии		Проверил	Утвердил

ЗАКАЗЧИК: UTG ГЕНЕРАЛЬНЫЙ ПОДРЯДЧИК: UET ПОДРЯДЧИК: PBG ГЕНЕРАЛЬНЫЙ ПРОЕКТИРОВЩИК: EAST WEST ENGINEERING

Изм.	Кол.уч.	Лист	№ док.	Подпись	Дата	EWE0426-MGL1-STR-054-DRW-750502-A1		
						«СТРОИТЕЛЬСТВО НОВЫХ НИТОК (УЧАСТКОВ) ГАЗОПРОВОДОВ «ГАЗЛИ – САРИМОЙ» И «АКЧАЛОК – ГАЗЛИ – НУКУС» ОБЩЕЙ ПРОТЯЖЕННОСТЬЮ НЕ МЕНЕЕ 275 КМ».		
ГИП		Кирпичников С.			09.09.26	ГАЗОПРОВОД "ГАЗЛИ-САРИМОЙ" (54 КМ) Линейный крановый узел DN1000 КУП-D6	Стадия: РП	Лист: 1 / Листов: 1
Нач.отд.		Каршиев А.			09.09.26			
Исполн.		Хабиров Х.			09.09.26	Схема расположения кранового узла КУП-D6.	EAST WEST ENGINEERING	ООО "EAST-WEST Engineering" г. Ташкент 2026г.
Н.контр		Кирпичников С.			09.09.26			

Взам. инв. № | Подпись и дата | Инв.№ подл.

Формат / Format A2