Разрез 1-1 м 1:100.


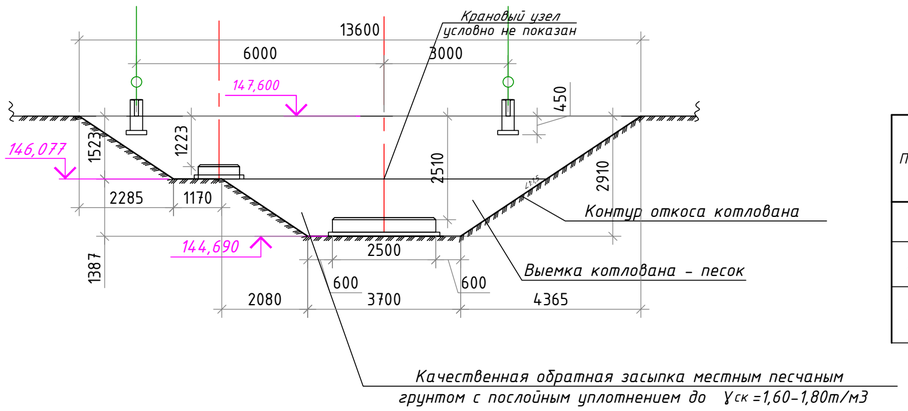


Таблица объемов земляных работ

Поз.	Наименование	Ед. изм.	Кол-во	Примечание
1	Выемка грунта	$м^3$ / m^3	235,12	
2	Обратная засыпка	$м^3$ / m^3	215,68	
3	Лишний грунт выемки для планировки по территории площадки строительства	$м^3$ / m^3	19,44	

План котлована м 1:100.

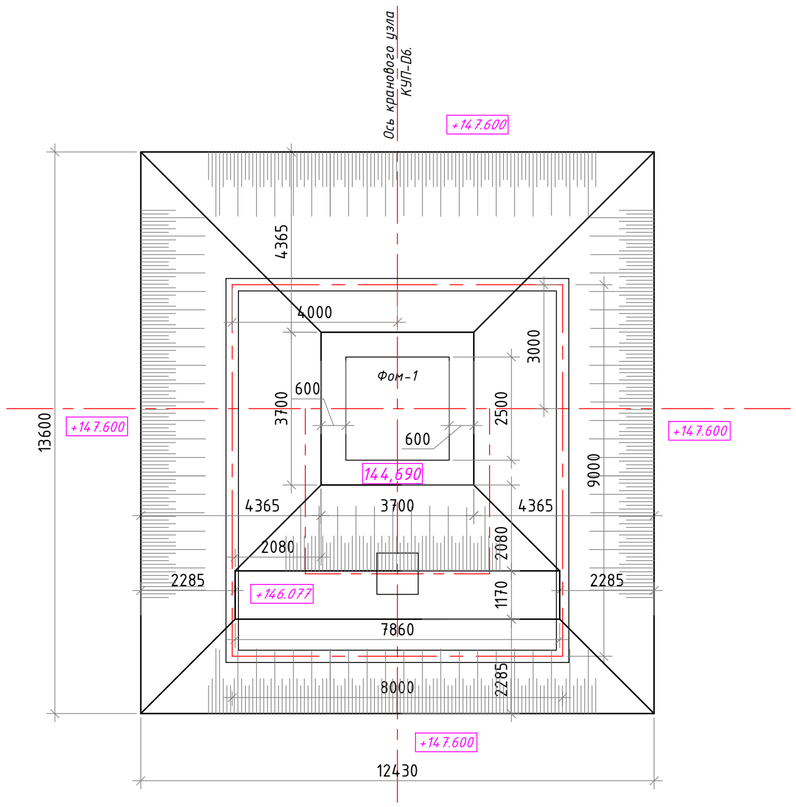

1. *Порядок производства работ:*

Проектом предусматриваются следующие мероприятия по подготовке основания:

Срезка растительного слоя грунта толщиной min. 10см (ПЛОДОРОДНЫЙ СЛОЙ ПОЧВЫ) $\gamma_{ск}$=1,3тн/м^3 с перемещением грунта в отвал для последующего использования его при рекультивации. Срезку растительного слоя грунта выполнять за 1-2 прохода по одному следу при отсутствии корней кустарников и деревьев, она учтена в разделе проекта "ГЕНЕРАЛЬНОГО ПЛАНА". Грунт в зависимости от трудности разработки механизированным способом - I-й группы согласно дополнения к КР 02.01 - Земляные сооружения, основания и фундаменты.*

Выемку грунта котлована выполнять механизированным способом при помощи одноковшового экскаватора с емкостью ковша 0,65м^3 с перемещением в отвал, учесть потери 1,5%.

Котлован должен быть освидетельствован с участием инженера-геолога с целью определения пригодности грунтов в качестве основания.

Обратную засыпку пазух котлована выполнять местным песчаным грунтом после устройства фундаментов с качественным послойным уплотнением. Высота уплотняющего слоя грунта не более 30см. по высоте, согласно СНИП КР 02.01 - Земляные сооружения, основания и фундаменты.*

До начала производства земляных работ должен быть составлен проект производства работ, в котором решаются следующие вопросы:

- порядок разработки котлована с учетом очередности этапов строительства;
- уточненные габариты котлована, согласно данного чертежа;
- места складирования грунта для обратной засыпки;
- механизмы для разработки грунтов, для уплотнения дна котлована, грунтов обратной засыпки;
- при необходимости - порядок замачивания грунтов;
- обеспечение лабораторного контроля за качеством уплотнения грунтов;

Все работы выполнять с соблюдением требований:

- ШНК 3.01.01-22 "Организация строительного производства";
- КР 02.01 "Земляные сооружения, основания и фундаменты";
- КМК 3.01.02-23 "Техника безопасности в строительстве".

При производстве земляных работ необходимо уточнить соответствие грунтов принятых в проекте. В случае обнаружения других грунтов сообщить об этом проектной организации для принятия соответствующих решений. А также при обнаружении под подошвой предполагаемого сооружения неоднородного грунта с включениями мусора, выбрать его на всю мощность, компенсировав выборку послойно уплотненными местными грунтами (Нсл<30см и Ку=0.95) до уровня проектной отметки дна котлована;

Общее примечание:

1. Котлован разработан в соответствии с решением по привязке объекта на генплане, согласно принятым габаритам и конструктивным решениям в проекте;

2. В котловане изображены контуры проектируемых фундаментов и трубопровода;

3. Строительные категории грунтов при разработке механизмами следует принять, исходя из их плотности:

- для почвенно-растительного слоя - 1,2-1,4 тн/м3;
- для песчаного грунта - 1,58 тн/м^3

УКАЗАНИЯ ПО ПРОИЗВОДСТВУ РАБОТ ДЛЯ ПОДГОТОВКИ ОСНОВАНИЯ:

Перед началом производства земляных работ по котловану под фундаменты приступить только после перенесения за пределы котлована или заглушения имеющихся в пределах контура котлована сетей и коммуникаций;

Перенос существующих подземных и наземных коммуникаций (технологические трубопроводы, водопроводные и электрические сети, газопроводные трубопроводы и т.д.) с площадки строительства должен осуществляться после согласования с инстанциями.

Необходимо выполнение общих вертикальных планировочных земляных работ на площадке.

Перед производством работ по заложению фундамента котлован должен быть освидетельствован инженером-геологом;

Примечание:

1. Песок мелкий с частицами из суглинка - группа грунта в зависимости от трудности их разработки механизированным способом (одноковшовыми экскаваторами) - I группа, (бульдозерами)- II группа, согласно таблице 1-1а, (вручную) - Iгруппа, согласно таблице 1-18 КР 02.01 - Земляные сооружения, основания и фундаменты. ДОПОЛНЕНИЯ И ПОПРАВКИ К ТЕХНИЧЕСКОЙ ЧАСТИ.*

Внимание!

Обратную засыпку котлована выполнить до отметки 161,10.

От отметки 161,10 предусмотреть насыпь до спланированных, планировочных отметок земли на территории кранового узла КУП-D2 - 161,40 и 161,30, данная насыпь учтена в части проекта Генерального плана (ГП).

Под газопроводными трубопроводами обратную засыпку (пазухи) выполнять вручную согласно СНИП КР 02.01 - Земляные сооружения, основания и фундаменты.*

A1	09.09.2026	Выпущено для строительства		
R1	29.07.2026	Выпущено для рассмотрения		
Рев	Дата	Назначение ревизии	Проверил	Утвердил

ЗАКАЗЧИК: UTG ГЕНЕРАЛЬНЫЙ ПОДРЯДЧИК: UET ПОДРЯДЧИК: PBG ГЕНЕРАЛЬНЫЙ ПРОЕКТИРОВЩИК: EAST WEST ENGINEERING

Изм.	Кол.уч.	Лист	№ док.	Подпись	Дата	EWE0426-MGL1-STR-054-DRW-750504-A1		
						«СТРОИТЕЛЬСТВО НОВЫХ НИТОК (УЧАСТКОВ) ГАЗОПРОВОДОВ «ГАЗЛИ - САРИМОЙ» И «АКЧАЛОК - ГАЗЛИ - НУКУС» ОБЩЕЙ ПРОТЯЖЕННОСТЬЮ НЕ МЕНЕЕ 275 КМ».		
ГИП		Кирпичников С.			09.09.26			
Нач.отд.		Каршиев А.			09.09.26	ГАЗОПРОВОД "ГАЗЛИ-САРИМОЙ" (54 КМ) Линейный крановый узел DN1000 КУП-D6	Стадия: РП	Лист: 1 / Листов: 1
Исполн.		Смирнова И.			09.09.26			
Н.контр		Кирпичников С.			09.09.26	Котлован под крановый узел.	ООО "EAST-WEST Engineering" г. Ташкент 2026г.	

Взам. инв. № | Подпись и дата | Инв.№ подл.

Формат / Format A2