1 – 1 м 1:25.

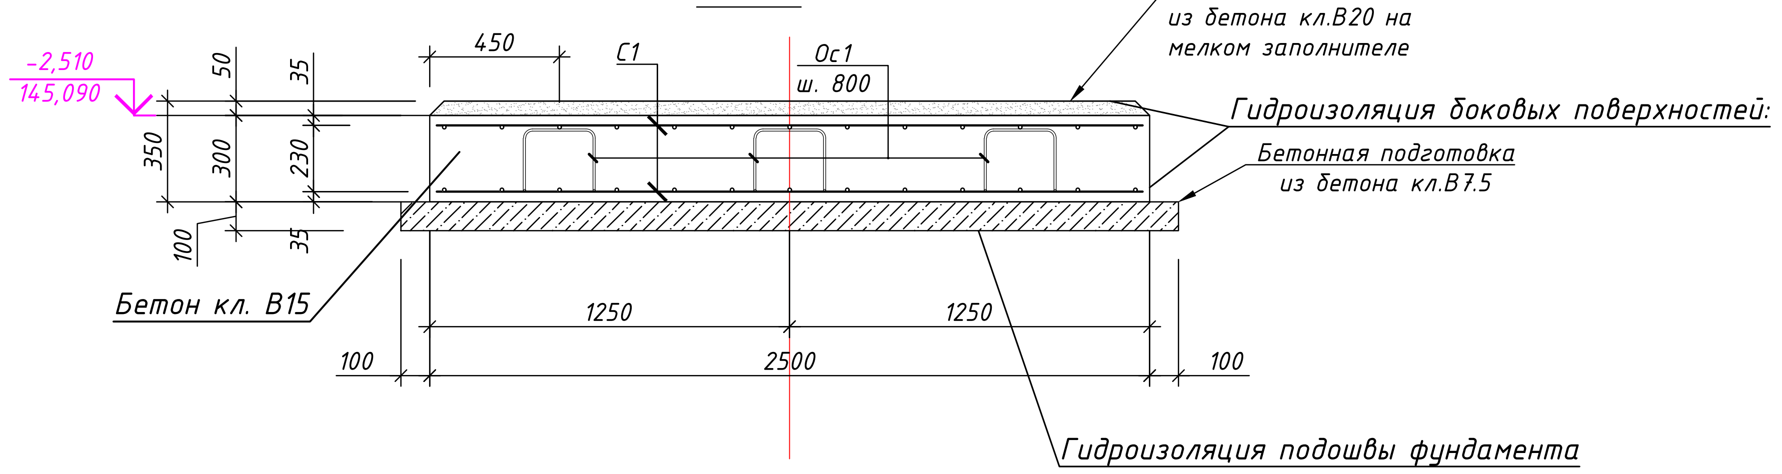
-2,510
145,090
450
С1
Ос1
ш. 800
50
35
350
300
230
100
35
Монтажная подливка из бетона кл.В20 на мелком заполнителе
Гидроизоляция боковых поверхностей:
Бетонная подготовка из бетона кл.В7.5
Бетон кл. В15
1250
1250
100
2500
100
Гидроизоляция подошвы фундамента

Ведомость деталей

Поз.	Эскиз
Ос1	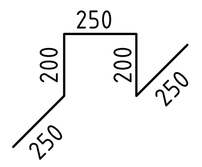

Размеры хомутов даны по центру стержня.

Спецификация элементов

Марка Поз.	Обозначение	Наименование	Кол.шт	Масса ед., кг	Прим.
		Фундамент Фом-1			
		Сборные единицы			
С1	См. данный лист	Сетка С1	2		153.87
		Детали			
Ос1	ГОСТ 34028-2016	Ф8 А240 L=1150 мм	9	0.45	4.08
		Сетка С1			
а1	ГОСТ 34028-2016	Ф14 А500 L=2450 мм	26	2.96	76.94
		Материалы			
	на подливку	Бетон кл. В20, W6, F50			0.30 м^3
		Бетон кл. В15, W6, F50			1.88 м^3
	на подготовку	Бетон кл. В7.5			0.73м^3
		Гидроизоляция фундамента на площади:			16,55 м^2

Фундамент Фом-1

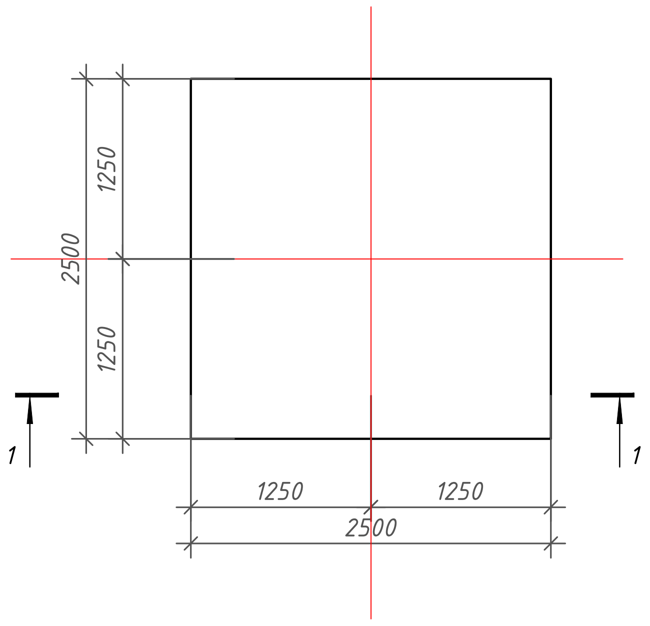

Сетка С1

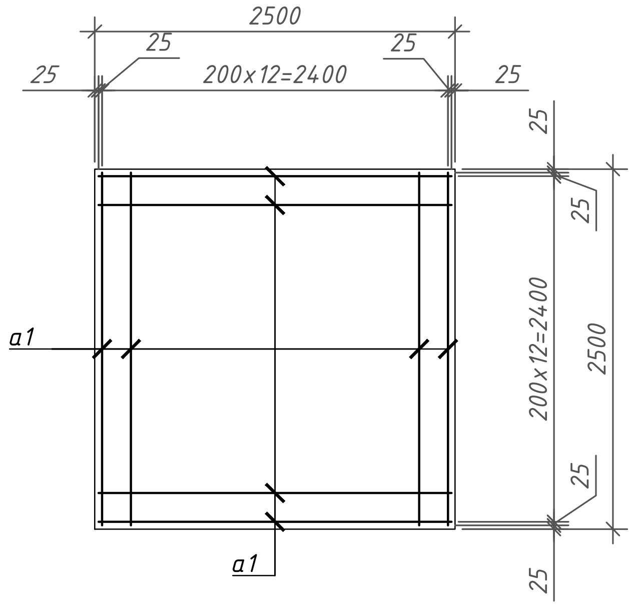

Примечания:

1. Объединение арматурных стержней в плоские сетки или пространственные каркасы выполнять вязальной стальной отожженной проволокой d=0.8-1.0мм. Применение ручной электродуговой сварки не допускается.
2. Подливку выполнить из бетона кл. В20 на мелком заполнителе.
3. Фундамент Фом-1 разработан под шаровой кран. Бетонирование выполнять после получения оборудования и сверки с паспортными данными.
4. Фиксаторы для крепления двух сеток марки Ос-1 устанавливать в шахматном порядке.
5. Расположение фундамента смотри чертёж: Схема расположения кранового узла КУП-D6.
6. Фундаментов Фом-1 изготовить в количестве - 1шт.
7. Бетон для фундамента применять на сульфатостойком портландцементе.

Гидроизоляция фундамента из двух слоев полимерного покрытия на основе лака ХП-734 по ГОСТ 52165-2003 толщиной 25 мкм.

Ведомость расхода стали, кг

Марка элемента	Изделия арматурные					Общий расход
	Арматура класса				Всего	
	А240		А500			
	ГОСТ 34028-2016		ГОСТ 34028-2016			
	Ф8	Итого	Ф14	Итого		
Фундамент Фом1	4.08	4.08	153.87	153.87	157.95	157.95

Взам. инв. №

Подпись и дата

Инв.№ подл.

Рев	Дата	Назначение ревизии	Проверил	Утвердил
А1	09.09.2026	Выпущено для строительство		
R1	29.07.2026	Выпущено для рассмотрения		

ЗАКАЗЧИК: UTG UZTRANSGAZ

ГЕНЕРАЛЬНЫЙ ПОДРЯДЧИК: UET UZBEKENERGOTAMIR

ПОДРЯДЧИК: PBG Pro Build Generation

ГЕНЕРАЛЬНЫЙ ПРОЕКТИРОВЩИК: EAST WEST ENGINEERING

EWE0426-MGL1-STR-054-DRW-750505-A1

«СТРОИТЕЛЬСТВО НОВЫХ НИТОК (УЧАСТКОВ) ГАЗОПРОВОДОВ «ГАЗЛИ - САРИМОЙ» И «АКЧАЛОК - ГАЗЛИ - НУКУС» ОБЩЕЙ ПРОТЯЖЕННОСТЬЮ НЕ МЕНЕЕ 275 КМ».

Изм.	Кол.уч.	Лист	№ док.	Подпись	Дата
ГИП		Кирпичников С.			09.09.26
Нач.отд.		Каршиев А.			09.09.26
Исполн.		Хабиров Х.			09.09.26
Н.контр		Кирпичников С.			09.09.26

ГАЗОПРОВОД "ГАЗЛИ-САРИМОЙ" (54 КМ)
Линейный крановый узел DN1000 КУП-D6

Стадия	Лист	Листов
РП	1	1

Фундамент Фом-1.

EAST WEST ENGINEERING
ООО "EAST-WEST Engineering"
г. Ташкент 2026г.

Формат / Format A2