ВИД

Калитка К-1 м 1:25.

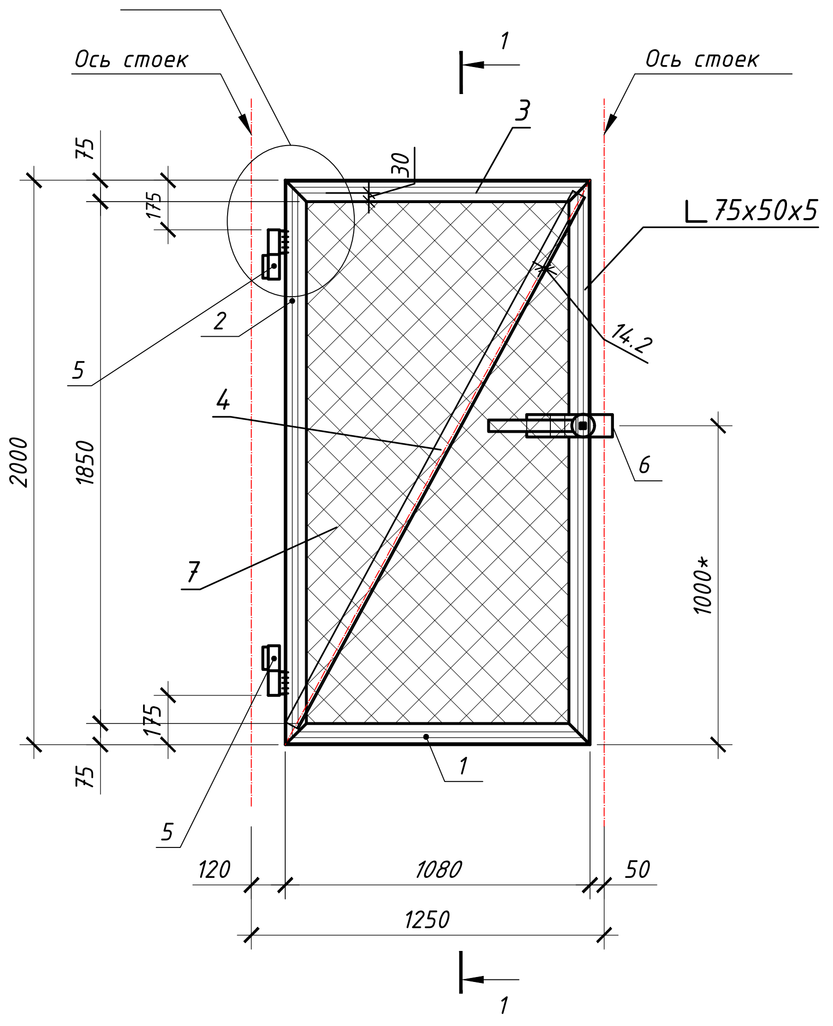

Разрез 1-1 м 1:25.

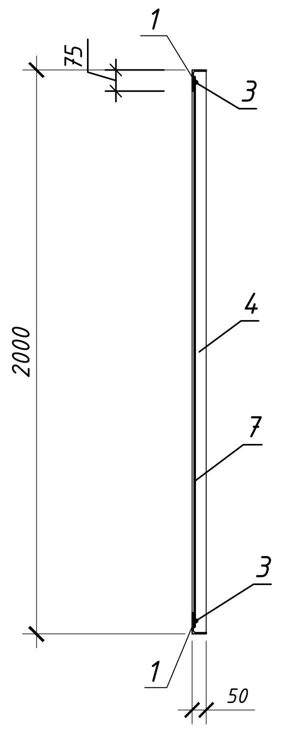

Спецификация расхода материалов

Марка Поз.	Обозначение	Наименование	Кол. шт.	Масса ед., кг	Приме-чание
К-1		Калитка К-1		47,73	вес на 1 шт.
1	ГОСТ 8510-93*, Сталь С235	L75x50x5 L=1080	2	5.17	10.35
2	ГОСТ 8510-93*, Сталь С235	L75x50x5 L=2000	2	9.58	19.16
3	ГОСТ 34028-2016	Арматура Ф6.0 А240 Lобщ=5800	1	0.222 кг/м.п	1.29
4	ГОСТ 8510-93*, Сталь С235	L50x50x5 L=2140	1	8.07	8.07
5	Серия 3.017-1.05.110.100	Петля крепления калитки	2	2,0	4,0
6		ЭМЗУ типа "Базальт"	1		или аналог
7	ГОСТ 5336-80*	Сетка рабица №50-3.0,размером			
		1030 x 1950мм; S=2.01м2	1	2,42 кг/м2	4.86
		Материалы:			
		Окраска металлоконструкций масляной краской за 2 раза			1,99м^2

Примечания:
1. Сварку вести электродами Э42А ГОСТ9467-85 по РСтУз 865-98
2. Конструкция должна быть покрыта масляной краской за 2 раза по грунтовке.
3. Сетку прикрепить к элементам обрамления калитки.
4. Применять петлю по серии 3.017-1.05.110.100 (2шт.) Петли свариваются к полотну калитки.
5. Крепления замка установить по месту.
6. Калиток К-1 изготовить в количестве 2 шт.

ГОСТ 5264-80-Т1-◺6

Узел 1 м 1:10.

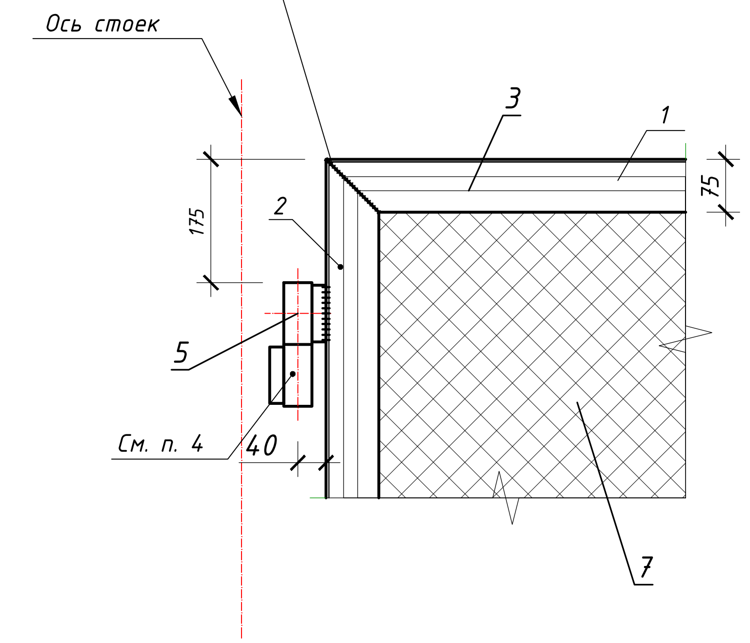

Рев	Дата	Назначение ревизии	Проверил	Утвердил
A1	09.09.2026	Выпущено для строительство		
R1	29.07.2026	Выпущено для рассмотрения		

ЗАКАЗЧИК: UTG UZTRANSGAZ

ГЕНЕРАЛЬНЫЙ ПОДРЯДЧИК: UET UZBEKENERGOTAMIR

ПОДРЯДЧИК: PBG Pro Build Generation

ГЕНЕРАЛЬНЫЙ ПРОЕКТИРОВЩИК: EAST WEST ENGINEERING

EWE0426-MGL1-STR-054-DRW-750515-A1

«СТРОИТЕЛЬСТВО НОВЫХ НИТОК (УЧАСТКОВ) ГАЗОПРОВОДОВ «ГАЗЛИ - САРИМОЙ» И «АКЧАЛОК - ГАЗЛИ - НУКУС» ОБЩЕЙ ПРОТЯЖЕННОСТЬЮ НЕ МЕНЕЕ 275 КМ».

Изм.	Кол.уч.	Лист	№ док.	Подпись	Дата
ГИП		Кирпичников С.			09.09.26
Нач.отд.		Каршиев А.			09.09.26
Исполн.		Хабиров Х.			09.09.26
Н.контр		Кирпичников С.			09.09.26

ГАЗОПРОВОД "ГАЗЛИ-САРИМОЙ" (54 КМ)
Линейный крановый узел DN1000 КУП-Д6

Стадия	Лист	Листов
РП	1	1

Калитка К-1.

EAST WEST ENGINEERING
ООО "EAST-WEST Engineering"
г. Ташкент 2026г.

Взам. инв. №

Подпись и дата

Инв.№ подл.

Формат / Format A3