Схема расположения листов

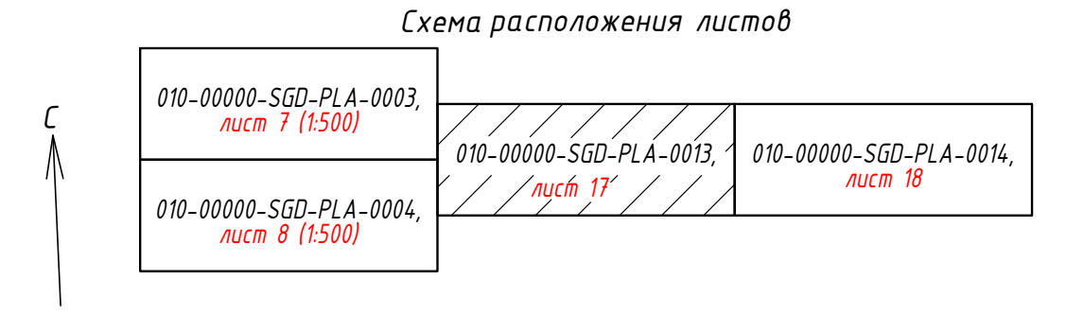

С
010-00000-SGD-PLA-0003, лист 7 (1:500)
010-00000-SGD-PLA-0004, лист 8 (1:500)
010-00000-SGD-PLA-0013, лист 17
010-00000-SGD-PLA-0014, лист 18

Точки подключения с 010-00000-SGD-PLA-0003, лист 7 (1:500), 010-00000-SGD-PLA-0004, лист 8 (1:500)

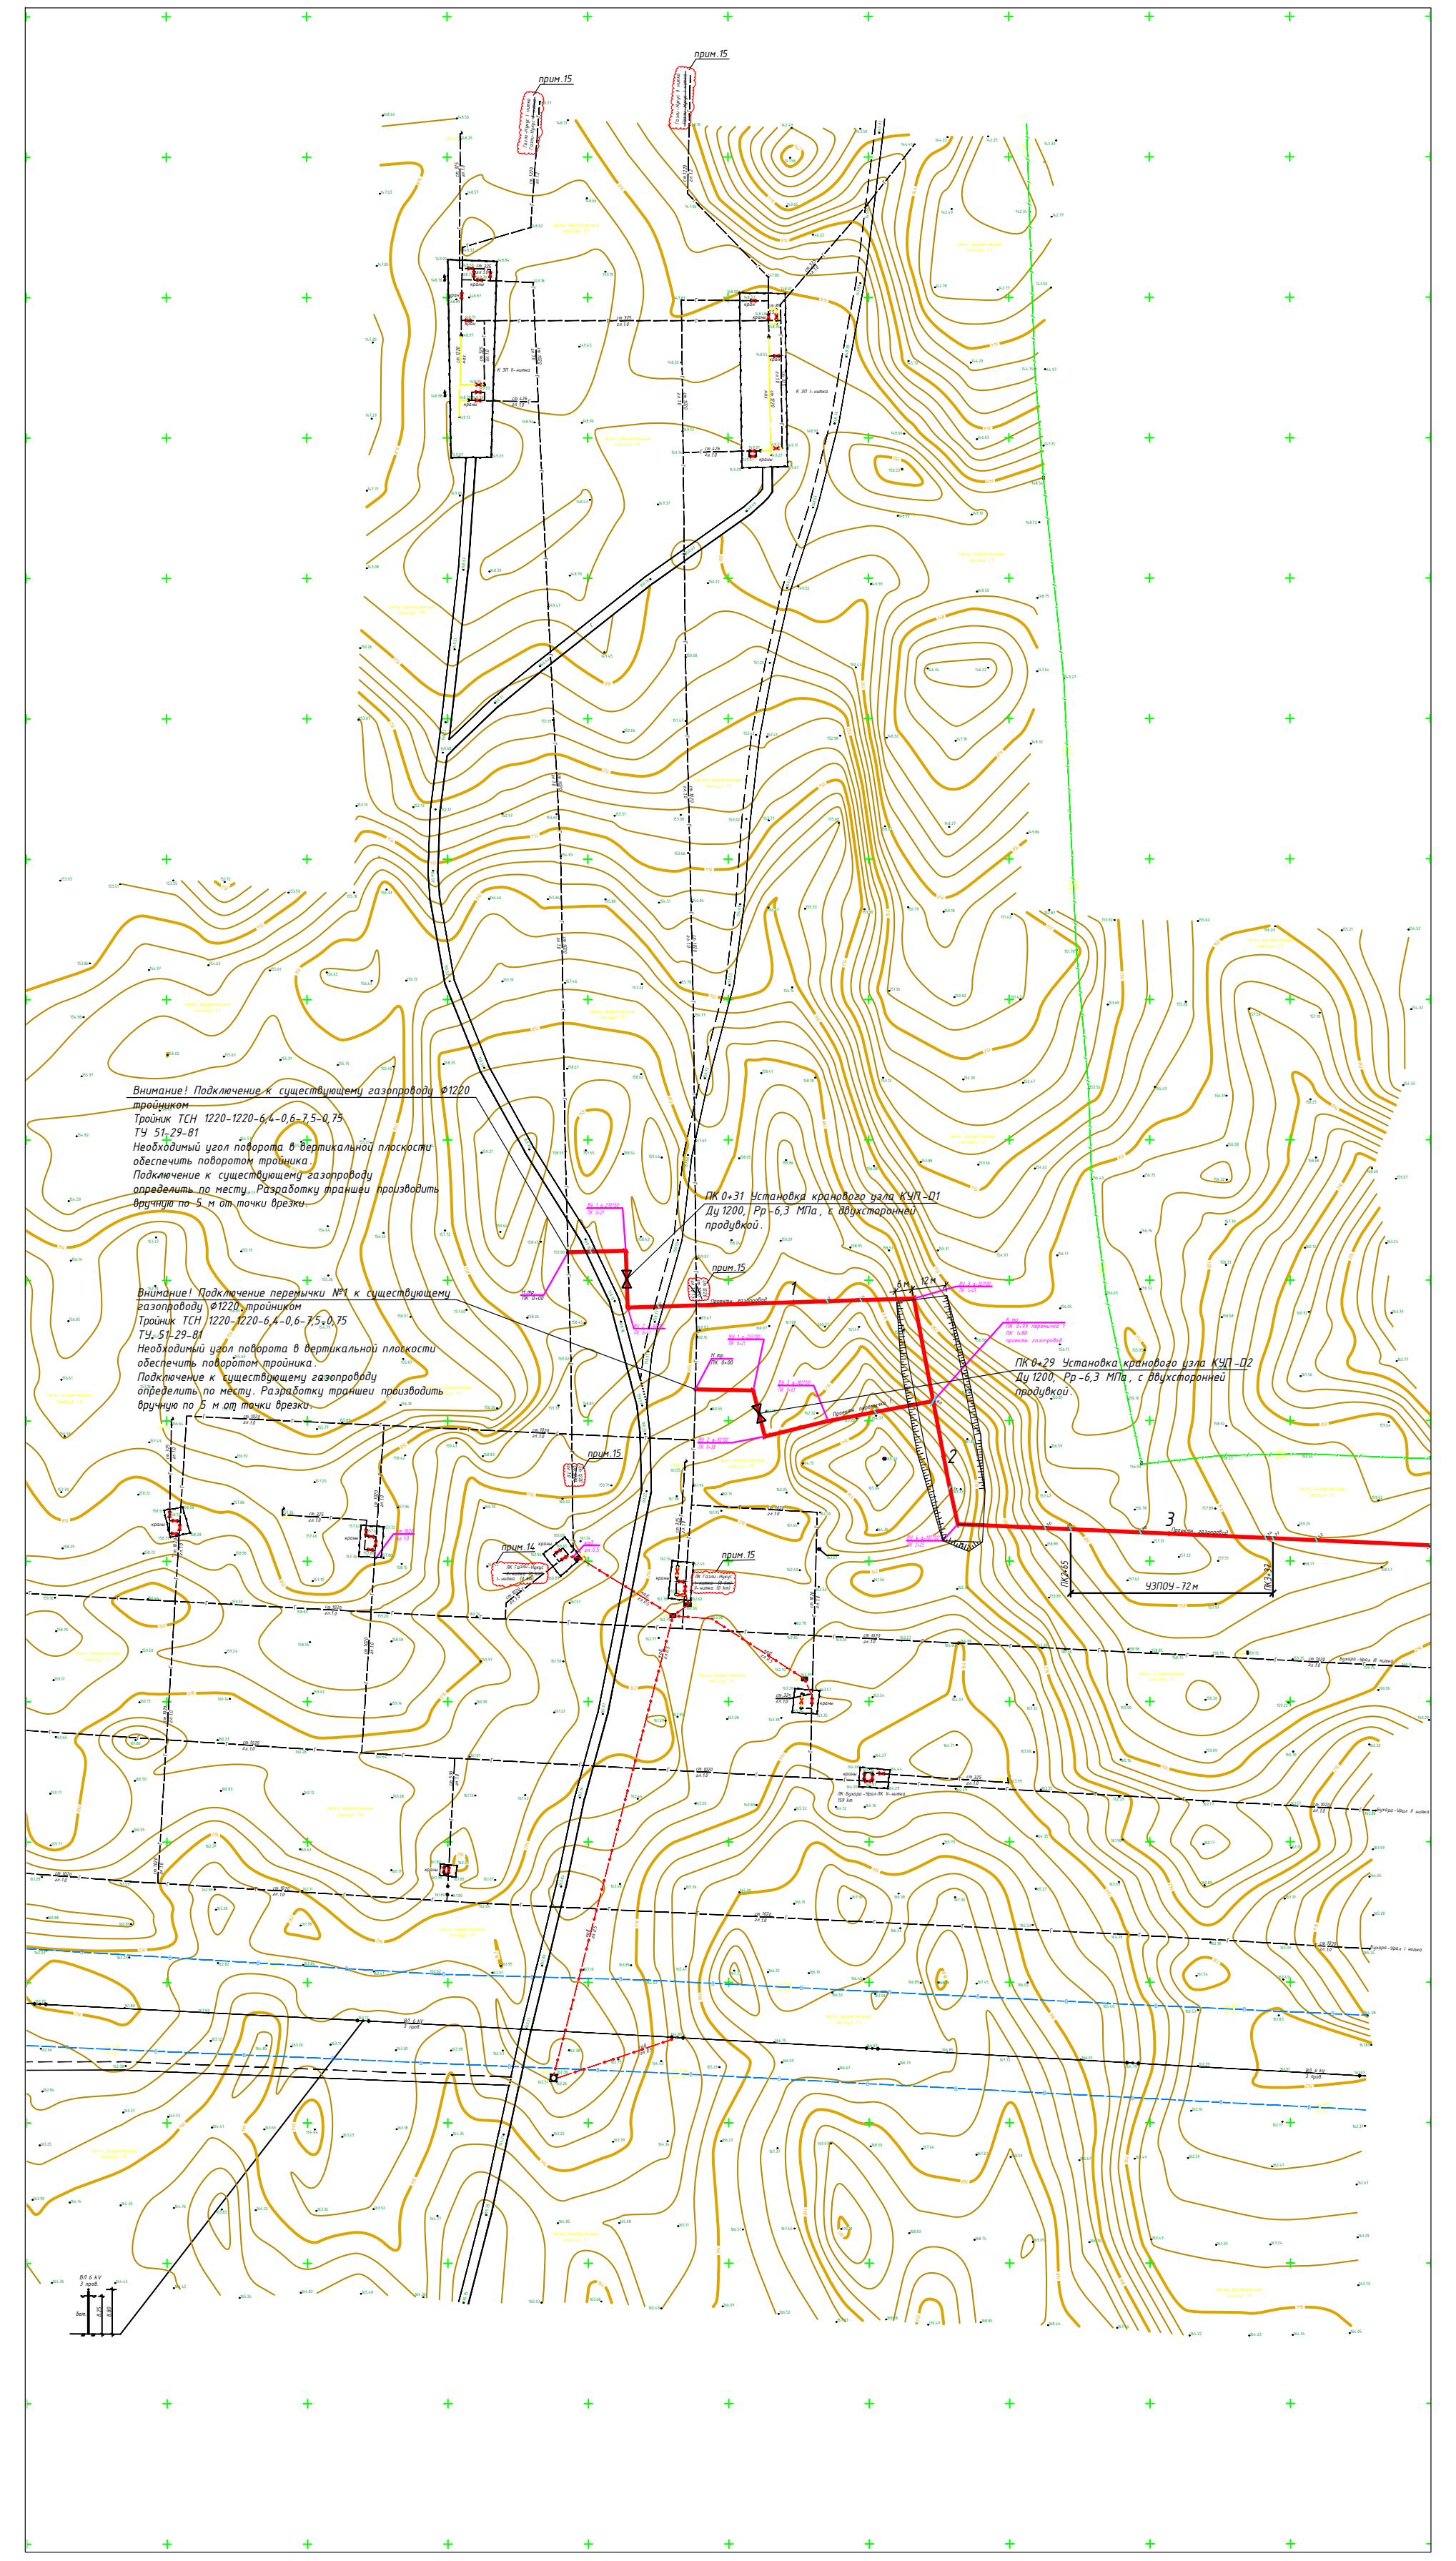

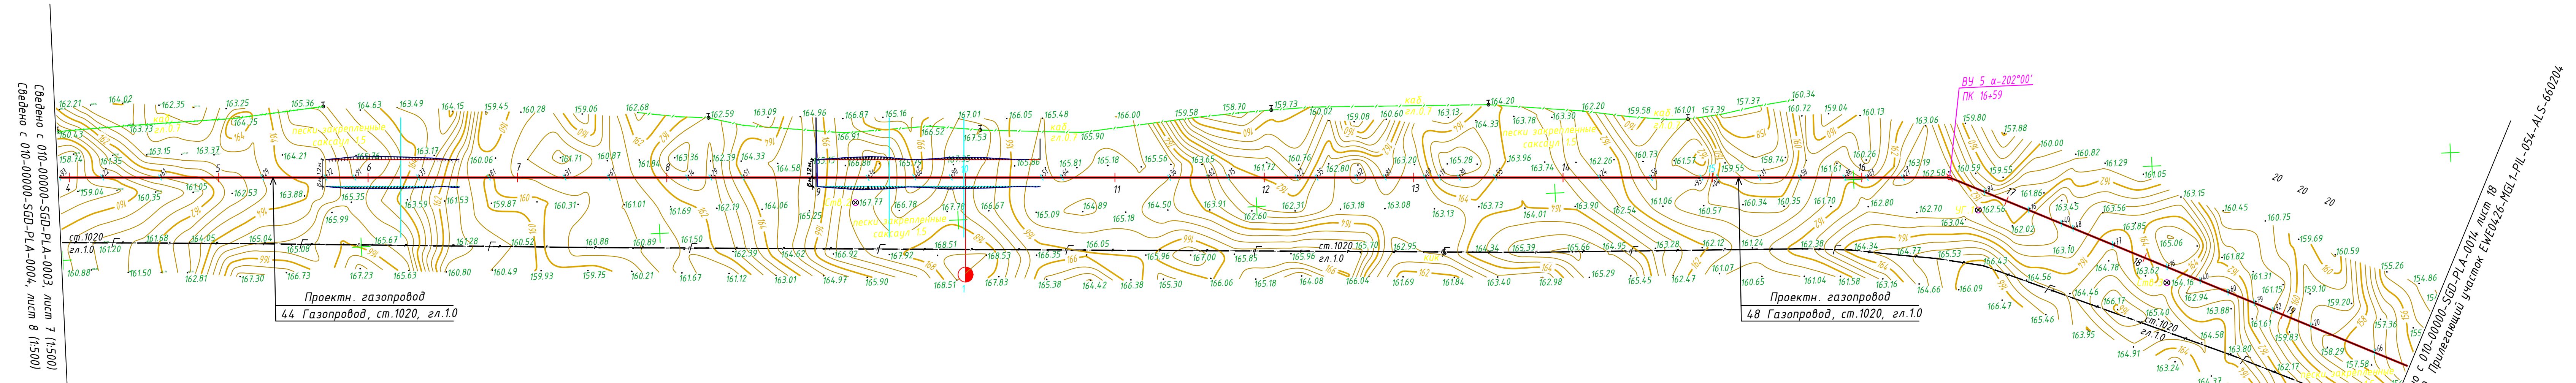

Внимание! Подключение к существующему газопроводу Ф1220 тройником
Тройник ТСН 1220-1220-6,4-0,6-7,5-0,75
ТУ 51-29-81
Необходимый угол поворота в вертикальной плоскости обеспечить поворотом тройника.
Подключение к существующему газопроводу определить по месту. Разработку траншеи производить вручную по 5 м от точки врезки.

ПК 0+31 Установка кранового узла Ду 1200 Рр -6,3 MPa, с двухсторонней продувкой.

Внимание! Газопровод Ф1220, гл.1,5 м. Расстояние в свету между газопроводами выдержать не менее 0,35. Разработку траншеи по 2 m в обе стороны от пересечения вести вручную.

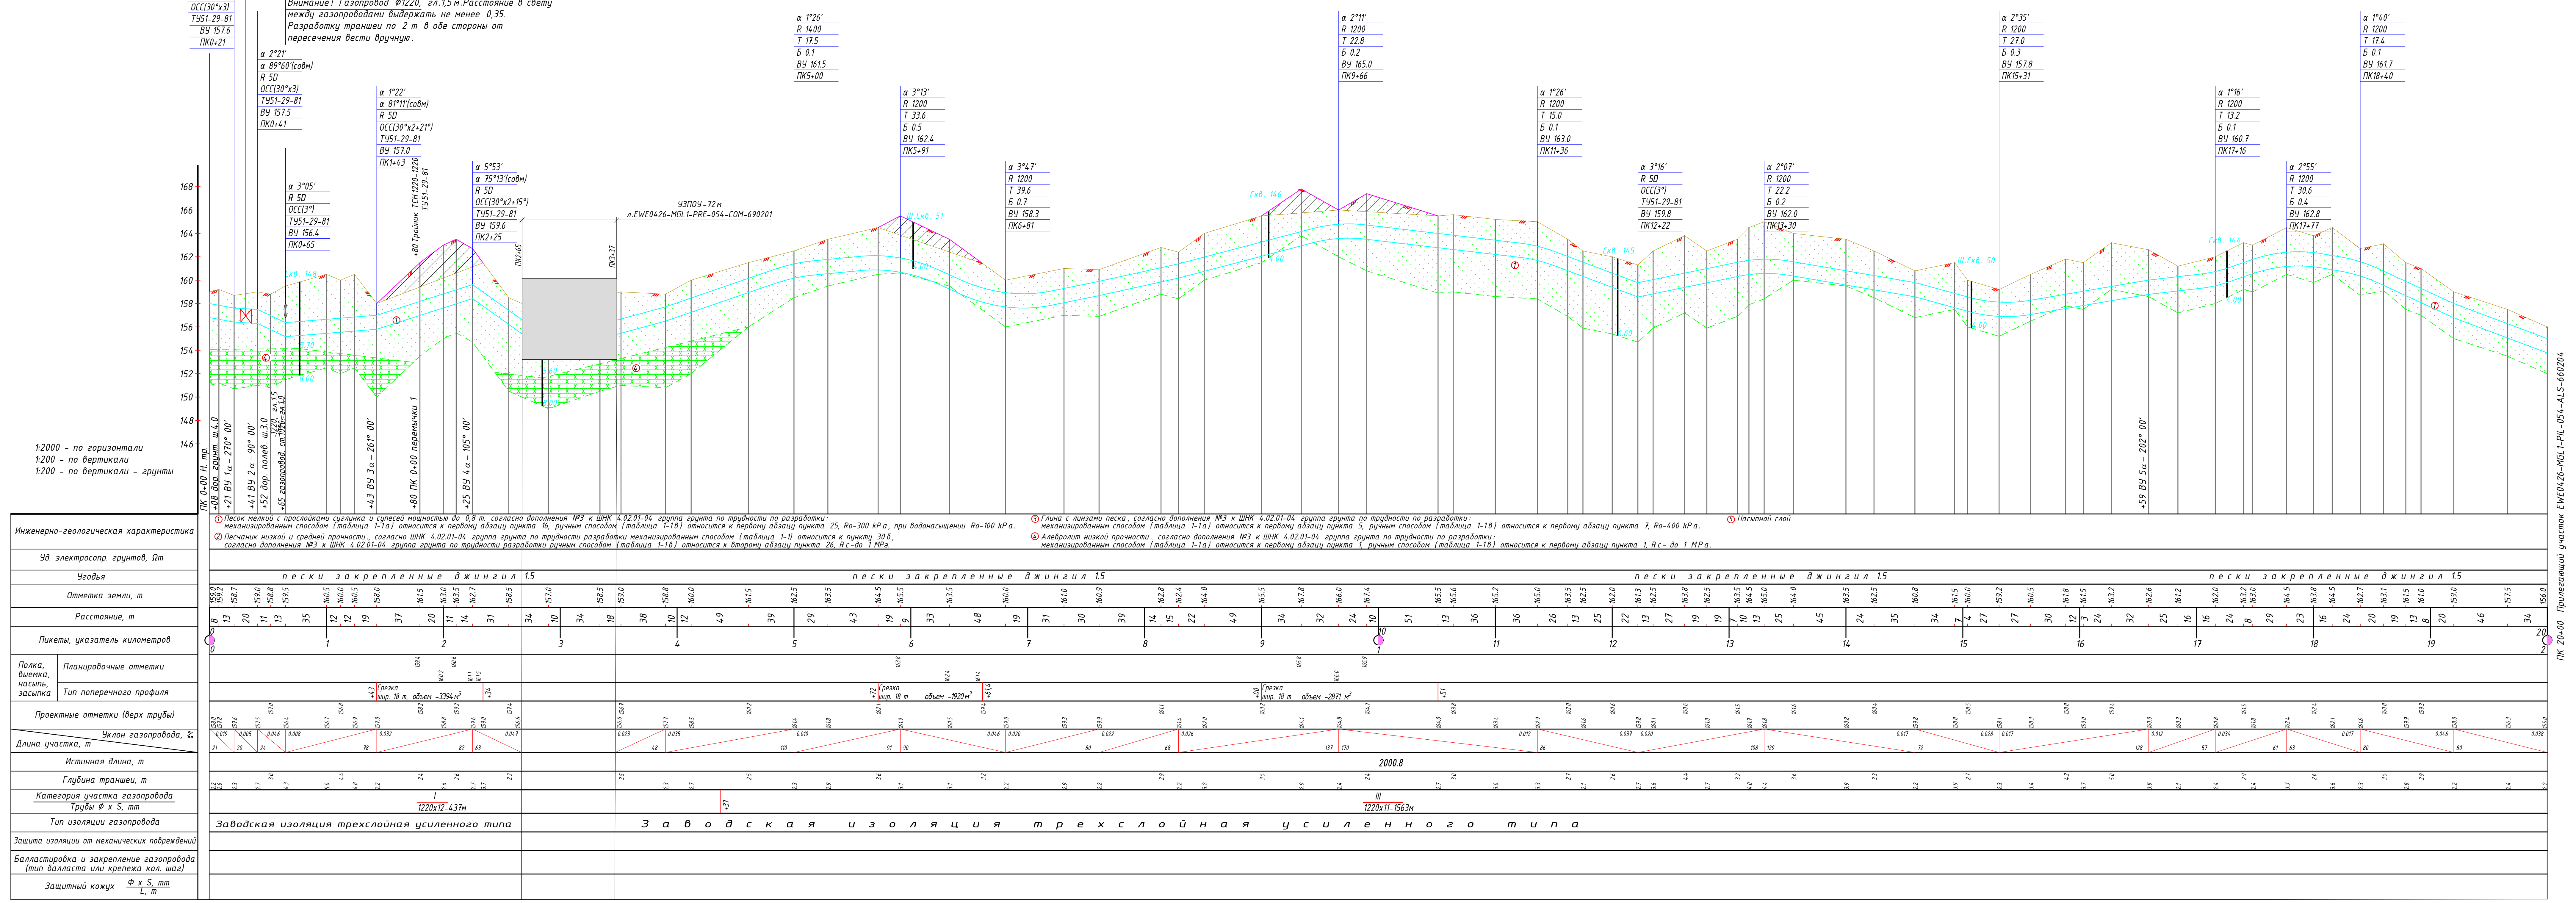

α 0°48'
α 90°01'(совм)
R 5D
ОСС(30°х3)
ТУ51-29-81
ВУ 157.6
ПК0+21
α 2°21'
α 89°60'(совм)
R 5D
ОСС(30°х3)
ТУ51-29-81
ВУ 157.5
ПК0+41
α 1°22'
α 81°11'(совм)
R 5D
ОСС(30°х2+21°)
1:2000 - по горизонтали
1:200 - по вертикали
1:200 - по вертикали - грунты
ПК 0+00 Н. тр.
+08 дор. грунт. ш.4.0
+21 ВУ 1α - 270° 00'
+41 ВУ 2α - 90° 00'
+52 дор. полев. ш.3.0
+65 газопровод ст.1020, гл.1.0
+43 ВУ 3α - 261° 00'
+80 ПК 0+00 перемычки 1
+25 ВУ 4α - 105° 00'
Инженерно-геологическая характеристика
① Песок мелкий с прослойками суглинка и супесей мощностью до 0,8 m. согласно дополнения №3 к ШНК 4.02.01-04 группа грунта по трудности по разработки: механизированным способом (таблица 1-1а) относится к первому абзацу пункта 16, ручным способом (таблица 1-1в) относится к первому абзацу пункта 25, Ro-300 kPa, при водонасыщении Ro-100 kPa.
② Песчаник низкой и средней прочности., согласно ШНК 4.02.01-04 группа грунта по трудности разработки механизированным способом (таблица 1-1) относится к пункту 30б, согласно дополнения №3 к ШНК 4.02.01-04 группа грунта по трудности разработки ручным способом (таблица 1-1в) относится к второму абзацу пункта 26, Rc-до 1 MPa.
③ Глина с линзами песка, согласно
④ Алевролит низкой прочности., согла
Уд. электросопр. грунтов, Ωm
Угодья
пески закрепленные джингил 1.5
Отметка земли, m
Расстояние, m
Пикеты, указатели километров
Планировочные отметки
Тип поперечного профиля
Проектные отметки (верх трубы)
Уклон ‰, длина участка, m
Исходная длина, m
Глубина траншеи, m
Категория участка газопровода
Трубы Ø х S, mm
Защита изоляции от механических повреждений
Балластировка и закрепление газопровода (тип балласта или крепления кол. шт)
Защитный кожух
2000.0
Заводская изоляция трехслойная усиленного типа
ПК 20+00 Прилегающий участок EWE0426-MGL1-PIL-054-ALS-660204

Внимание! Подключение к существующему газопроводу Ф1220 тройником
Тройник ТСН 1220-1220-6,4-0,6-7,5-0,75
ТУ 51-29-81
Необходимый угол поворота в вертикальной плоскости обеспечить поворотом тройника.
Подключение к существующему газопроводу определить по месту. Разработку траншеи производить вручную по 5 м от точки врезки.

ПК 0+29 Установка кранового узла Ду 1200, Рр -6,3 мРа с двухсторонней продувкой.

Внимание! Подключение перемычки к проектному газопроводу Ф1220 тройником
Тройник ТСН 1220-1220-6,4-0,6-7,5-0,75
ТУ 51-29-81
Необходимый угол поворота в вертикальной плоскости обеспечить поворотом тройника (учтен по основному газопроводу).

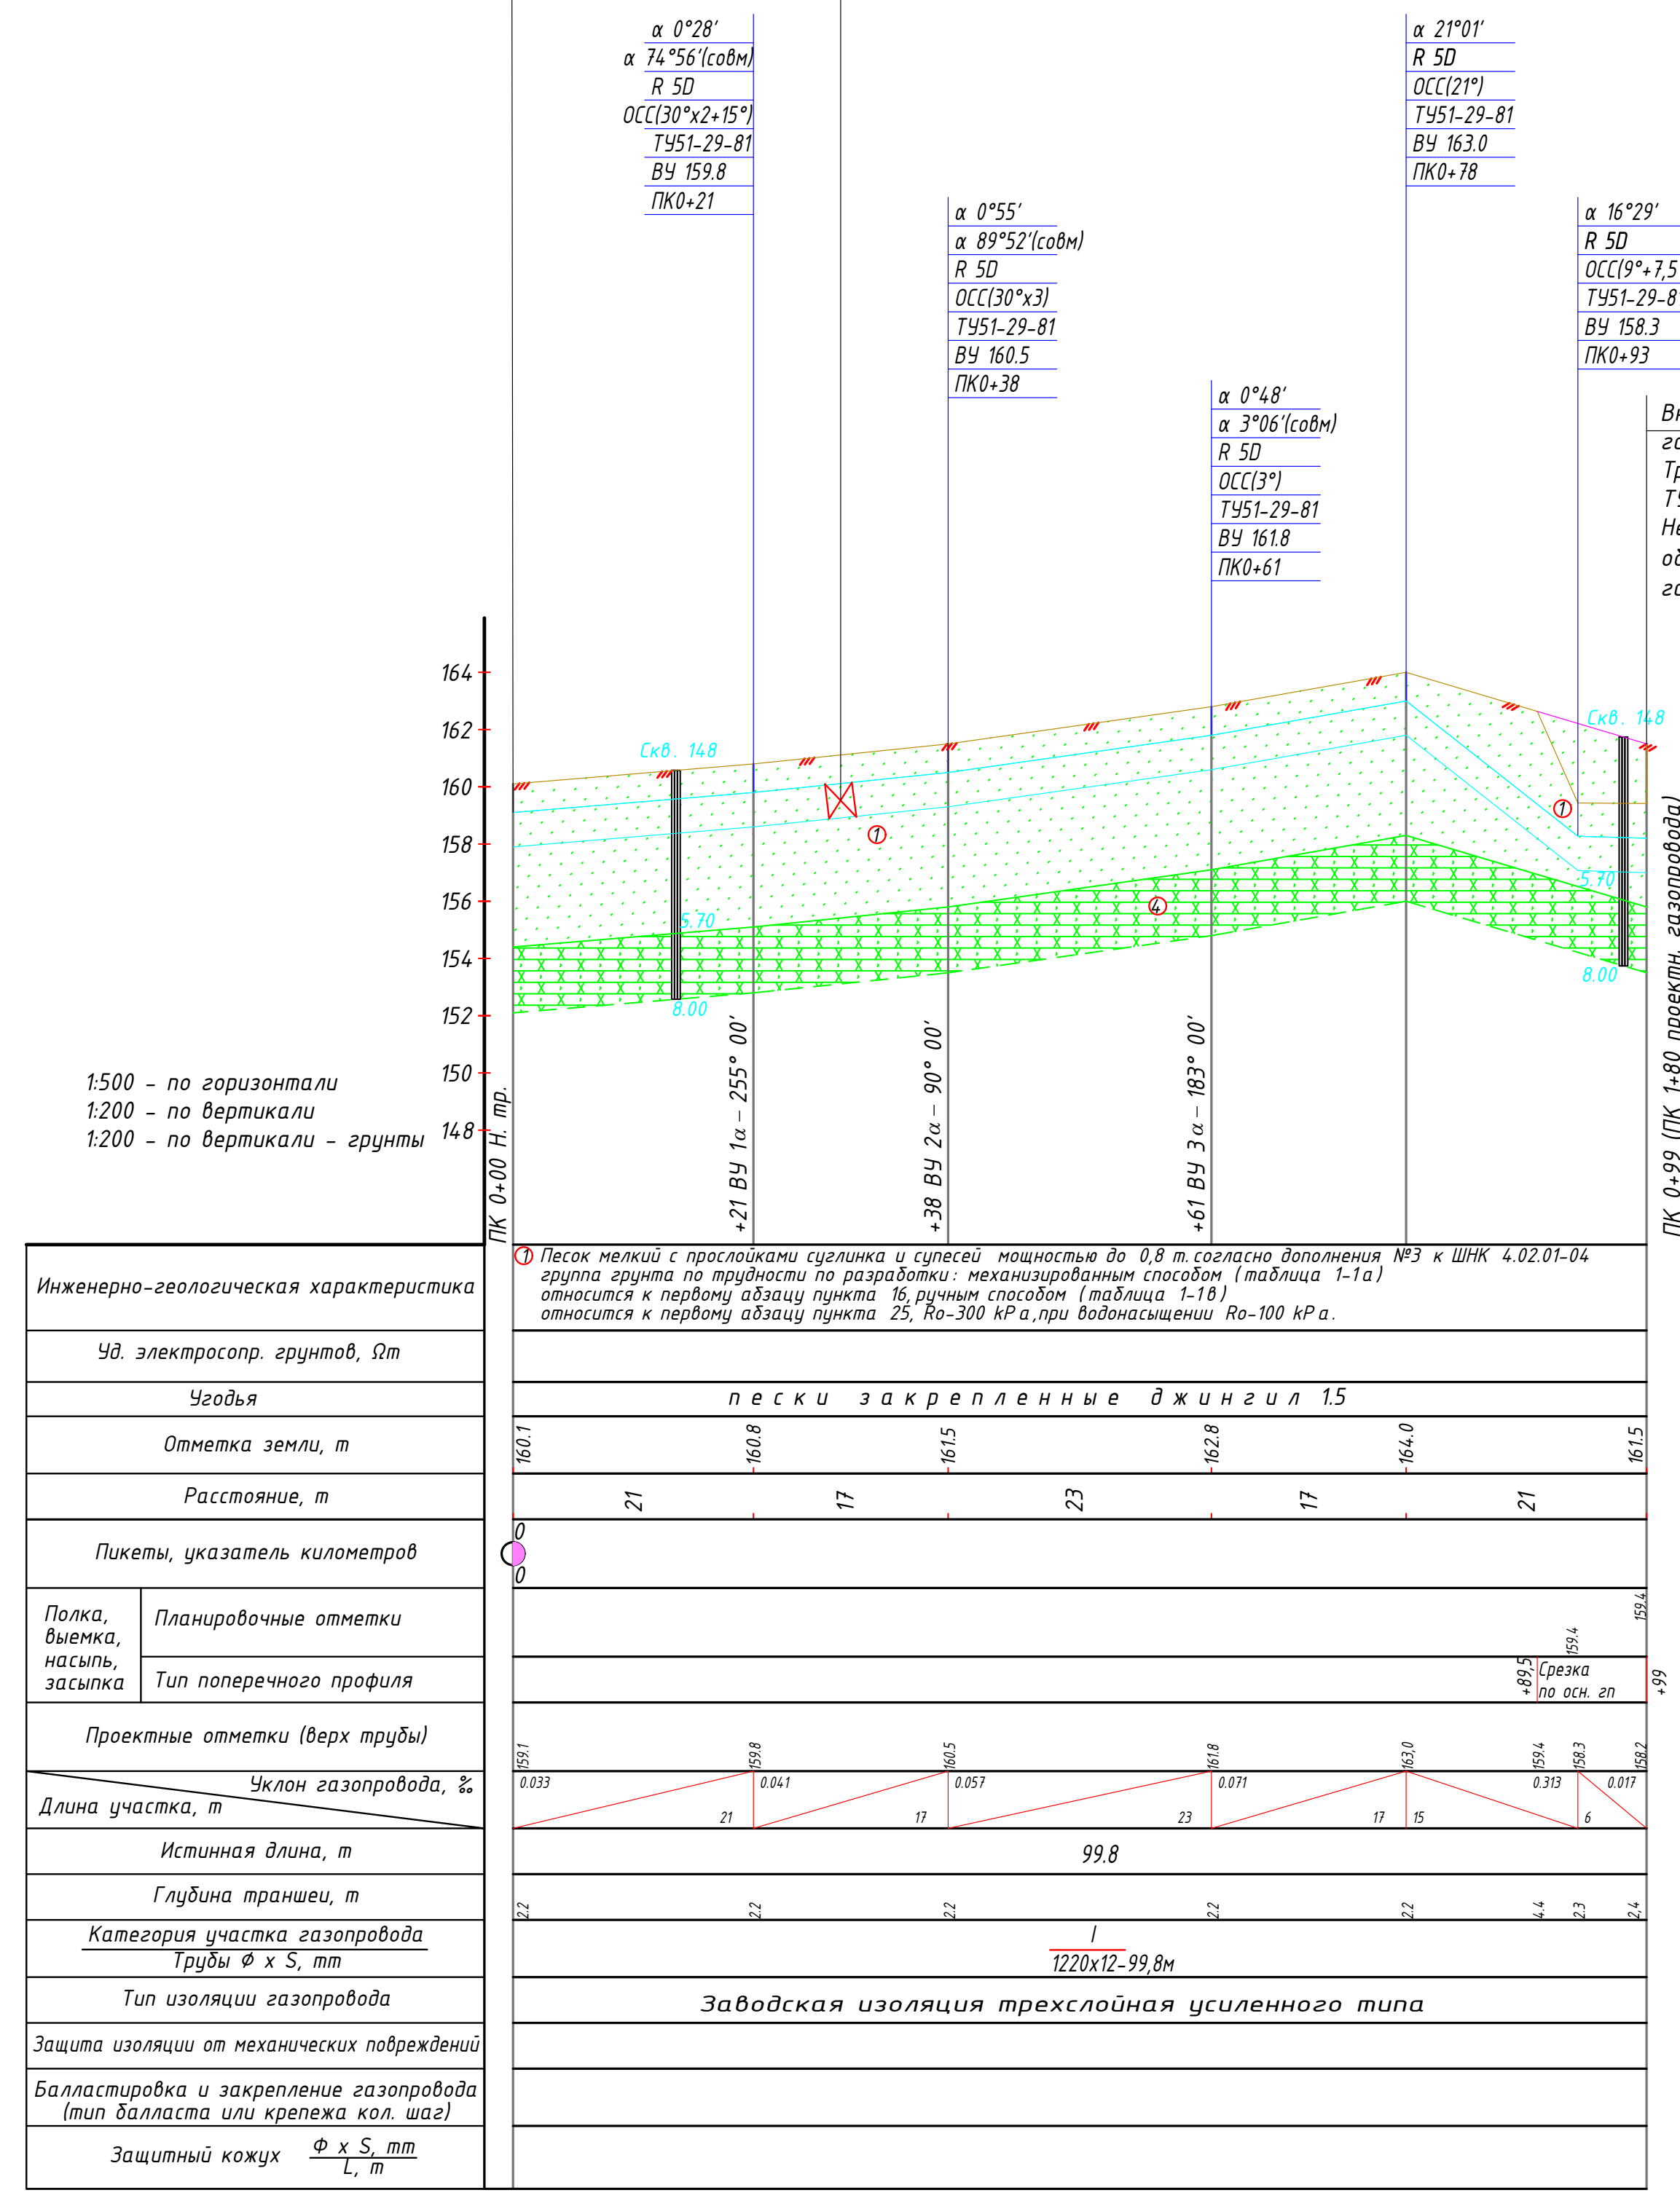

α 0°28'
α 74°56'(совм)
R 5D
ОСС(30°х2+15°)
ТУ51-29-81
ВУ 159.8
α 16°29'
R 5D
ОСС(9°+7,5°)
ТУ51-29-81
ВУ 158.3
ПК0+93
α 21°01'
R 5D
ОСС(21°)
ТУ51-29-81
ВУ 163.0
ПК0+78
Скв. 148
Прилегающий участок EWE0426-MGL1-PIL-054-ALS-66020
1:500 - по горизонтали
1:200 - по вертикали
1:200 - по вертикали - грунты
ПК 0+00 Н. тр.
+21 ВУ 1α - 255° 00'
+38 ВУ 2α - 90° 00'
+61 ВУ 3α - 183° 00'
ПК 0+99 (ПК 1+80 проектн. газопровода)
Инженерно-геологическая характеристика
① Песок мелкий с прослойками суглинка и супесей мощностью до 0,8 m. согласно дополнения №3 к ШНК 4.02.01-04 группа грунта по трудности по разработки: механизированным способом (таблица 1-1а) относится к первому абзацу пункта 16, ручным способом (таблица 1-1в) относится к первому абзацу пункта 25, Ro-300 kPa, при водонасыщении Ro-100 kPa.
Уд. электросопр. грунтов, Ωm
Угодья
пески закрепленные джингил 1.5
Отметка земли, m
160.1
160.8
161.5
162.8
164.0
161.5
Расстояние, m
21
17
23
17
21
Пикеты, указатели километров
Планировочные отметки
Тип поперечного профиля
Проектные отметки (верх трубы)
Уклон ‰, длина участка, m
Исходная длина, m
99.0
Глубина траншеи, m
Категория участка газопровода
Трубы Ø х S, mm
Защита изоляции от механических повреждений
Балластировка и закрепление газопровода (тип балласта или крепления кол. шт)
Защитный кожух
Заводская изоляция трехслойная усиленного типа

Ведомость углов поворотов перемычки №1 в горизонтальной плоскости

№№ углов и створов	Величина левого угла	Длина линии, m	Радиус R, m	Угол α°	Тангенс T₁, m	Тангенс T₂, m	Кривая K, m	Бис-сектриса Б, m	
0+00		21							
ВУ 1	255°00'	17	5D	75°00'	(ОСС30°х2+15°)-5Д-1220 (12К60)-5,5-075-УТУ51-29-81				
ВУ 2	90°00'	23	5D	90°00'	(ОСС30°х3)-5Д-1220 (12К60)-5,5-075-УТУ51-29-81				
ВУ 3	183°00'	38	5D	3°00'	ОСС3°-5Д-1220 (12К60)-5,5-075-У ТУ51-29-81				
0+99		L-99							

Экспликация деталей и отдельных изделий перемычки№1

№ п. п.	Наименование деталей	Ед изм.	Кол.	Примечание
1	ОСС30°-5Д-1220 (12К60)-5,5-075-У ТУ51-29-81	шт	5	
2	ОСС 21°-5Д-1220 (12К60)-5,5-075-У ТУ51-29-81	шт	1	
3	ОСС 15°-5Д-1220 (12К60)-5,5-075-У ТУ51-29-81	шт	1	
4	ОСС 9°-5Д-1220 (12К60)-5,5-075-У ТУ51-29-81	шт	1	
5	ОСС 7,5°-5Д-1220 (12К60)-5,5-075-У ТУ51-29-81	шт	1	
6	ОСС 3°-5Д-1220 (12К60)-5,5-075-У ТУ51-29-81	шт	1	
7	Тройник ТСН 1220-1220-6,4-0,6-7,5-0,75 ТУ 51-29-81	шт	1	

Ведомость углов поворотов газопровода в горизонтальной плоскости

№№ углов и створов	Величина левого угла	Длина линии, m	Радиус R, m	Угол α°	Тангенс T₁, m	Тангенс T₂, m	Кривая K, m	Бис-сектриса Б, m	Составляющие элементы угла
0+00		21							
ВУ 1	270°00'	20	5D	90°00'	(ОСС 30°х3) -5Д-1220(12К60)-5,5-075-У ТУ51-29-81				
ВУ 2	90°00'	102	5D	90°00'	(ОСС 30°х3)-5Д-1220(12К60)-5,5-075-У ТУ51-29-81				
ВУ 3	261°00'	82	5D	81°00'	(ОСС 30°х2+21°) -5Д-1220(12К60)-5,5-075-У ТУ51-29-81				
ВУ 4	105°00'	1434	5D	75°00'	(ОСС 30°х2+15°)-5Д-1220 (12К60)-5,5-075-У ТУ51-29-81				
ВУ 5	202°00'	341	5D	22°00'	ОСС 21°-5Д-1220 (12К60)-5,5-075-У ТУ51-29-81				
20+00		L-2000							

Экспликация деталей и отдельных изделий газопровода

№ п. п.	Наименование деталей	Ед изм.	Кол.	Примечание
1	ОСС30°-5Д-1220 (12К60)-5,5-075-У ТУ51-29-81	шт	10	
2	ОСС 21°-5Д-1220 (12К60)-5,5-075-У ТУ51-29-81	шт	2	
3	ОСС 15°-5Д-1220 (12К60)-5,5-075-У ТУ51-29-81	шт	1	
4	ОСС 6°-5Д-1220 (12К60)-5,5-075-У ТУ51-29-81	шт	1	
5	ОСС 3°-5Д-1220 (12К60)-5,5-075-У ТУ51-29-81	шт	2	
6	Тройник ТСН 1220-1220-6,4-0,6-7,5-0,75 ТУ 51-29-81	шт	1	

1 Общие данные - чертеж EWE0426-MGL1-PIL-054-COM-660201

2. Ситуационный план см. EWE0426-MGL1-PIL-054-DRW-660202

3 До начала работ руководитель строительной организации должен разработать и согласовать схему и инструкцию по безопасному производству работ в охранной зоне газопровода и его сооружений.

4 Производство работ на данном участке вести в строгом соответствии с "Инструкцией по производству строительных работ в охранных зонах магистральных трубопроводов Мингазпрома" ВСН 51-1-80.

5 Ширину полосы отвода земель для строительства газопровода см. типовой чертеж EWE0426-MGL1-PIL-DRW-810201.

6 Охранную зону магистрального газопровода см. типовой чертеж EWE0426-MGL1-PIL-DRW-810202.

7 Поперечный разрез траншеи см. типовой чертеж EWE0426-MGL1-PIL-DRW-810203.

8. Перед рытьем траншеи на данном участке должна предусматриваться предварительная планировка строительной полосы (срезку грунта в зоне выполнить по проекту).

9. Точное местоположение и глубину заложения существующих трубопроводов определить шурфованием вручную и перед началом работ обозначить предупреждающими и разъясняющими знаками, освещаемыми в ночное время.

10. Земляные работы в зоне по 2 m в обе стороны от пересечений выполнить без применения ударных инструментов вручную в присутствии представителей эксплуатирующих организаций, и известить их о начале и окончании работ на пересечениях.

11. При пересечении с подземными коммуникациями контроль монтажных сварных соединений по 20 m в обе стороны выполнить радиографическим методом.

12. Проезд техники через существующий газопровод выполнить по специально устроенным переездам (ВТУ МГ-1).

13. Производство работ, сварку, контроль монтажных сварных соединений и испытание газопровода производить в соответствии с ШНК 2.05.06-22, QR 02.01, QR 06.08, ВСН 51-3-85, ВСН 005-88, ВСН 006-89, ВСН 011-88, ВСН 012-88, "Правилами техники безопасности при строительстве магистральных стальных трубопроводов".

14 На период эксплуатации по трассе газопровода установить следующие сигнальные знаки:
- на углах поворота в плане трассы опознавательный столб (85.00-08.00-000:00.08- МР);
- сигнальный знак, совмещенный с катодными выводами через 1 km (см. раздел ЭХЗ).

15. Номера существующих ниток изменены и диаметр существующих газопроводов в месте подключения принят 1220 по уточнению Заказчика в схеме PFD л. EWE0426-MGL1-P RE-054-PFD-610101-R2 и откорректированного изыскательского материала (письмо MGL-EM-PBG-EWE-0016).

16. Толщину стенки отводов должен просчитать Завод-изготовитель с учетом своих технологических возможностей, обеспечив прочность и надежность соединительных деталей на расчетный срок службы газопровода, и с учетом того что толщина стенки отводов не менее толщины стенки основной трубы.

17. Стыки врезки в существующий газопровод-гарантийные, которые должны быть в строгом соответствии с "Правилами безопасности при эксплуатации магистральных газопроводов" 2003 г.

18. Врезку в существующие газопроводы производить в соответствии с требованиями, изложенными в "Типовой инструкции на производство огневых работ на действующих магистральных газопроводах, газосборных сетях, газовых промыслов", утвержденных Мингазпромом 9 июня 1971 г., ВСН 006-89.

19. Размещение механизированных колонн, баз, стоянок машин и механизмов, складов ГСМ и другого оборудования осуществлять только за пределами опасной зоны газопровода.

20. Земляные работы в зоне по 5 м в обе стороны от врезки в существующий газопровод выполнить без применения ударных инструментов вручную в присутствии представителя организации, эксплуатирующей этот газопровод.

22. Производство работ при пересечении с существующим газопроводами вести в строгом соответствии с "Инструкцией по производству строительных работ в охранных зонах магистральных трубопроводов Мингазпрома" ВСН 51-1-80.

Рев.	Дата	Назначение ревизии	Проверил	Утвердил
A2	17.08.2026	Выпущено для строительства		
A1	16.07.2026	Выпущено для строительства		
R2	26.06.2026	Выпущено для рассмотрения		
R1	03.06.2026	Выпущено для рассмотрения		

ЗАКАЗЧИК: UZTRANSGAZ «TRANSGAZINJINIRING»
ГЕНЕРАЛЬНЫЙ ПОДРЯДЧИК: UZBEKENERGOTAMIR
ПОДРЯДЧИК: PBG Pro Build Generation
ГЕНЕРАЛЬНЫЙ ПРОЕКТИРОВЩИК: EAST WEST ENGINEERING

EWE0426-MGL1-PIL-054-ALS-660203-A2

«СТРОИТЕЛЬСТВО НОВЫХ НИТОК (УЧАСТКОВ) ГАЗОПРОВОДОВ «ГАЗЛИ - САРИМОЙ» И «АКЧАЛОК - ГАЗЛИ - НУКУС» ОБЩЕЙ ПРОТЯЖЕННОСТЬЮ НЕ МЕНЕЕ 275 КМ».

Изм.	Кол.уч.	Лист	№док.	Подпись	Дата
ГИП		Схабицкий А.			17.08.2026
Провер.		**Схабицкий А.**			17.08.2026
Исполн.		Шафиева О.			17.08.2026
Н.контр		Схабицкий А.			17.08.2026

ГАЗОПРОВОД «ГАЗЛИ-САРИМОЙ» (54 КМ)

Стадия	Лист	Листов
РД	1	1

План и продольный профиль газопровода ПК 0+00- ПК 20+00 и перемычки №1 ПК 0+00- ПК 0+99

ООО "EAST-WEST Engineering"
г. Ташкент 2026г.

Формат А2х5