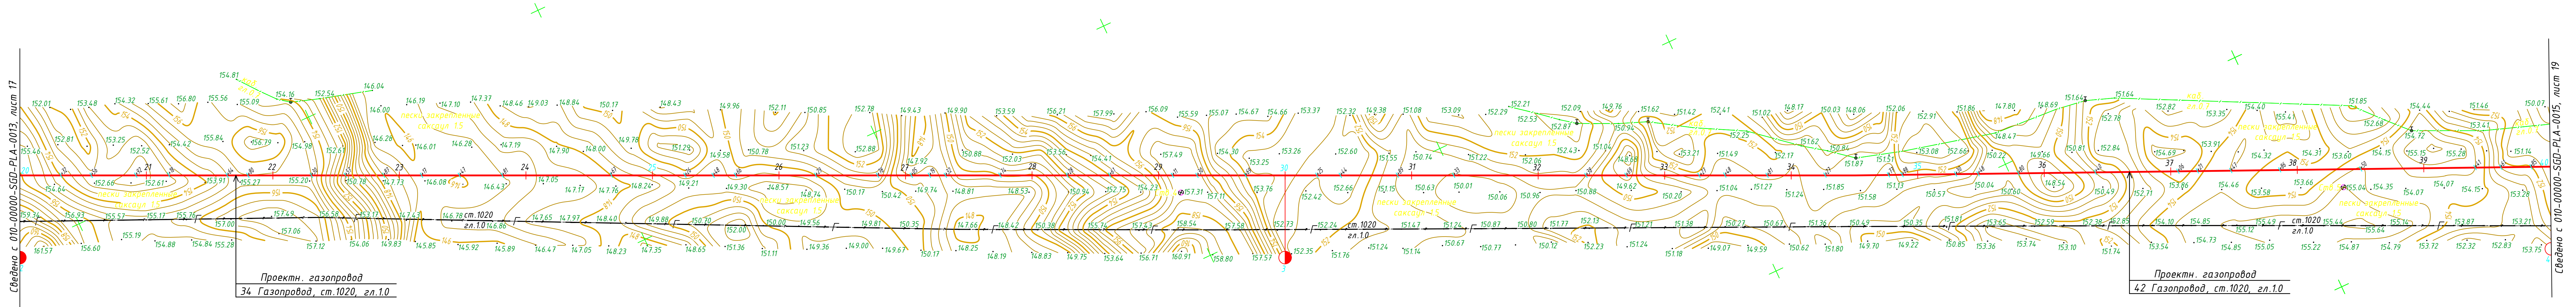
Сведено с 010-00000-SGD-PLA-0013, лист 17
Сведено с 010-00000-SGD-PLA-0015, лист 19
Проектн. газопровод
34 Газопровод, ст.1020, гл.1.0
42 Газопровод, ст.1020, гл.1.0
пески закрепленные саксаул 1.5
ст.1020
гл.1.0
20
21
22
23
24
25

Экспликация деталей и отдельных изделий

№ п. п.	Наименование деталей	Ед изм.	Кол.	Примечание
1	ОСС 7,5°-5Д-1220(12К60)-5,5-075-У ТУ51-29-81	шт	2	
2	ОСС 6°-5Д-1220(12К60)-5,5-075-У ТУ51-29-81	шт	1	
3	ОСС 3°-5Д-1220(12К60)-5,5-075-У ТУ51-29-81	шт	1	

1 Общие данные - чертеж EWE0426-MGL1-PIL-054-COM-660201
2 Ситуационный план - чертеж EWE0426-MGL1-PIL-054-DRW-660202
3 До начала работ руководитель строительной организации должен разработать и согласовать схему и инструкцию по безопасному производству работ в охранной зоне газопровода и его сооружений.
4 Производство работ на данном участке вести в строгом соответствии с "Инструкцией по производству строительных работ в охранных зонах магистральных трубопроводов Мингазпрома" ВСН 51-1-80.
5 Ширину полосы отвода земель для строительства газопровода см. типовой чертеж EWE0426-MGL1-PIL-DRW-810201.
6 Охранную зону магистрального газопровода см. типовой чертеж EWE0426-MGL1-PIL-DRW-810202.
7 Поперечный разрез траншеи см. типовой чертеж EWE0426-MGL1-PIL-DRW-810203.

Схема расположения листов

010-00000-SGD-PLA-0013, лист 17	010-00000-SGD-PLA-0014, лист 18	010-00000-SGD-PLA-0015, лист 19

1:2000 - по горизонтали
1:200 - по вертикали
1:200 - по вертикали - грунты


Прилегающий участок EWE0426-MGL1-PIL-054-ALS-660203
Прилегающий участок EWE0426-MGL1-PIL-054-ALS-660205
158
156
154
152
150
148
146
144
142
140
138
136
134
Инженерно-геологическая характеристика
Уд. электросопр. грунтов, Ωm
Угодья
пески закрепленные джингил 1.5
Отметка земли, m
Расстояние, m
Пикеты, указатель километров
ПК 20+00
ПК 40+00
Полка, выемка, насыпь, засыпка
Планировочные отметки
Тип поперечного профиля
Проектные отметки (верх трубы)
Уклон газопровода, ‰
Длина участка, m
Истинная длина, m
2001.2
Глубина траншеи, m
Категория участка газопровода
Трубы Φ x S, mm
III
1220x11
Тип изоляции газопровода
Заводская изоляция трехслойная усиленного типа
Защита изоляции от механических повреждений
Подсыпка мягким грунтом толщиной 0.1 м и обсыпка мягким грунтом толщиной 0.2 м над верхней образующей трубопровода
Балластировка и закрепление газопровода (тип балласта или крепежа кол. шаг)
Отсутствует
Защитный кожух Φ x S, mm / L, m
Отсутствует

① Песок мелкий с прослойками суглинка и супесей мощностью до 0,8 m. согласно дополнения №3 к ШНК 4.02.01-04 группа грунта по трудности по разработки: механизированным способом (таблица 1-1а) относится к первому абзацу пункта 16, ручным способом (таблица 1-1б) относится к первому абзацу пункта 25, Ro-300 kPa, при водонасыщении Ro-100 kPa.
② Песчаник низкой и средней прочности., согласно ШНК 4.02.01-04 группа грунта по трудности разработки механизированным способом (таблица 1-1) относится к пункту 30б, согласно дополнения №3 к ШНК 4.02.01-04 группа грунта по трудности разработки ручным способом (таблица 1-1б) относится ко второму абзацу пункта 26, Rc-до 1 MPa.
③ Глина с линзами песка, согласно дополнения №3 к ШНК 4.02.01-04 группа грунта по трудности по разработки: механизированным способом (таблица 1-1а) относится к первому абзацу пункта 5, ручным способом (таблица 1-1б) относится к первому абзацу пункта 7, Ro-400 kPa.
④ Алевролит низкой прочности., согласно дополнения №3 к ШНК 4.02.01-04 группа грунта по трудности по разработки: механизированным способом (таблица 1-1а) относится к первому абзацу пункта 1, ручным способом (таблица 1-1б) относится к первому абзацу пункта 1, Rc- до 1 MPa.
⑤ Насыпной слой

Согласовано

Геолог	Усмонов	
Геолог	Жонузоков	
Испол.	Насруллозода	
Топограф	Бахтигузин	
Топограф	Абдуллаев	
Гидролог	Бахадиров	

Взам. инв.№
Подп. и дата
Инв. № подл.

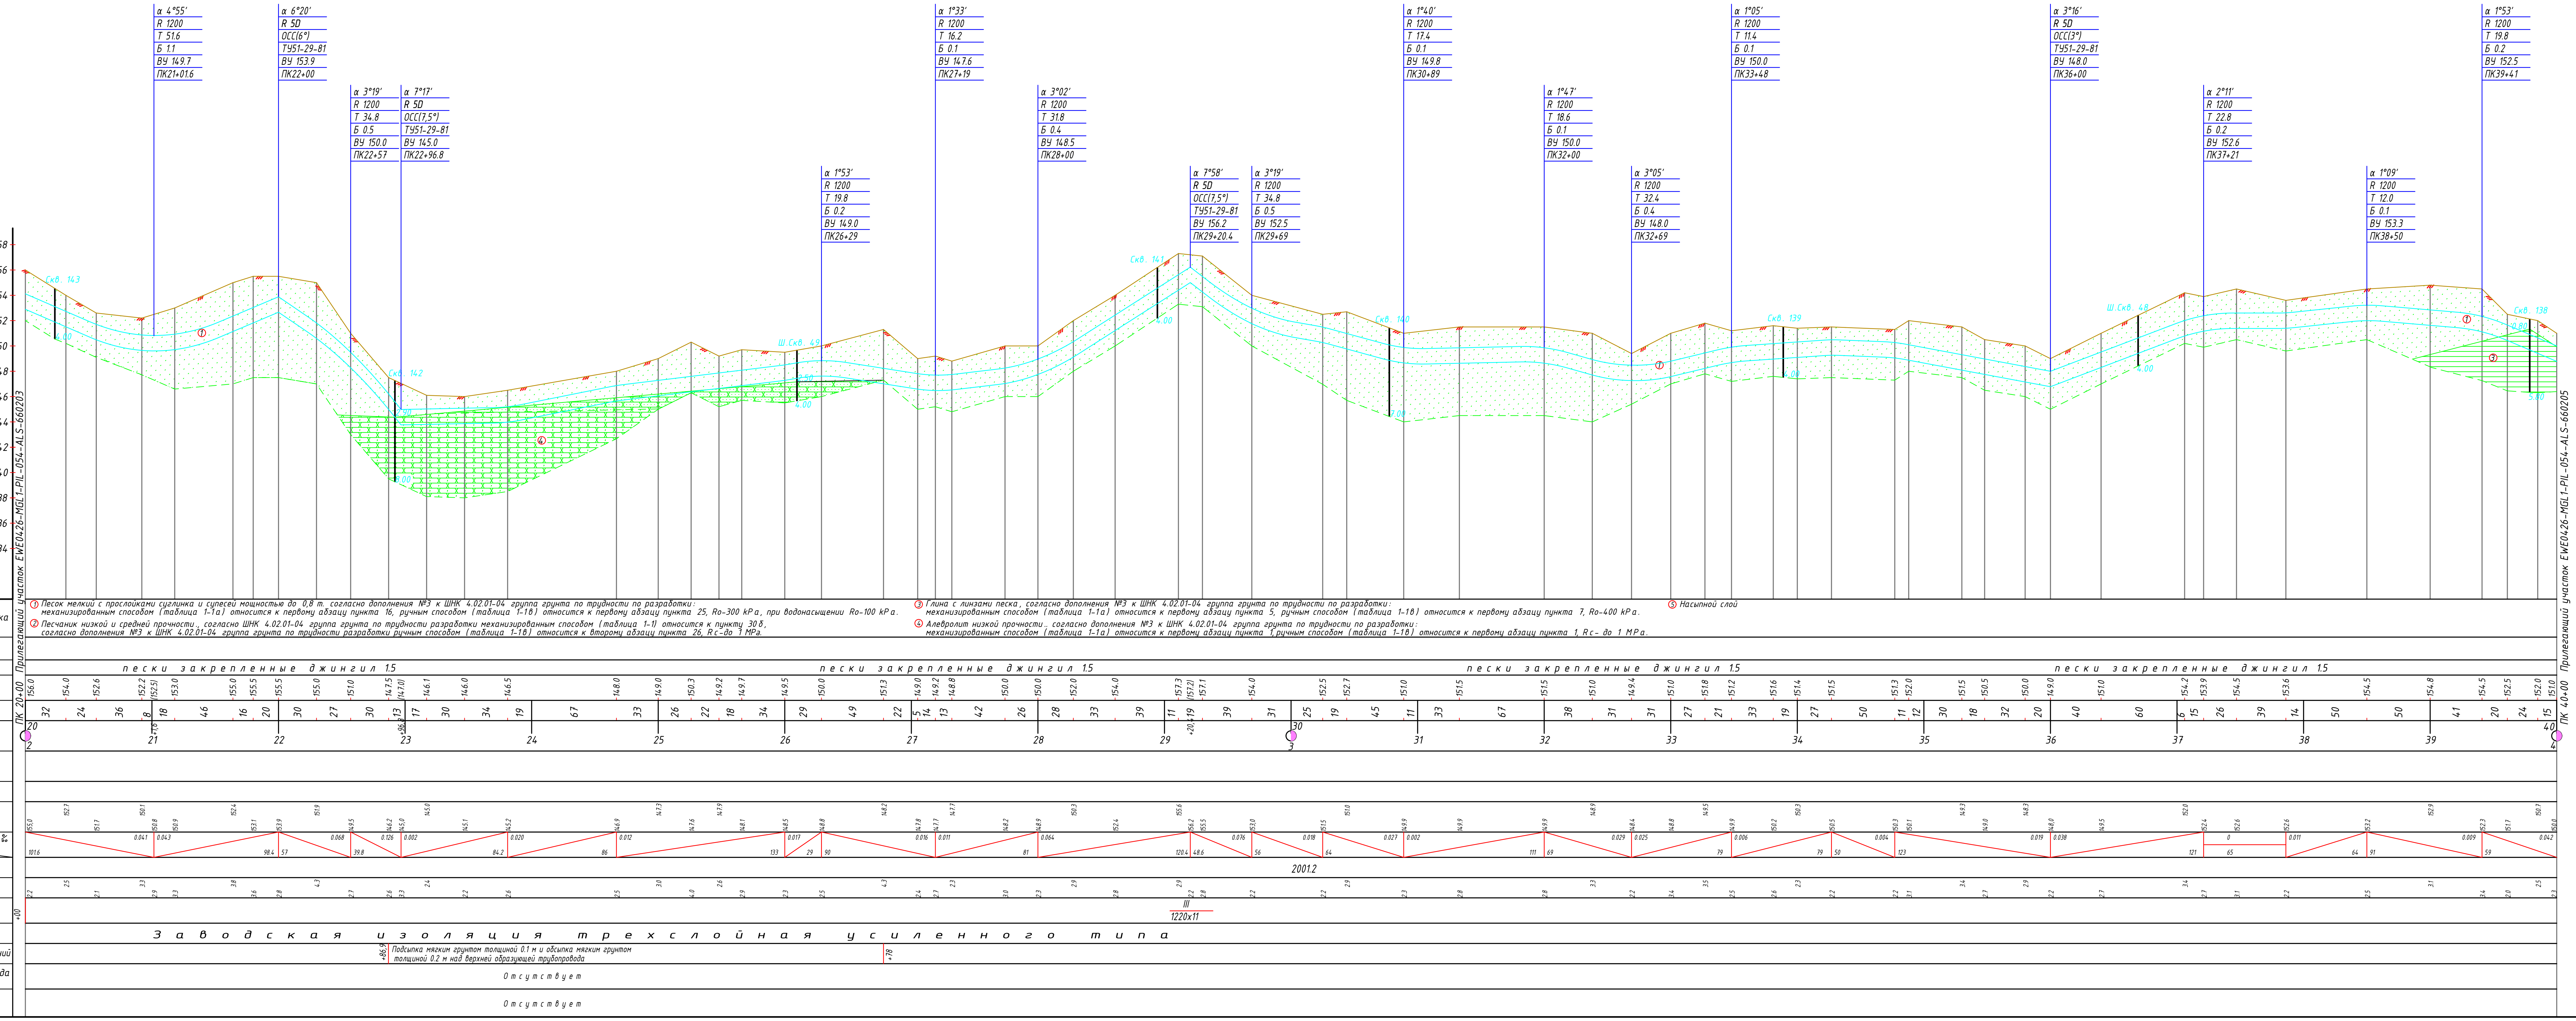Рев.	Дата	Назначение ревизии	Проверил	Утвердил
A2	17.08.2026	Выпущено для строительства		
A1	16.07.2026	Выпущено для строительства		
R2	26.06.2026	Выпущено для рассмотрения		
R1	03.06.2026	Выпущено для рассмотрения		

ЗАКАЗЧИК: UTG UZTRANSGAZ
ГЕНЕРАЛЬНЫЙ ПОДРЯДЧИК: UET UZBEKENERGOTAMIR
ПОДРЯДЧИК: PBG Pro Build Generation
ГЕНЕРАЛЬНЫЙ ПРОЕКТИРОВЩИК: EAST WEST ENGINEERING

EWE0426-MGL1-PIL-054-ALS-660204-A2

«СТРОИТЕЛЬСТВО НОВЫХ НИТОК (УЧАСТКОВ) ГАЗОПРОВОДОВ «ГАЗЛИ - САРИМОЙ» И «АКЧАЛОК - ГАЗЛИ - НУКУС» ОБЩЕЙ ПРОТЯЖЕННОСТЬЮ НЕ МЕНЕЕ 275 КМ».

Изм.	Кол.уч.	Лист	№док.	Подпись	Дата
ГИП		Схабицкий А.			17.08.2026
Провер.		Схабицкий А.			17.08.2026
Исполн.		Шафиева О.			17.08.2026
Н.контр		Схабицкий А.			17.08.2026

ГАЗОПРОВОД «ГАЗЛИ-САРИМОЙ» (54 КМ)

Стадия	Лист	Листов
РД	1	1

План и продольный профиль газопровода
ПК 20+00- ПК 40+00

EAST WEST ENGINEERING
ООО "EAST-WEST Engineering"
г. Ташкент 2026г.

Формат А2х4