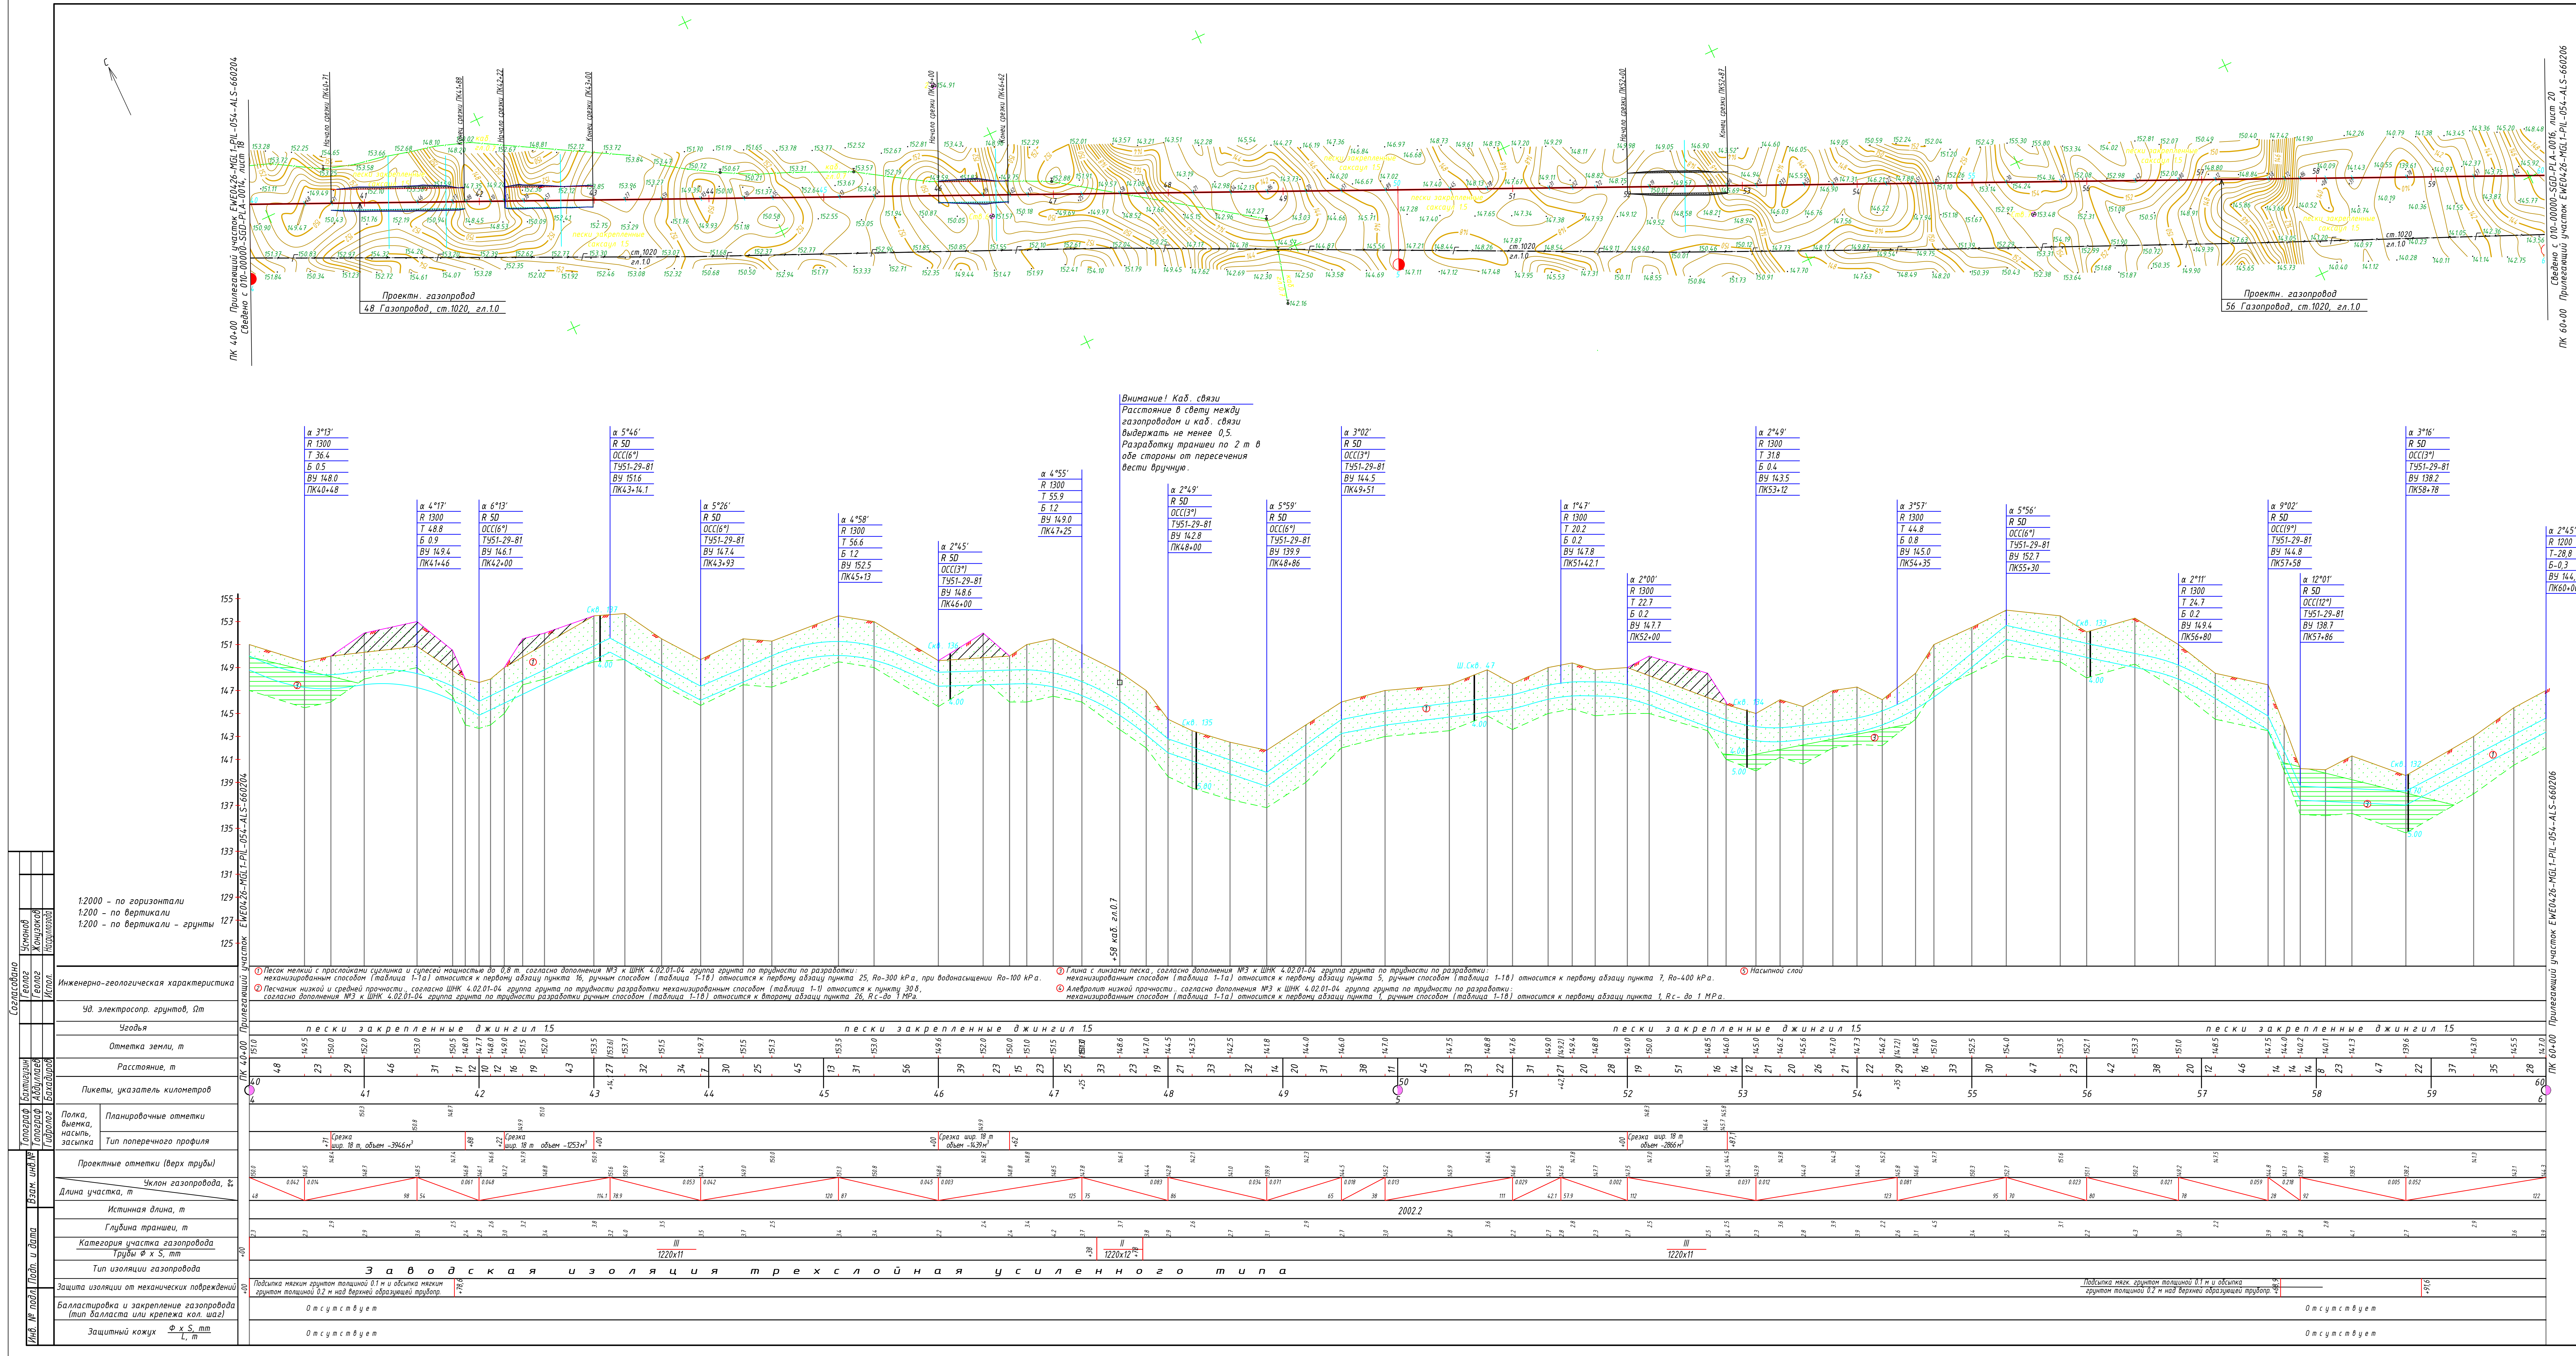
Проектир. газопровод
48 Газопровод, ст.1020, гл.1.0
56 Газопровод, ст.1020, гл.1.0
ПК 40+00 Прилегающий участок EWE0426-MGL1-PIL-054-ALS-660204
ПК 60+00 Прилегающий участок EWE0426-MGL1-PIL-054-ALS-660206
α 4°55'
R 1300
T 55.9
Б 1.2
ВУ 149.0
ПК47+25
α 2°49'
R 5D
ОСС(3°)
ТУ51-29-81
ВУ 142.8
α 5°59'
R 5D
ОСС(6°)
ТУ51-29-81
α 3°02'
R 5D
ОСС(3°)
ТУ51-29-81
ВУ 144.5
ПК49+51
+58 каб. гл.0.7
1:2000 - по горизонтали
1:200 - по вертикали
1:200 - по вертикали - грунты
Инженерно-геологическая характеристика
Уд. электросопр. грунтов, Ωm
Угодья
Отметка земли, m
Расстояние, m
Пикеты, указатель километров
Полка, выемка, насыпь, засыпка
Планировочные отметки
Тип поперечного профиля
Проектные отметки (верх трубы)
Уклон газопровода, ‰
Длина участка, m
Истинная длина, m
Глубина траншеи, m
Категория участка газопровода
Трубы Ф x S, mm
Тип изоляции газопровода
Защита изоляции от механических повреждений
Балластировка и закрепление газопровода (тип балласта или крепежа кол. шаг)
Защитный кожух Ф x S, mm / L, m
пески закрепленные джингил 1.5
2002.2
III 1220x11
II 1220x12
Заводская изоляция трехслойная усиленного типа
Подсыпка мягким грунтом толщиной 0.1 м и обсыпка мягким грунтом толщиной 0.2 м над верхней образующей трубопр.
Отсутствует
Согласовано
Топограф Бахтигузин
Топограф Абдуллаев
Гидролог Бахадиров
Геолог Усмонов
Геолог Жонузоков
Испол. Насруллозода
Взам. инв.№
Подп. и дата
Инв. № подл.

Внимание! Каб. связи
Расстояние в свету между газопроводом и каб. связи выдержать не менее 0,5.
Разработку траншеи по 2 m в обе стороны от пересечения вести вручную.

① Песок мелкий с прослойками суглинка и супесей мощностью до 0,8 m. согласно дополнения №3 к ШНК 4.02.01-04 группа грунта по трудности по разработки: механизированным способом (таблица 1-1а) относится к первому абзацу пункта 16, ручным способом (таблица 1-1б) относится к первому абзацу пункта 25, Ro-300 kPa, при водонасыщении Ro-100 kPa.

② Песчаник низкой и средней прочности., согласно ШНК 4.02.01-04 группа грунта по трудности разработки механизированным способом (таблица 1-1) относится к пункту 30 б, согласно дополнения №3 к ШНК 4.02.01-04 группа грунта по трудности разработки ручным способом (таблица 1-1б) относится к второму абзацу пункта 26, Rc-до 1 MPa.

③ Глина с линзами песка, согласно дополнения №3 к ШНК 4.02.01-04 группа грунта по трудности по разработки: механизированным способом (таблица 1-1а) относится к первому абзацу пункта 5, ручным способом (таблица 1-1б) относится к первому абзацу пункта 7, Ro-400 kPa.

④ Алевролит низкой прочности., согласно дополнения №3 к ШНК 4.02.01-04 группа грунта по трудности по разработки: механизированным способом (таблица 1-1а) относится к первому абзацу пункта 1, ручным способом (таблица 1-1б) относится к первому абзацу пункта 1, Rc- до 1 MPa.

⑤ Насыпной слой

Экспликация деталей и отдельных изделий

№ п. п.	Наименование деталей	Ед изм.	Кол.	Примечание
1	ОСС 12° 1220-5Д-1220(12К60)-5,5-075-У ТУ51-29-81	шт	1	
2	ОСС 9°-5Д-1220(12К60)-5,5-075-У ТУ51-29-81	шт	1	
3	ОСС 6°-5Д-1220(12К60)-5,5-075-У ТУ51-29-81	шт	5	
4	ОСС 3°-5Д-1220(12К60)-5,5-075-У ТУ51-29-81	шт	4	

Схема расположения листов

010-00000-SGD-PLA-0014, лист 18	010-00000-SGD-PLA-0015, лист 19	010-00000-SGD-PLA-0016, лист 20

1 Общие данные - чертеж EWE0426-MGL1-PIL-054-COM-660201
2 Ситуационный план см. EWE0426-MGL1-PIL-054-DRW-660202
3 Точное местоположение и глубину заложения существующих коммуникаций определить шурфованием вручную и перед началом работ обозначить предупреждающими и разъясняющими знаками, освещаемыми в ночное время.
4 Земляные работы в зоне по 2 м в обе стороны от пересечений выполнить без применения ударных инструментов вручную в присутствии представителей эксплуатирующих организаций и известить их о начале и окончании работ на пересечениях.
5 До начала работ руководитель строительной организации должен разработать и согласовать схему и инструкцию по безопасному производству работ в охранной зоне газопровода и его сооружений.
6 Проезд техники через существующие трубопроводы выполнить по специально устроенному переезду, сделанному из щебеночной подушки, с укладкой бетонных плит по ВТУ МГ-1.
7 Производство работ на данном участке вести в строгом соответствии с "Инструкцией по производству строительных работ в охранных зонах магистральных трубопроводов Мингазпрома" ВСН 51-1-80.
8 Ширину полосы отвода земель для строительства газопровода см. типовой чертеж EWE0426-MGL1-PIL-DRW-810201.
9 Охранную зону магистрального газопровода см. типовой чертеж EWE0426-MGL1-PIL-DRW-810202.
10 Поперечный разрез траншеи см. типовой чертеж EWE0426-MGL1-PIL-DRW-810203.
11. Работы на пересечении с кабелем связи производить в присутствии представителей эксплуатирующих организаций и известить их о начале и окончании работ на пересечении.
12. Для защиты кабеля связи от механических повреждений заключить его в полиэтиленовую трубу, концы которой вывести в каждую сторону от газопровода не менее чем на 2 м.

Рев.	Дата	Назначение ревизии	Проверил	Утвердил
A2	17.08.2026	Выпущено для строительства		
A1	16.07.2026	Выпущено для строительства		
R2	26.06.2026	Выпущено для рассмотрения		
R1	03.06.2026	Выпущено для рассмотрения		

ЗАКАЗЧИК: UTG UZTRANSGAZ «TRANSGAZINJINIRING»
ГЕНЕРАЛЬНЫЙ ПОДРЯДЧИК: UET UZBEKENERGOTAMIR
ПОДРЯДЧИК: PBG Pro Build Generation
ГЕНЕРАЛЬНЫЙ ПРОЕКТИРОВЩИК: EAST WEST ENGINEERING

EWE0426-MGL1-PIL-054-ALS-660205-A2

«СТРОИТЕЛЬСТВО НОВЫХ НИТОК (УЧАСТКОВ) ГАЗОПРОВОДОВ «ГАЗЛИ - САРИМОЙ» И «АКЧАЛОК - ГАЗЛИ - НУКУС» ОБЩЕЙ ПРОТЯЖЕННОСТЬЮ НЕ МЕНЕЕ 275 КМ».

Изм.	Кол.уч.	Лист	№док.	Подпись	Дата
ГИП		Схабицкий А.			17.08.2026
Провер.		**Схабицкий А.**			17.08.2026
Исполн.		Шафиева О.			17.08.2026
Н.контр		Схабицкий А.			17.08.2026

ГАЗОПРОВОД «ГАЗЛИ-САРИМОЙ» (54 КМ)

Стадия	Лист	Листов
РД	1	1

План и продольный профиль газопровода
ПК 40+00- ПК 60+00

EAST WEST ENGINEERING
ООО "EAST-WEST Engineering"
г. Ташкент 2026г.

Формат А2х4