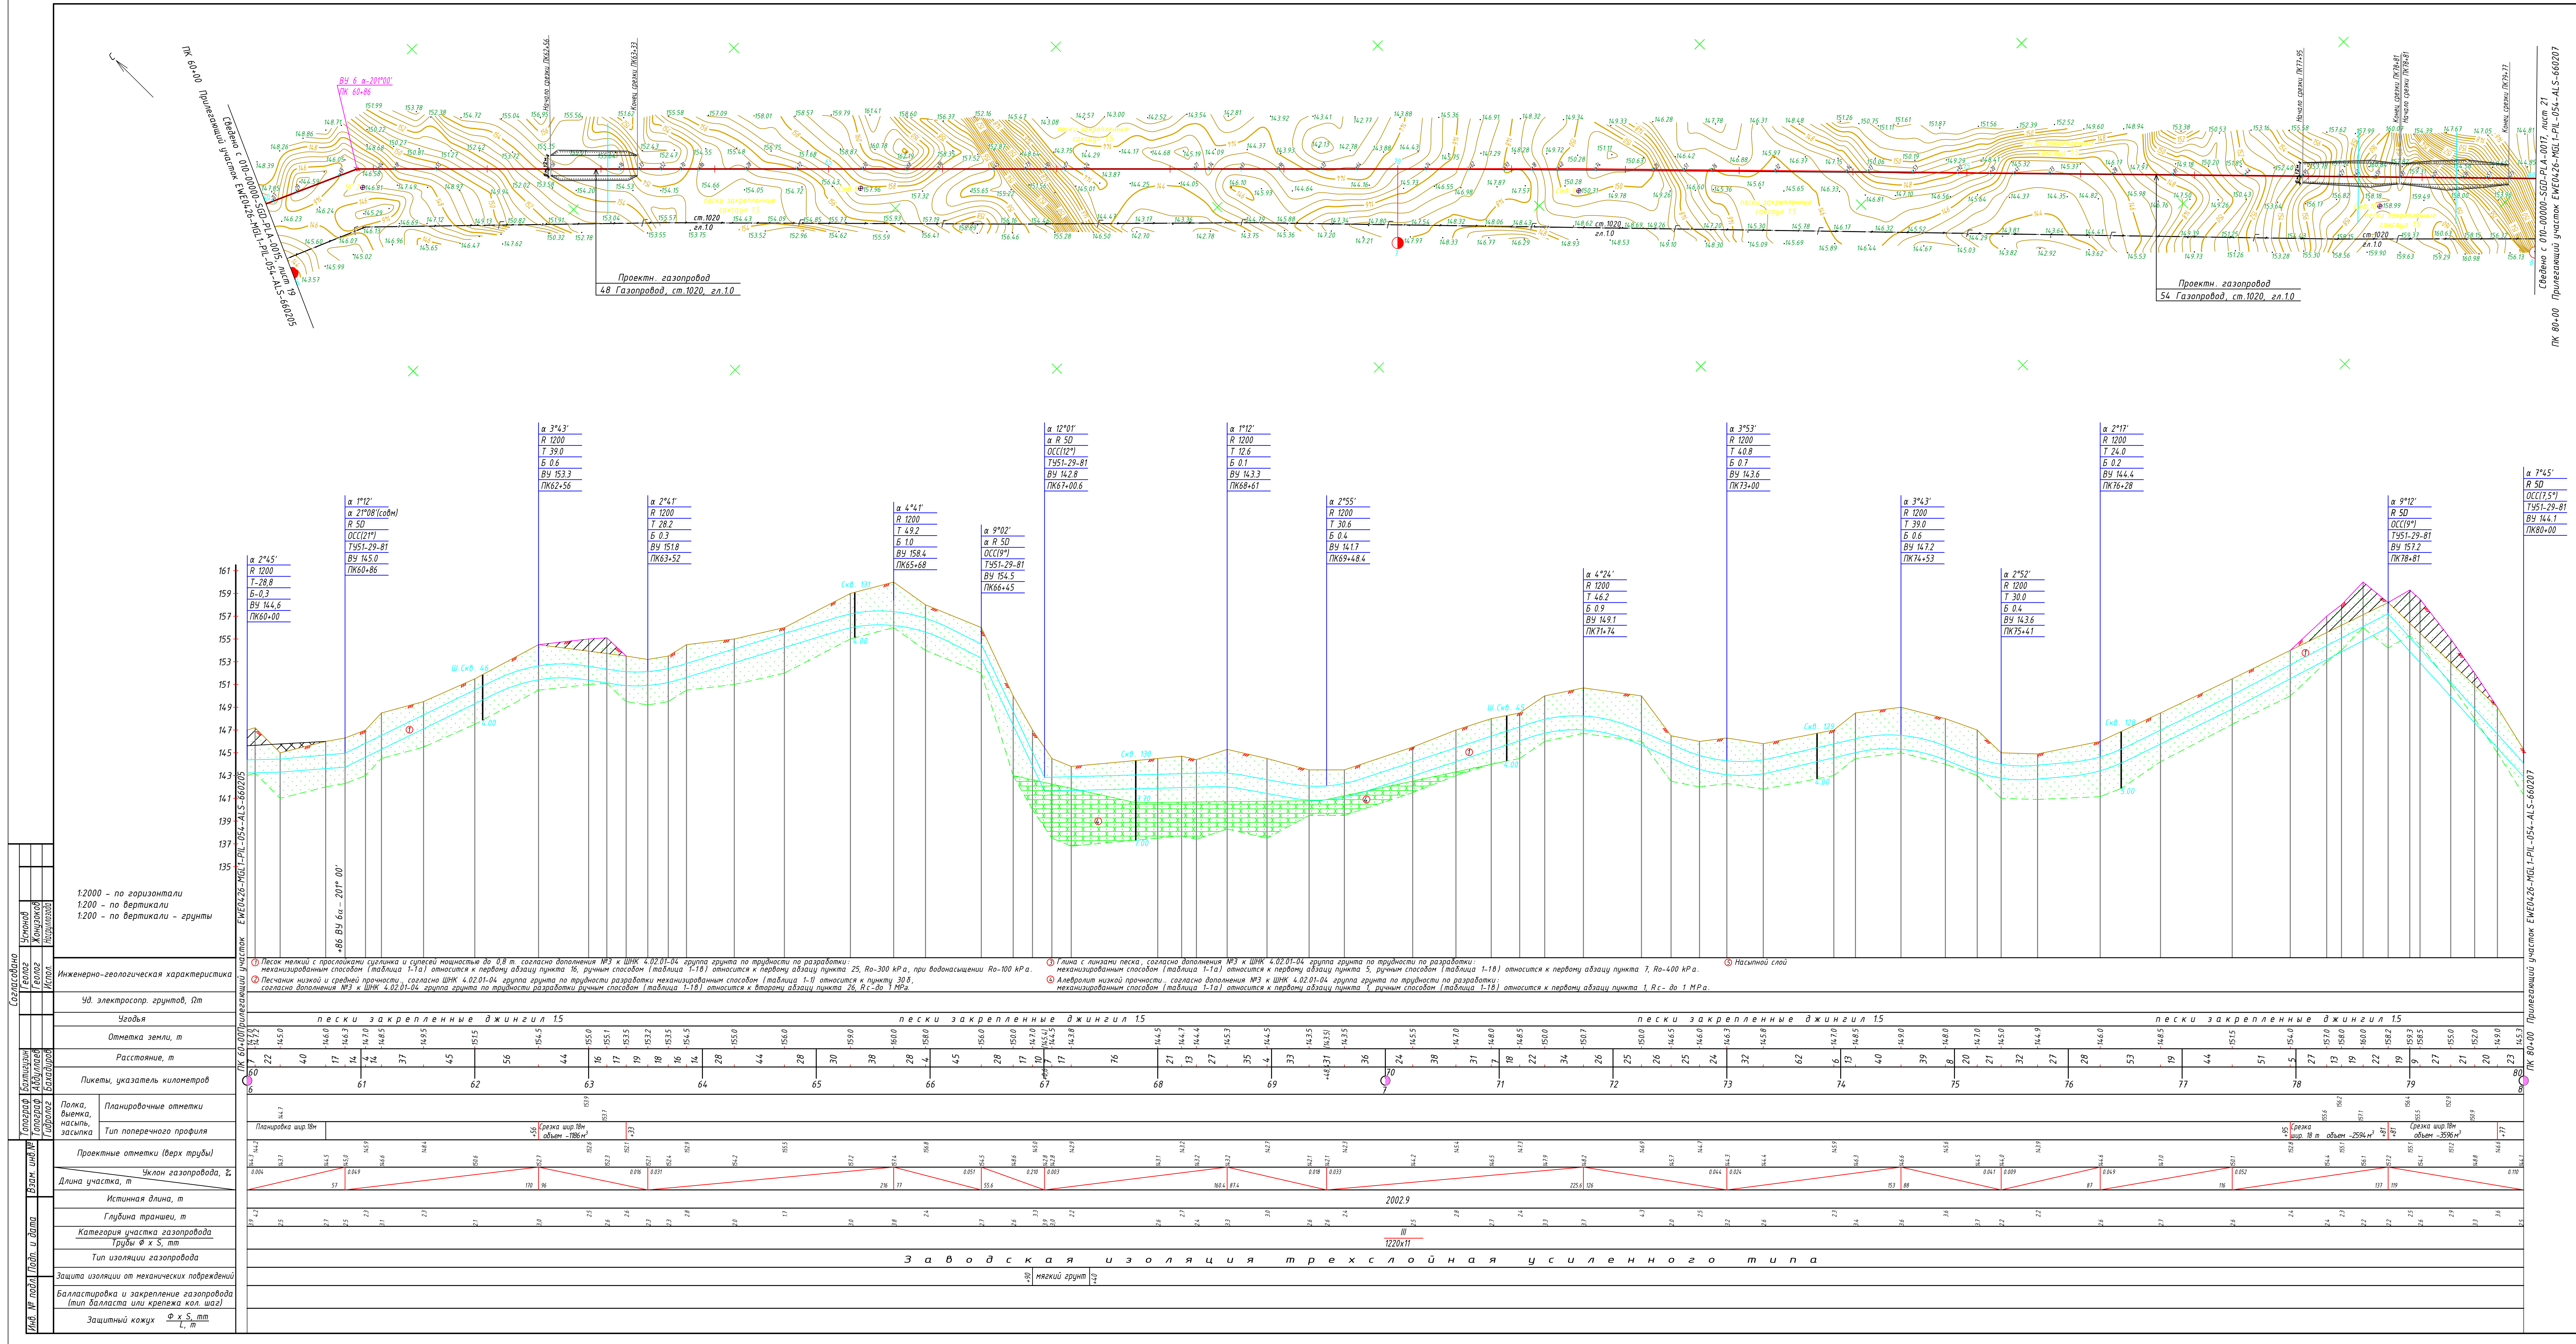
Сведения с 010-00000-SGD-PLA-0015 лист 19 Прилегающий участок EWE0426-MGL1-PIL-054-ALS-660205
ПК 60+00
Сведения с 010-00000-SGD-PLA-0017, лист 21 Прилегающий участок EWE0426-MGL1-PIL-054-ALS-660207
ПК 80+00
Проектн. газопровод
48 Газопровод, ст.1020, гл.1.0
54 Газопровод, ст.1020, гл.1.0
ПК 60+00 Прилегающий участок EWE0426-MGL1-PIL-054-ALS-660205
ПК 80+00 Прилегающий участок EWE0426-MGL1-PIL-054-ALS-660207
+86 ВУ 6α – 201° 00'
пески закрепленные джингил 1.5
Планировка шир.18м
Заводская изоляция трехслойная усиленного типа
2002.9
III
1220х11
мягкий грунт
Инженерно-геологическая характеристика
Уд. электросопр. грунтов, Ωm
Угодья
Отметка земли, m
Расстояние, m
Пикеты, указатель километров
Полка, выемка, насыпь, засыпка
Планировочные отметки
Тип поперечного профиля
Проектные отметки (верх трубы)
Уклон газопровода, ‰
Длина участка, m
Истинная длина, m
Глубина траншеи, m
Категория участка газопровода / Трубы Φ x S, mm
Тип изоляции газопровода
Защита изоляции от механических повреждений
Балластировка и закрепление газопровода (тип балласта или крепежа кол. шаг)
Защитный кожух Φ x S, mm / L, m
Согласовано
Топограф Бахтигузин
Топограф Абдуллаев
Гидролог Бахадиров
Геолог Усмонов
Геолог Жонузоков
Испол. Насруллозода
Взам. инв.№
Подп. и дата
Инв. № подл.

1:2000 – по горизонтали
1:200 – по вертикали
1:200 – по вертикали – грунты

① Песок мелкий с прослойками суглинка и супесей мощностью до 0,8 m. согласно дополнения №3 к ШНК 4.02.01-04 группа грунта по трудности по разработки: механизированным способом (таблица 1-1а) относится к первому абзацу пункта 16, ручным способом (таблица 1-1в) относится к первому абзацу пункта 25, Ro-300 kPa, при водонасыщении Ro-100 kPa.

② Песчаник низкой и средней прочности., согласно ШНК 4.02.01-04 группа грунта по трудности разработки механизированным способом (таблица 1-1) относится к пункту 30 б, согласно дополнения №3 к ШНК 4.02.01-04 группа грунта по трудности разработки ручным способом (таблица 1-1в) относится к второму абзацу пункта 26, Rc-до 1 MPa.

③ Глина с линзами песка, согласно дополнения №3 к ШНК 4.02.01-04 группа грунта по трудности по разработки: механизированным способом (таблица 1-1а) относится к первому абзацу пункта 5, ручным способом (таблица 1-1в) относится к первому абзацу пункта 7, Ro-400 kPa.

④ Алевролит низкой прочности.. согласно дополнения №3 к ШНК 4.02.01-04 группа грунта по трудности по разработки: механизированным способом (таблица 1-1а) относится к первому абзацу пункта 1, ручным способом (таблица 1-1в) относится к первому абзацу пункта 1, Rc- до 1 MPa.

⑤ Насыпной слой

Ведомость углов поворотов газопровода в горизонтальной плоскости

№№ углов и створов	Величина левого угла	Длина линии, m	Элементы кривых						
			Радиус R, m	Угол α°	Тангенс T₁, m	Тангенс T₂, m	Кривая K, m	Биссектриса Б, m	Составляющие элементы угла
60+00		86							
ВУ 6	201°00'	914	5D	21°00'	ОСС 21°-5Д-1220 (12К60)-5,5-075-У ТУ51-29-81				
80+00		L-2000							

Схема расположения листов

010-00000-SGD-PLA-0015, лист 19	010-00000-SGD-PLA-0016, лист 20	010-00000-SGD-PLA-0017, лист 21

Экспликация деталей и отдельных изделий

№ п. п.	Наименование деталей	Ед изм.	Кол.	Примечание
1	ОСС 21°-5Д-1220 (12К60)-5,5-075-У ТУ51-29-81	шт	1	
2	ОСС 12°-5Д-1220 (12К60)-5,5-075-У ТУ51-29-81	шт	1	
3	ОСС 9°-5Д-1220 (12К60)-5,5-075-У ТУ51-29-81	шт	2	
4	ОСС 7,5°-5Д-1220 (12К60)-5,5-075-У ТУ51-29-81	шт	1	

1 Общие данные - чертеж EWE0426-MGL1-PIL-054-COM-660201
2 Ситуационный план см. EWE0426-MGL1-PIL-054-DRW-660202
3 До начала работ руководитель строительной организации должен разработать и согласовать схему и инструкцию по безопасному производству работ в охранной зоне газопровода и его сооружений.
4 Производство работ на данном участке вести в строгом соответствии с "Инструкцией по производству строительных работ в охранных зонах магистральных трубопроводов Мингазпрома" ВСН 51-1-80.
5 Ширину полосы отвода земель для строительства газопровода см. типовой чертеж EWE0426-MGL1-PIL-DRW-810201.
6 Охранную зону магистрального газопровода см. типовой чертеж EWE0426-MGL1-PIL-DRW-810202.
7 Поперечный разрез траншеи см. типовой чертеж EWE0426-MGL1-PIL-DRW-810203.

Рев.	Дата	Назначение ревизии	Проверил	Утвердил
A2	17.08.2026	Выпущено для строительства		
A1	16.07.2026	Выпущено для строительства		
R2	26.06.2026	Выпущено для рассмотрения		
R1	03.06.2026	Выпущено для рассмотрения		

ЗАКАЗЧИК: UTG UZTRANSGAZ
ГЕНЕРАЛЬНЫЙ ПОДРЯДЧИК: UET UZBEKENERGOTAMIR
ПОДРЯДЧИК: PBG Pro Build Generation
ГЕНЕРАЛЬНЫЙ ПРОЕКТИРОВЩИК: EAST WEST ENGINEERING

EWE0426-MGL1-PIL-054-ALS-660206-A2

«СТРОИТЕЛЬСТВО НОВЫХ НИТОК (УЧАСТКОВ) ГАЗОПРОВОДОВ «ГАЗЛИ - САРИМОЙ» И «АКЧАЛОК - ГАЗЛИ - НУКУС» ОБЩЕЙ ПРОТЯЖЕННОСТЬЮ НЕ МЕНЕЕ 275 КМ».

Изм.	Кол.уч.	Лист	№док.	Подпись	Дата
ГИП		Схабицкий А.			17.08.2026
Провер.		**Схабицкий А.**			17.08.2026
Исполн.		Шафиева О.			17.08.2026
Н.контр		Схабицкий А.			17.08.2026

ГАЗОПРОВОД «ГАЗЛИ-САРИМОЙ» (54 КМ)

Стадия	Лист	Листов
РД	1	1

План и продольный профиль газопровода ПК 60+00- ПК 80+00

ООО "EAST-WEST Engineering"
г. Ташкент 2026г.

Формат A2x4