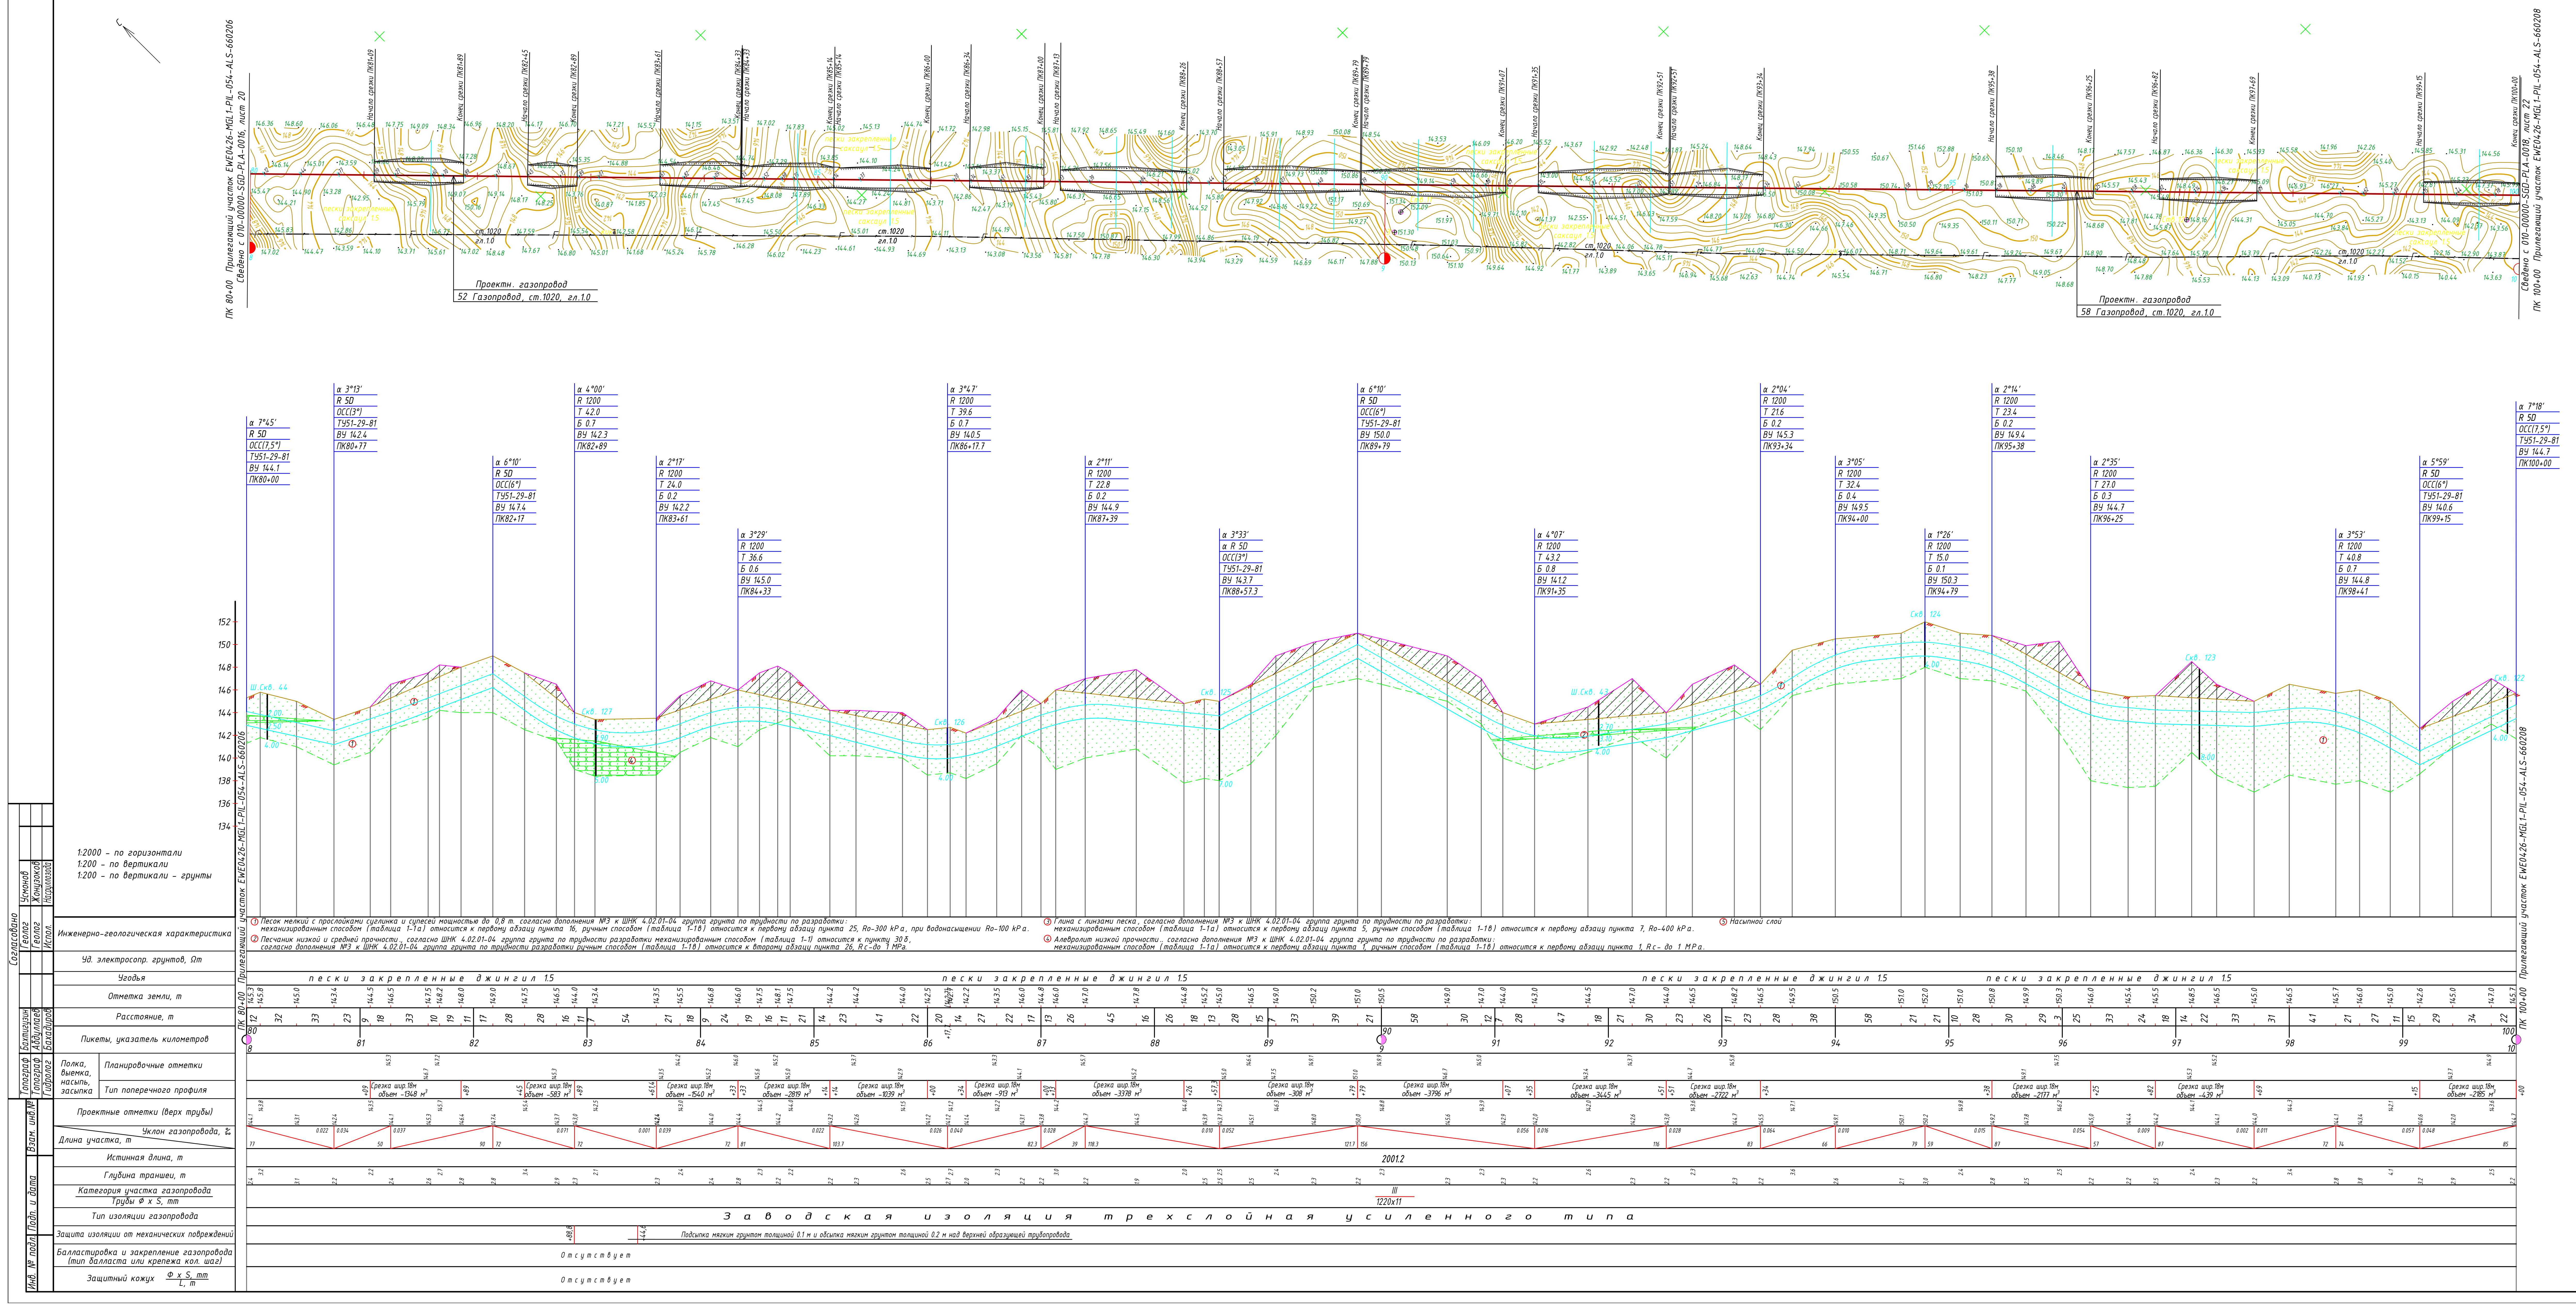
ПК 80+00 Прилегающий участок EWE0426-MGL1-PIL-054-ALS-660206
Сведено с 010-00000-SGD-PLA-0016, лист 20
ПК 100+00 Прилегающий участок EWE0426-MGL1-PIL-054-ALS-660208
Сведено с 010-00000-SGD-PLA-0018, лист 22
Начало срезки ПК81+09
Конец срезки ПК81+89
Начало срезки ПК82+45
Конец срезки ПК82+89
Начало срезки ПК83+61
пески закрепленные саксаул 1.5
ст.1020
гл.1.0
Проектн. газопровод
52 Газопровод, ст.1020, гл.1.0
58 Газопровод, ст.1020, гл.1.0
134
136
138
140
142
144
146
148
150
152
Инженерно-геологическая характеристика
Уд. электросопр. грунтов, Ωm
Угодья
Отметка земли, m
Расстояние, m
Пикеты, указатель километров
Полка, выемка, насыпь, засыпка
Планировочные отметки
Тип поперечного профиля
Проектные отметки (верх трубы)
Уклон газопровода, ‰
Длина участка, m
Истинная длина, m
Глубина траншеи, m
Категория участка газопровода
Трубы Φ x S, mm
Тип изоляции газопровода
Защита изоляции от механических повреждений
Балластировка и закрепление газопровода (тип балласта или крепежа кол. шаг)
Защитный кожух Φ x S, mm / L, m
пески закрепленные джингил 1.5
Срезка шир.18м объем -1348 m³
Срезка шир.18м объем -583 m³
Срезка шир.18м объем -1540 m³
Срезка шир.18м объем -2819 m³
Срезка шир.18м объем -1039 m³
Срезка шир.18м объем -913 m³
Срезка шир.18м объем -3378 m³
Срезка шир.18м объем -308 m³
Срезка шир.18м объем -3796 m³
Срезка шир.18м объем -3445 m³
2001.2
III
1220x11
Заводская изоляция трехслойная усиленного типа
Подсыпка мягким грунтом толщиной 0.1 м и обсыпка мягким грунтом толщиной 0.2 м над верхней образующей трубопровода
Отсутствует
Отсутствует

Согласовано

Геолог	Усмонов	
Геолог	Жонузоков	
Испол.	Насруллозода	
Топограф	Бахтигузин	
Топограф	Абдуллаев	
Гидролог	Бахадиров	

Взам. инв.№

Подп. и дата

Инв. № подл.

1:2000 – по горизонтали
1:200 – по вертикали
1:200 – по вертикали – грунты

① Песок мелкий с прослойками суглинка и супесей мощностью до 0,8 m. согласно дополнения №3 к ШНК 4.02.01-04 группа грунта по трудности по разработки: механизированным способом (таблица 1-1а) относится к первому абзацу пункта 16, ручным способом (таблица 1-1в) относится к первому абзацу пункта 25, Ro-300 kPa, при водонасыщении Ro-100 kPa.

② Песчаник низкой и средней прочности, согласно ШНК 4.02.01-04 группа грунта по трудности разработки механизированным способом (таблица 1-1) относится к пункту 30 б, согласно дополнения №3 к ШНК 4.02.01-04 группа грунта по трудности разработки ручным способом (таблица 1-1в) относится к второму абзацу пункта 26, Rc-до 1 MPa.

③ Глина с линзами песка, согласно дополнения №3 к ШНК 4.02.01-04 группа грунта по трудности по разработки: механизированным способом (таблица 1-1а) относится к первому абзацу пункта 5, ручным способом (таблица 1-1в) относится к первому абзацу пункта 7, Ro-400 kPa.

④ Алевролит низкой прочности. согласно дополнения №3 к ШНК 4.02.01-04 группа грунта по трудности по разработки: механизированным способом (таблица 1-1а) относится к первому абзацу пункта 1, ручным способом (таблица 1-1в) относится к первому абзацу пункта 1, Rc- до 1 MPa.

⑤ Насыпной слой

Экспликация деталей и отдельных изделий

№ п. п.	Наименование деталей	Ед изм.	Кол.	Примечание
1	ОСС 6°-5Д-1220(12К60)-5,5-075-У ТУ51-29-81	шт	3	
2	ОСС 3°-5Д-1220(12К60)-5,5-075-У ТУ51-29-81	шт	2	

Схема расположения листов

010-00000-SGD-PLA-0016, лист 20	010-00000-SGD-PLA-0017, лист 21	010-00000-SGD-PLA-0018, лист 22

1 Общие данные - чертеж EWE0426-MGL1-PIL-054-COM-660201
2 Ситуационный план см. EWE0426-MGL1-PIL-054-DRW-660202
3 Производство работ на данном участке вести в строгом соответствии с "Инструкцией по производству строительных работ в охранных зонах магистральных трубопроводов Мингазпрома" ВСН 51-1-80.
4 Ширину полосы отвода земель для строительства газопровода см. типовой чертеж EWE0426-MGL1-PIL-DRW-810201.
5 Охранную зону магистрального газопровода см. типовой чертеж EWE0426-MGL1-PIL-DRW-810202.
6 Поперечный разрез траншеи см. типовой чертеж EWE0426-MGL1-PIL-DRW-810203.

Рев.	Дата	Назначение ревизии	Проверил	Утвердил
A2	17.08.2026	Выпущено для строительства		
A1	16.07.2026	Выпущено для строительства		
R2	26.06.2026	Выпущено для рассмотрения		
R1	03.06.2026	Выпущено для рассмотрения		

ЗАКАЗЧИК: UZTRANSGAZ ГЕНЕРАЛЬНЫЙ ПОДРЯДЧИК: UZBEKENERGOTAMIR ПОДРЯДЧИК: PBG Pro Build Generation ГЕНЕРАЛЬНЫЙ ПРОЕКТИРОВЩИК: EAST WEST ENGINEERING

EWE0426-MGL1-PIL-054-ALS-660207-A2

«СТРОИТЕЛЬСТВО НОВЫХ НИТОК (УЧАСТКОВ) ГАЗОПРОВОДОВ «ГАЗЛИ – САРИМОЙ» И «АКЧАЛОК – ГАЗЛИ – НУКУС» ОБЩЕЙ ПРОТЯЖЕННОСТЬЮ НЕ МЕНЕЕ 275 КМ».

Изм.	Кол.уч.	Лист	№док.	Подпись	Дата
ГИП		Схабицкий А.			17.08.2026
Провер.		Схабицкий А.			17.08.2026
Исполн.		Шафиева О.			17.08.2026
Н.контр		Схабицкий А.			17.08.2026

ГАЗОПРОВОД «ГАЗЛИ-САРИМОЙ» (54 КМ)

Стадия	Лист	Листов
РД	1	1

План и продольный профиль газопровода
ПК 80+00– ПК 100+00

ООО "EAST-WEST Engineering"
г. Ташкент 2026г.

Формат A2x4