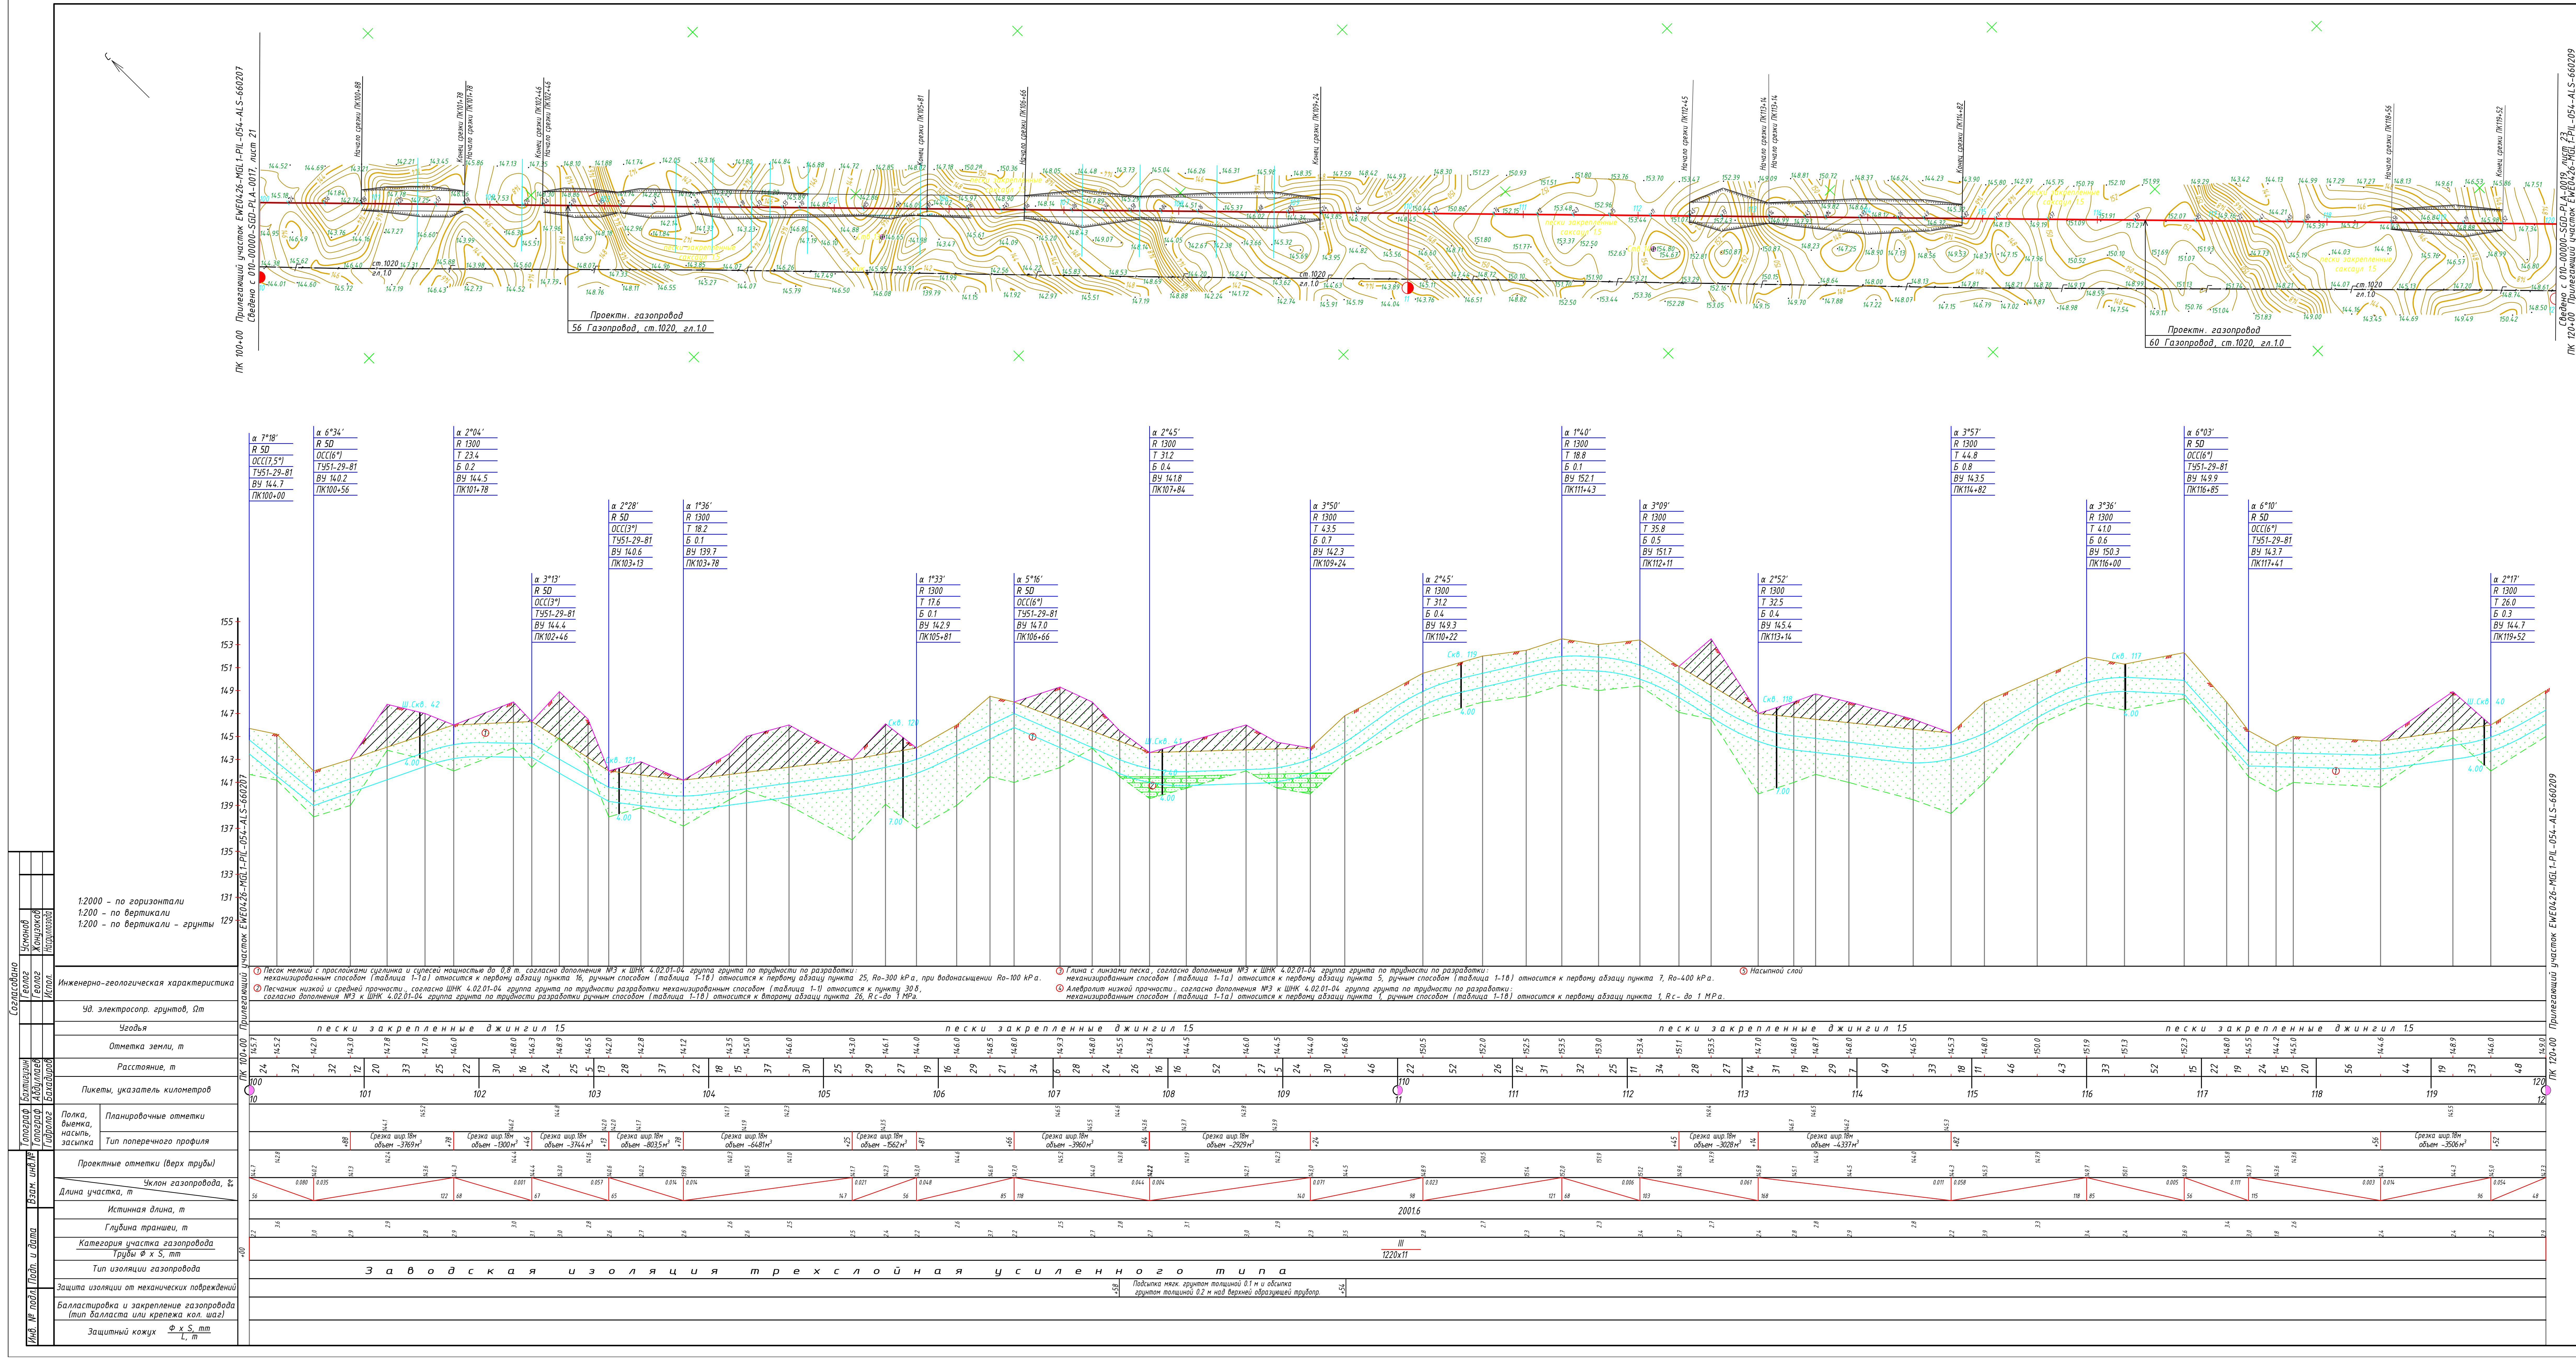
Инженерно-геологическая характеристика
Уд. электросопр. грунтов, Ωm
Угодья
Отметка земли, m
Расстояние, m
Пикеты, указатель километров
Полка, выемка, насыпь, засыпка
Планировочные отметки
Тип поперечного профиля
Проектные отметки (верх трубы)
Уклон газопровода, ‰
Длина участка, m
Истинная длина, m
Глубина траншеи, m
Категория участка газопровода
Трубы Φ x S, mm
Тип изоляции газопровода
Защита изоляции от механических повреждений
Балластировка и закрепление газопровода (тип балласта или крепежа кол. шаг)
Защитный кожух Φ x S, mm / L, m
пески закрепленные джингил 1.5
Заводская изоляция трехслойная усиленного типа
Проекты газопровод
56 Газопровод, ст.1020, гл.1.0
60 Газопровод, ст.1020, гл.1.0
ПК 100+00 Прилегающий участок EWE0426-MGL1-PIL-054-ALS-660207
ПК 120+00 Прилегающий участок EWE0426-MGL1-PIL-054-ALS-660209
Согласовано
Усмонов
Жонузоков
Насруллозода
Геолог
Геолог
Испол.
Бахтигузин
Абдуллаев
Бахадиров
Топограф
Топограф
Гидролог
Взам. инв.№
Подп. и дата
Инв. № подл.

1:2000 – по горизонтали
1:200 – по вертикали
1:200 – по вертикали – грунты

① Песок мелкий с прослойками суглинка и супесей мощностью до 0,8 m. согласно дополнения №3 к ШНК 4.02.01-04 группа грунта по трудности по разработки: механизированным способом (таблица 1-1а) относится к первому абзацу пункта 16, ручным способом (таблица 1-1в) относится к первому абзацу пункта 25, Ro-300 kPa, при водонасыщении Ro-100 kPa.

② Песчаник низкой и средней прочности., согласно ШНК 4.02.01-04 группа грунта по трудности разработки механизированным способом (таблица 1-1) относится к пункту 30 б, согласно дополнения №3 к ШНК 4.02.01-04 группа грунта по трудности разработки ручным способом (таблица 1-1в) относится к второму абзацу пункта 26, Rc-до 1 MPa.

③ Глина с линзами песка, согласно дополнения №3 к ШНК 4.02.01-04 группа грунта по трудности по разработки: механизированным способом (таблица 1-1а) относится к первому абзацу пункта 5, ручным способом (таблица 1-1в) относится к первому абзацу пункта 7, Ro-400 kPa.

④ Алевролит низкой прочности.. согласно дополнения №3 к ШНК 4.02.01-04 группа грунта по трудности по разработки: механизированным способом (таблица 1-1а) относится к первому абзацу пункта 1, ручным способом (таблица 1-1в) относится к первому абзацу пункта 1, Rc- до 1 MPa.

⑤ Насыпной слой

Схема расположения листов

010-00000-SGD-PLA-0017, лист 21	010-00000-SGD-PLA-0018, лист 22	010-00000-SGD-PLA-0019, лист 23

Экспликация деталей и отдельных изделий

№ п. п.	Наименование деталей	Ед изм.	Кол.	Примечание
1	ОСС 7.5°-5Д-1220(12К60)-5,5-075-У ТУ51-29-81	шт	1	
2	ОСС 6°-5Д-1220(12К60)-5,5-075-У ТУ51-29-81	шт	4	
3	ОСС 3°-5Д-1220(12К60)-5,5-075-У ТУ51-29-81	шт	2	

1. Общие данные - чертеж EWE0426-MGL1-PIL-054-COM-660201
2. Ситуационный план см. EWE0426-MGL1-PIL-054-DRW-660202
3. Производство работ на данном участке вести в строгом соответствии с "Инструкцией по производству строительных работ в охранных зонах магистральных трубопроводов Мингазпрома" ВСН 51-1-80.
4. Ширину полосы отвода земель для строительства газопровода см. типовой чертеж EWE0426-MGL1-PIL-DRW-810201.
5. Охранную зону магистрального газопровода см. типовой чертеж EWE0426-MGL1-PIL-DRW-810202.
6. Поперечный разрез траншеи см. типовой чертеж EWE0426-MGL1-PIL-DRW-810203.

Рев.	Дата	Назначение ревизии	Проверил	Утвердил
A2	17.08.2026	Выпущено для строительства		
A1	16.07.2026	Выпущено для строительства		
R2	26.06.2026	Выпущено для рассмотрения		
R1	03.06.2026	Выпущено для рассмотрения		

ЗАКАЗЧИК: UTG UZTRANSGAZ «TRANSGAZINJINIRING»
ГЕНЕРАЛЬНЫЙ ПОДРЯДЧИК: UET UZBEKENERGOTAMIR
ПОДРЯДЧИК: PBG Pro Build Generation
ГЕНЕРАЛЬНЫЙ ПРОЕКТИРОВЩИК: EAST WEST ENGINEERING

EWE0426-MGL1-PIL-054-ALS-660208-A2

«СТРОИТЕЛЬСТВО НОВЫХ НИТОК (УЧАСТКОВ) ГАЗОПРОВОДОВ «ГАЗЛИ – САРИМОЙ» И «АКЧАЛОК – ГАЗЛИ – НУКУС» ОБЩЕЙ ПРОТЯЖЕННОСТЬЮ НЕ МЕНЕЕ 275 КМ».

Изм.	Кол.уч.	Лист	№док.	Подпись	Дата
ГИП		Схабицкий А.			17.08.2026
Провер.		**Схабицкий А.**			17.08.2026
Исполн.		Шафиева О.			17.08.2026
Н.контр		Схабицкий А.			17.08.2026

ГАЗОПРОВОД «ГАЗЛИ-САРИМОЙ» (54 КМ)

Стадия	Лист	Листов
РД	1	1

План и продольный профиль газопровода
ПК 100+00- ПК 120+00

ООО "EAST-WEST Engineering"
г. Ташкент 2026г.

Формат A2x4