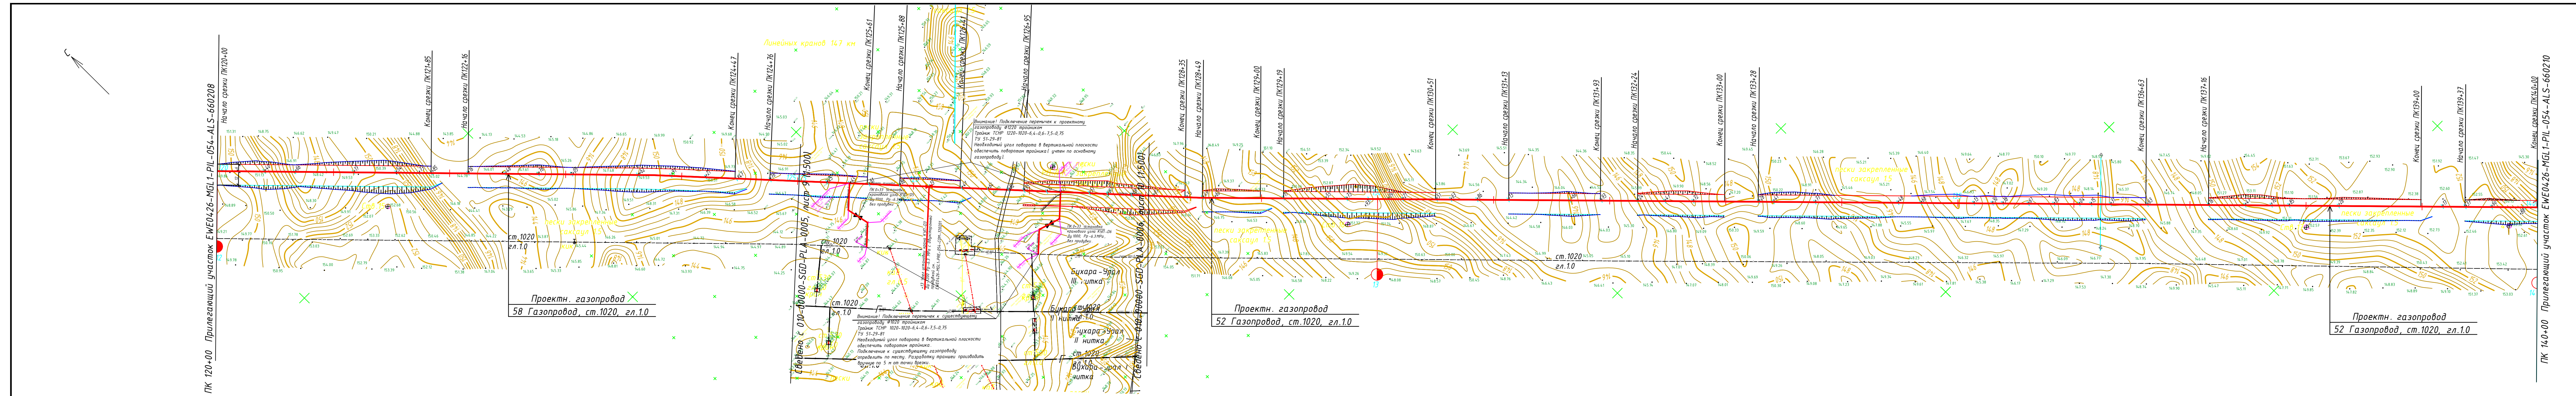
Проект. газопровод
58 Газопровод, ст.1020, ст.1,0
52 Газопровод, ст.1020, ст.1,0

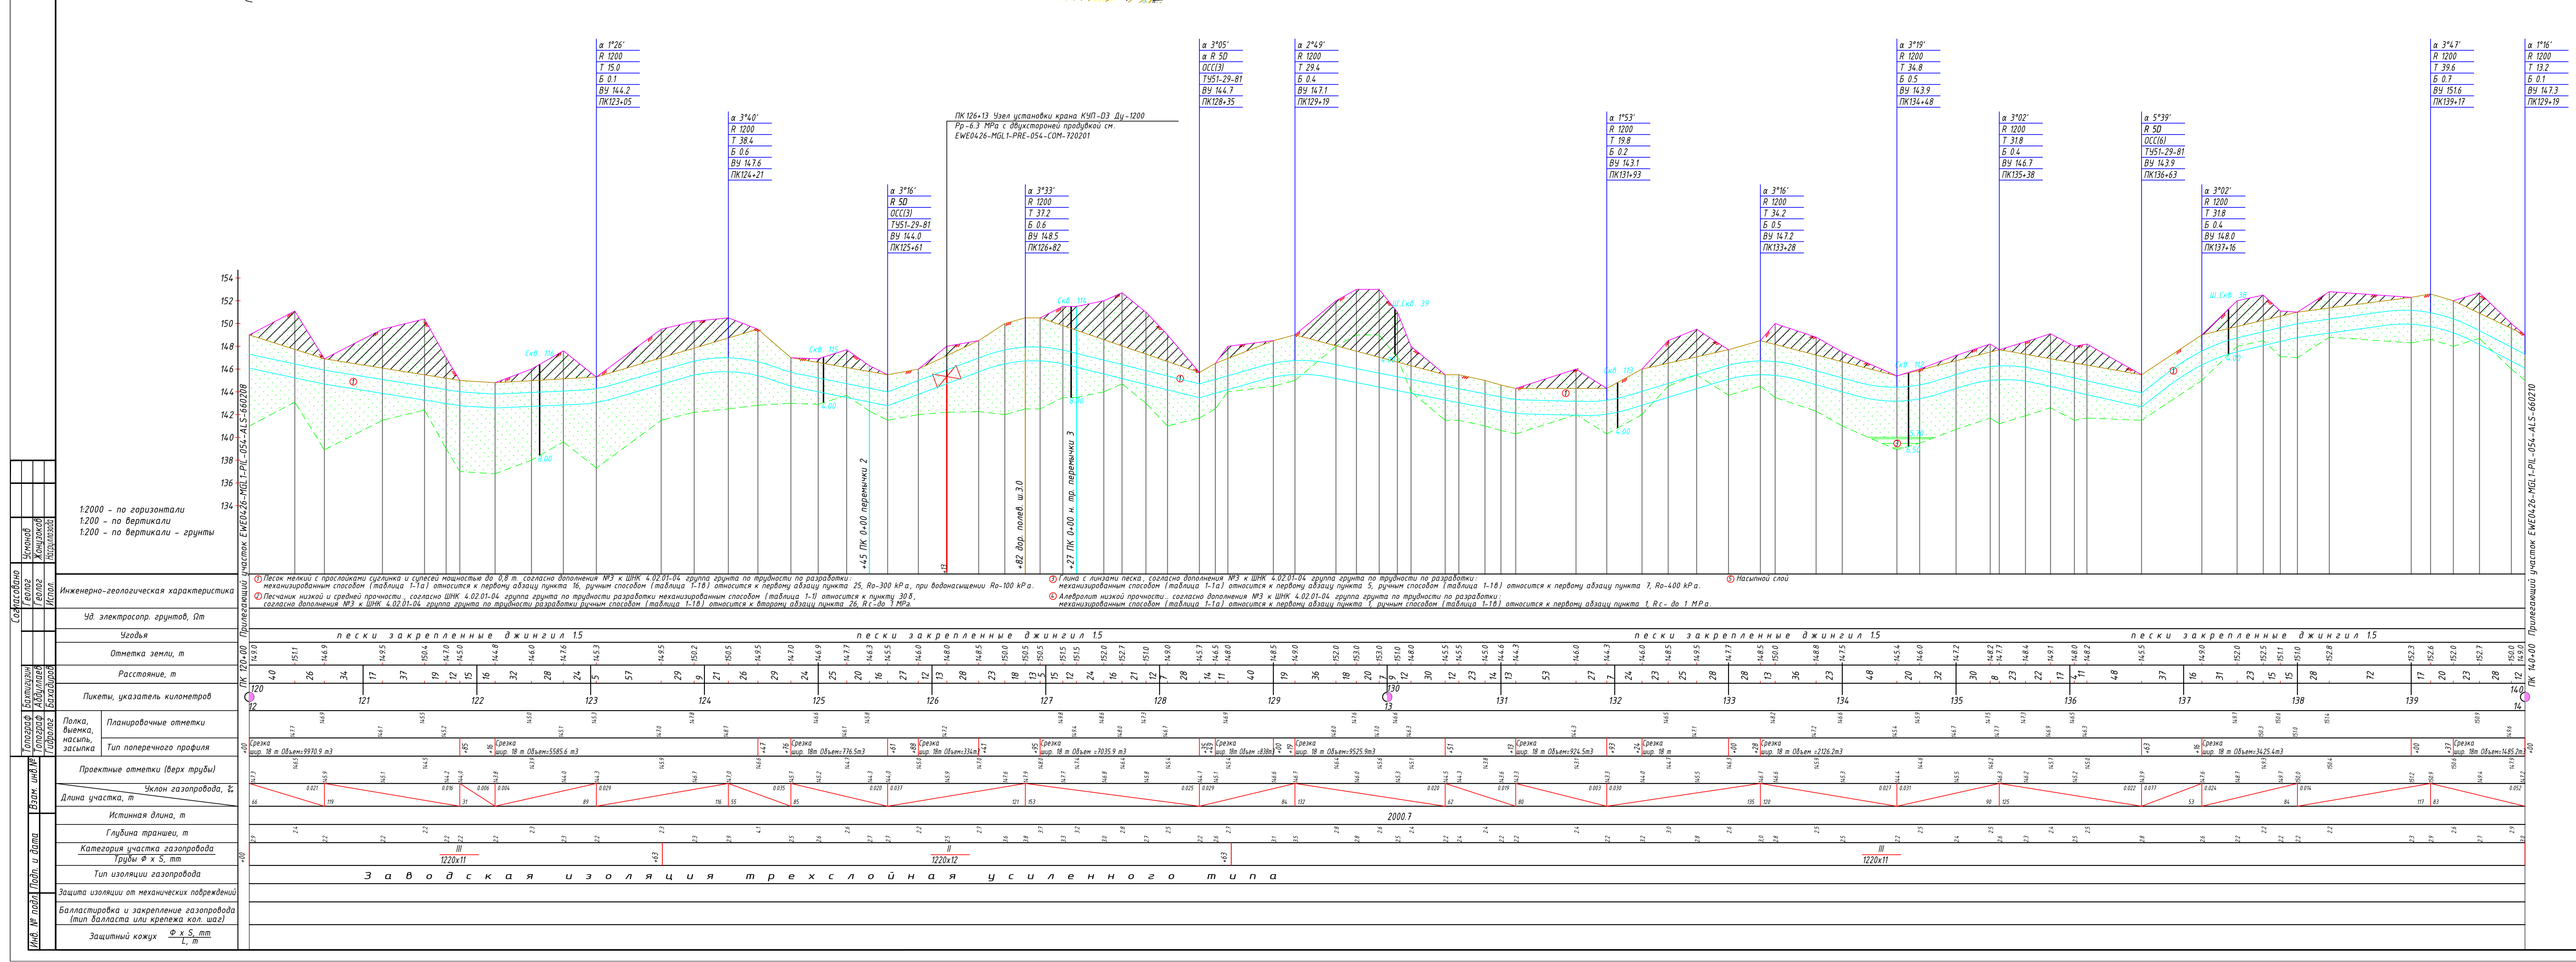
ПК 120+00 Прилегающий участок EWE0426-MGL1-PIL-054-ALS-660208
ПК 140+00 Прилегающий участок EWE0426-MGL1-PIL-054-ALS-660210
+45 ПК 0+00 перемычки 2
+82 дор. полев. ш.3.0
+27 ПК 0+00 н. тр. перемычки 3
Уд. электросопр. грунтов, Ωm
Угодья
пески закрепленные джингил 1.5
Отметка земли, m
Расстояние, m
Пикеты, указатель километров
Планировочные отметки
Тип поперечного профиля
Проектные отметки (верх трубы)
Уклон газопровода, ‰
Длина участка, m
Глубина траншеи, m
Категория участка газопровода
Тип изоляции газопровода
Заводская изоляция трехслойная усиленного типа
Защита изоляции от механических повреждений
Балластировка и закрепление газопровода (тип балласта или крепежа кол. шт)
Защитный кожух

1:2000 - по горизонтали
1:200 - по вертикали
1:200 - по вертикали - грунты

Инженерно-геологическая характеристика

① Песок мелкий с прослойками суглинка и супесей мощностью до 0,8 m. согласно дополнения №3 к ШНК 4.02.01-04 группа грунта по трудности по разработки: механизированным способом (таблица 1-1а) относится к первому абзацу пункта 16, ручным способом (таблица 1-1в) относится к первому абзацу пункта 25, Ro-300 kPa, при водонасыщении Ro-100 kPa.

② Песчаник низкой и средней прочности., согласно ШНК 4.02.01-04 группа грунта по трудности разработки механизированным способом (таблица 1-1) относится к пункту 30 б, согласно дополнения №3 к ШНК 4.02.01-04 группа грунта по трудности разработки ручным способом (таблица 1-1в) относится к второму абзацу пункта 26, Rc-до 1 MPa.

③ Глина с линзами песка, согласно дополнения №3 к ШНК 4.02.01-04 группа грунта по трудности по разработки: механизированным способом (таблица 1-1а) относится к первому абзацу пункта 5, ручным способом (таблица 1-1в) относится к первому абзацу пункта 7, Ro-400 kPa.

④ Алевролит низкой прочности.. согласно дополнения №3 к ШНК 4.02.01-04 группа грунта по трудности по разработки: механизированным способом (таблица 1-1а) относится к первому абзацу пункта 1, ручным способом (таблица 1-1в) относится к первому абзацу пункта 1, Rc- до 1 MPa.

⑤ Насыпной слой

Согласовано		
Геолог	Усмонов	
Геолог	Жонузоков	
Испол.	Насруллозода	
	Бахтигузин	
	Абдуллаев	
	Бахадиров	

Ведомость углов поворотов перемычки №2 в горизонтальной плоскости

№№ углов и створов	Величина левого угла	Длина линии, m	Элементы кривых: Радиус R, m	Угол α°	Тангенс T1, m	Тангенс T2, m	Кривая K, m	Биссектриса Б, m	
0+00									
		23							
ВУ 1	120°00'		5D	60°00'	(ОСС 30°x2)-5Д-1020(10K60)-5,5-0,75-У ТУ 51-29-81				
		20							
ВУ 2	240°00'		5D	60°00'	(ОСС 30°x2)-5Д-1020(10K60)-5,5-0,75-У ТУ 51-29-81				
		21							
0+64									
		L-64							

Ведомость углов поворотов перемычки №3 в горизонтальной плоскости

№№ углов и створов	Величина левого угла	Длина линии, m	Элементы кривых: Радиус R, m	Угол α°	Тангенс T1, m	Тангенс T2, m	Кривая K, m	Биссектриса Б, m	
0+00									
		23							
ВУ 1	240°00'		5D	60°00'	(ОСС 30°x2)-5Д-1020(10K60)-5,5-0,75-У ТУ 51-29-81				
		20							
ВУ 2	120°00'		5D	60°00'	(ОСС 30°x2)-5Д-1020(10K60)-5,5-0,75-У ТУ 51-29-81				
		21							
0+64									
		L-64							

Внимание! Подключение перемычки к проектному газопроводу Ø1220 тройником
Тройник ТСНР 1220-1020-6,4-0,6-7,5-0,75
ТУ 51-29-81
Необходимый угол поворота в вертикальной плоскости обеспечить поворотом тройника (учтен по основному газопроводу).

Внимание! Подключение к существующему газопроводу Ø1020 тройником
Тройник ТСНР 1020-1020-6,4-0,6-7,5-0,75
ТУ 51-29-81
Необходимый угол поворота в вертикальной плоскости обеспечить поворотом тройника.
Подключение к существующему газопроводу определить по месту. Разработку траншеи производить вручную по 5 м от точки врезки.

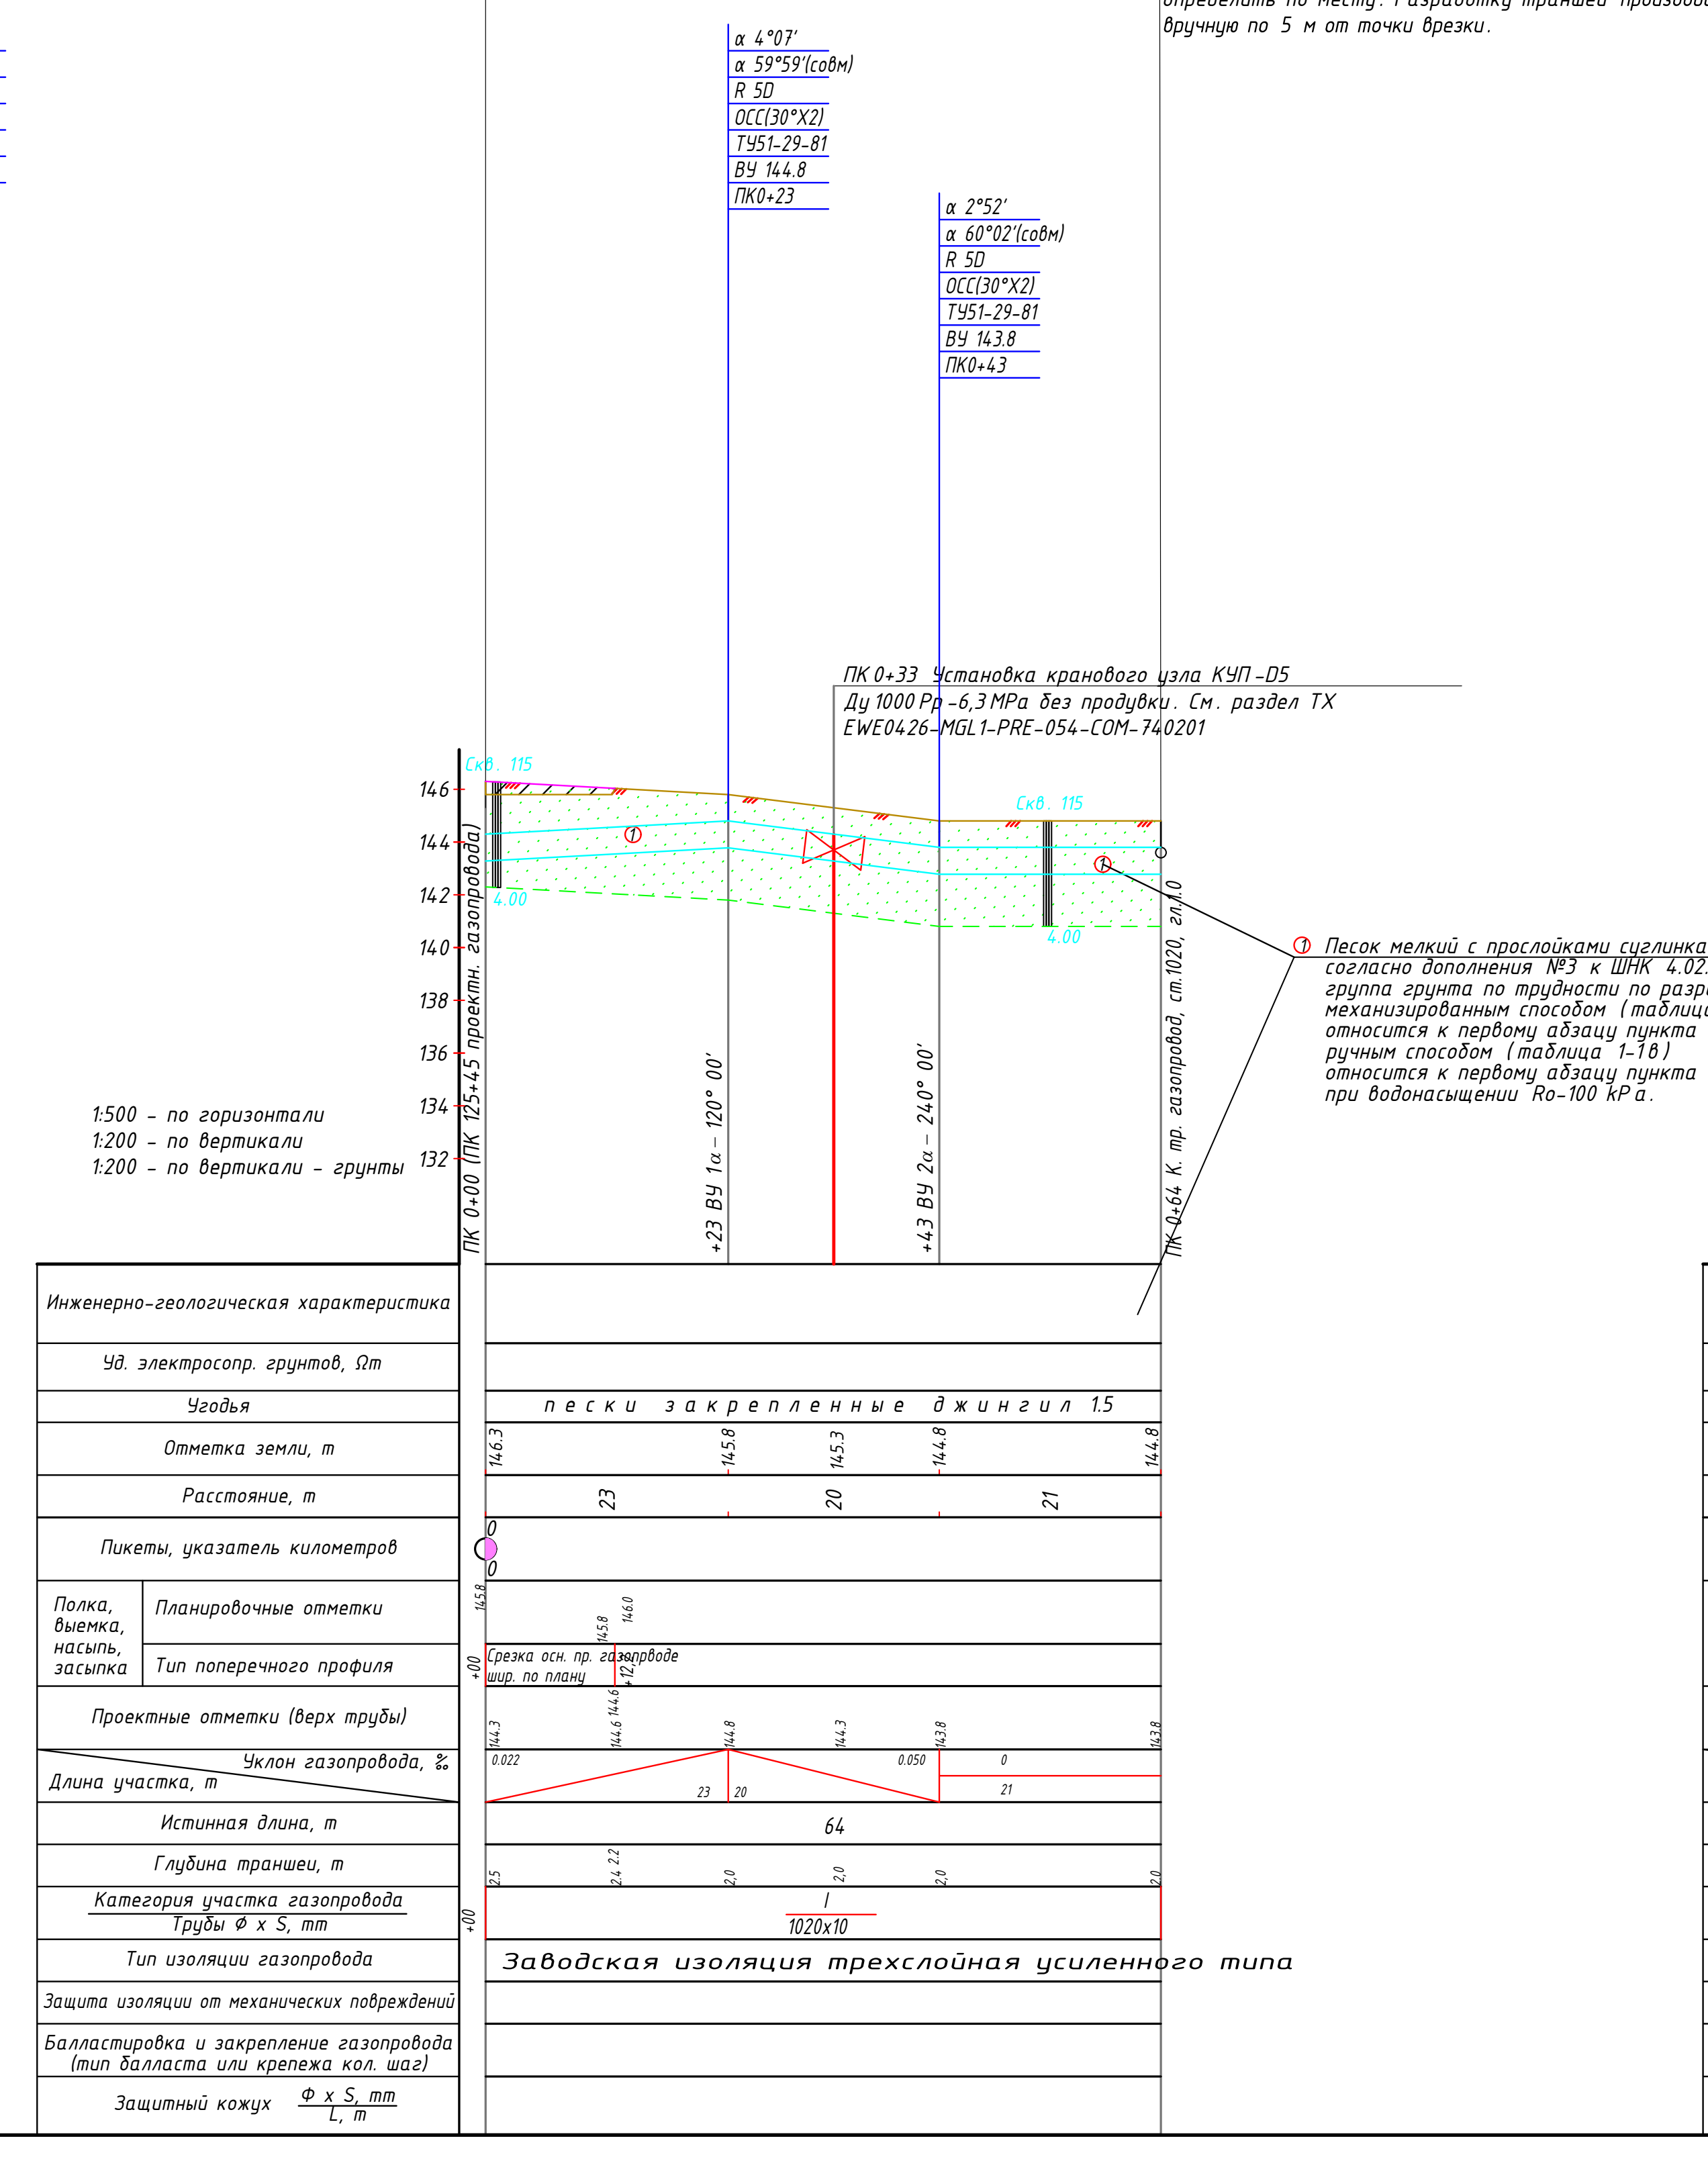

Внимание! Подключение перемычки к проектному газопроводу Ø1220 тройником
Тройник ТСНР 1220-1020-6,4-0,6-7,5-0,75
ТУ 51-29-81
Необходимый угол поворота в вертикальной плоскости обеспечить поворотом тройника (учтен по основному газопроводу).

Внимание! Подключение к существующему газопроводу Ø1020 тройником
ТСНР 1020-1020-6,4-0,6-7,5-0,75
ТУ 51-29-81
Необходимый угол поворота в вертикальной плоскости обеспечить поворотом тройника.
Подключение к существующему газопроводу определить по месту. Разработку траншеи производить вручную по 5 м от точки врезки.

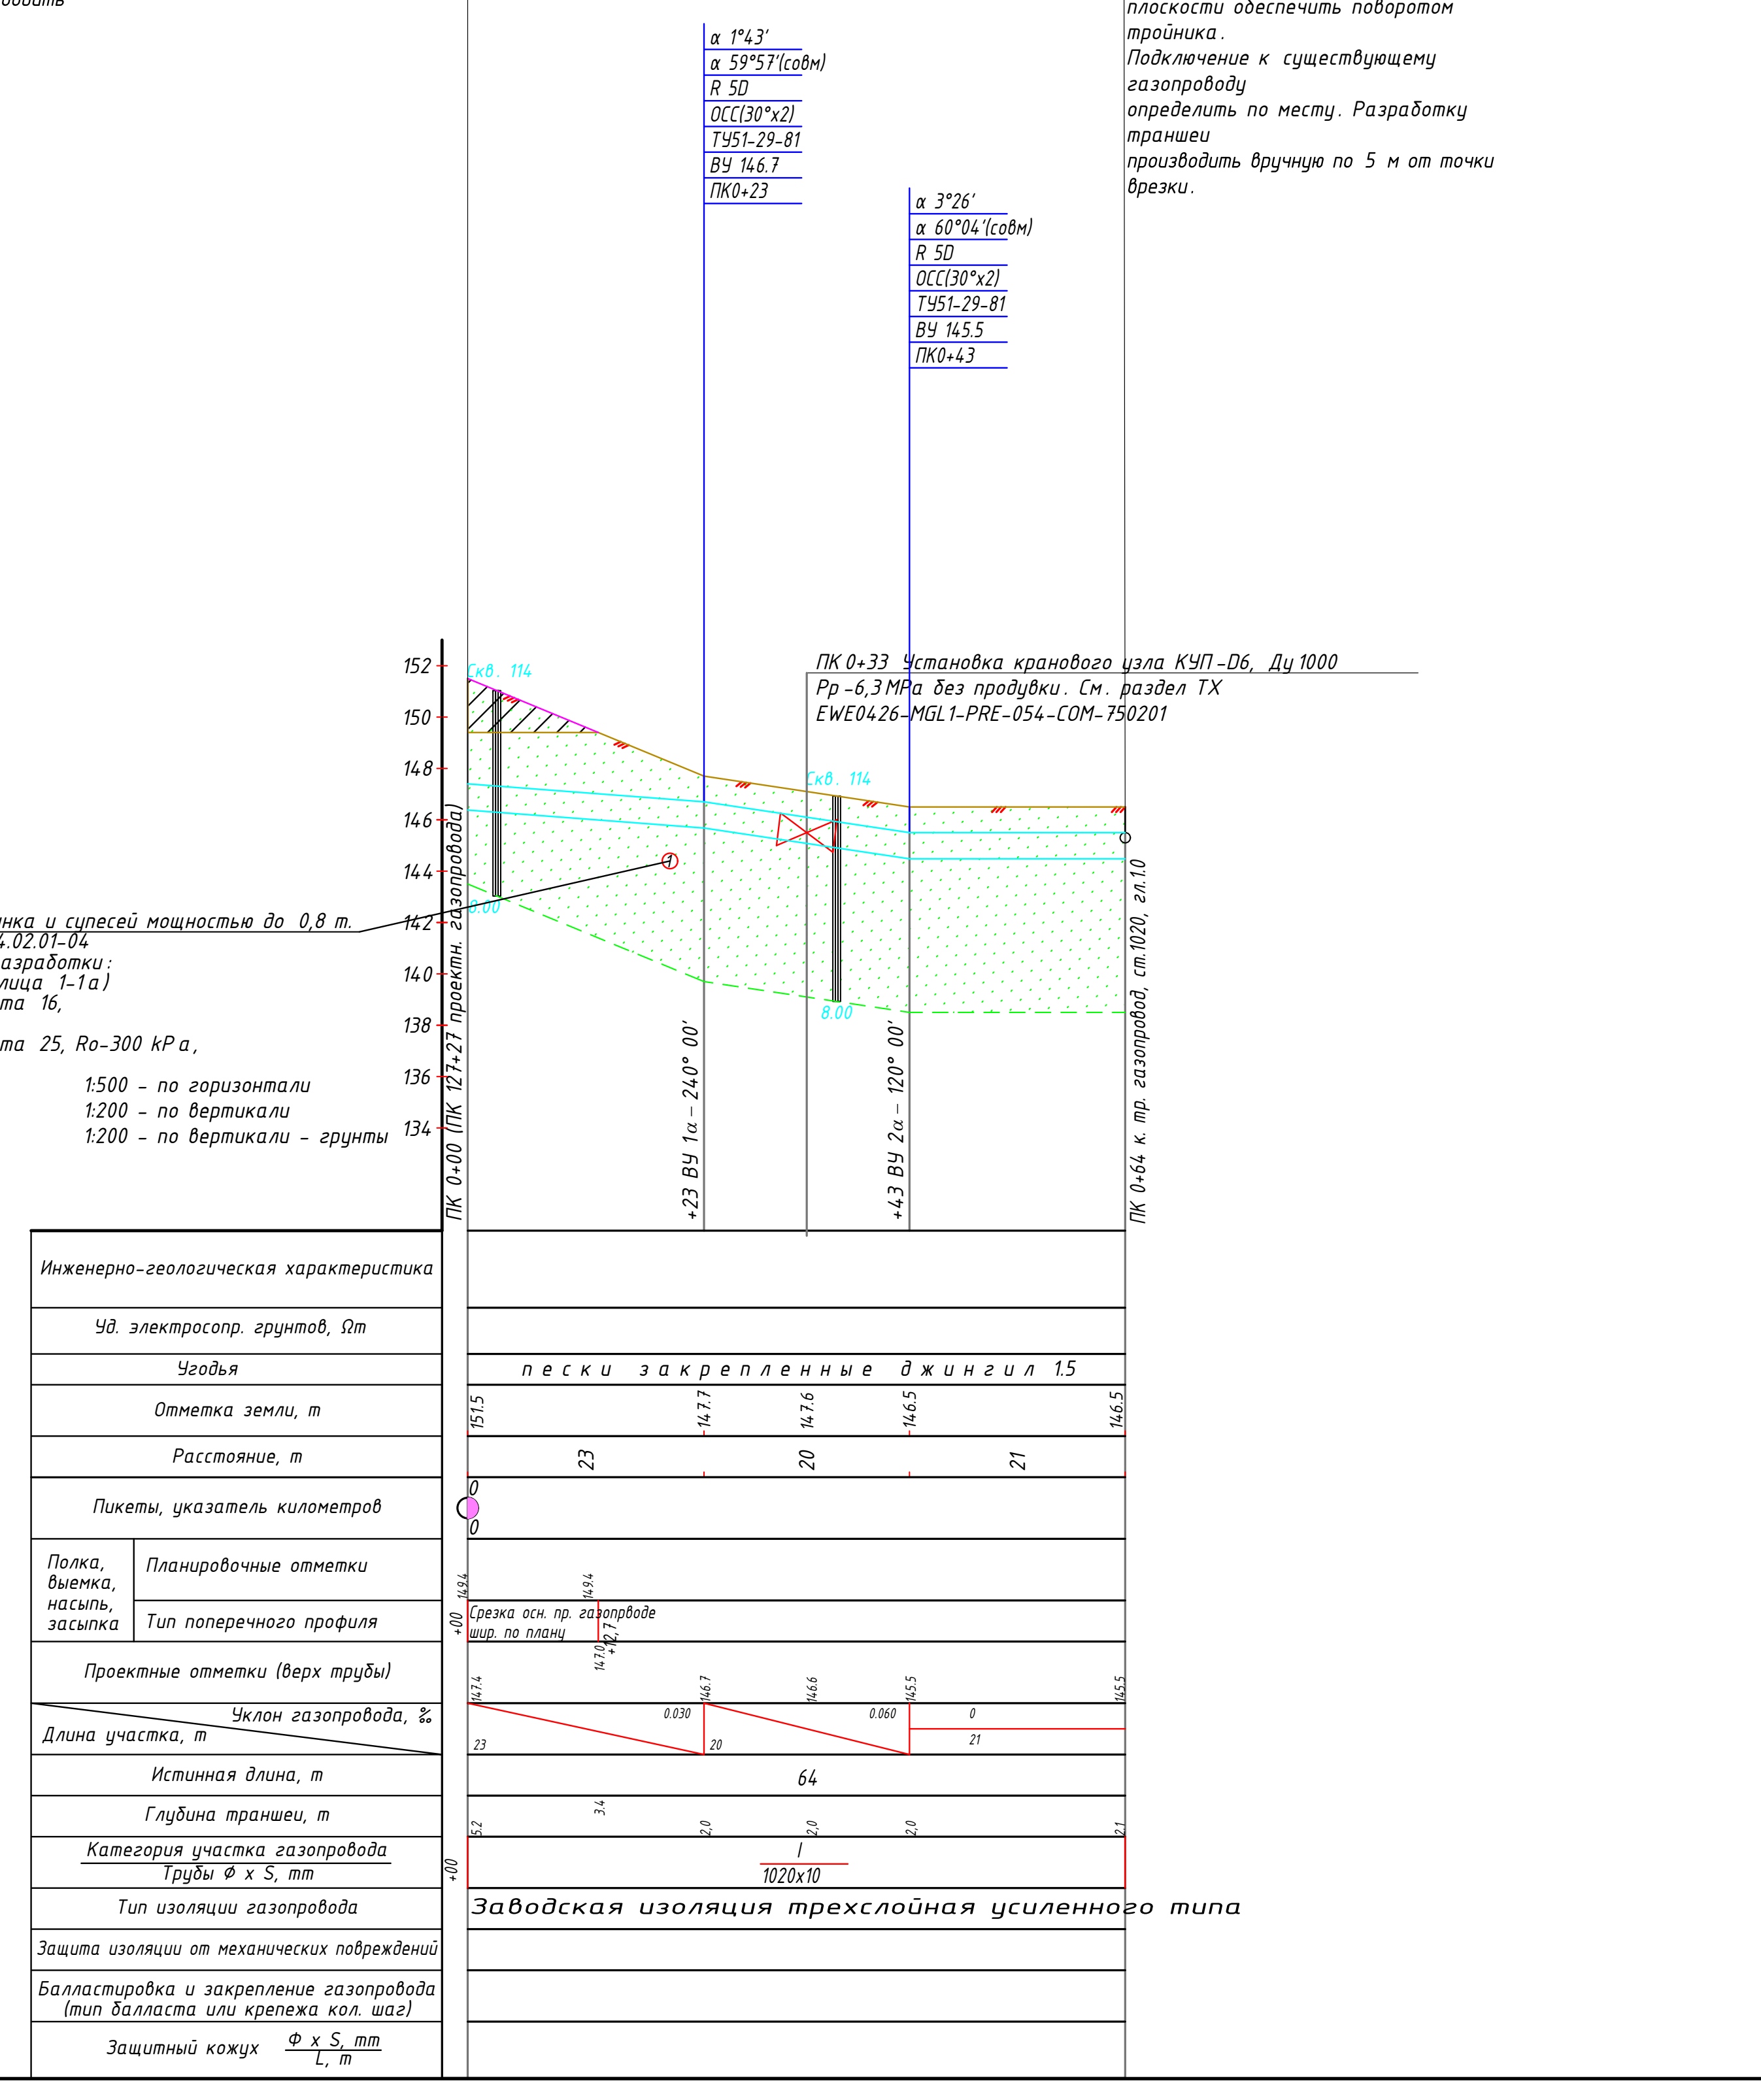

Экспликация деталей и отдельных изделий

№ п. п.	Наименование деталей	Ед изм.	Кол.	Примечание
1	ОСС 30°-5Д-1020(10K60)-5,5-0,75-У ТУ 51-29-81	шт	8	
2	ОСС 6°-5Д-1220(12K60)-5,5-0,75-У ТУ 51-29-81	шт	1	
3	ОСС 3°-5Д-1220(12K60)-5,5-0,75-У ТУ 51-29-81	шт	2	
4	ТСНР 1220x1020-6,4-0,6-7,5-0,75-K60 ТУ 51-29-81	шт	2	
5	ТСНР 1020x1020-6,4-0,6-7,5-0,75-K60 ТУ 51-29-81	шт	2	

1 Общие данные - чертеж EWE0426-MGL1-PIL-054-COM-660201
2 Ситуационный план см. EWE0426-MGL1-PIL-054-DRW-660202
3 До начала работ руководитель строительной организации должен разработать и согласовать схему и инструкцию по безопасному производству работ в охранной зоне газопровода и его сооружений.
4 Производство работ на данном участке вести в строгом соответствии с "Инструкцией по производству строительных работ в охранных зонах магистральных трубопроводов Мингазпрома" ВСН 51-1-80.
5 Ширину полосы отвода земель для строительства газопровода см. типовой чертеж EWE0426-MGL1-PIL-000-DRW-810201.
6 Охранную зону магистрального газопровода см. типовой чертеж EWE0426-MGL1-PIL-000-DRW-810202.
7 Поперечный разрез траншеи см. типовой чертеж EWE0426-MGL1-PIL-000-DRW-810203.
Перед рытьем траншеи на данном участке должна предусматриваться предварительная планировка строительной полосы (срезку грунта в зоне выполнить по проекту).
9 Стыки врезки в существующий газопровод-гарантийные, которые должны быть в строгом соответствии с "Правилами безопасности при эксплуатации магистральных газопроводов" 2003 г.
10 Врезку в существующие газопроводы производить в соответствии с требованиями, изложенными в "Типовой инструкции на производство огневых работ на действующих магистральных газопроводах, газосборных сетях, газовых промыслов", утвержденных Мингазпромом 9 июня 1971 г., ВСН 006-89.
11 Размещение механизированных колонн, баз, стоянок машин и механизмов, складов ГСМ и другого оборудования осуществлять только за пределами опасной зоны газопровода.
12 Земляные работы в зоне по 5 м в обе стороны от врезки в существующий газопровод выполнить без применения ударных инструментов вручную в присутствии представителя организации, эксплуатирующей этот газопровод.
13 Производство работ при пересечении с существующим газопроводами вести в строгом соответствии с "Инструкцией по производству строительных работ в охранных зонах магистральных трубопроводов Мингазпрома" ВСН 51-1-80.
14 Проезд техники через существующий газопровод выполнить по специально устроенным переездам (ВТУ МГ-1).
15 Производство работ, сварку, контроль монтажных сварных соединений и испытание газопровода производить в соответствии с ШНК 2.05.06-22, QR 02.01, QR 06.08, ВСН 51-3-85, ВСН 005-88, ВСН 006-89, ВСН 011-88, ВСН 012-88, "Правилами техники безопасности при строительстве магистральных стальных трубопроводов".
16 На период эксплуатации по трассе газопровода установить следующие сигнальные знаки:
- на углах поворота в плане трассы опознавательный столб (85.00-08.00-000:00.08-MP);
- сигнальный знак, совмещенный с катодными выводами через 1 km (см. раздел ЭХЗ).
17 Номера существующих ниток изменены и диаметр существующих газопроводов в месте подключения принят 1220 по уточнению Заказчика в схеме PFD л. EWE0426-MGL1-PRE-054-PFD-610101-R2 и откорректированного изыскательского материала (письмо MGL-EM-PBG-EWE-0016).

Схема расположения листов

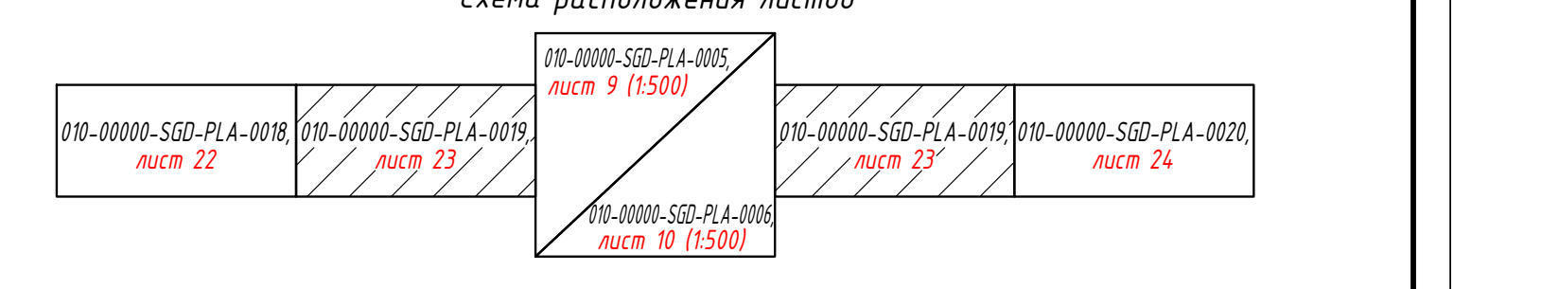

Рев.	Дата	Назначение ревизии	Проверил	Утвердил
A2	17.08.2026	Выпущено для строительства		
A1	16.07.2026	Выпущено для строительства		
R2	02.07.2026	Выпущено для рассмотрения		
R1	03.06.2026	Выпущено для рассмотрения		

ЗАКАЗЧИК: UZTRANSGAZ
ГЕНЕРАЛЬНЫЙ ПОДРЯДЧИК: UZBEKENERGOTAMIR
ПОДРЯДЧИК: PBG Pro Build Generation
ГЕНЕРАЛЬНЫЙ ПРОЕКТИРОВЩИК: EAST WEST ENGINEERING

EWE0426-MGL1-PIL-054-ALS-660209-A2

«СТРОИТЕЛЬСТВО НОВЫХ НИТОК (УЧАСТКОВ) ГАЗОПРОВОДОВ «ГАЗЛИ - САРИМОЙ» И «АКЧАЛОК - ГАЗЛИ - НУКУС» ОБЩЕЙ ПРОТЯЖЕННОСТЬЮ НЕ МЕНЕЕ 275 КМ».

Изм.	Кол.уч.	Лист	№док.	Подпись	Дата
ГИП		Схабицкий А.			17.08.2026
Провер.		Шафиева О.			17.08.2026
Исполн.		Енгалычев А.			17.08.2026
Н.контр		Схабицкий А.			17.08.2026

ГАЗОПРОВОД «ГАЗЛИ-САРИМОЙ» (54 КМ)

Стадия	Лист	Листов
РД	1	1

План и продольный профиль газопровода ПК 120- ПК 140, перемычки №2 ПК 0+00- ПК 0+64 и перемычки №3 ПК 0+00- ПК 0+64

ООО "EAST-WEST Engineering"
г. Ташкент 2026г.

Формат А2х5