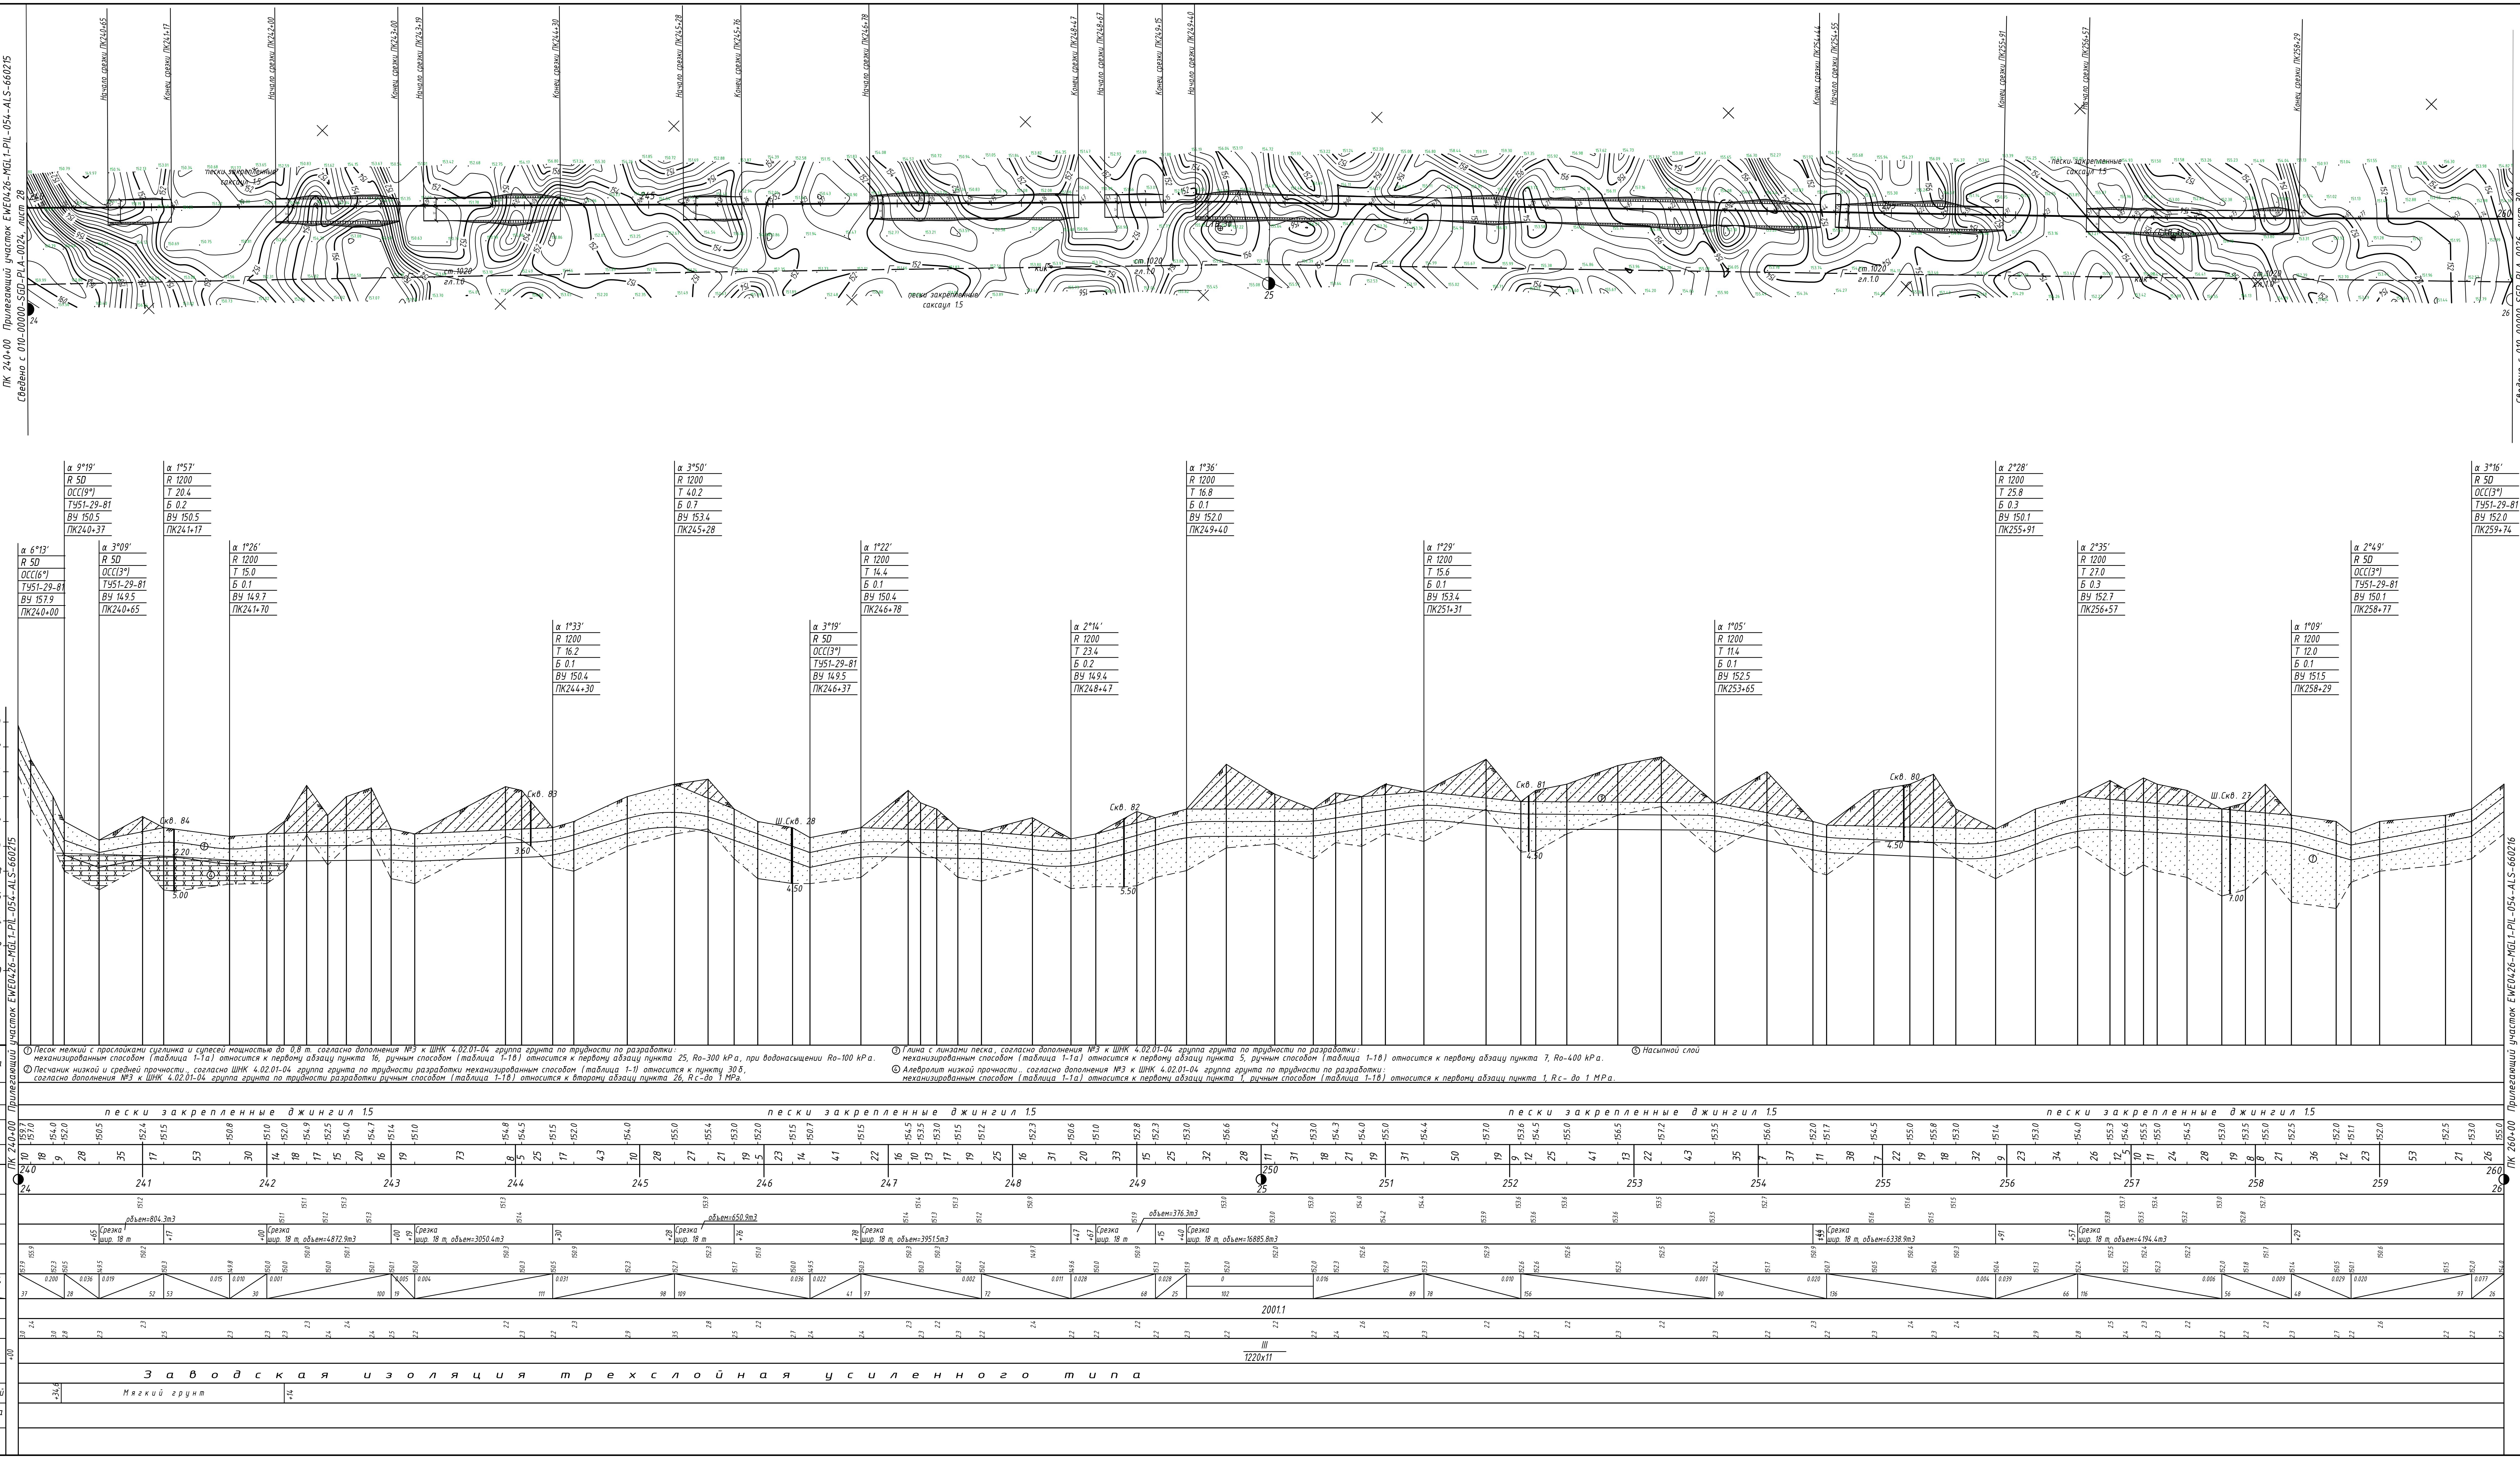
ПК 240+00 Прилегающий участок EWE0426-MGL1-PIL-054-ALS-660215
Сведено с 010-00000-SGD-PLA-0024, лист 28
ПК 260+00 Прилегающий участок EWE0426-MGL1-PIL-054-ALS-660216
Сведено с 010-00000-SGD-PLA-0026, лист 30
α 6°13' R 5D ОСС(6°) ТУ51-29-81 ВУ 157.9 ПК240+00
α 9°19' R 5D ОСС(9°) ТУ51-29-81 ВУ 150.5 ПК240+37
α 3°09' R 5D ОСС(3°) ТУ51-29-81 ВУ 149.5 ПК240+65
α 1°57' R 1200 Т 20.4 Б 0.2 ВУ 150.5 ПК241+17
α 1°26' R 1200 Т 15.0 Б 0.1 ВУ 149.7 ПК241+70
α 1°33' R 1200 Т 16.2 Б 0.1 ВУ 150.4 ПК244+30
α 3°50' R 1200 Т 40.2 Б 0.7 ВУ 153.4 ПК245+28
α 3°19' R 5D ОСС(3°) ТУ51-29-81 ВУ 149.5 ПК246+37
α 1°22' R 1200 Т 14.4 Б 0.1 ВУ 150.4 ПК246+78
α 2°14' R 1200 Т 23.4 Б 0.2 ВУ 149.4 ПК248+47
α 1°36' R 1200 Т 16.8 Б 0.1 ВУ 152.0 ПК249+40
α 1°29' R 1200 Т 15.6 Б 0.1 ВУ 153.4 ПК251+31
α 1°05' R 1200 Т 11.4 Б 0.1 ВУ 152.5 ПК253+65
α 2°28' R 1200 Т 25.8 Б 0.3 ВУ 150.1 ПК255+91
α 2°35' R 1200 Т 27.0 Б 0.3 ВУ 152.7 ПК256+57
α 1°09' R 1200 Т 12.0 Б 0.1 ВУ 151.5 ПК258+29
α 2°49' R 5D ОСС(3°) ТУ51-29-81 ВУ 150.1 ПК258+77
α 3°16' R 5D ОСС(3°) ТУ51-29-81 ВУ 152.0 ПК259+74
Скв. 84
Скв. 83
Ш.Скв. 28
Скв. 82
Скв. 81
Скв. 80
Ш.Скв. 27
160
158
156
154
152
150
148
146
144
142
140
Инженерно-геологическая характеристика
Уд. электросопр. грунтов, Ωm
Угодья
пески закрепленные джингил 1.5
Отметка земли, m
Расстояние, m
Пикеты, указатель километров
240
241
242
243
244
245
246
247
248
249
250
251
252
253
254
255
256
257
258
259
260
24
25
26
Полка, выемка, насыпь, засыпка
Планировочные отметки
Тип поперечного профиля
Проектные отметки (верх трубы)
Уклон газопровода, ‰
Длина участка, m
Истинная длина, m
2001.1
Глубина траншеи, m
Категория участка газопровода
Трубы Φ x S, mm
III
1220x11
Тип изоляции газопровода
Заводская изоляция трехслойная усиленного типа
Защита изоляции от механических повреждений
Мягкий грунт
Балластировка и закрепление газопровода (тип балласта или крепежа кол. шаг)
Защитный кожух Φ x S, mm / L, m

1:2000 – по горизонтали
1:200 – по вертикали
1:200 – по вертикали – грунты

① Песок мелкий с прослойками суглинка и супесей мощностью до 0,8 m. согласно дополнения №3 к ШНК 4.02.01-04 группа грунта по трудности по разработки: механизированным способом (таблица 1-1а) относится к первому абзацу пункта 16, ручным способом (таблица 1-1в) относится к первому абзацу пункта 25, Ro-300 kPa, при водонасыщении Ro-100 kPa.

② Песчаник низкой и средней прочности., согласно ШНК 4.02.01-04 группа грунта по трудности разработки механизированным способом (таблица 1-1) относится к пункту 30 б, согласно дополнения №3 к ШНК 4.02.01-04 группа грунта по трудности разработки ручным способом (таблица 1-1в) относится к второму абзацу пункта 26, Rc-до 1 MPa.

③ Глина с линзами песка, согласно дополнения №3 к ШНК 4.02.01-04 группа грунта по трудности по разработки: механизированным способом (таблица 1-1а) относится к первому абзацу пункта 5, ручным способом (таблица 1-1в) относится к первому абзацу пункта 7, Ro-400 kPa.

④ Алевролит низкой прочности.. согласно дополнения №3 к ШНК 4.02.01-04 группа грунта по трудности по разработки: механизированным способом (таблица 1-1а) относится к первому абзацу пункта 1, ручным способом (таблица 1-1в) относится к первому абзацу пункта 1, Rc- до 1 MPa.

⑤ Насыпной слой

Согласовано

Усмонов	Жонузоков	Насруллозода
Геолог	Геолог	Испол.
Бахтигузин	Абдуллаев	Бахадиров
Топограф	Топограф	Гидролог

Взам. инв.№

Подп. и дата

Инв. № подл.

Экспликация деталей и отдельных изделий

№ п. п.	Наименование деталей	Ед изм.	Кол.	Примечание
1	ОСС 9°-5Д-1220(12К60)-5,5-0,75-У ТУ 51-29-81	шт	1	
2	ОСС 3°-5Д-1220(12К60)-5,5-0,75-У ТУ 51-29-81	шт	4	

1 Общие данные – чертеж EWE0426-MGL1-PIL-054-COM-660201
2 Ситуационный план см. EWE0426-MGL1-PIL-054-DRW-660202
3 До начала работ руководитель строительной организации должен разработать и согласовать схему и инструкцию по безопасному производству работ в охранной зоне газопровода и его сооружений.
4 Производство работ на данном участке вести в строгом соответствии с "Инструкцией по производству строительных работ в охранных зонах магистральных трубопроводов Мингазпрома" ВСН 51-1-80.
5 Ширину полосы отвода земель для строительства газопровода см. типовой чертеж EWE0426-MGL1-PIL-DRW-810201.
6 Охранную зону магистрального газопровода см. типовой чертеж EWE0426-MGL1-PIL-DRW-810202.
7 Поперечный разрез траншеи см. типовой чертеж EWE0426-MGL1-PIL-DRW-810203.

Схема расположения листов

010-00000-SGD-PLA-0024, лист 28	▨ 010-00000-SGD-PLA-0025, лист 29	010-00000-SGD-PLA-0026, лист 30

Рев.	Дата	Назначение ревизии	Проверил	Утвердил
A2	17.08.2026	Выпущено для строительства		
A1	16.07.2026	Выпущено для строительства		
R2	02.07.2026	Выпущено для рассмотрения		
R1	03.06.2026	Выпущено для рассмотрения		

ЗАКАЗЧИК: UTG UZTRANSGAZ «TRANSGAZINJINIRING»
ГЕНЕРАЛЬНЫЙ ПОДРЯДЧИК: UET UZBEKENERGOTAMIR
ПОДРЯДЧИК: PBG Pro Build Generation
ГЕНЕРАЛЬНЫЙ ПРОЕКТИРОВЩИК: EAST WEST ENGINEERING

EWE0426-MGL1-PIL-054-ALS-660215-A2

«СТРОИТЕЛЬСТВО НОВЫХ НИТОК (УЧАСТКОВ) ГАЗОПРОВОДОВ «ГАЗЛИ – САРИМОЙ» И «АКЧАЛОК – ГАЗЛИ – НУКУС» ОБЩЕЙ ПРОТЯЖЕННОСТЬЮ НЕ МЕНЕЕ 275 КМ».

Изм.	Кол.уч.	Лист	№док.	Подпись	Дата
ГИП		Схабицкий А.			17.08.2026
Провер.		Шафиева О.			17.08.2026
Исполн.		Енгалычев А.			17.08.2026
Н.контр		Схабицкий А.			17.08.2026

ГАЗОПРОВОД «ГАЗЛИ-САРИМОЙ» (54 КМ)

Стадия	Лист	Листов
РД	1	1

План и продольный профиль газопровода
ПК 240+00- ПК 260+00

ООО "EAST-WEST Engineering"
г. Ташкент 2026г.

Формат A2x4