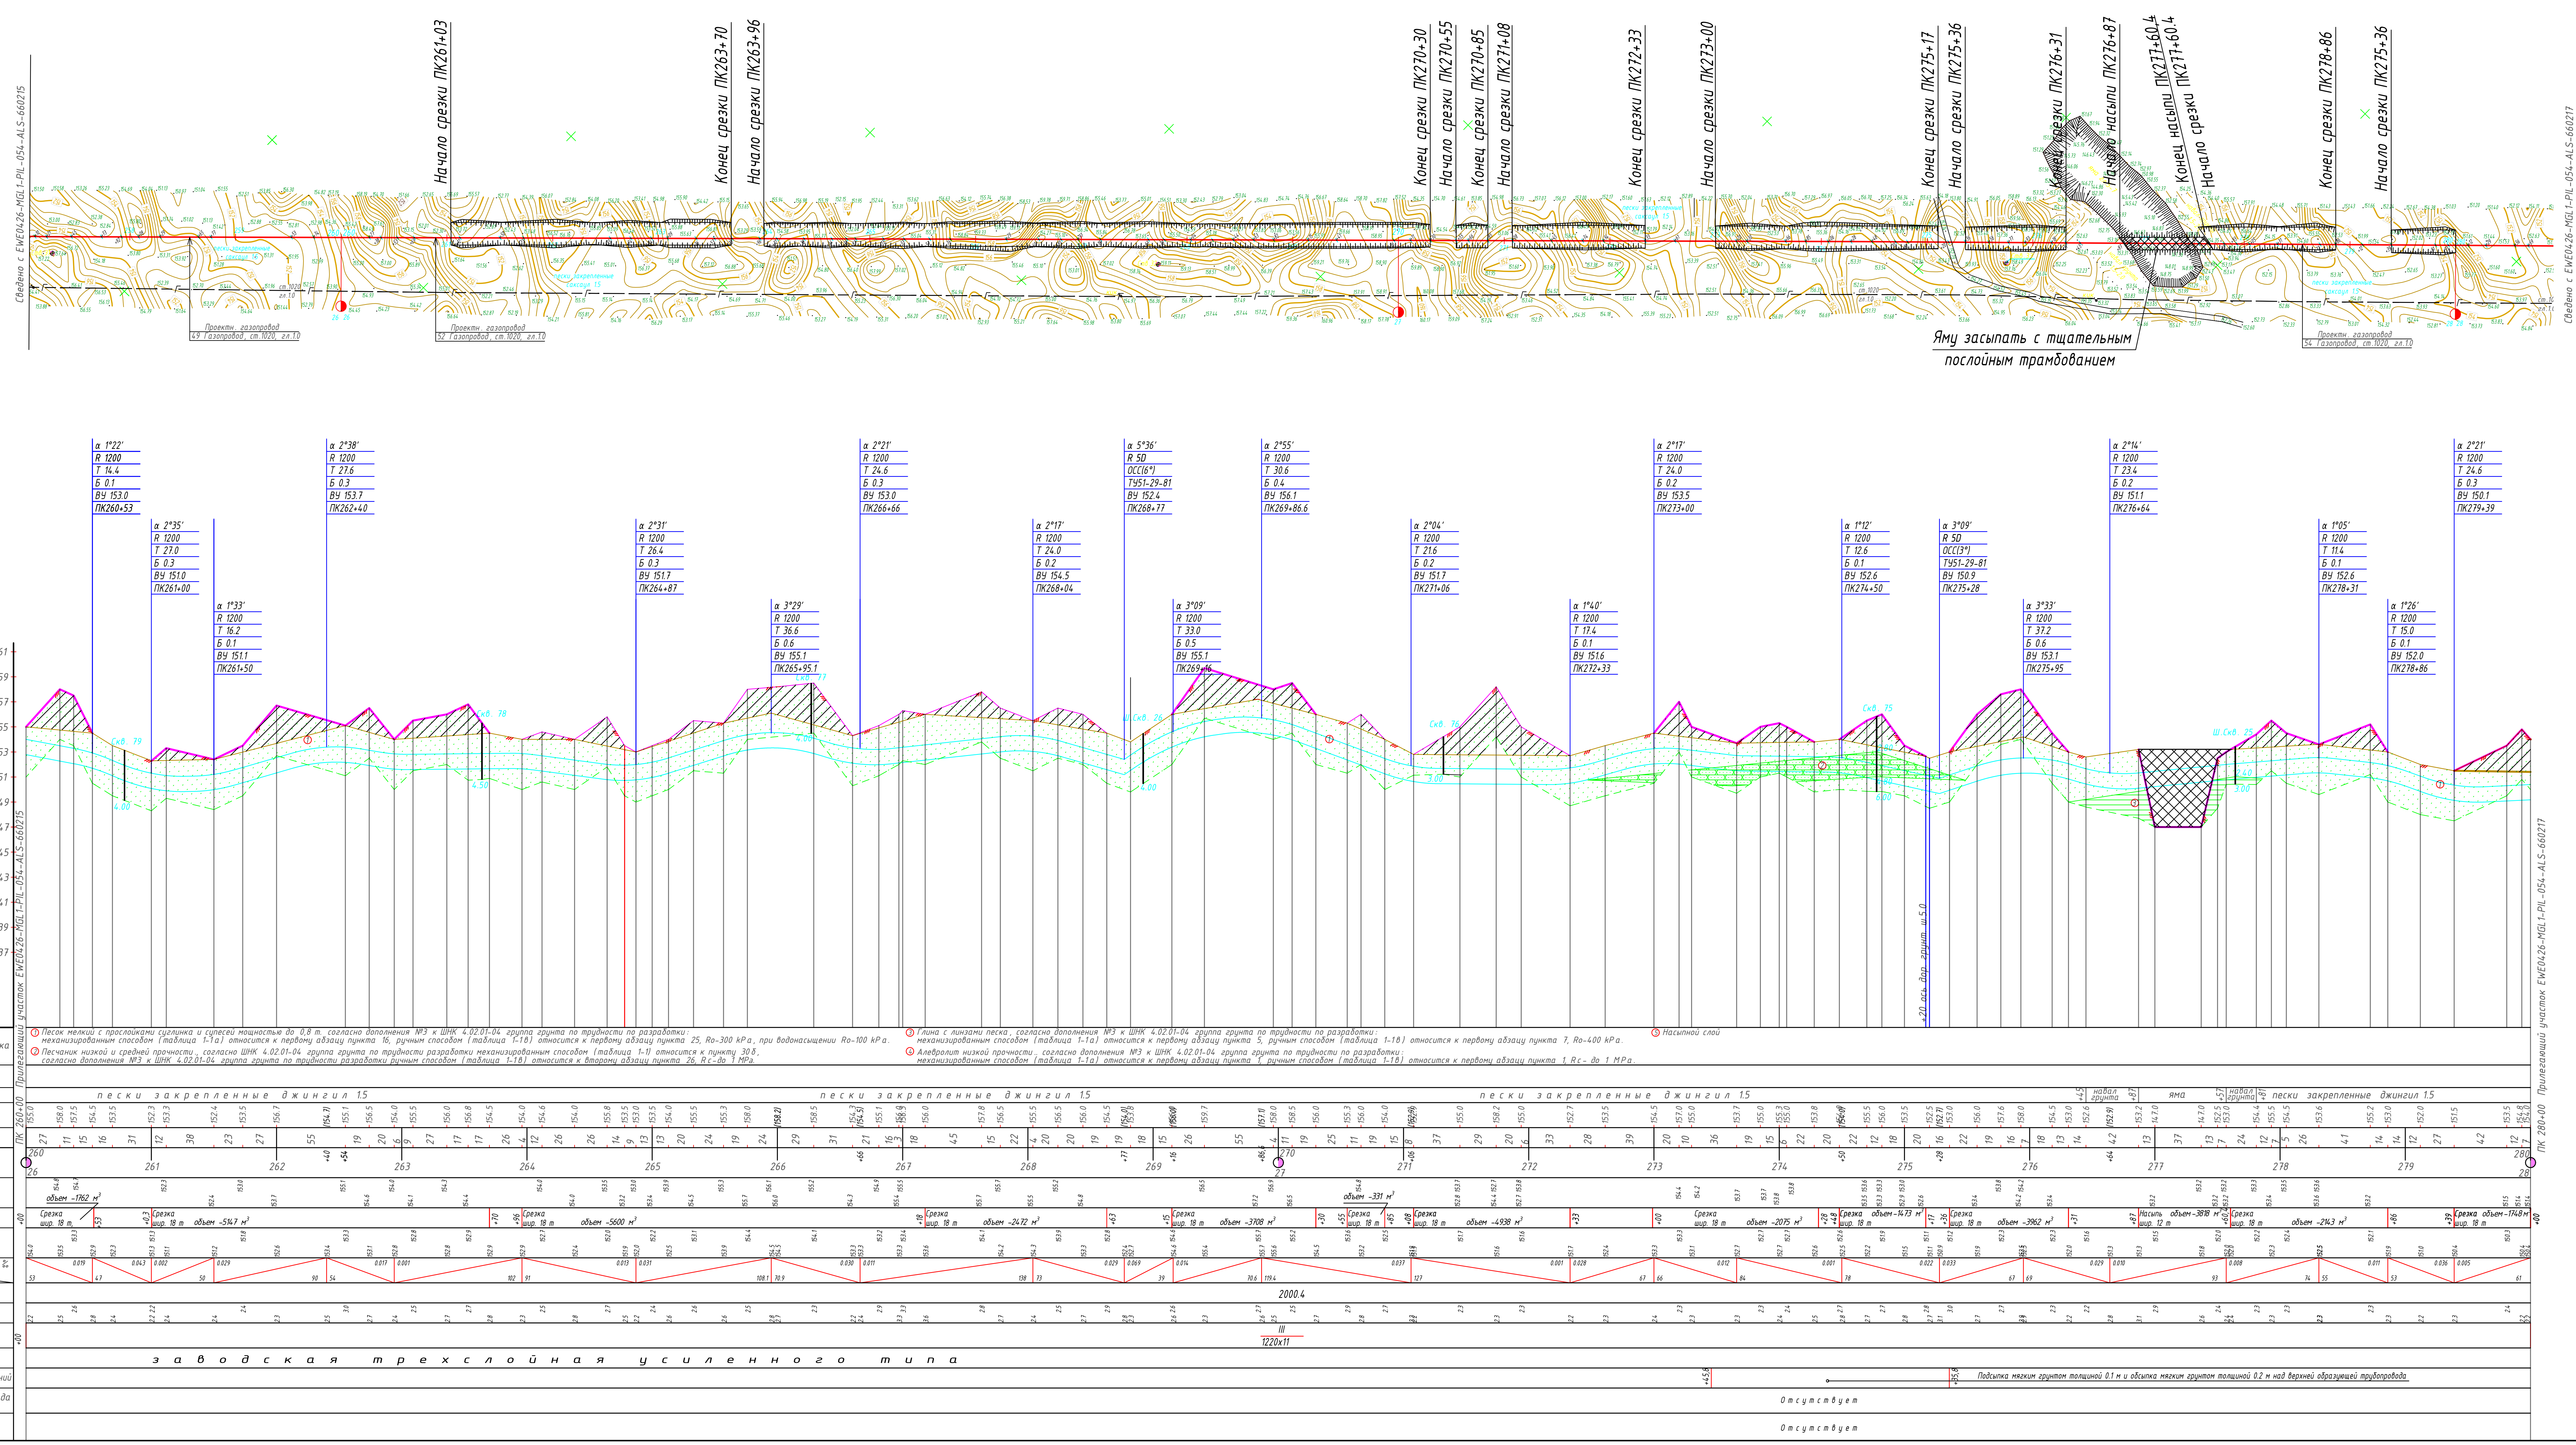
Начало срезки ПК261+03
Конец срезки ПК263+70
Начало срезки ПК263+96
Конец срезки ПК270+30
Начало срезки ПК270+55
Конец срезки ПК270+85
Начало срезки ПК271+08
Конец срезки ПК272+33
Начало срезки ПК273+00
Конец срезки ПК275+17
Начало срезки ПК275+36
Конец срезки ПК276+31
Начало насыпи ПК276+87
Конец насыпи ПК277+60.4
Начало срезки ПК277+60.4
Конец срезки ПК278+86
Начало срезки ПК279+36
Сведено с EWE0426-MGL1-PIL-054-ALS-660215
Сведено с EWE0426-MGL1-PIL-054-ALS-660217
Проектн. газопровод
54 Газопровод, ст.1020, гл.1.0
пески закрепленные саксаул 1.5
навал грунта
Яму засыпать с тщательным послойным трамбованием
Прилегающий участок EWE0426-MGL1-PIL-054-ALS-660215
Прилегающий участок EWE0426-MGL1-PIL-054-ALS-660217
ПК 260+00
ПК 280+00
пески закрепленные джингил 1.5
Срезка шир. 18 т
объем -1762 м³
объем -5147 м³
объем -5600 м³
объем -2472 м³
объем -3708 м³
2000.4
III
1220x11

1:2000 - по горизонтали
1:200 - по вертикали
1:200 - по вертикали - грунты

| | |
|---|---|
| Инженерно-геологическая характеристика | ① Песок мелкий с прослойками суглинка и супесей мощностью до 0,8 т. согласно дополнения №3 к ШНК 4.02.01-04 группа грунта по трудности по разработки: механизированным способом (таблица 1-1а) относится к первому абзацу пункта 16, ручным способом (таблица 1-1в) относится к первому абзацу пункта 25, Ro-300 kPa, при водонасыщении Ro-100 kPa.<br>② Песчаник низкой и средней прочности., согласно ШНК 4.02.01-04 группа грунта по трудности разработки механизированным способом (таблица 1-1) относится к пункту 30б, согласно дополнения №3 к ШНК 4.02.01-04 группа грунта по трудности разработки ручным способом (таблица 1-1в) относится к второму абзацу пункта 26, Rc-до 1 MPa.<br>③ Глина с линзами песка, согласно дополнения №3 к ШНК 4.02.01-04 группа грунта по трудности по разработки: механизированным способом (таблица 1-1а) относится к первому абзацу пункта 5, ручным способом (таблица 1-1в) относится к первому абзацу пункта 7, Ro-400 kPa.<br>④ Алевролит низкой прочности.. согласно дополнения №3 к ШНК 4.02.01-04 группа грунта по трудности по разработки: механизированным способом (таблица 1-1а) относится к первому абзацу пункта 1, ручным способом (таблица 1-1в) относится к первому абзацу пункта 1, Rc- до 1 MPa.<br>⑤ Насыпной слой |
| Уд. электросопр. грунтов, Ωm | |
| Угодья | пески закрепленные джингил 1.5 |
| Отметка земли, m | |
| Расстояние, m | |
| Пикеты, указатель километров | |
| Полка, выемка, насыпь, засыпка: Планировочные отметки | |
| Полка, выемка, насыпь, засыпка: Тип поперечного профиля | |
| Проектные отметки (верх трубы) | |
| Уклон газопровода, ‰ / Длина участка, m | |
| Истинная длина, m | 2000.4 |
| Глубина траншеи, m | |
| Категория участка газопровода / Трубы Ф x S, mm | III / 1220x11 |
| Тип изоляции газопровода | заводская трехслойная усиленного типа |
| Защита изоляции от механических повреждений | Подсыпка мягким грунтом толщиной 0.1 м и обсыпка мягким грунтом толщиной 0.2 м над верхней образующей трубопровода |
| Балластировка и закрепление газопровода (тип балласта или крепежа кол. шаг) | Отсутствует |
| Защитный кожух Ф x S, mm / L, m | Отсутствует |

Согласовано

| | | |
|---|---|---|
| Геолог | Усмонов | |
| Геолог | Жонузоков | |
| Испол. | Насруллозода | |
| Топограф | Бахтигузин | |
| Топограф | Абдуллаев | |
| Гидролог | Бахадиров | |

Взам. инв.№

Подп. и дата

Инв. № подл.

## Экспликация деталей и отдельных изделий

| № п. п. | Наименование деталей | Ед изм. | Кол. | Примечание |
|---|---|---|---|---|
| 1 | ОСС 3°-5Д-1220 (12К60)-5,5-075-У ТУ51-29-81 | шт | 1 | |
| 2 | ОСС 6°-5Д-1220 (12К60)-5,5-075-У ТУ51-29-81 | шт | 1 | |


Схема расположения листов
EWE0426-MGL1-PIL-054-ALS-660215
EWE0426-MGL1-PIL-054-ALS-660216
EWE0426-MGL1-PIL-054-ALS-660217

1 Общие данные - чертеж EWE0426-MGL1-PIL-054-COM-660201
2 Ситуационный план см. EWE0426-MGL1-PIL-054-DRW-660202
3 До начала работ руководитель строительной организации должен разработать и согласовать схему и инструкцию по безопасному производству работ в охранной зоне газопровода и его сооружений.
4 Производство работ на данном участке вести в строгом соответствии с "Инструкцией по производству строительных работ в охранных зонах магистральных трубопроводов Мингазпрома" ВСН 51-1-80.
5 Ширину полосы отвода земель для строительства газопровода см. типовой чертеж EWE0426-MGL1-PIL-000-DRW-810201.
6 Охранную зону магистрального газопровода см. типовой чертеж EWE0426-MGL1-PIL-000-DRW-810202.
7 Поперечный разрез траншеи см. типовой чертеж EWE0426-MGL1-PIL-000-DRW-810203.

| Рев. | Дата | Назначение ревизии | Проверил | Утвердил |
|---|---|---|---|---|
| A2 | 17.08.2026 | Выпущено для строительства | | |
| A1 | 16.07.2026 | Выпущено для строительства | | |
| R2 | 02.07.2026 | Выпущено для рассмотрения | | |
| R1 | 05.06.2026 | Выпущено для рассмотрения | | |

ЗАКАЗЧИК: UTG UZTRANSGAZ
ГЕНЕРАЛЬНЫЙ ПОДРЯДЧИК: UET UZBEKENERGOTAMIR
ПОДРЯДЧИК: PBG Pro Build Generation
ГЕНЕРАЛЬНЫЙ ПРОЕКТИРОВЩИК: EAST WEST ENGINEERING

# EWE0426-MGL1-PIL-054-ALS-660216-A2

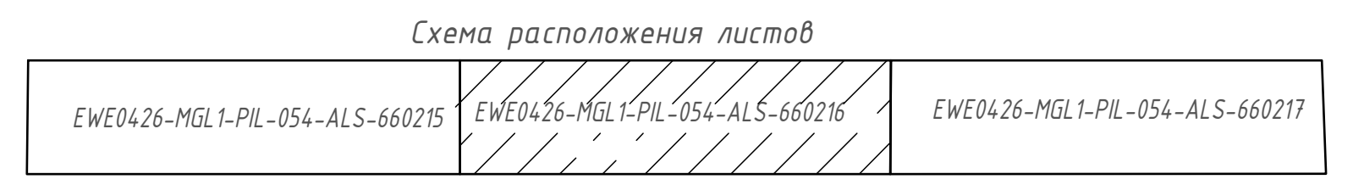«СТРОИТЕЛЬСТВО НОВЫХ НИТОК (УЧАСТКОВ) ГАЗОПРОВОДОВ «ГАЗЛИ - САРИМОЙ» И «АКЧАЛОК - ГАЗЛИ - НУКУС» ОБЩЕЙ ПРОТЯЖЕННОСТЬЮ НЕ МЕНЕЕ 275 КМ».

| Изм. | Кол.уч. | Лист | №док. | Подпись | Дата |
|---|---|---|---|---|---|
| ГИП | | Схабицкий А. | | | 08.2026 |
| Провер. | | Шафиева О. | | | 08.2026 |
| Исполн. | | Мухамадеева | | | 08.2026 |
| Н.контр | | Схабицкий А. | | | 08.2026 |

ГАЗОПРОВОД «ГАЗЛИ-САРИМОЙ» (54 КМ)

| Стадия | Лист | Листов |
|---|---|---|
| РД | 1 | 1 |

План и продольный профиль газопровода
ПК 260+00- ПК 280+00

ООО "EAST-WEST Engineering"
г. Ташкент 2026г.